

Crèche de Sceaux
Groupe LES PETITES CANAILLES
146, rue Houdan - Sceaux (92330)

DOSSIER DES TRAVAUX DE MIS EN CONFORMITE

25 / 10 / 2018

Maître d'Ouvrage :

LES PETITES CANAILLES
36, rue Pierret
92200 - Neuilly sur Seine
Tél : 01 58 83 48 35


Maître d'Œuvre :

ORCHESTRA AGENCEMENTS SAS
57, rue Dalayrac
94120 Fontenay-sous-bois
Tél : 01 41 79 53 62



Localisation jardin - 146, rue Houdan à Sceaux

Accès depuis habitation résidents
Hall de l'immeuble
Accès sur le jardin depuis la crèche

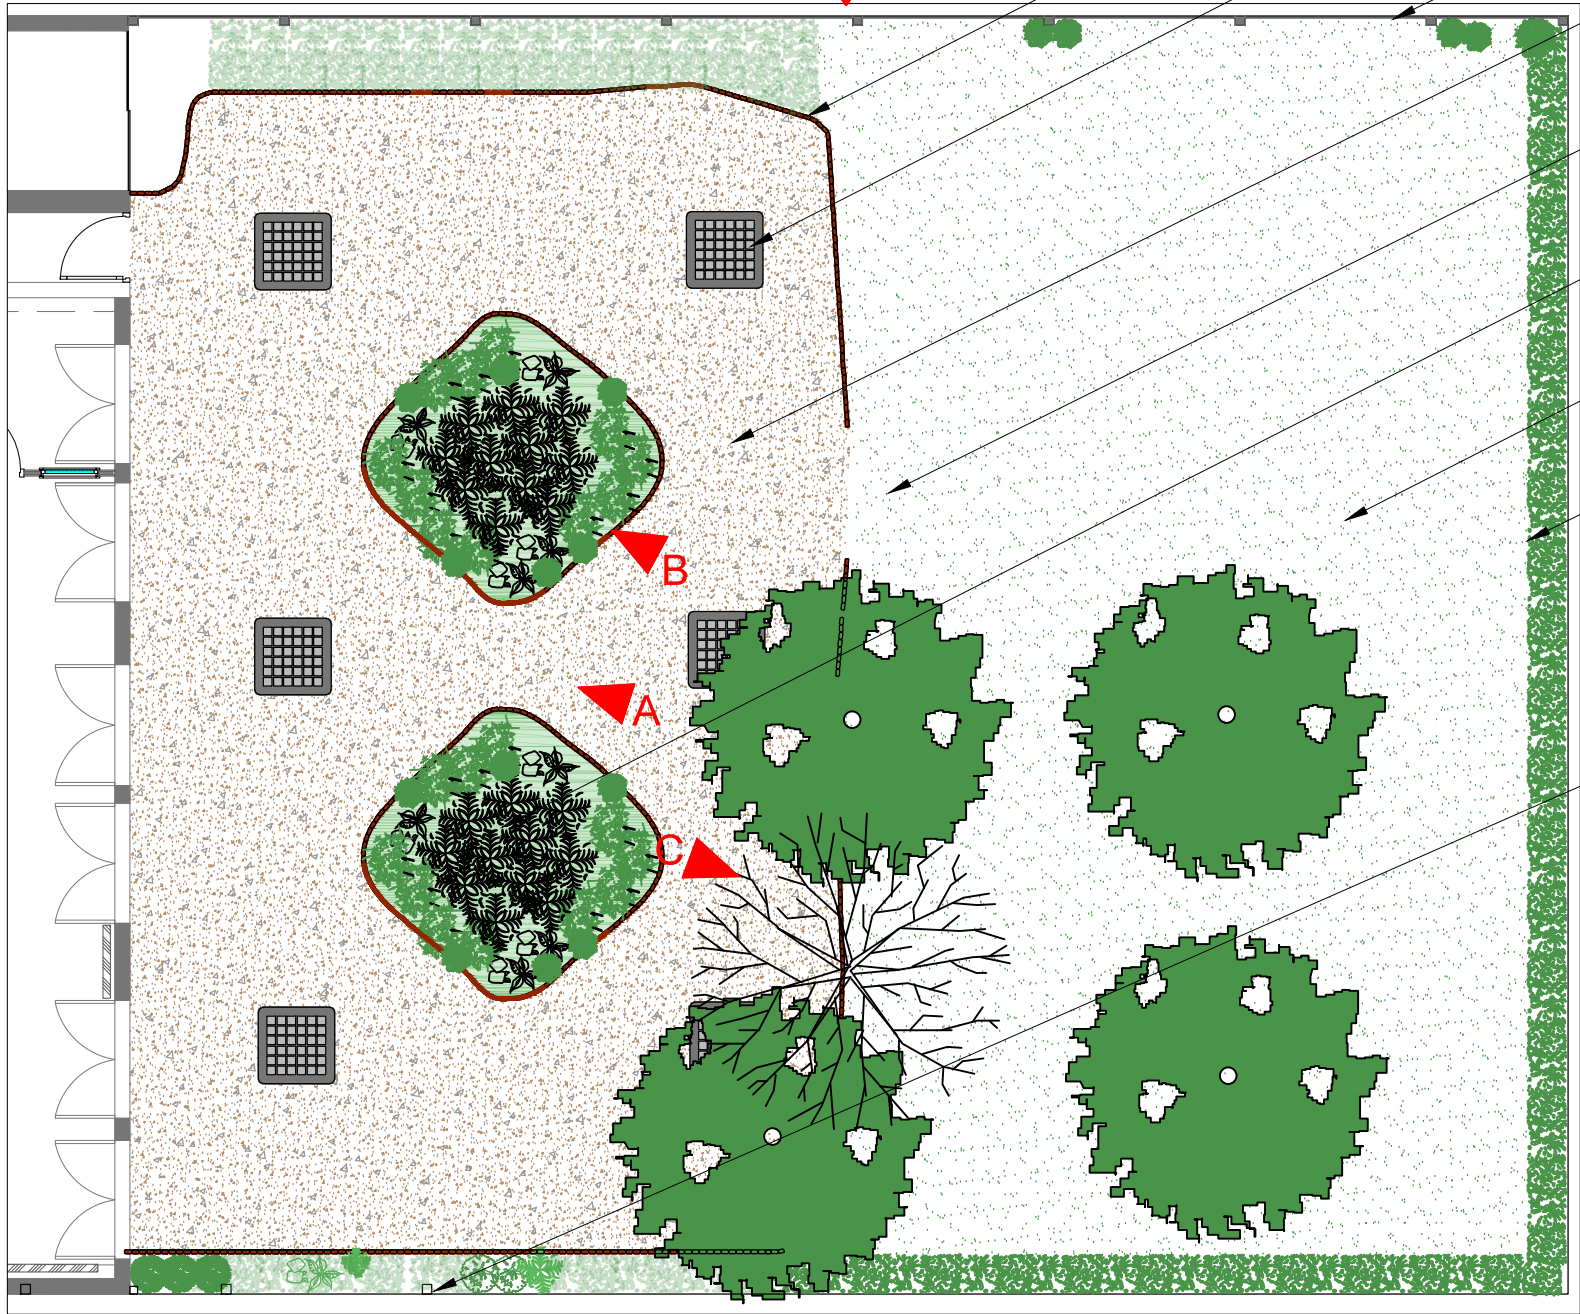

Cheminements au sol

Hublots du parking sous terrain

Séparation mur béton

Sol gravillons

Pente pour accès à la deuxième partie du jardin en soubassement

Jardinière

Sol pelouse

Séparation du voisinage avec des buissons

Séparation du voisinage avec une clôture



Vue A



Vue B



Vue C



Maître d'oeuvre
Orchestra Agencements SAS
57 rue Dalayrac 94120 Fontenay sous-bois
Tél : 01 41 79 53 62

Maître d'ouvrage
LES PETITES CANAILLES
36 rue Pierret - 92200 Neuilly sur Seine
Tél : 01 58 83 48 35

Affaire
LPC SCEAUX - 25 Berceaux
Surface : 276 m2

Libellé
Implantation jardin existant

Resp. Dossier : Benoît CHAMPIGNEUX			
Tél : 06 48 18 04 03	Mail : benoit.orchestra@orange.fr		
Date : 22 / 05 / 2018	Indice : 5	Echelle : 1/100	Format : A3

Implantation projet jardin

- Réalisation d'un sol dalles souples de 2m sur la largeur de la crèche
- Remplacement des menuiseries extérieures à l'identique sauf menuiserie du repos 2 (pour passer en double vitrage) + grilles extraction et prise d'air VMC
- Installation de stores bannes
- Réparation d'une clôture
- Mise en place de protection d'angle sur les aérations du parking

Portail d'accès

Remplacement des menuiseries extérieures à l'identique (sauf grilles VMC et menuiseries du repos 2)

Hublots du parking sous terrain

Suppression des 3 hublots du parking sous terrain situés à <8m de la façade

Sol gravillons existant

Sol dalles souples

Cloture type jardin Ht = 1,5m

Sol pelouse (pas de changement)

Séparation du voisinage avec des buissons (pas de changement)

Accès depuis habitation résidents

Hall de l'immeuble

Accès sur le jardin depuis la crèche

Clôture à réparer

Jardin crèche

Jardin résidents immeuble



Localisation jardin - 146, rue Houdan à Sceaux
Plan existant


Maître d'oeuvre
Orchestra Agencements SAS
57 rue Dalayrac 94120 Fontenay sous-bois
Tél : 01 41 79 53 62

Maître d'ouvrage
LES PETITES CANAILLES
36 rue Pierret - 92200 Neuilly sur Seine
Tél : 01 58 83 48 35


Affaire
LPC SCEAUX - 25 Berceaux
Surface : 276 m2

Libellé
Plan EXE de cloisonnement RDC
23/10/2018

Resp. Dossier : Benoît CHAMPIGNEUX			
Tél : 06 48 18 04 03	Mail : benoit.orchestra@orange.fr		
Date : 22/05/2018	Indice : 5	Echelle : 1/100	Format : A3

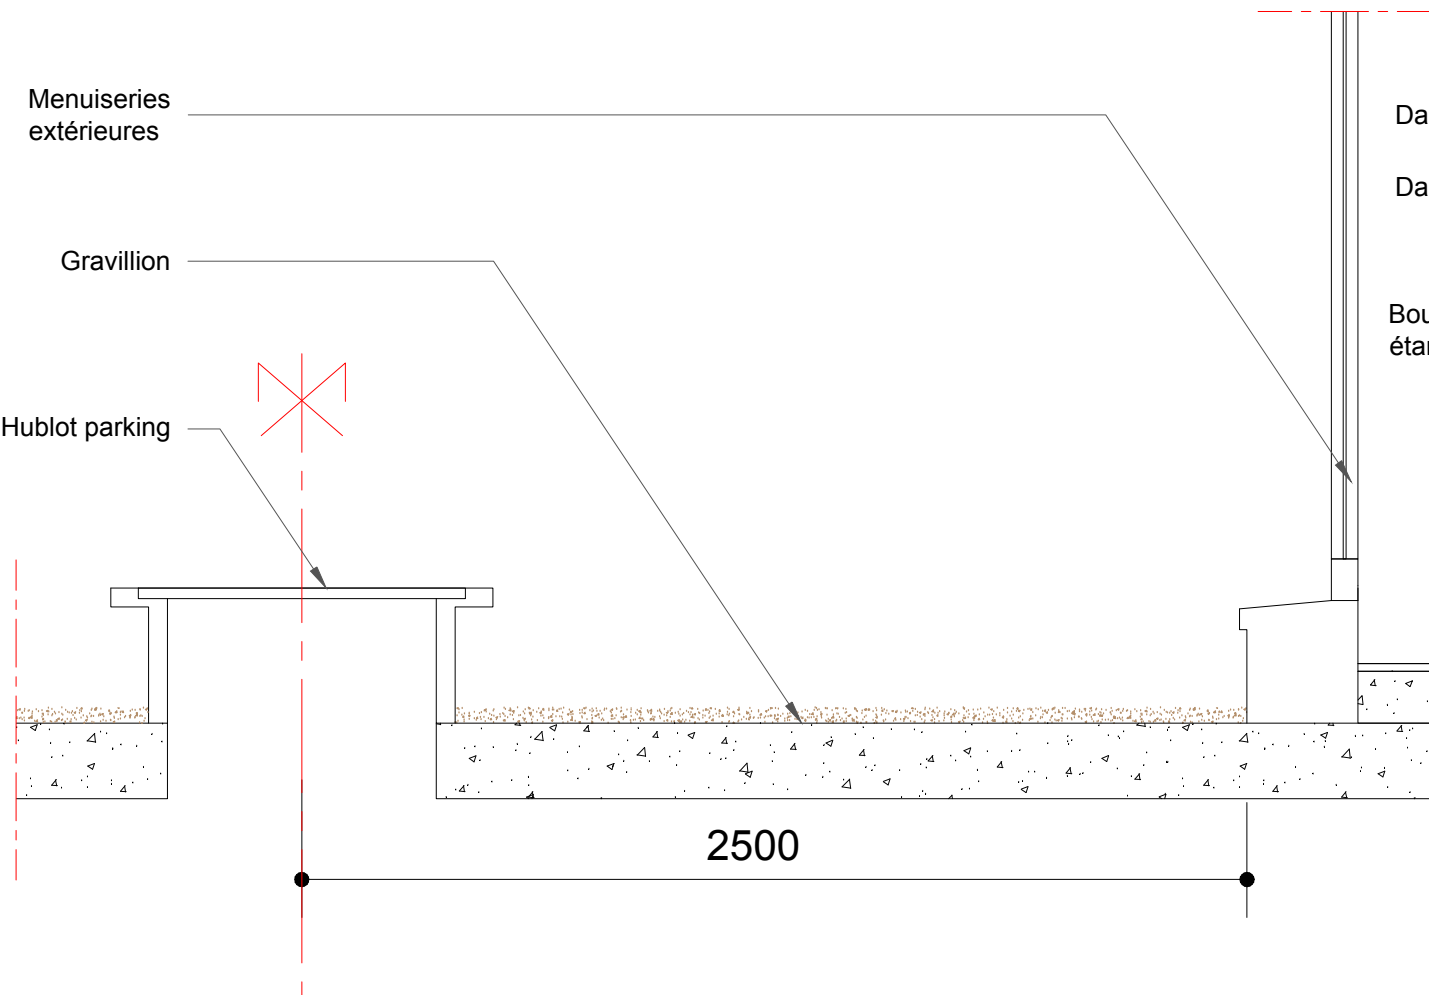


EXISTANT

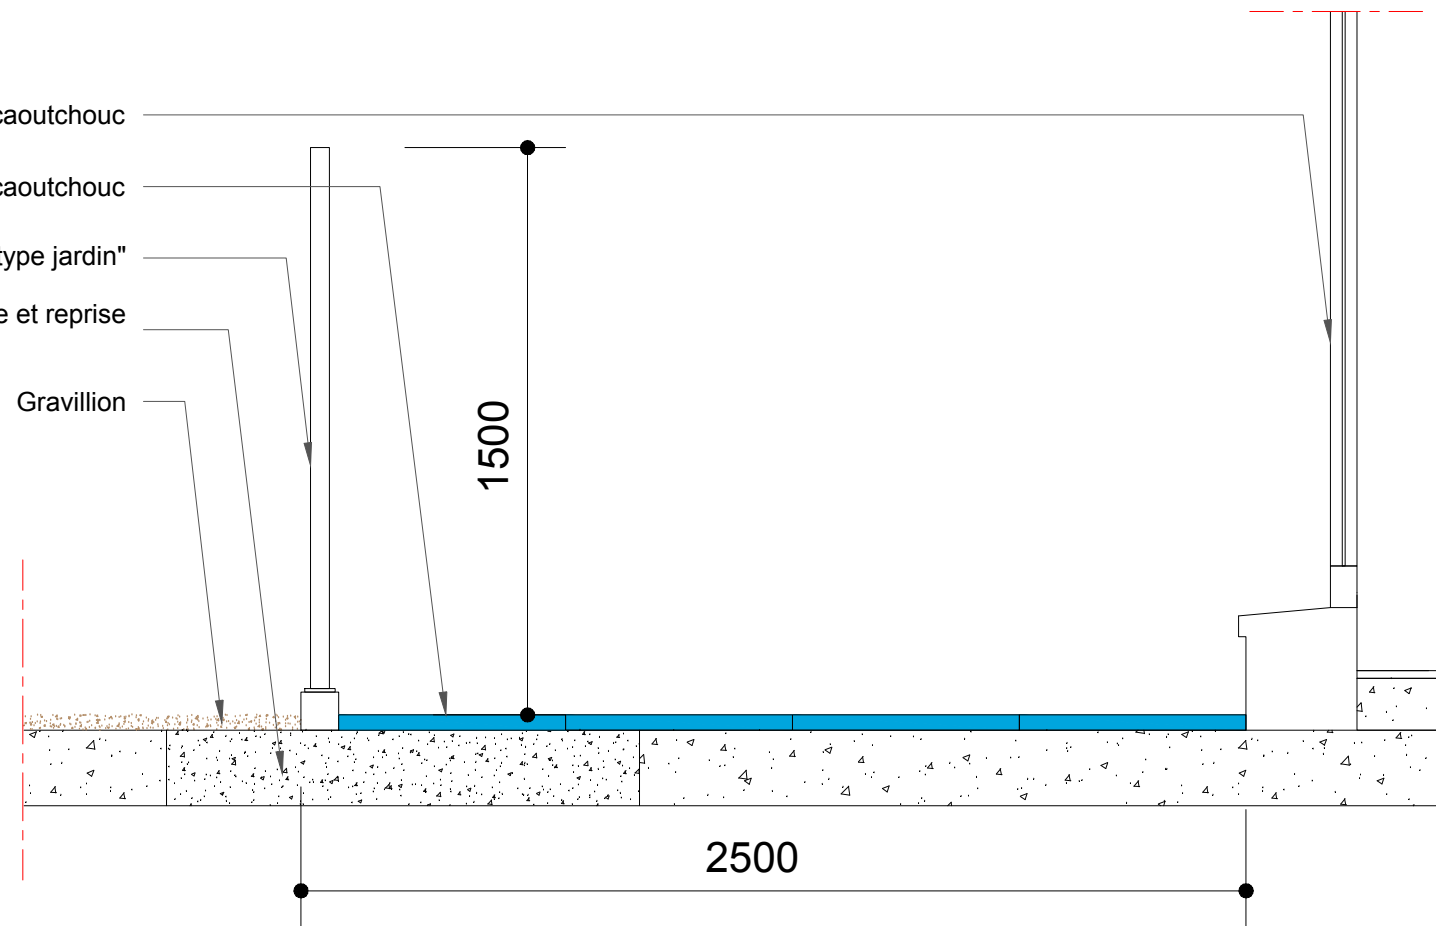


PROJET

- depose des puits de lumière du parking à < de 8m de la façade ;
- bouchage par coulage 3 dalles en béton des puits déposés y compris reprise de l'étanchéité ;
- réalisation d'un sol souple en dalles agréées pour les crèches sur 2,5 m sur la longueur de la crèche ;
- réalisation d'une cloture "type jardin" avec portillon d'accès de 1,5m d'hauteur ;

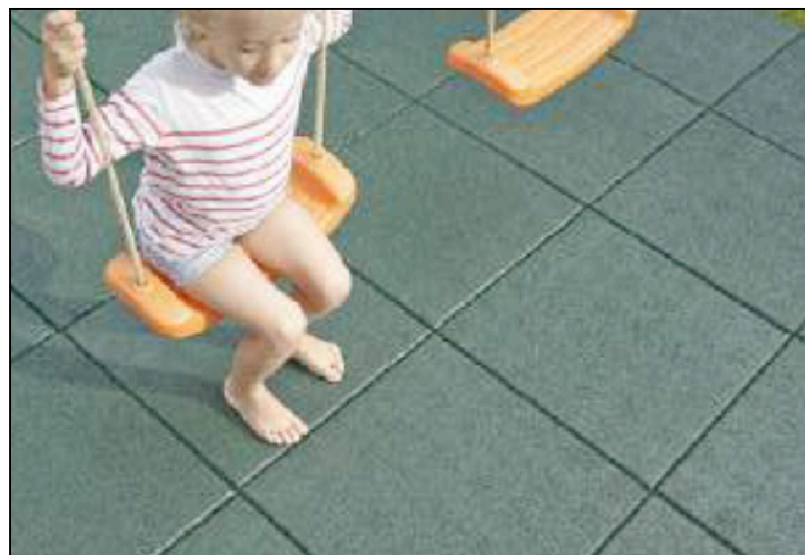

Exemple de dalles caoutchouc

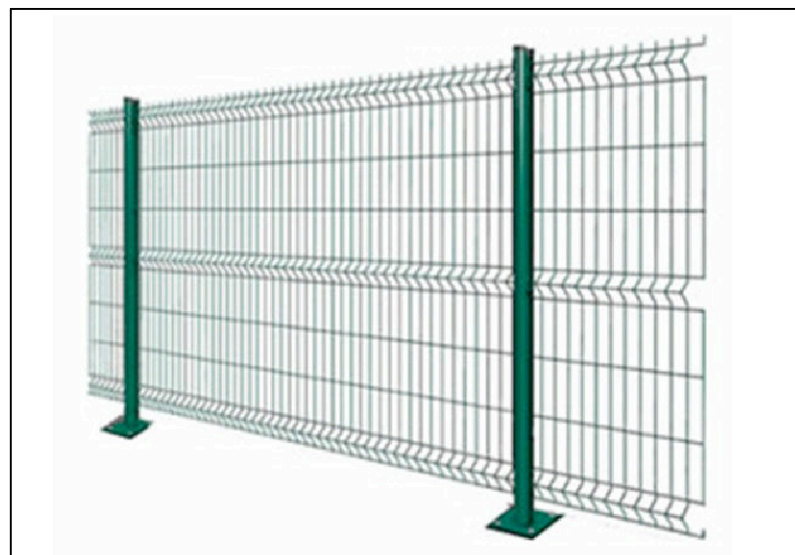

Exemple de cloture de jardin



Exemple de portillon de jardin

Maître d'oeuvre
Orchestra Agencements SAS
57 rue Dalayrac 94120 Fontenay sous-bois
Tél : 01 41 79 53 62

Maître d'ouvrage
LES PETITES CANAILLES
36 rue Pierret - 92200 Neuilly sur Seine
Tél : 01 58 83 48 35

Affaire
LPC SCEAUX - 25 Berceaux
Surface : 276 m2

Libellé
Plan EXE
coupe de principe de la
terrasse extérieure
23/10/2018

Resp. Dossier : Benoît CHAMPIGNEUX


Tél : 06 48 18 04 03 Mail : benoit.orchestra@orange.fr

Date : 22/05/2018

Indice : 5

Echelle : 1/20

Format : A3

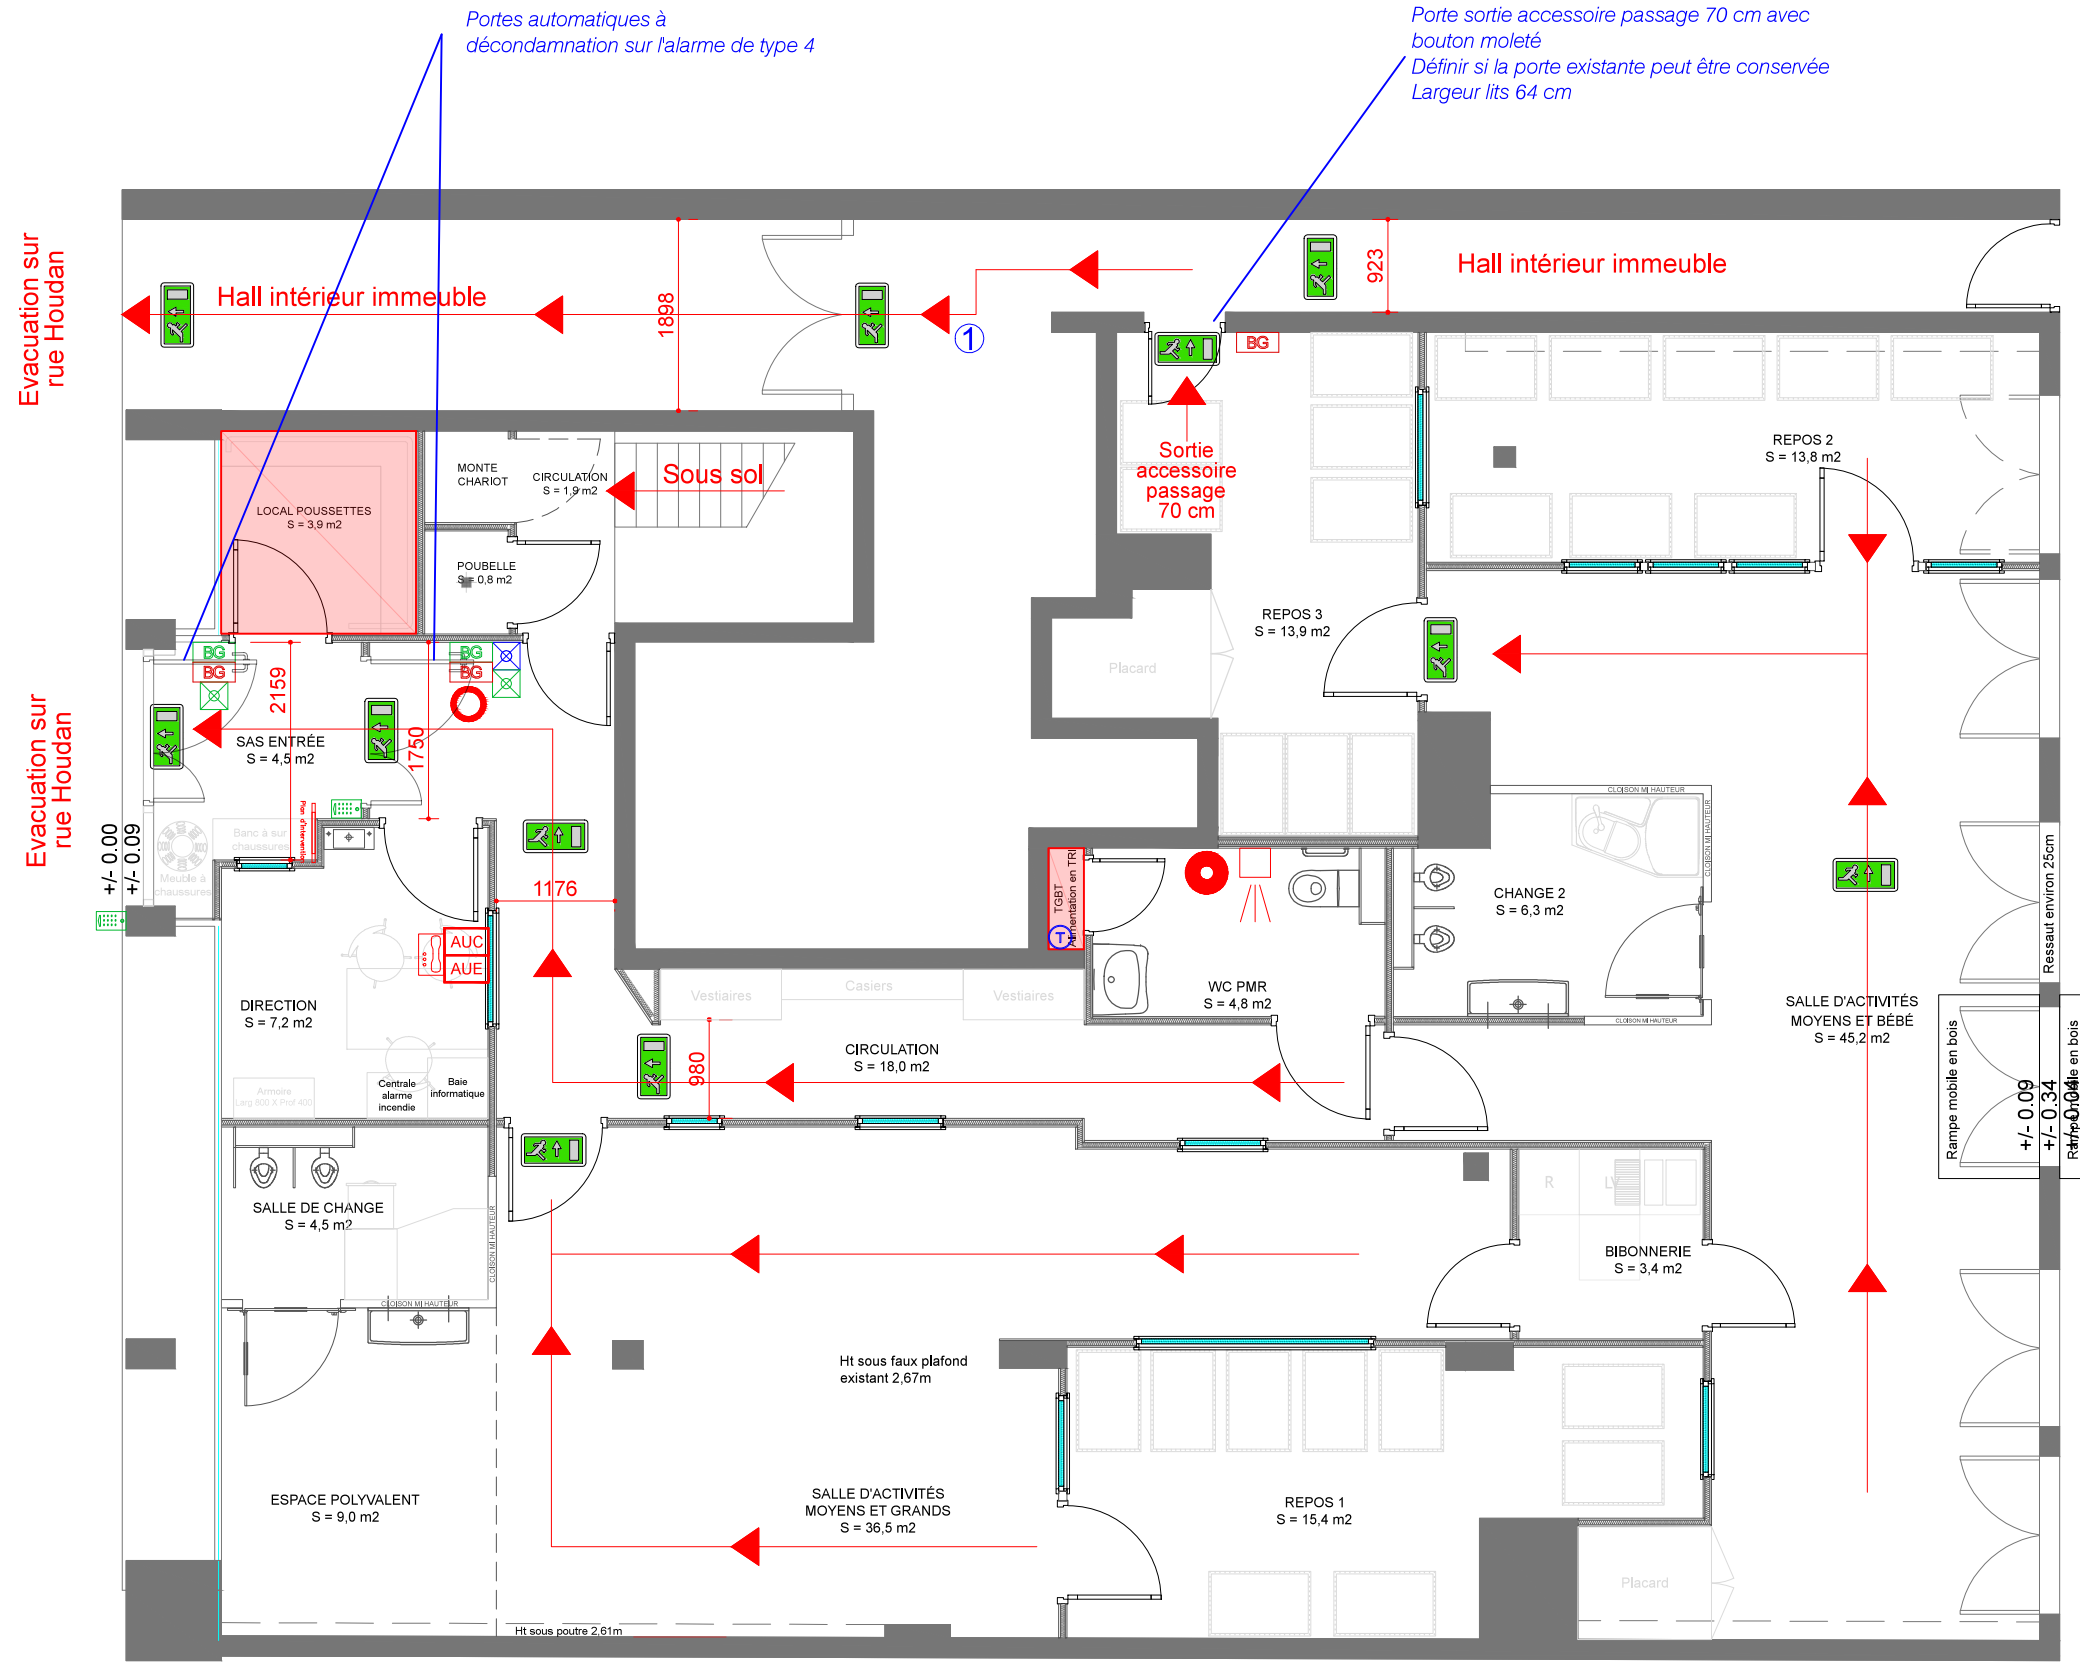

LÉGENDE SECURITÉ	
	Cheminement évacuation
	Flash lumineux
	Bloc autonome d'éclairage de sécurité
	Arrêt d'urgence climatisation
	Arrêt d'urgence électricité
	Extincteur eau pulvérisée
	Extincteur CO ²
	Plan d'intervention
	Déclencheur manuel ouverture porte
	Déclencheur manuel alarme incendie
	Digicode
	Détecteur tactile pour ouverture porte
	Combiné
	Coupeure générale éclairage
	Ligne téléphonique
	Zone coupe feu 1h