


DOS-
SIER
DCE

MULTI-ACCUEIL DE 30 BERCEAUX
78 400 CHATOU

MOA : SARL LPC YVELINES
15 Rue de l'Orient 78000 VERSAILLES




MAITRE D'OEUVRE  NAHK ARCHITECTURE 24 rue Yves Toudic - 75010 PARIS	PHASE DCE	VERSION 01	DATE 30/06/2023	OPÉRATION CREATION D'UN MULTI ACCUEIL DE 30 BERCEAUX ET REAMENAGEMENT D'UNE MAISON MEDICALE 30 ter Avenue de Brimont 78400 CHATOU	MAITRE D'OUVRAGE SARL LPC YVELINES 15 Rue de l'Orient 78000 VERSAILLES	N° DOC --	NOM DU DOCUMENT	ÉCHELLE --
--	---------------------------------	----------------------------------	---------------------------------------	---	--	---------------------------------	----------------------------	----------------------------------

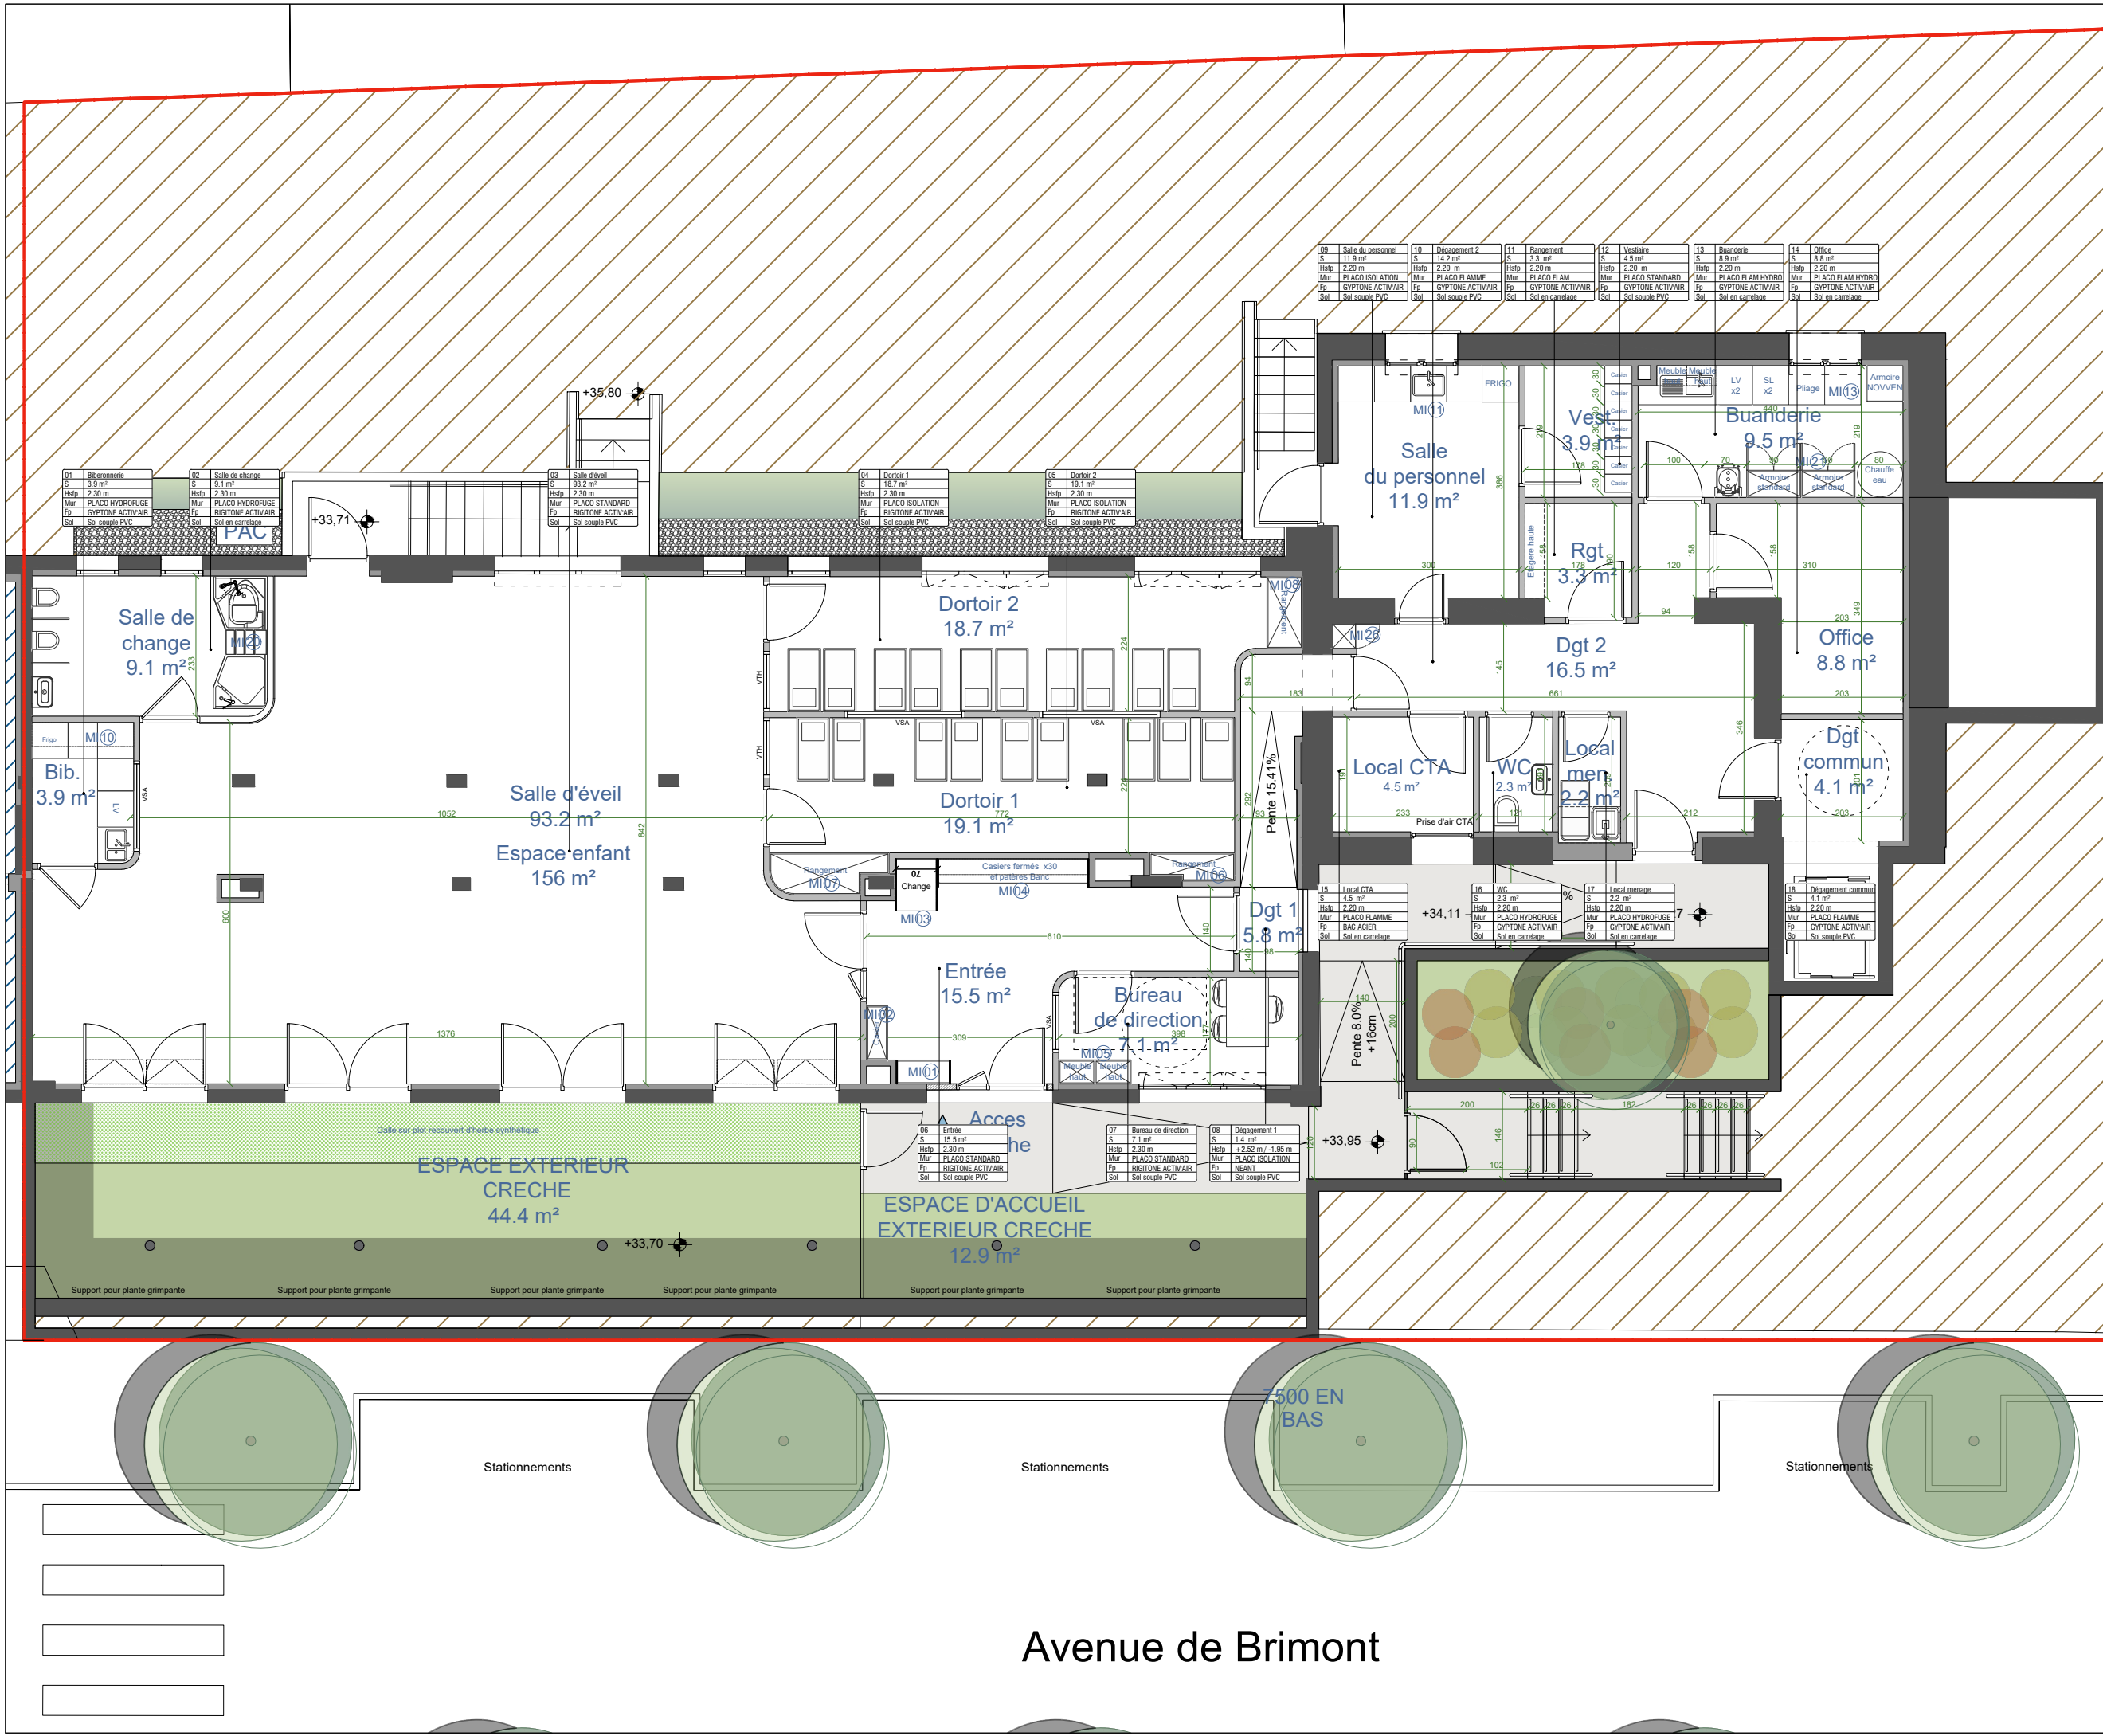



CREATION D'UN MULTI-ACCUEIL ET D'UNE MAISON MEDICALE 78400 CHATOU			
MOA	SARL LPC YVELINES 15 Rue de l'Orient78000 VERSAILLES		
MOE	NAHK ARCHITECTURE 24 Rue Yves Toudic, 75010 Paris		
NOM DU DOCUMENT			
PLAN CRECHE RDJ			
PHASE	PRO.DCE	ECH.	1/100
INDICE	1.1	DATE	30/06/2023
MODIFICATIONS			
INDICE DATE		OBJET	
1.1	30/06/2023	Diffusion initiale	

Avenue de Brimont

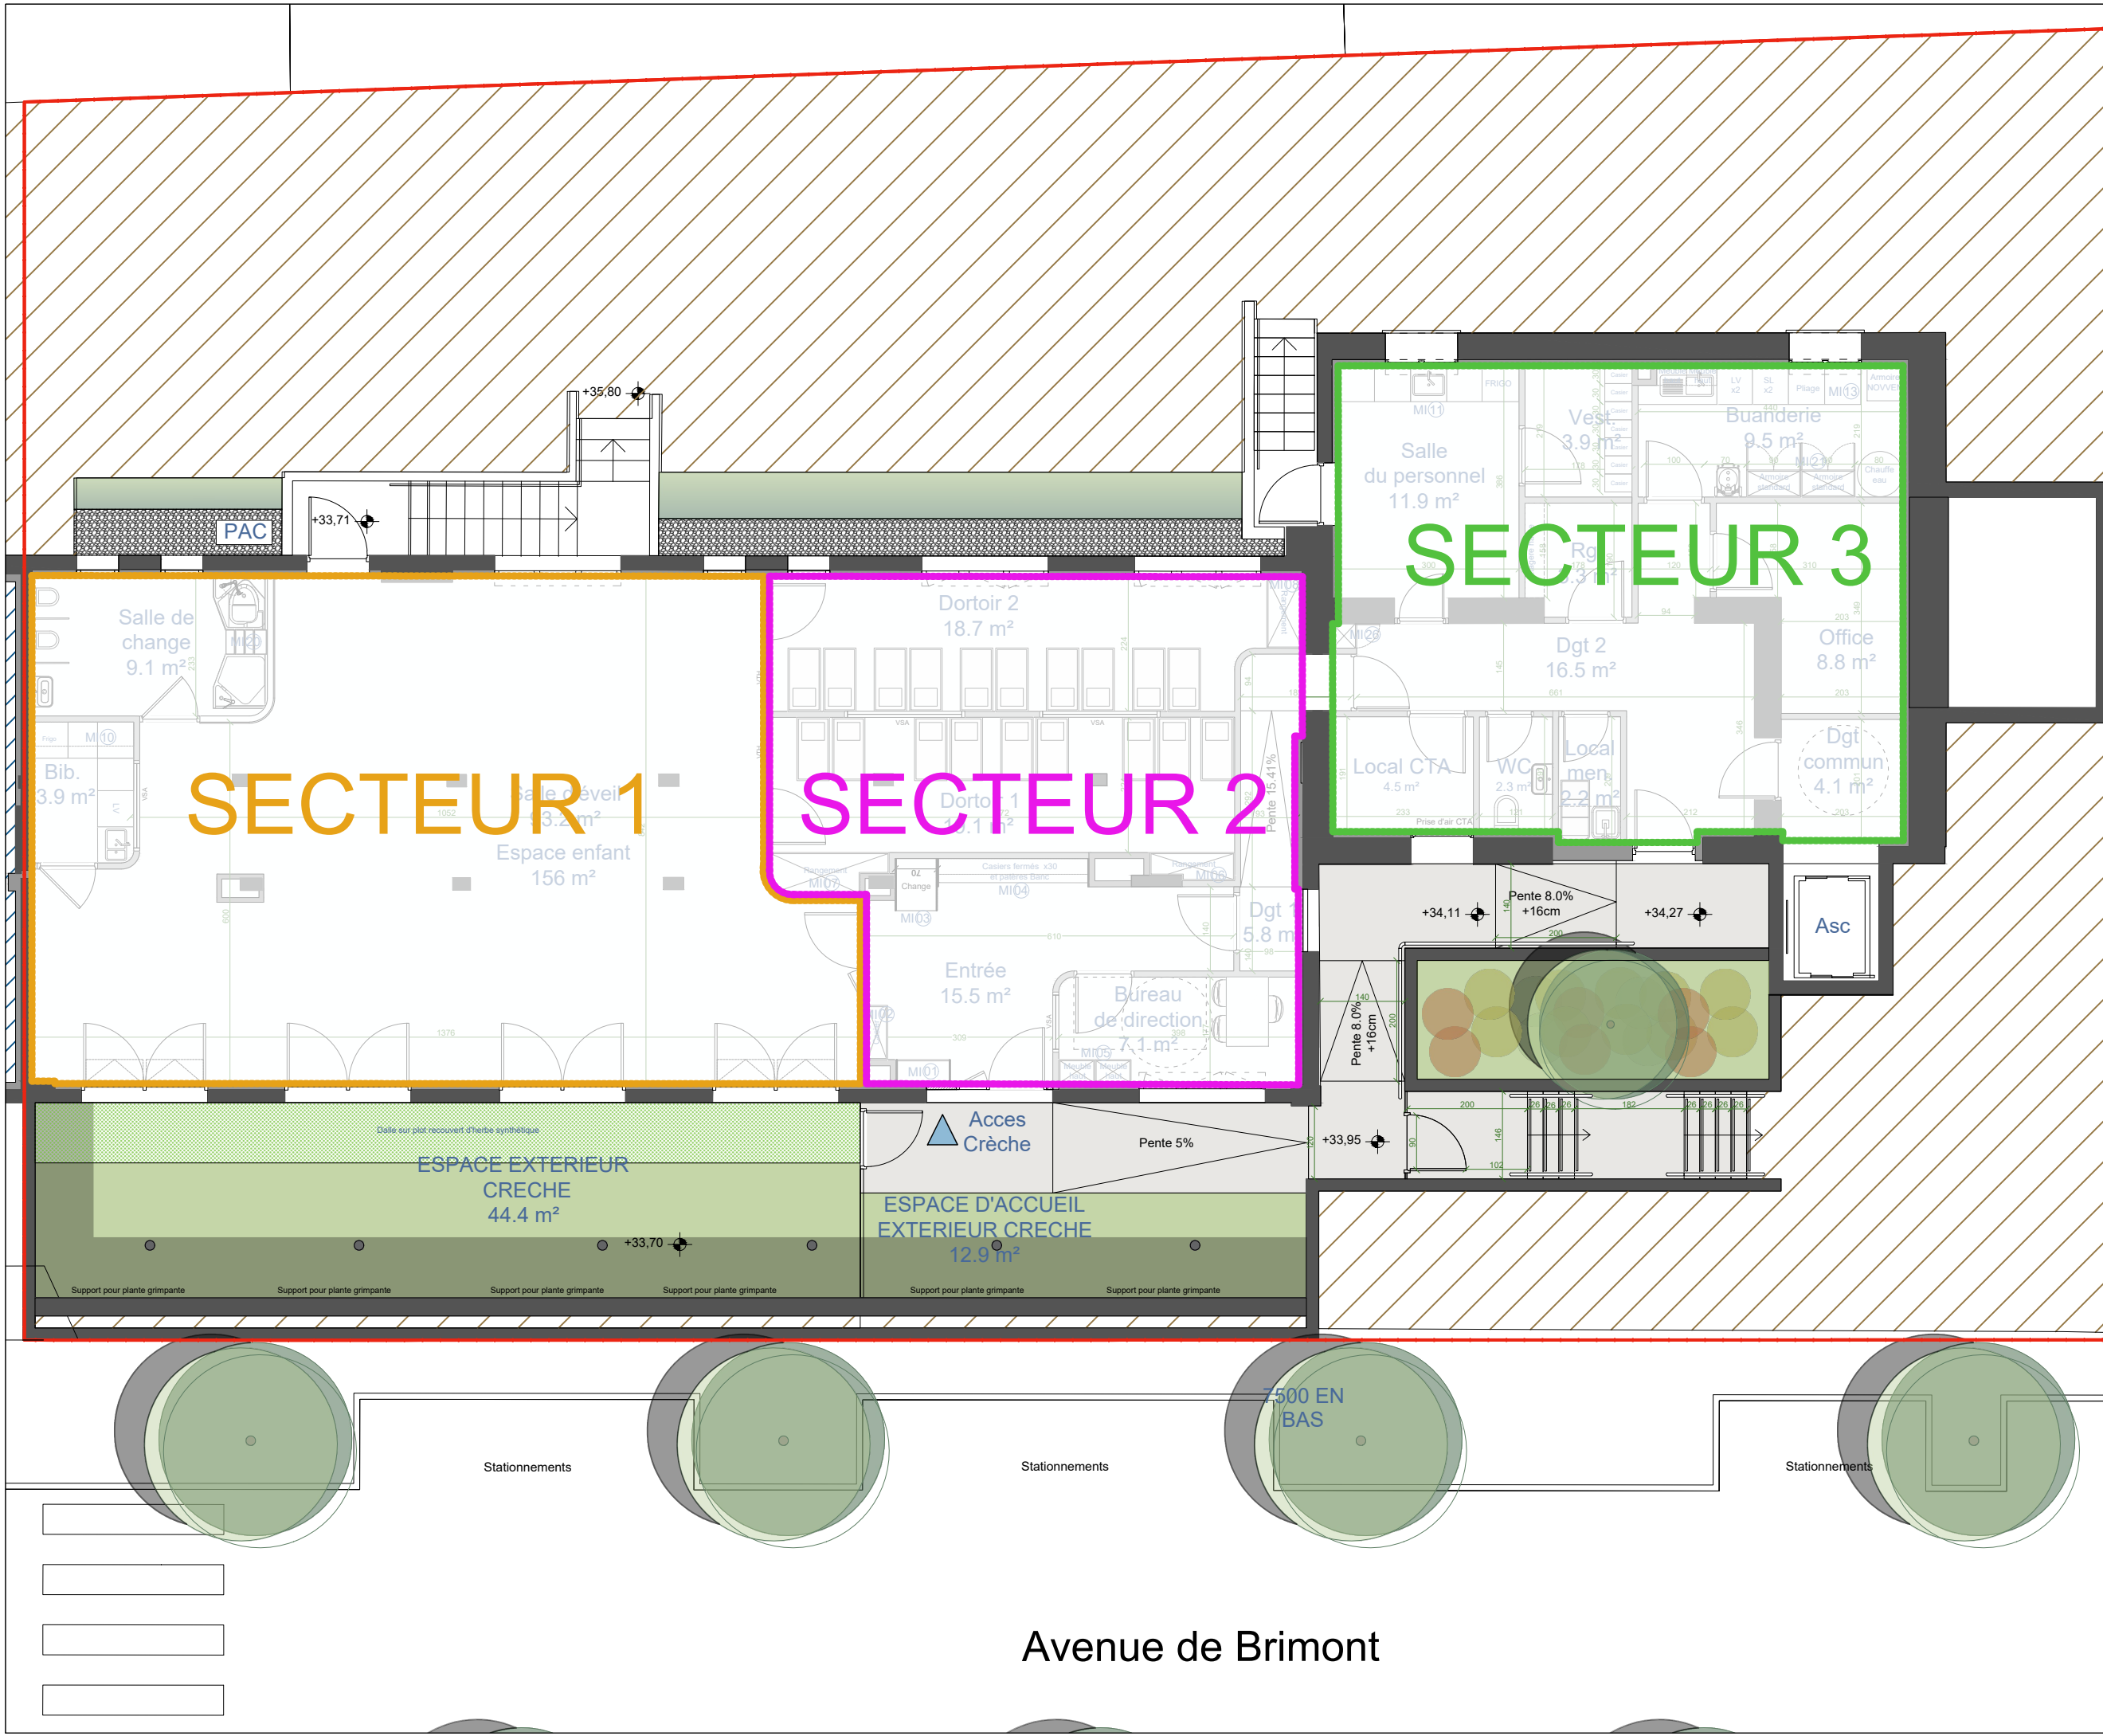


CREATION D'UN MULTI-ACCUEIL ET D'UNE MAISON MEDICALE 78400 CHATOU			
MOA	SARL LPC YVELINES 15 Rue de l'Orient78000 VERSAILLES		
MOE	NAHK ARCHITECTURE 24 Rue Yves Toudic, 75010 Paris		
NOM DU DOCUMENT			
PLAN DE LOCALISATION DES SECTEURS			
PHASE	PRO.DCE	ECH.	1/100
INDICE	1.1	DATE	30/06/2023
MODIFICATIONS			
INDICE DATE OBJET			
1.1	30/06/2023	Diffusion initiale	
SECTEUR 1 SECTEUR 2 SECTEUR 3			

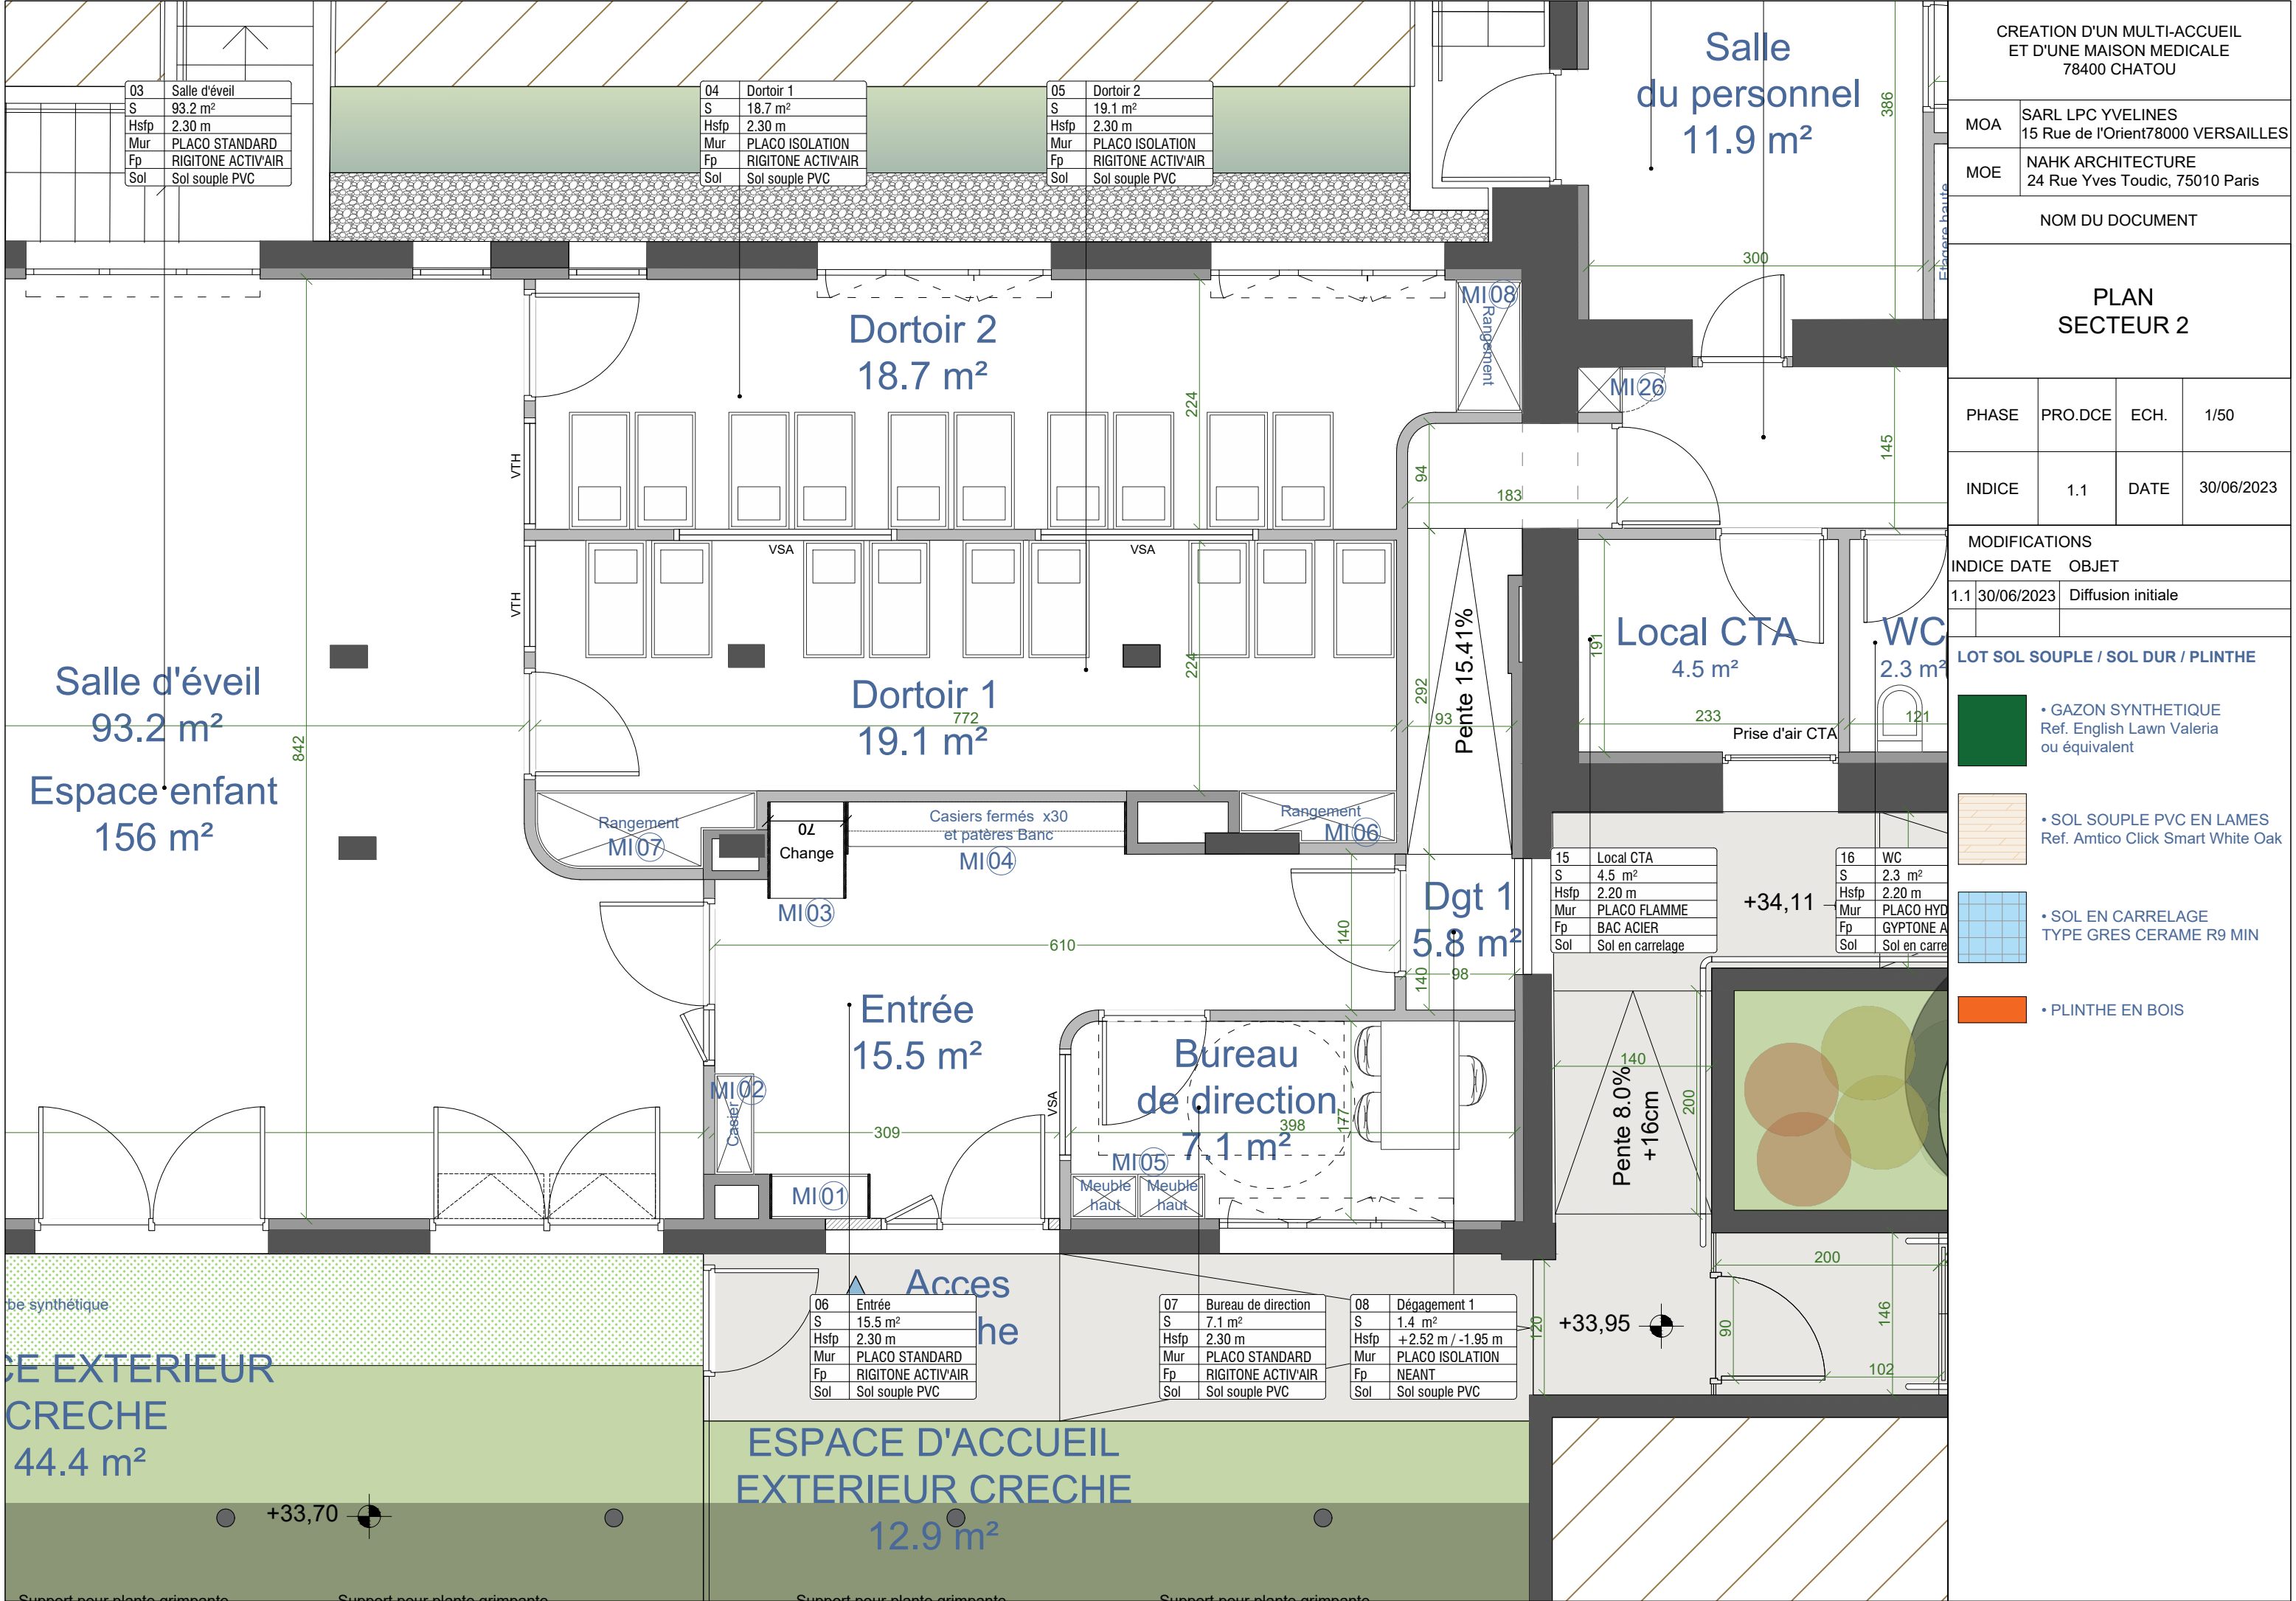

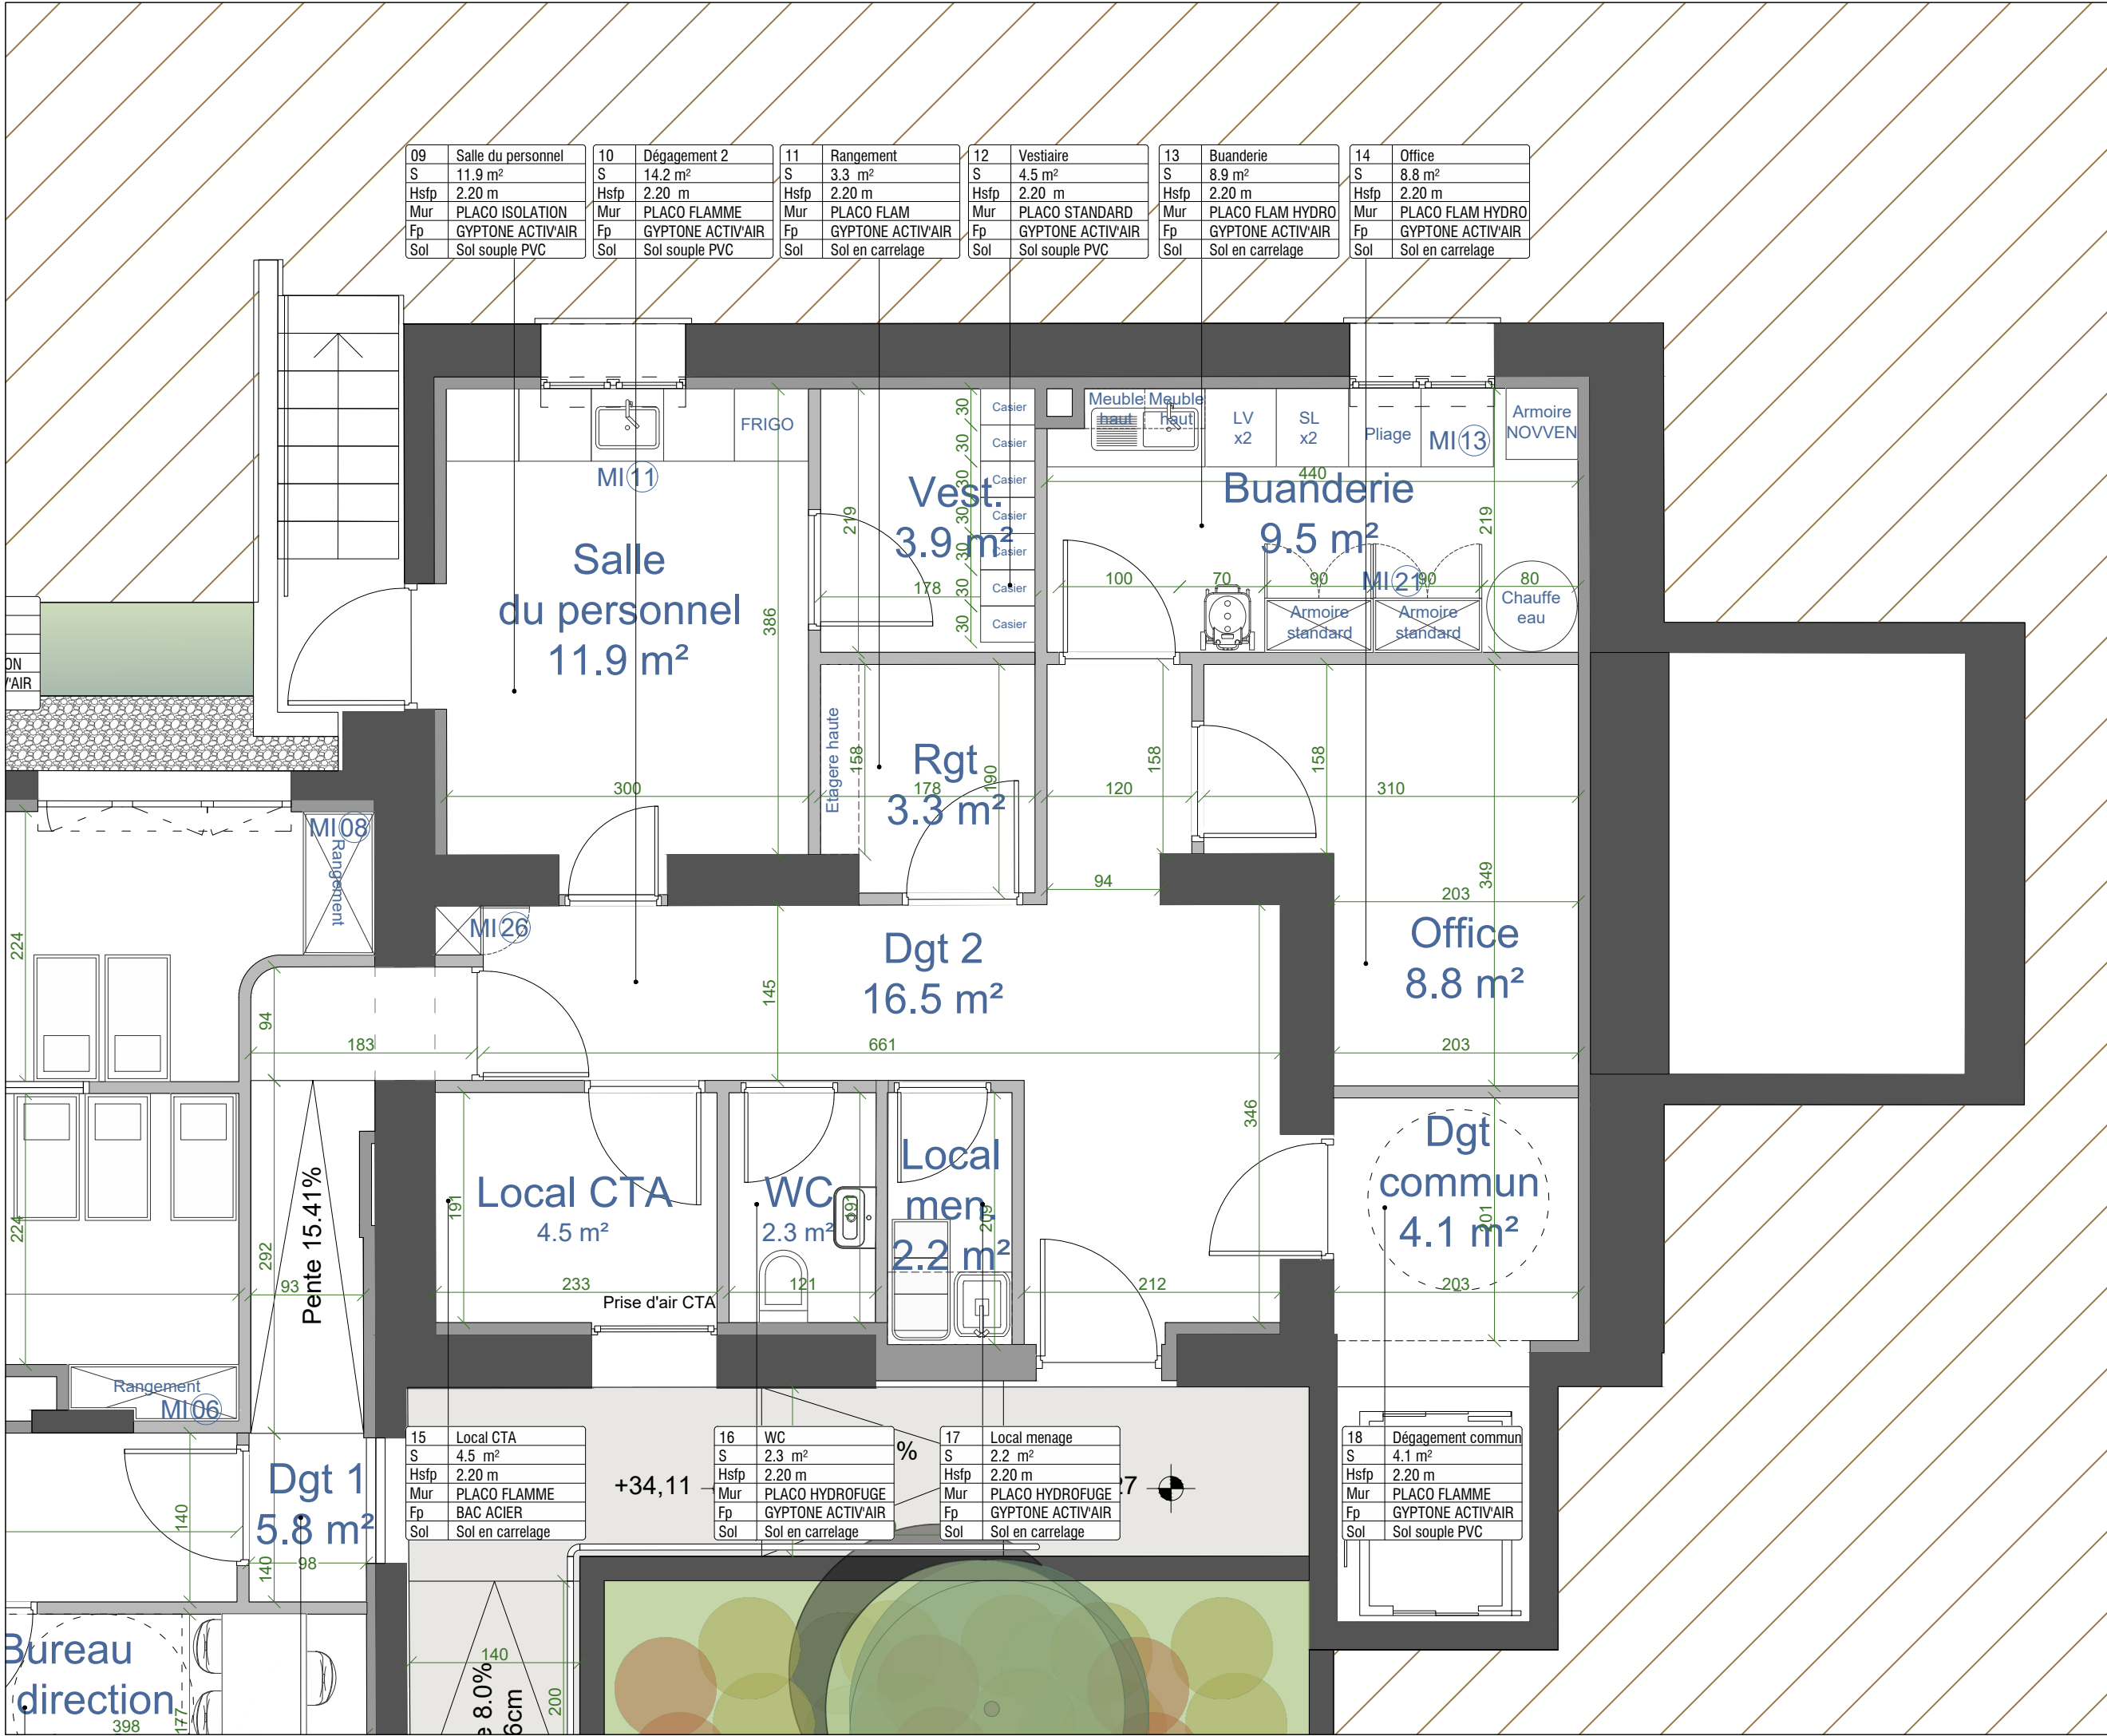

CREATION D'UN MULTI-ACCUEIL ET D'UNE MAISON MEDICALE 78400 CHATOU			
MOA	SARL LPC YVELINES 15 Rue de l'Orient78000 VERSAILLES		
MOE	NAHK ARCHITECTURE 24 Rue Yves Toudic, 75010 Paris		
NOM DU DOCUMENT			
PLAN SECTEUR 3			
PHASE	PRO.DCE	ECH.	1/50
INDICE	1.1	DATE	30/06/2023
MODIFICATIONS			
INDICE DATE OBJET			
1.1	30/06/2023	Diffusion initiale	

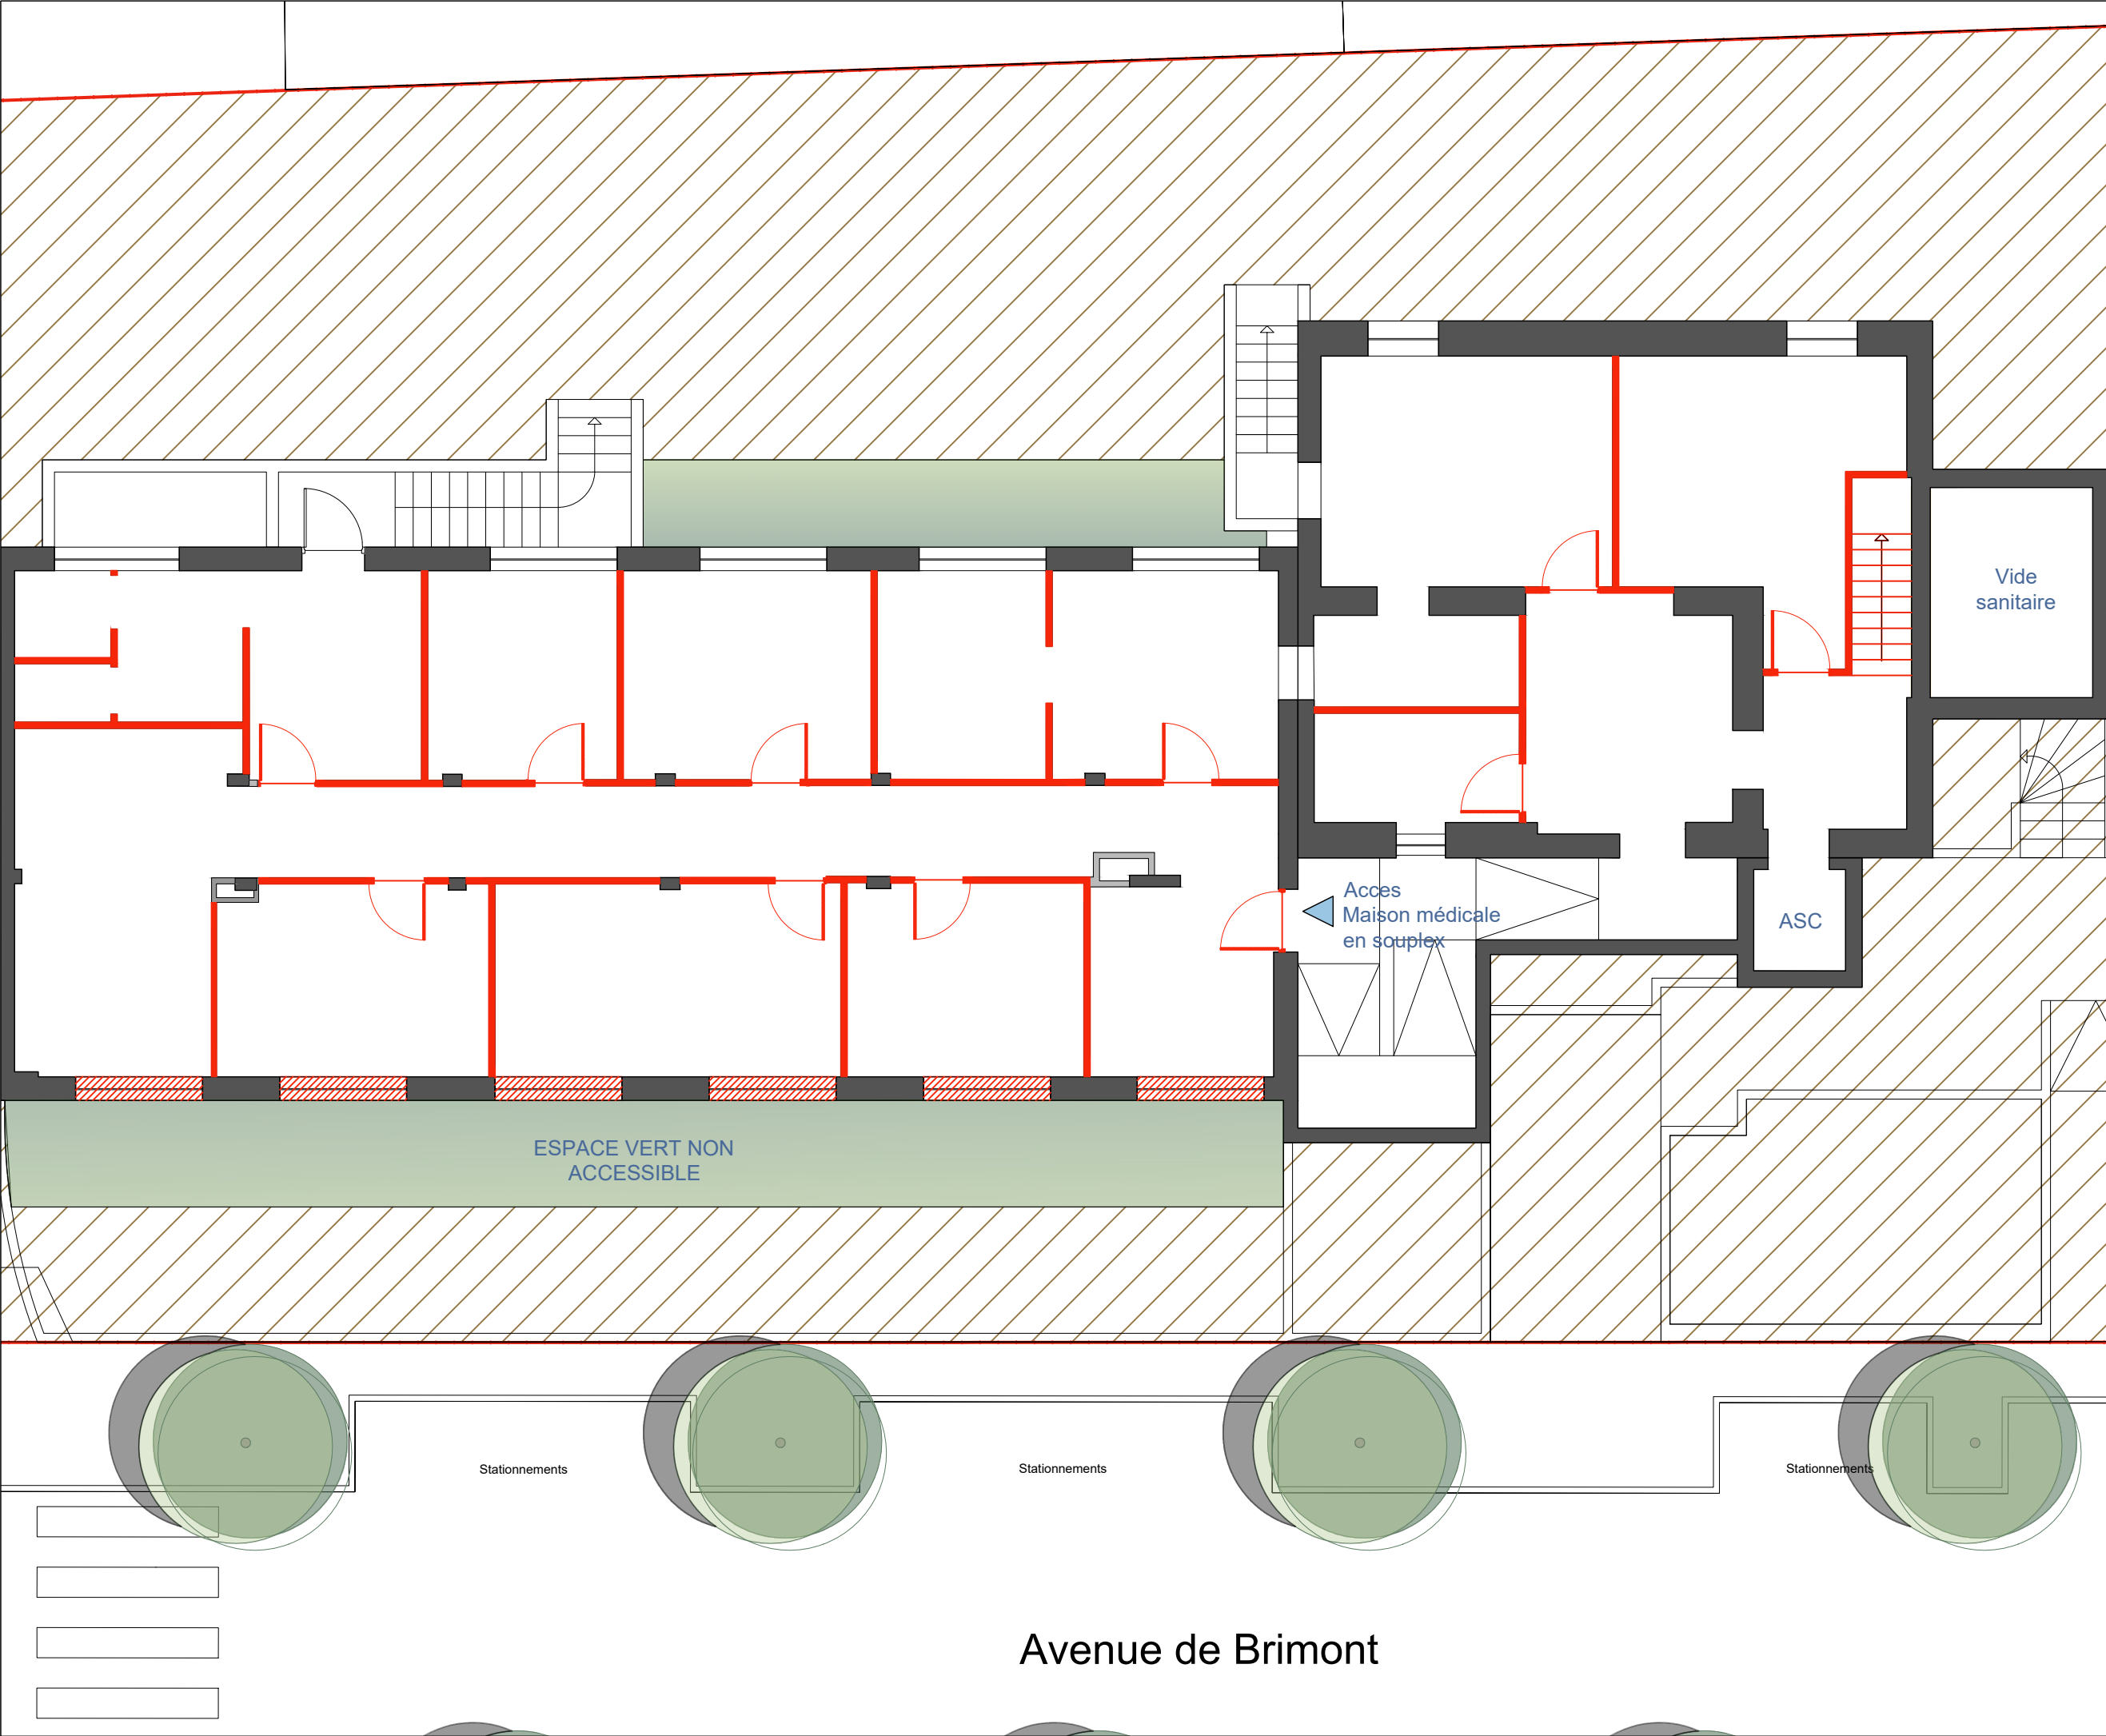

CREATION D'UN MULTI-ACCUEIL
ET D'UNE MAISON MEDICALE
78400 CHATOU

MOA

SARL LPC YVELINES
15 Rue de l'Orient78000 VERSAILLES

MOE

NAHK ARCHITECTURE
24 Rue Yves Toudic, 75010 Paris

NOM DU DOCUMENT

PLAN DE LOCALISATION
DES DEMOLITIONS

PHASE

PRO.DCE

ECH.

1/100

INDICE

1.1

DATE

30/06/2023

MODIFICATIONS

INDICE

DATE

OBJET

1.1


30/06/2023

Diffusion initiale

DEMOLITION

• CLOISON DEMOLIE

• ALLEE DEMOLIE

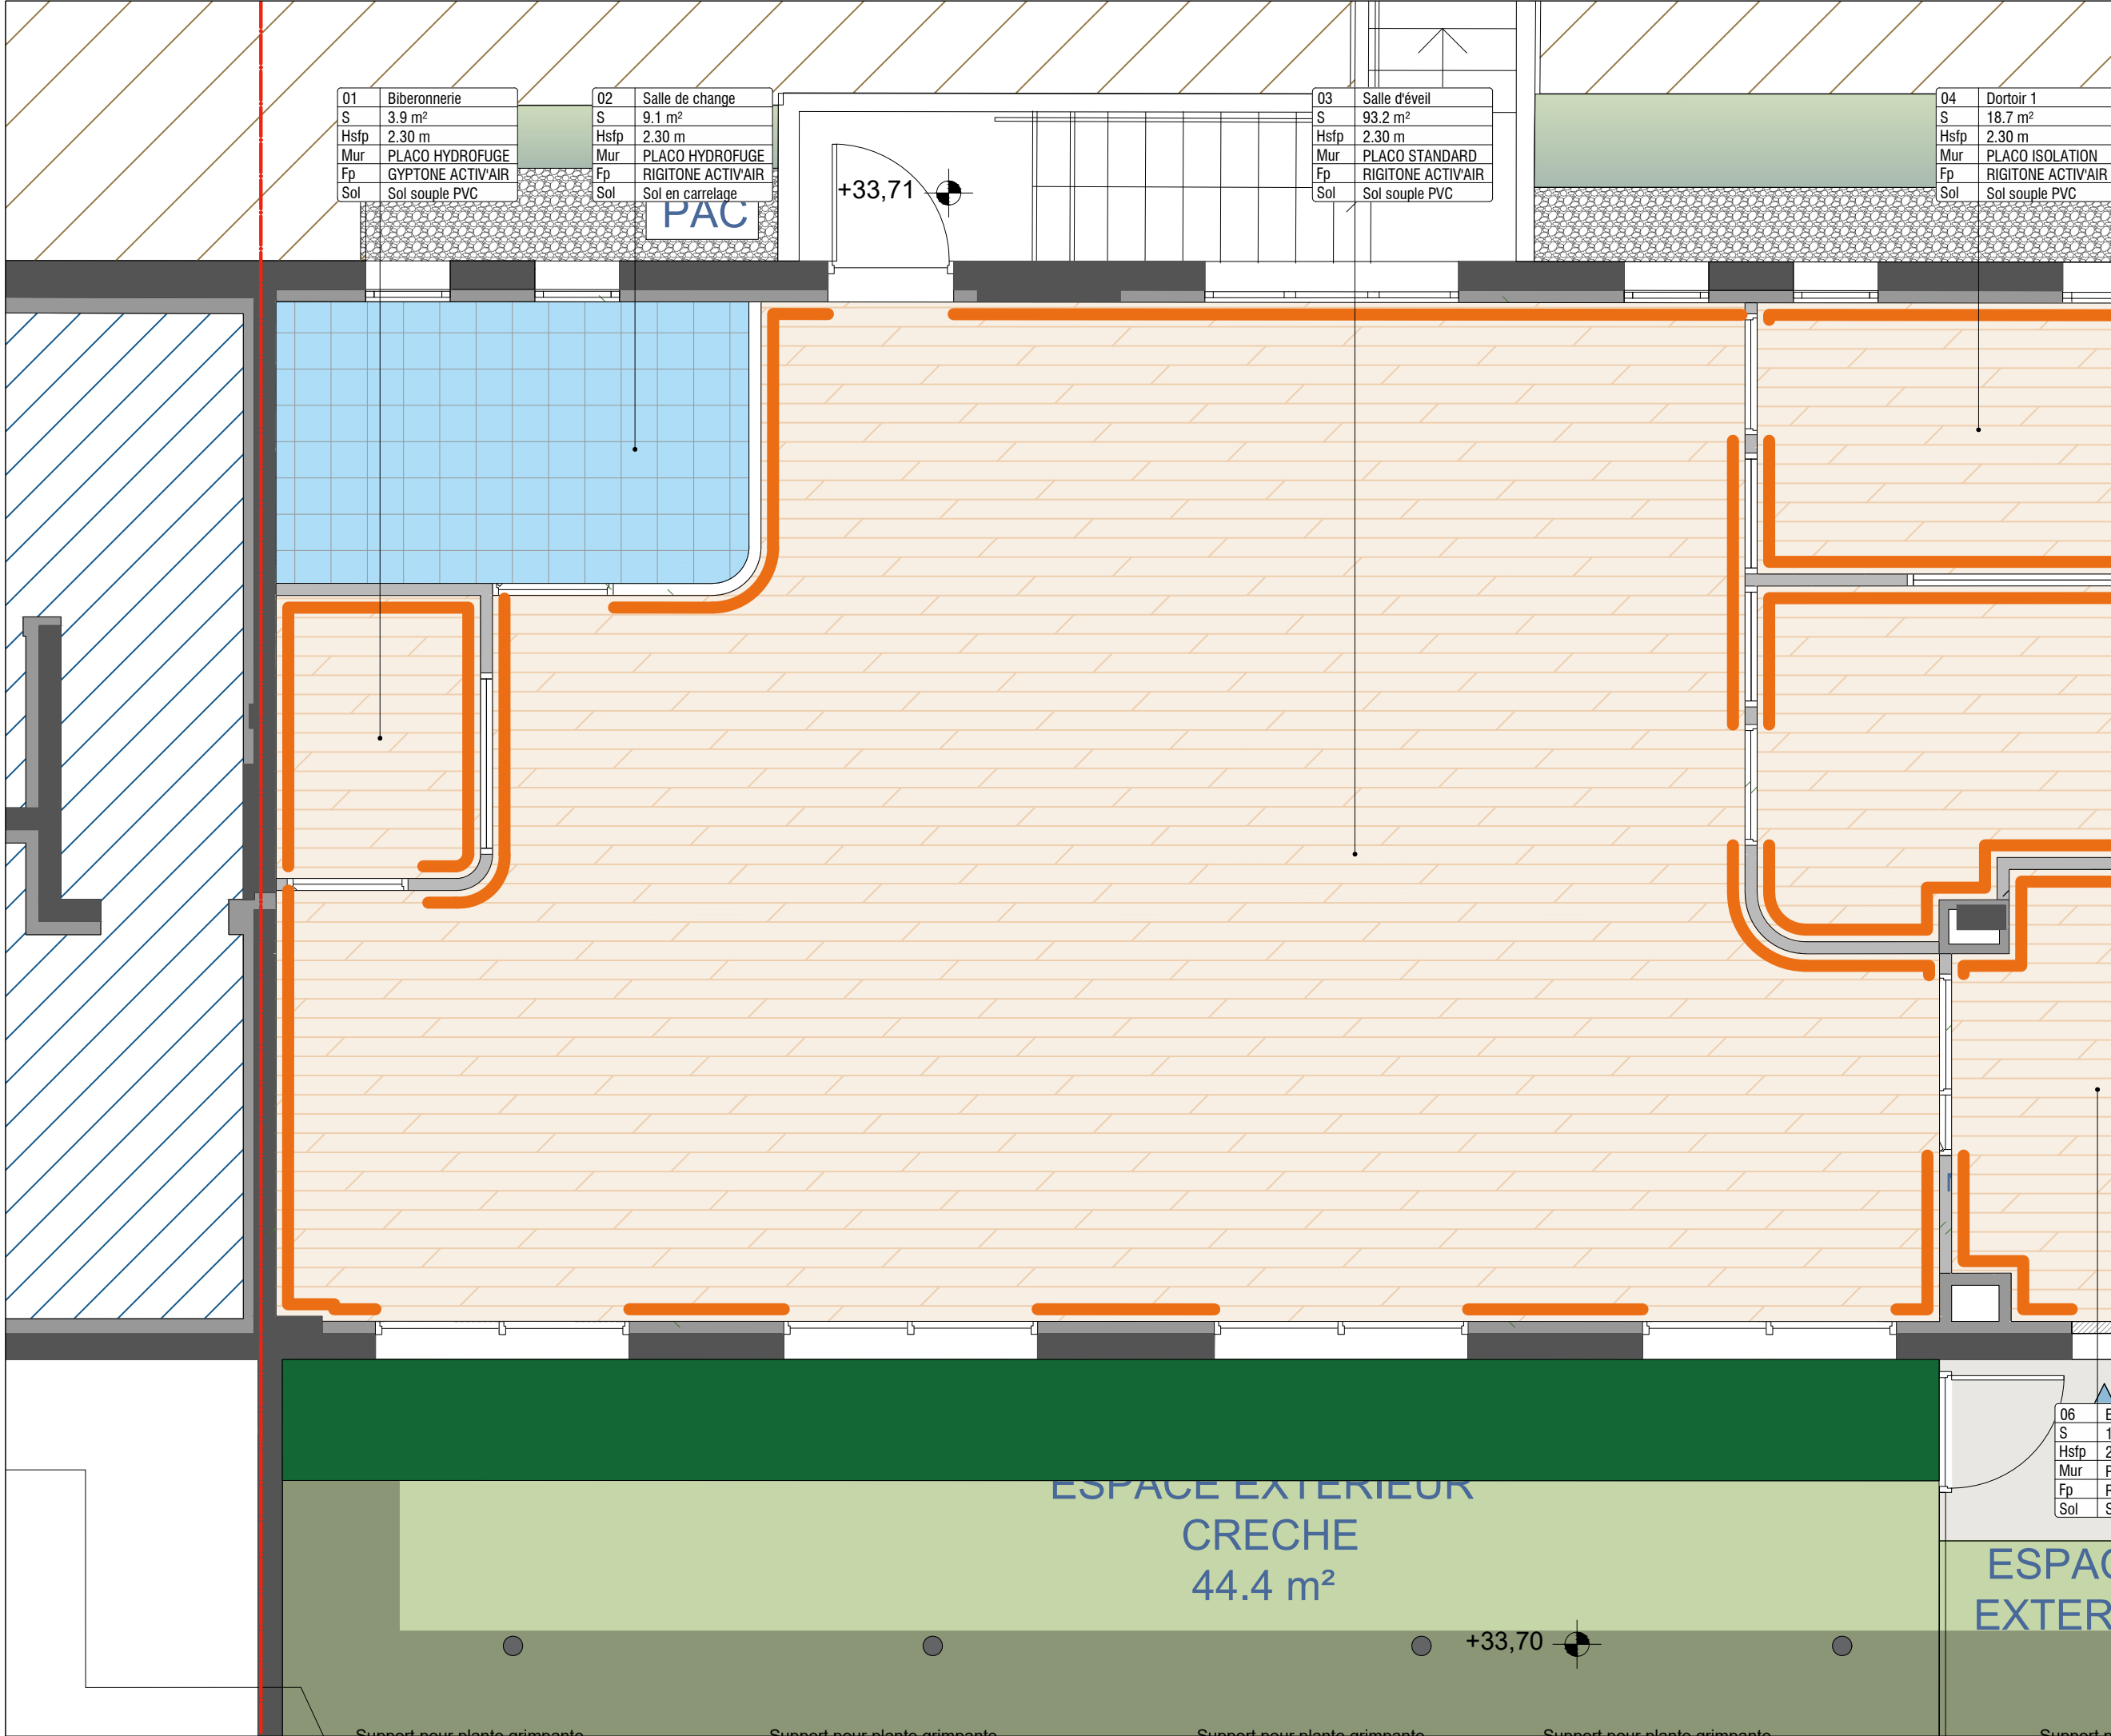

CREATION D'UN MULTI-ACCUEIL
ET D'UNE MAISON MEDICALE
78400 CHATOU

MOA

SARL LPC YVELINES
15 Rue de l'Orient78000 VERSAILLES

MOE

NAHK ARCHITECTURE
24 Rue Yves Toudic, 75010 Paris

NOM DU DOCUMENT

REVETEMENTS DE SOL
SECTEUR 1

PHASE

PRO.DCE

ECH.

1/50

INDICE

1.1

DATE

30/06/2023

MODIFICATIONS

INDICE

DATE

OBJET

1.1

30/06/2023

Diffusion initiale


LOT SOL SOUPLE / SOL DUR / PLINTHE

• GAZON SYNTHETIQUE
Ref. English Lawn Valeria
ou équivalent

• SOL SOUPLE PVC EN LAMES
Ref. Amtico Click Smart White Oak

• SOL EN CARRELAGE
TYPE GRES CERAME R9 MIN

• PLINTHE EN BOIS

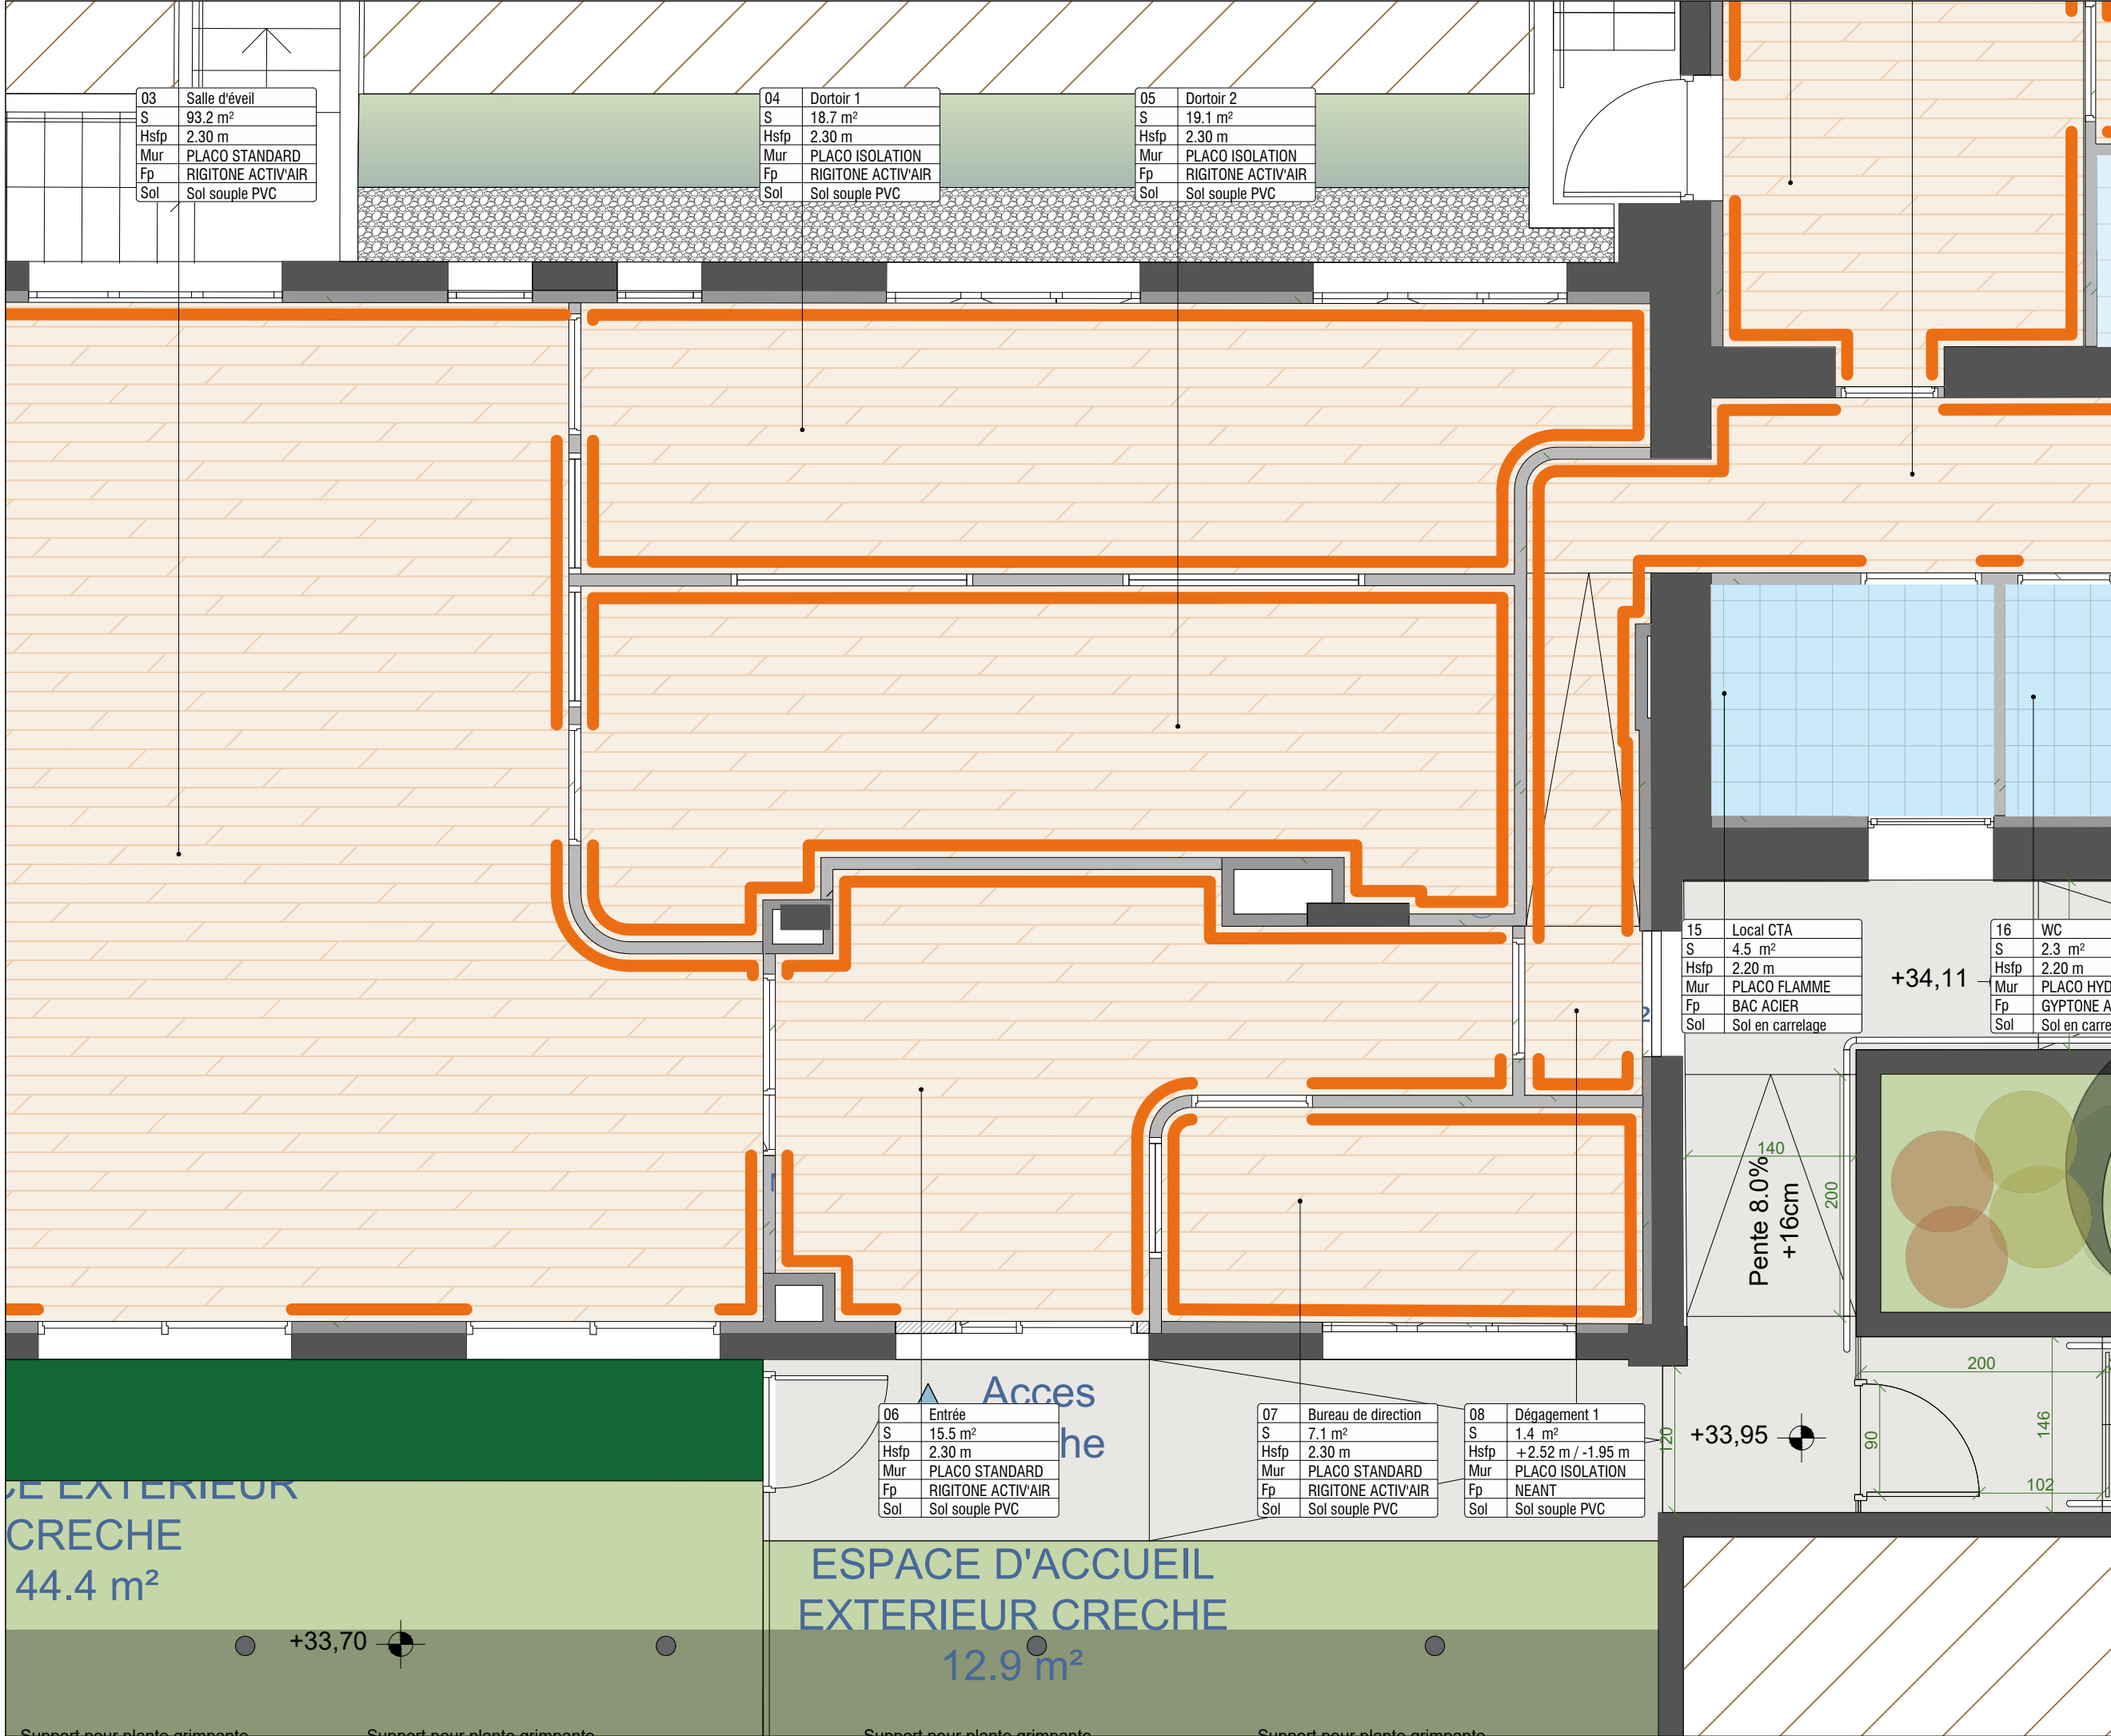

CREATION D'UN MULTI-ACCUEIL
ET D'UNE MAISON MEDICALE
78400 CHATOU

MOA

SARL LPC YVELINES
15 Rue de l'Orient78000 VERSAILLES

MOE

NAHK ARCHITECTURE
24 Rue Yves Toudic, 75010 Paris

NOM DU DOCUMENT

REVETEMENTS DE SOL
SECTEUR 2

PHASE

PRO.DCE

ECH.

1/50

INDICE

1.1

DATE

30/06/2023

MODIFICATIONS

INDICE

DATE

OBJET

1.1

30/06/2023

Diffusion initiale


LOT SOL SOUPLE / SOL DUR / PLINTHE


• GAZON SYNTHETIQUE
Ref. English Lawn Valeria
ou équivalent


• SOL SOUPLE PVC EN LAMES
Ref. Amtico Click Smart White Oak


• SOL EN CARRELAGE
TYPE GRES CERAME R9 MIN

• PLINTHE EN BOIS

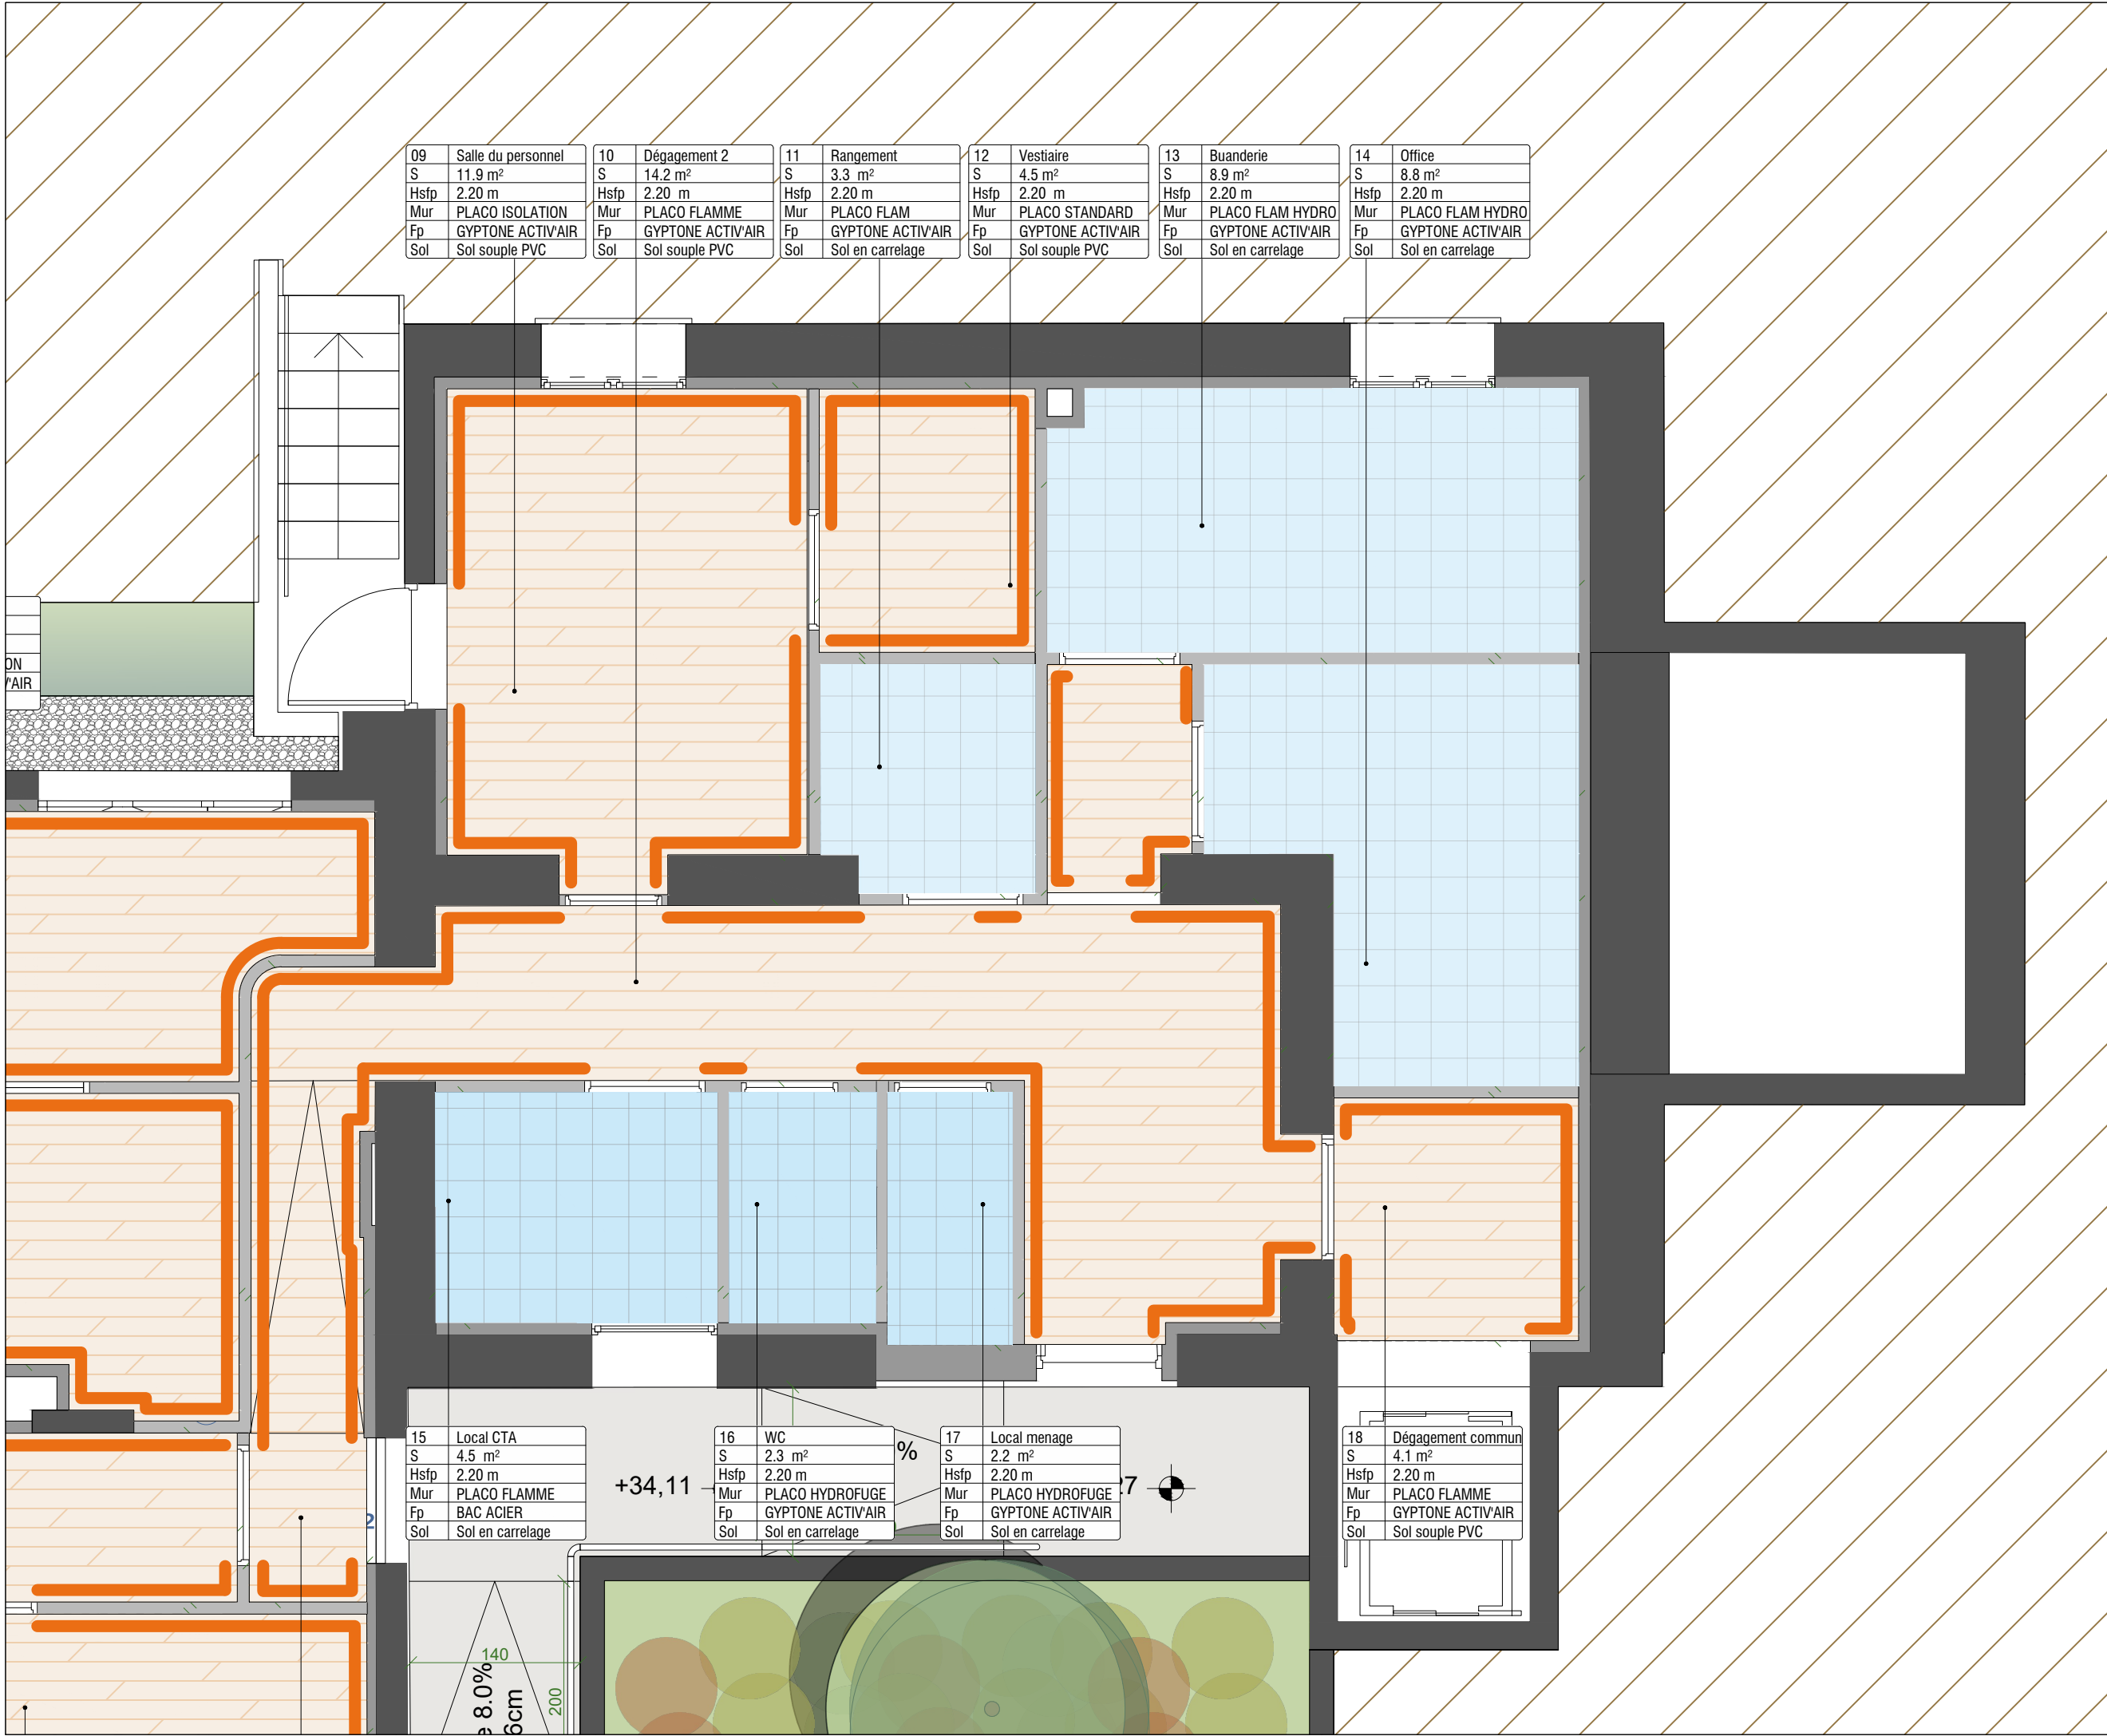


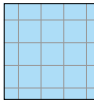CREATION D'UN MULTI-ACCUEIL ET D'UNE MAISON MEDICALE 78400 CHATOU			
MOA	SARL LPC YVELINES 15 Rue de l'Orient78000 VERSAILLES		
MOE	NAHK ARCHITECTURE 24 Rue Yves Toudic, 75010 Paris		
NOM DU DOCUMENT			
REVETEMENTS DE SOL SECTEUR 3			
PHASE	PRO.DCE	ECH.	1/50
INDICE	1.1	DATE	30/06/2023
MODIFICATIONS			
INDICE	DATE	OBJET	
1.1	30/06/2023	Diffusion initiale	
LOT SOL SOUPLE / SOL DUR / PLINTHE			
 • GAZON SYNTHETIQUE Ref. English Lawn Valeria ou équivalent			
 • SOL SOUPLE PVC EN LAMES Ref. Amtico Click Smart White Oak			
 • SOL EN CARRELAGE TYPE GRES CERAME R9 MIN			
 • PLINTHE EN BOIS			

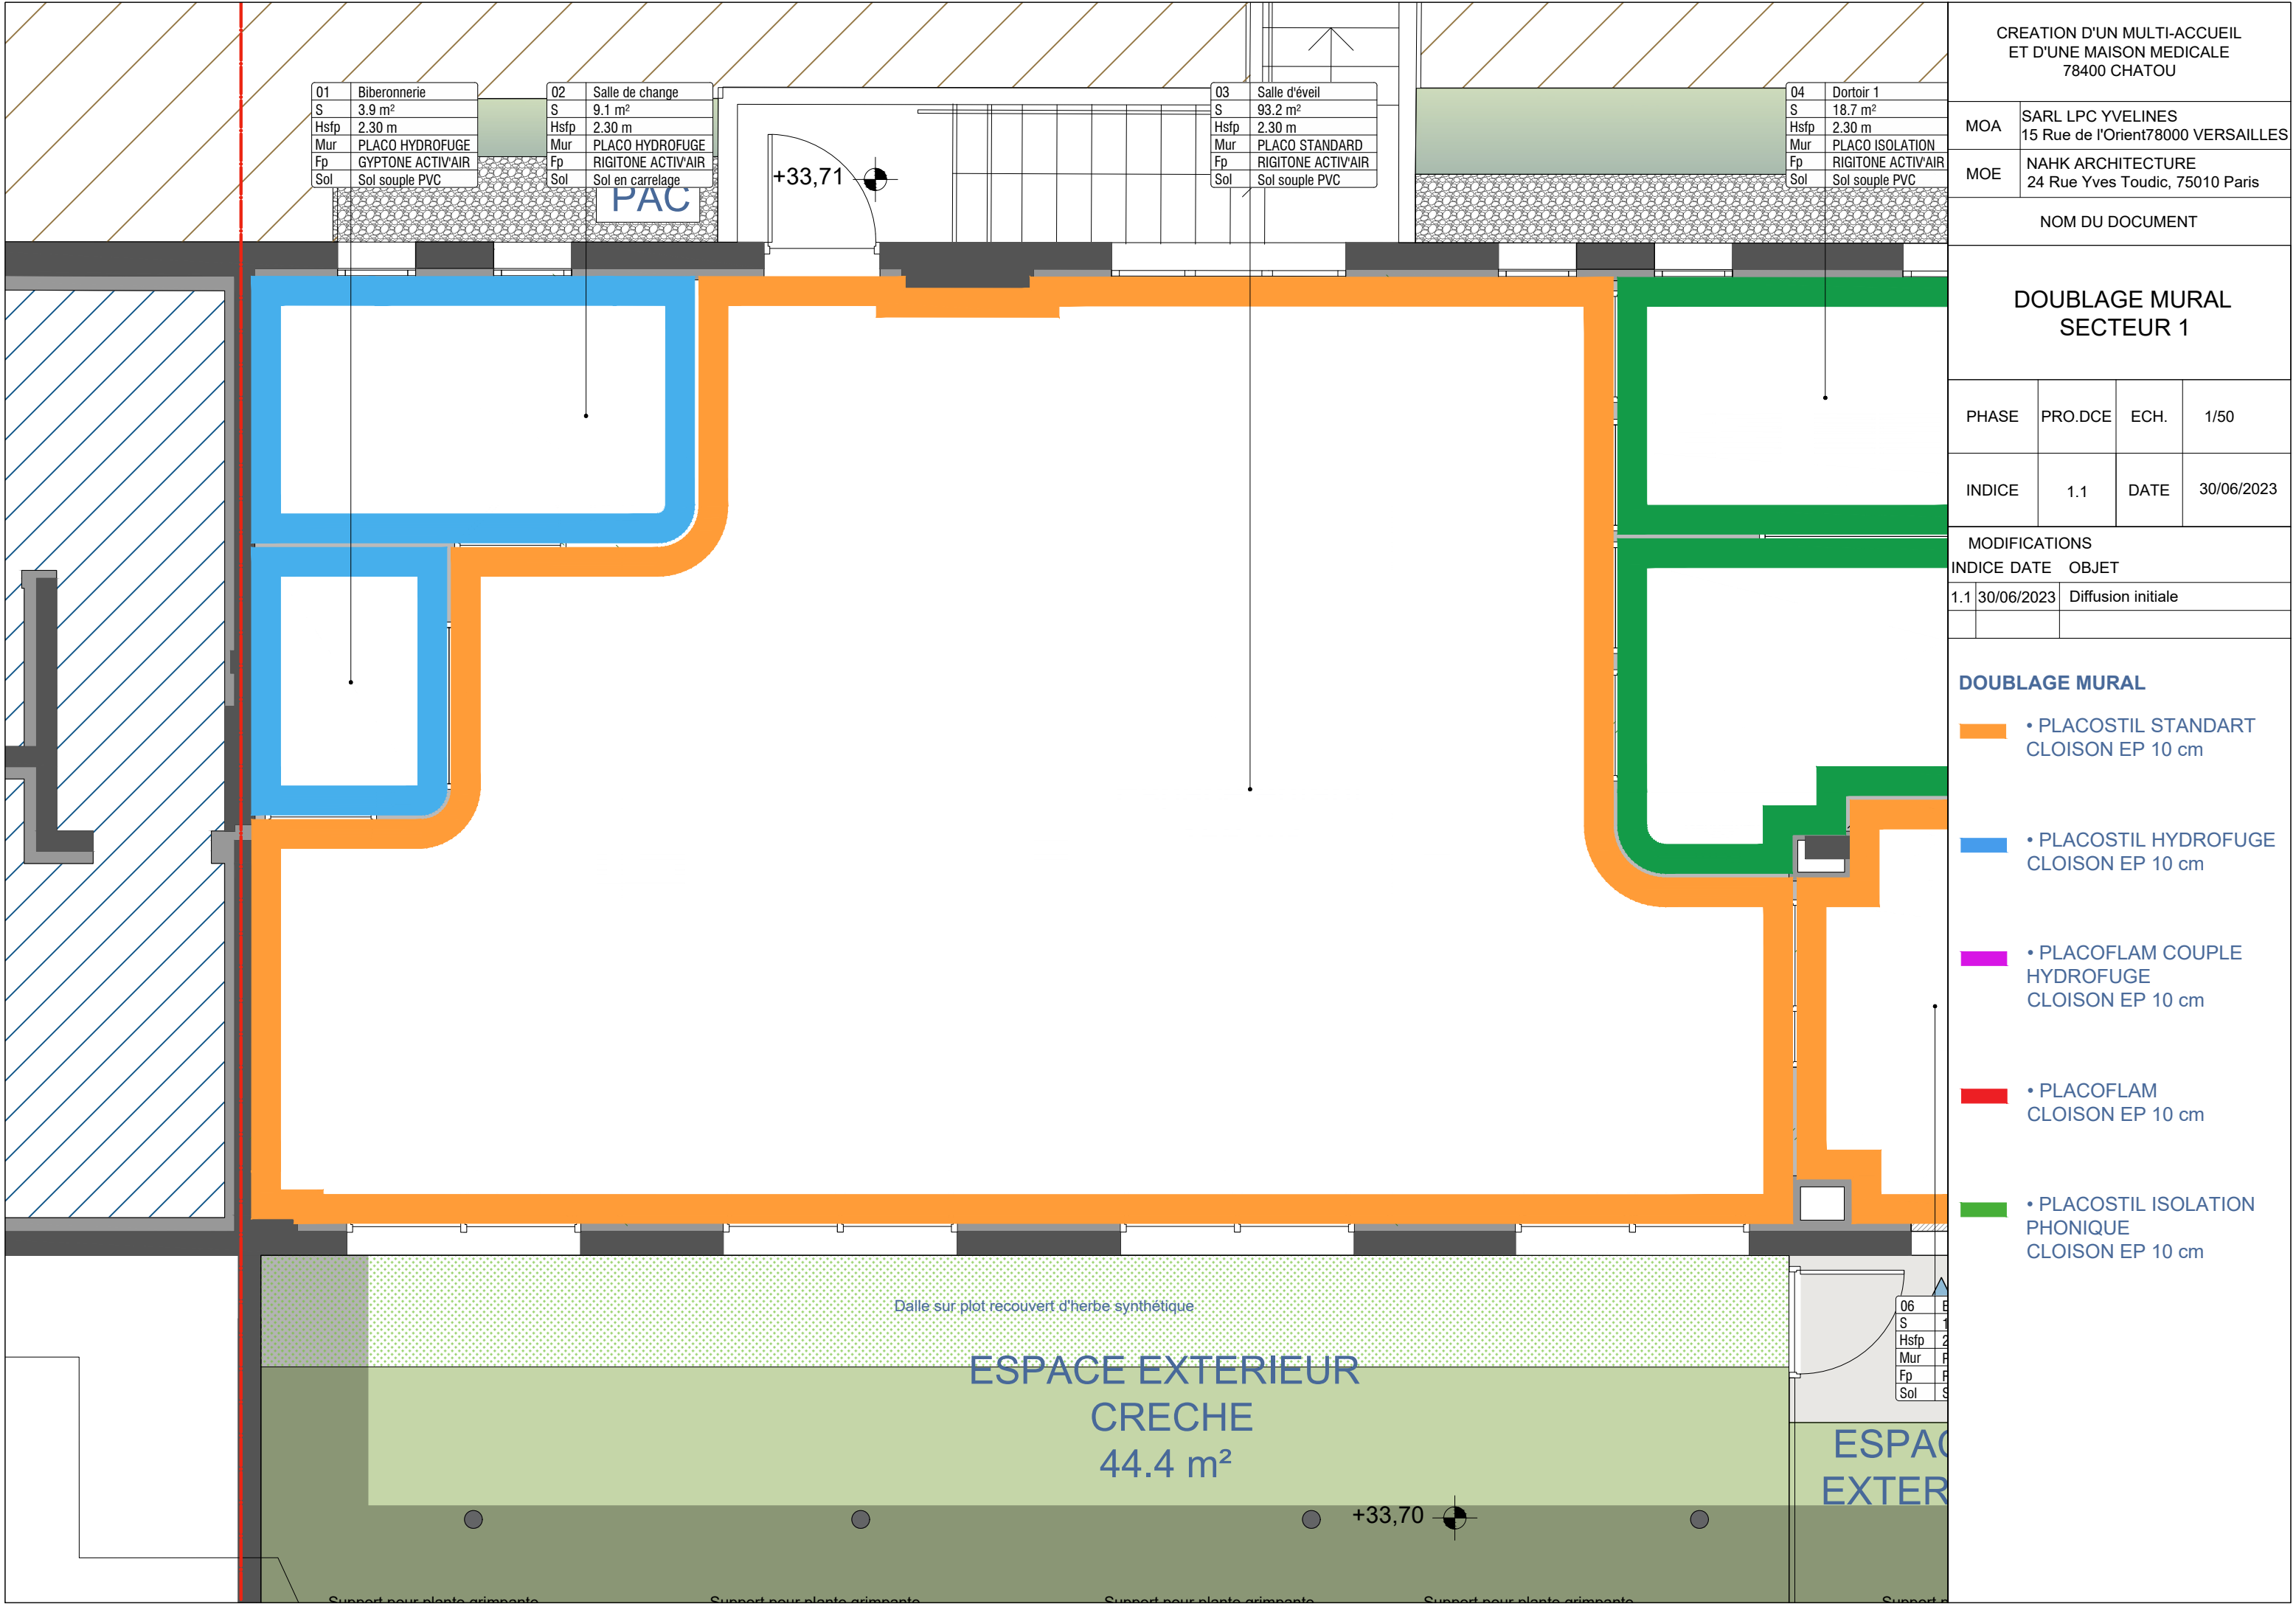


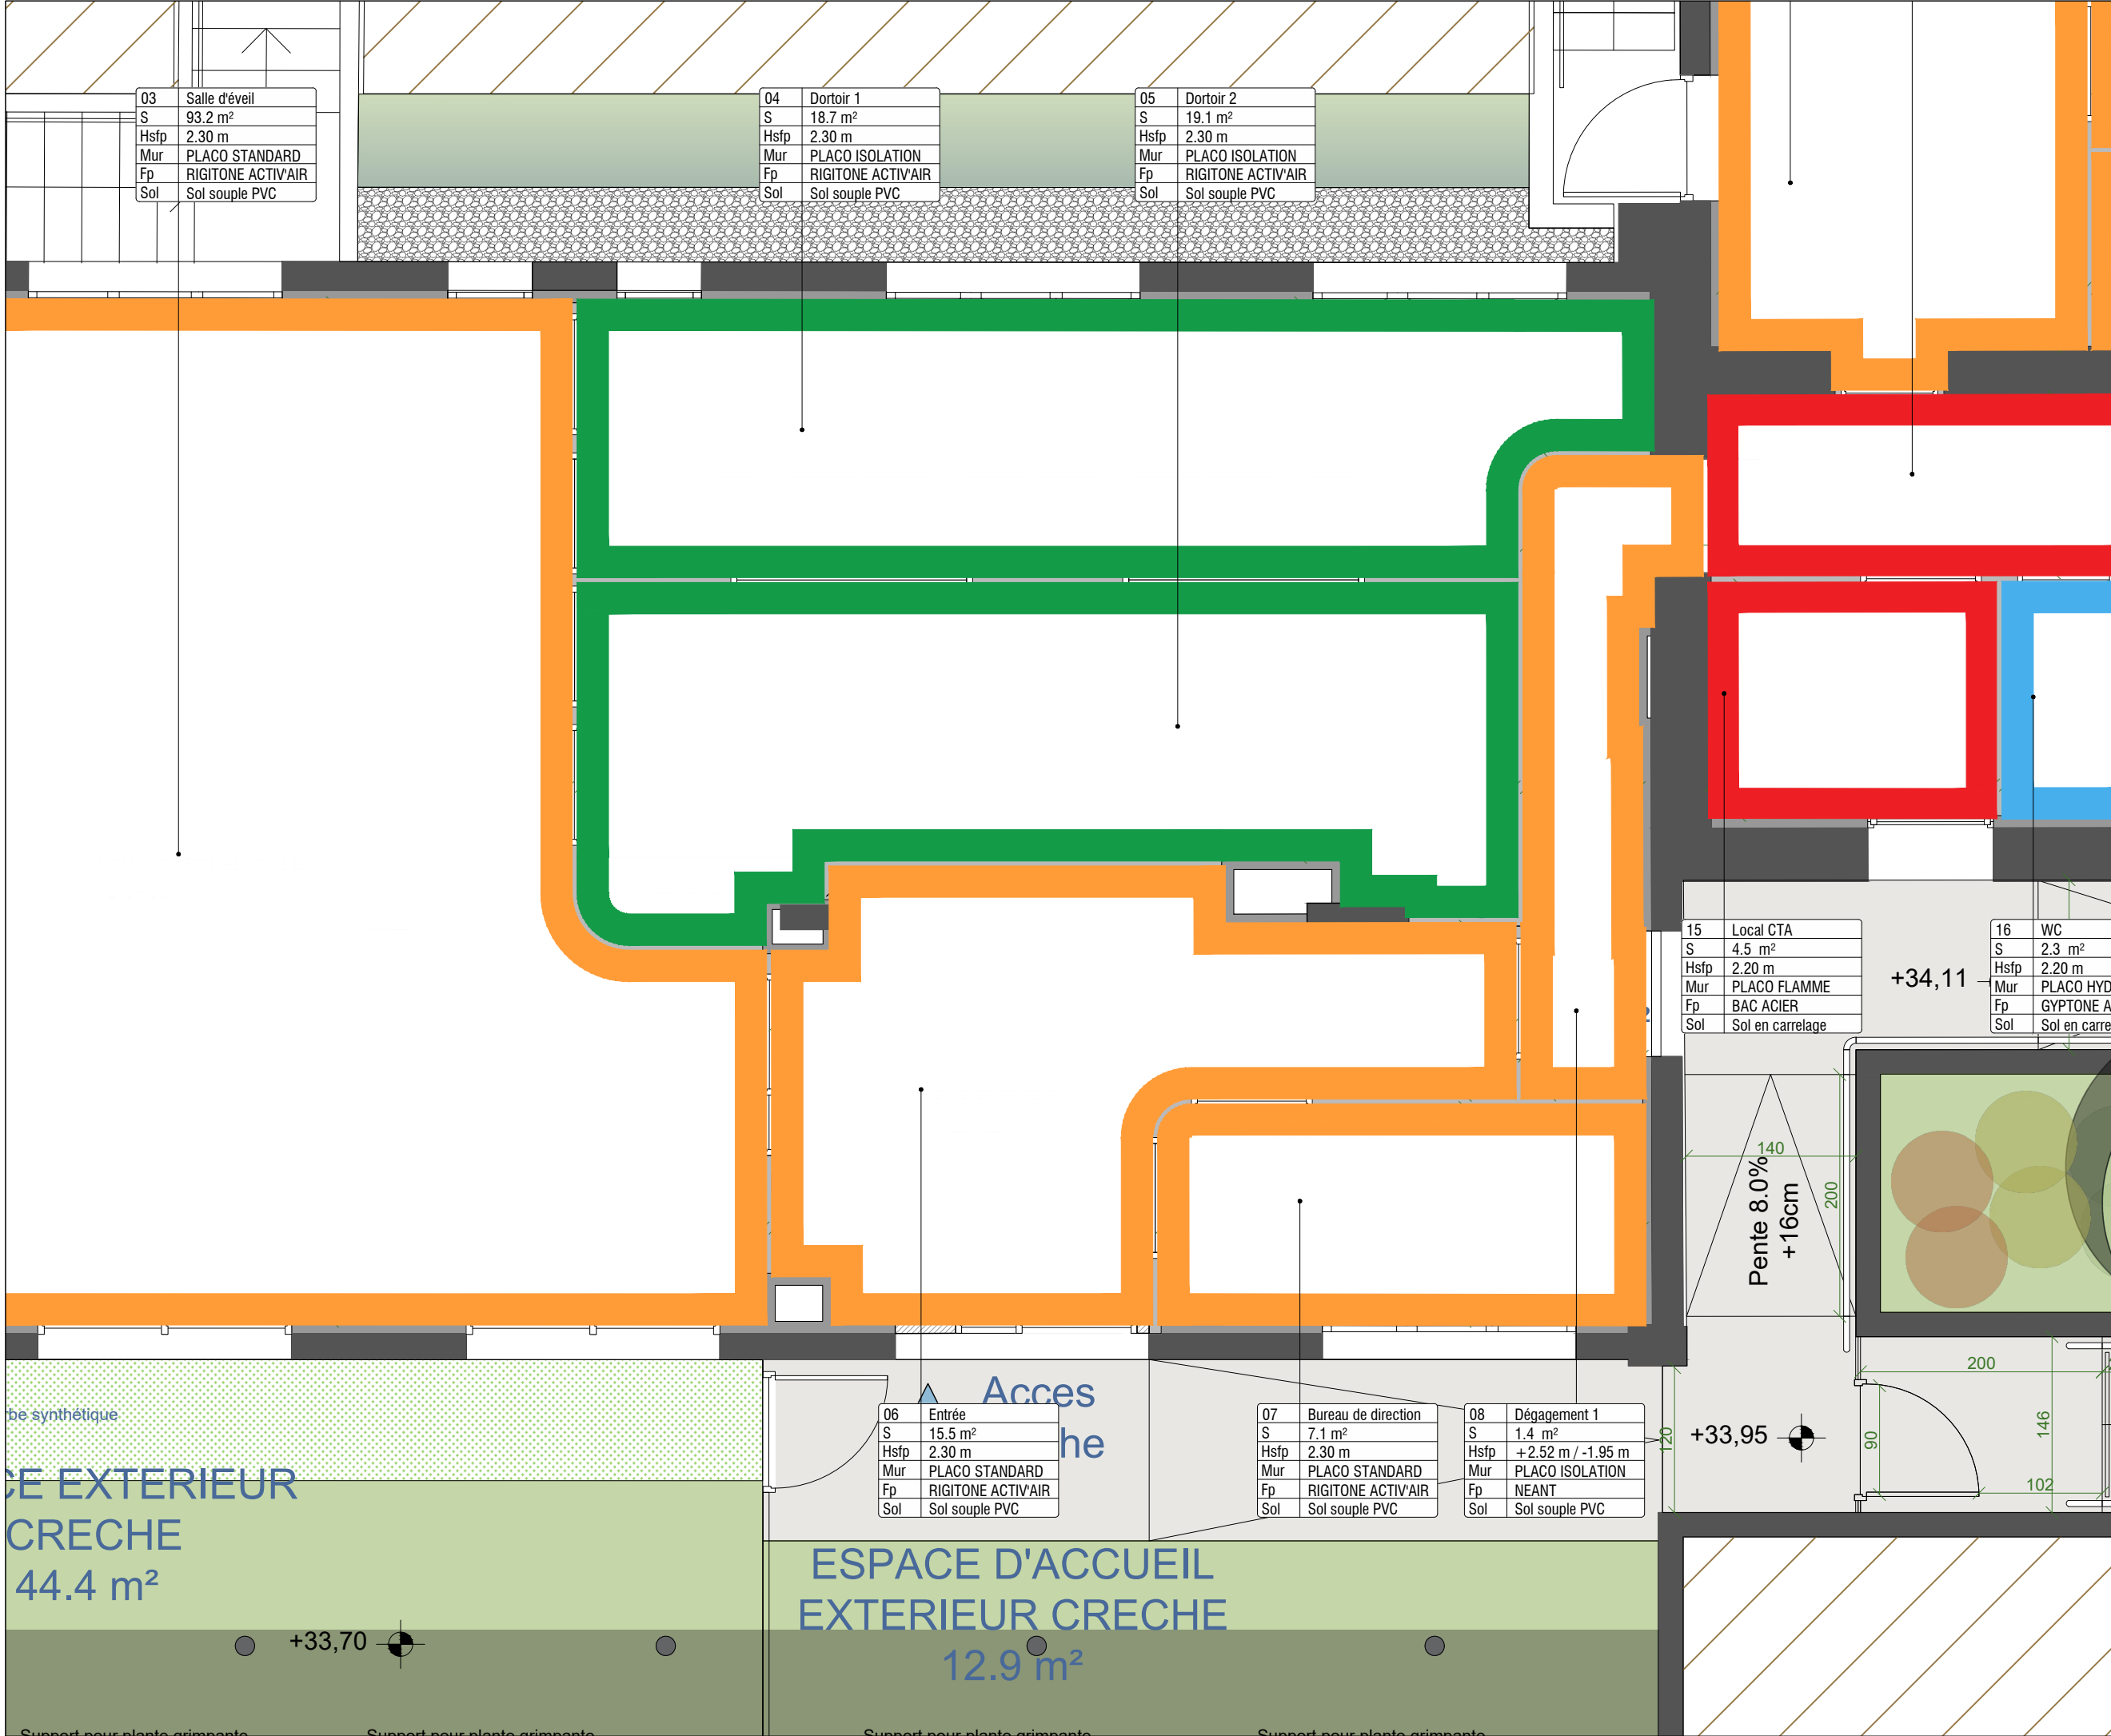


CREATION D'UN MULTI-ACCUEIL ET D'UNE MAISON MEDICALE 78400 CHATOU			
MOA	SARL LPC YVELINES 15 Rue de l'Orient78000 VERSAILLES		
MOE	NAHK ARCHITECTURE 24 Rue Yves Toudic, 75010 Paris		
NOM DU DOCUMENT			
DOUBLAGE MURAL SECTEUR 2			
PHASE	PRO.DCE	ECH.	1/50
INDICE	1.1	DATE	30/06/2023
MODIFICATIONS			
INDICE	DATE	OBJET	
1.1	30/06/2023	Diffusion initiale	
DOUBLAGE MURAL • PLACOSTIL STANDART CLOISON EP 10 cm • PLACOSTIL HYDROFUGE CLOISON EP 10 cm • PLACOFLAM COUPLE HYDROFUGE CLOISON EP 10 cm • PLACOFLAM CLOISON EP 10 cm • PLACOSTIL ISOLATION PHONIQUE CLOISON EP 10 cm			

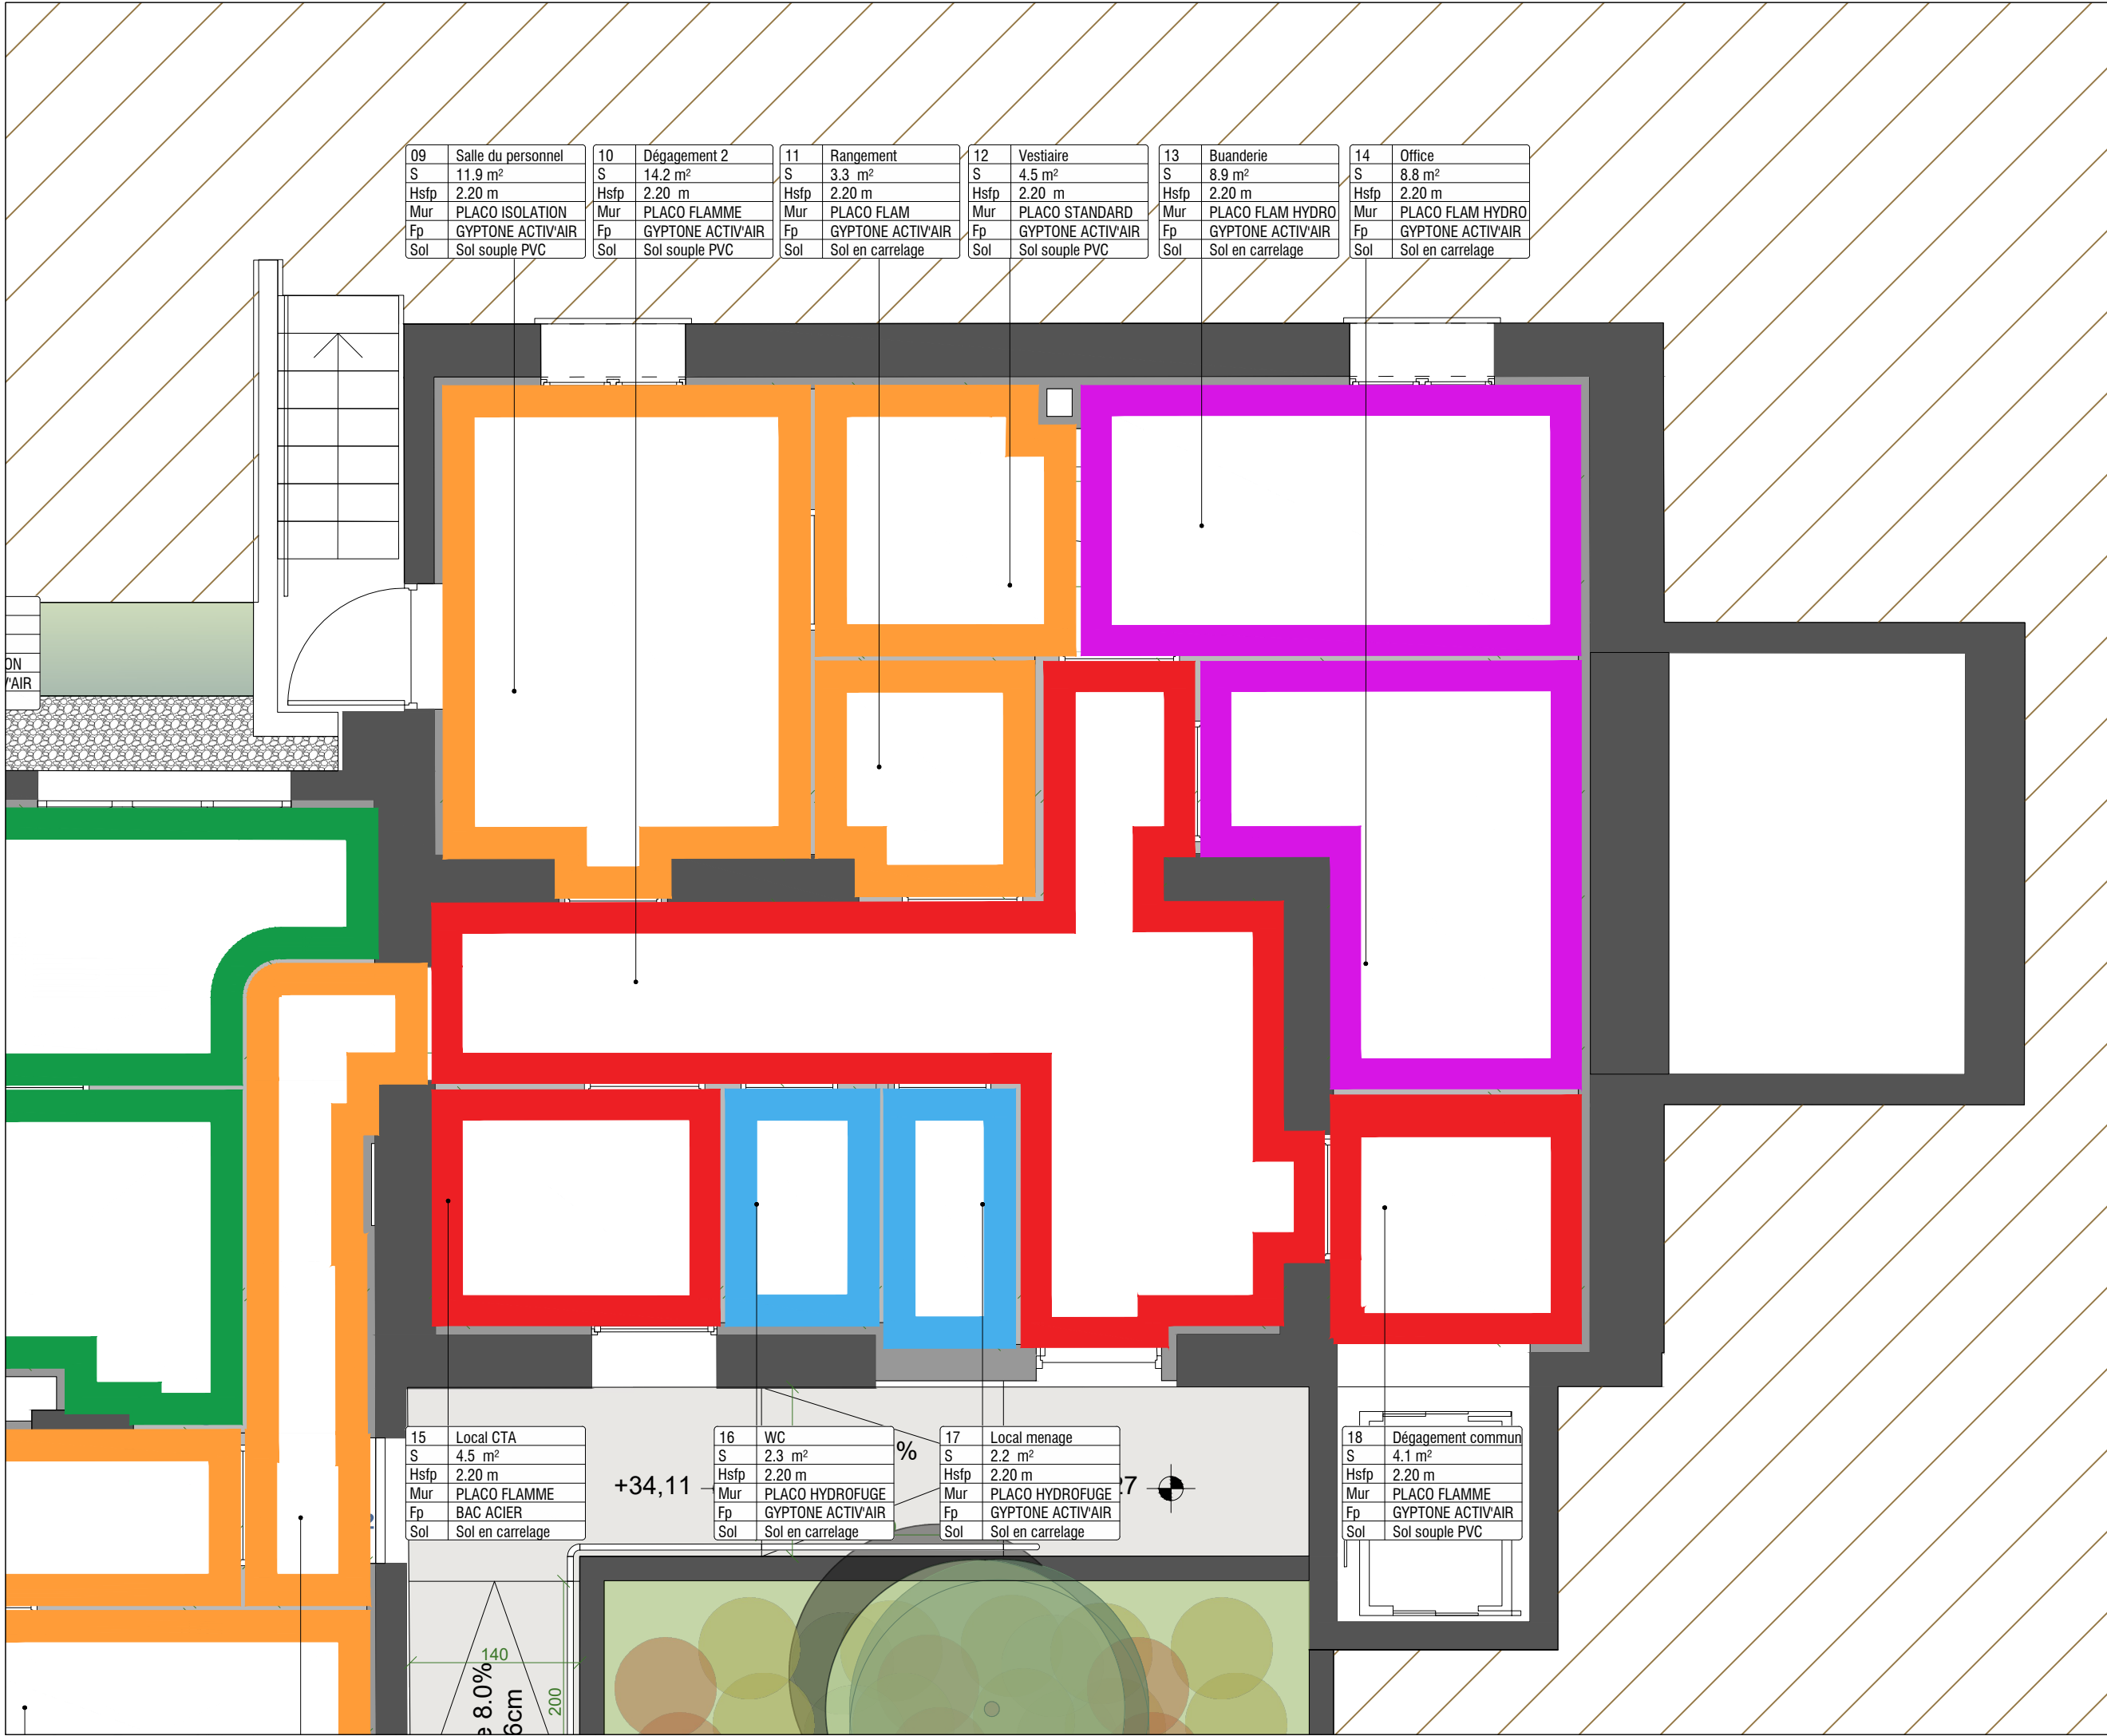

CREATION D'UN MULTI-ACCUEIL ET D'UNE MAISON MEDICALE 78400 CHATOU			
MOA	SARL LPC YVELINES 15 Rue de l'Orient78000 VERSAILLES		
MOE	NAHK ARCHITECTURE 24 Rue Yves Toudic, 75010 Paris		
NOM DU DOCUMENT			
DOUBLAGE MURAL SECTEUR 3			
PHASE	PRO.DCE	ECH.	1/50
INDICE	1.1	DATE	30/06/2023
MODIFICATIONS			
INDICE DATE OBJET			
1.1	30/06/2023	Diffusion initiale	
DOUBLAGE MURAL • PLACOSTIL STANDART CLOISON EP 10 cm • PLACOSTIL HYDROFUGE CLOISON EP 10 cm • PLACOFLAM COUPLE HYDROFUGE CLOISON EP 10 cm • PLACOFLAM CLOISON EP 10 cm • PLACOSTIL ISOLATION PHONIQUE CLOISON EP 10 cm			

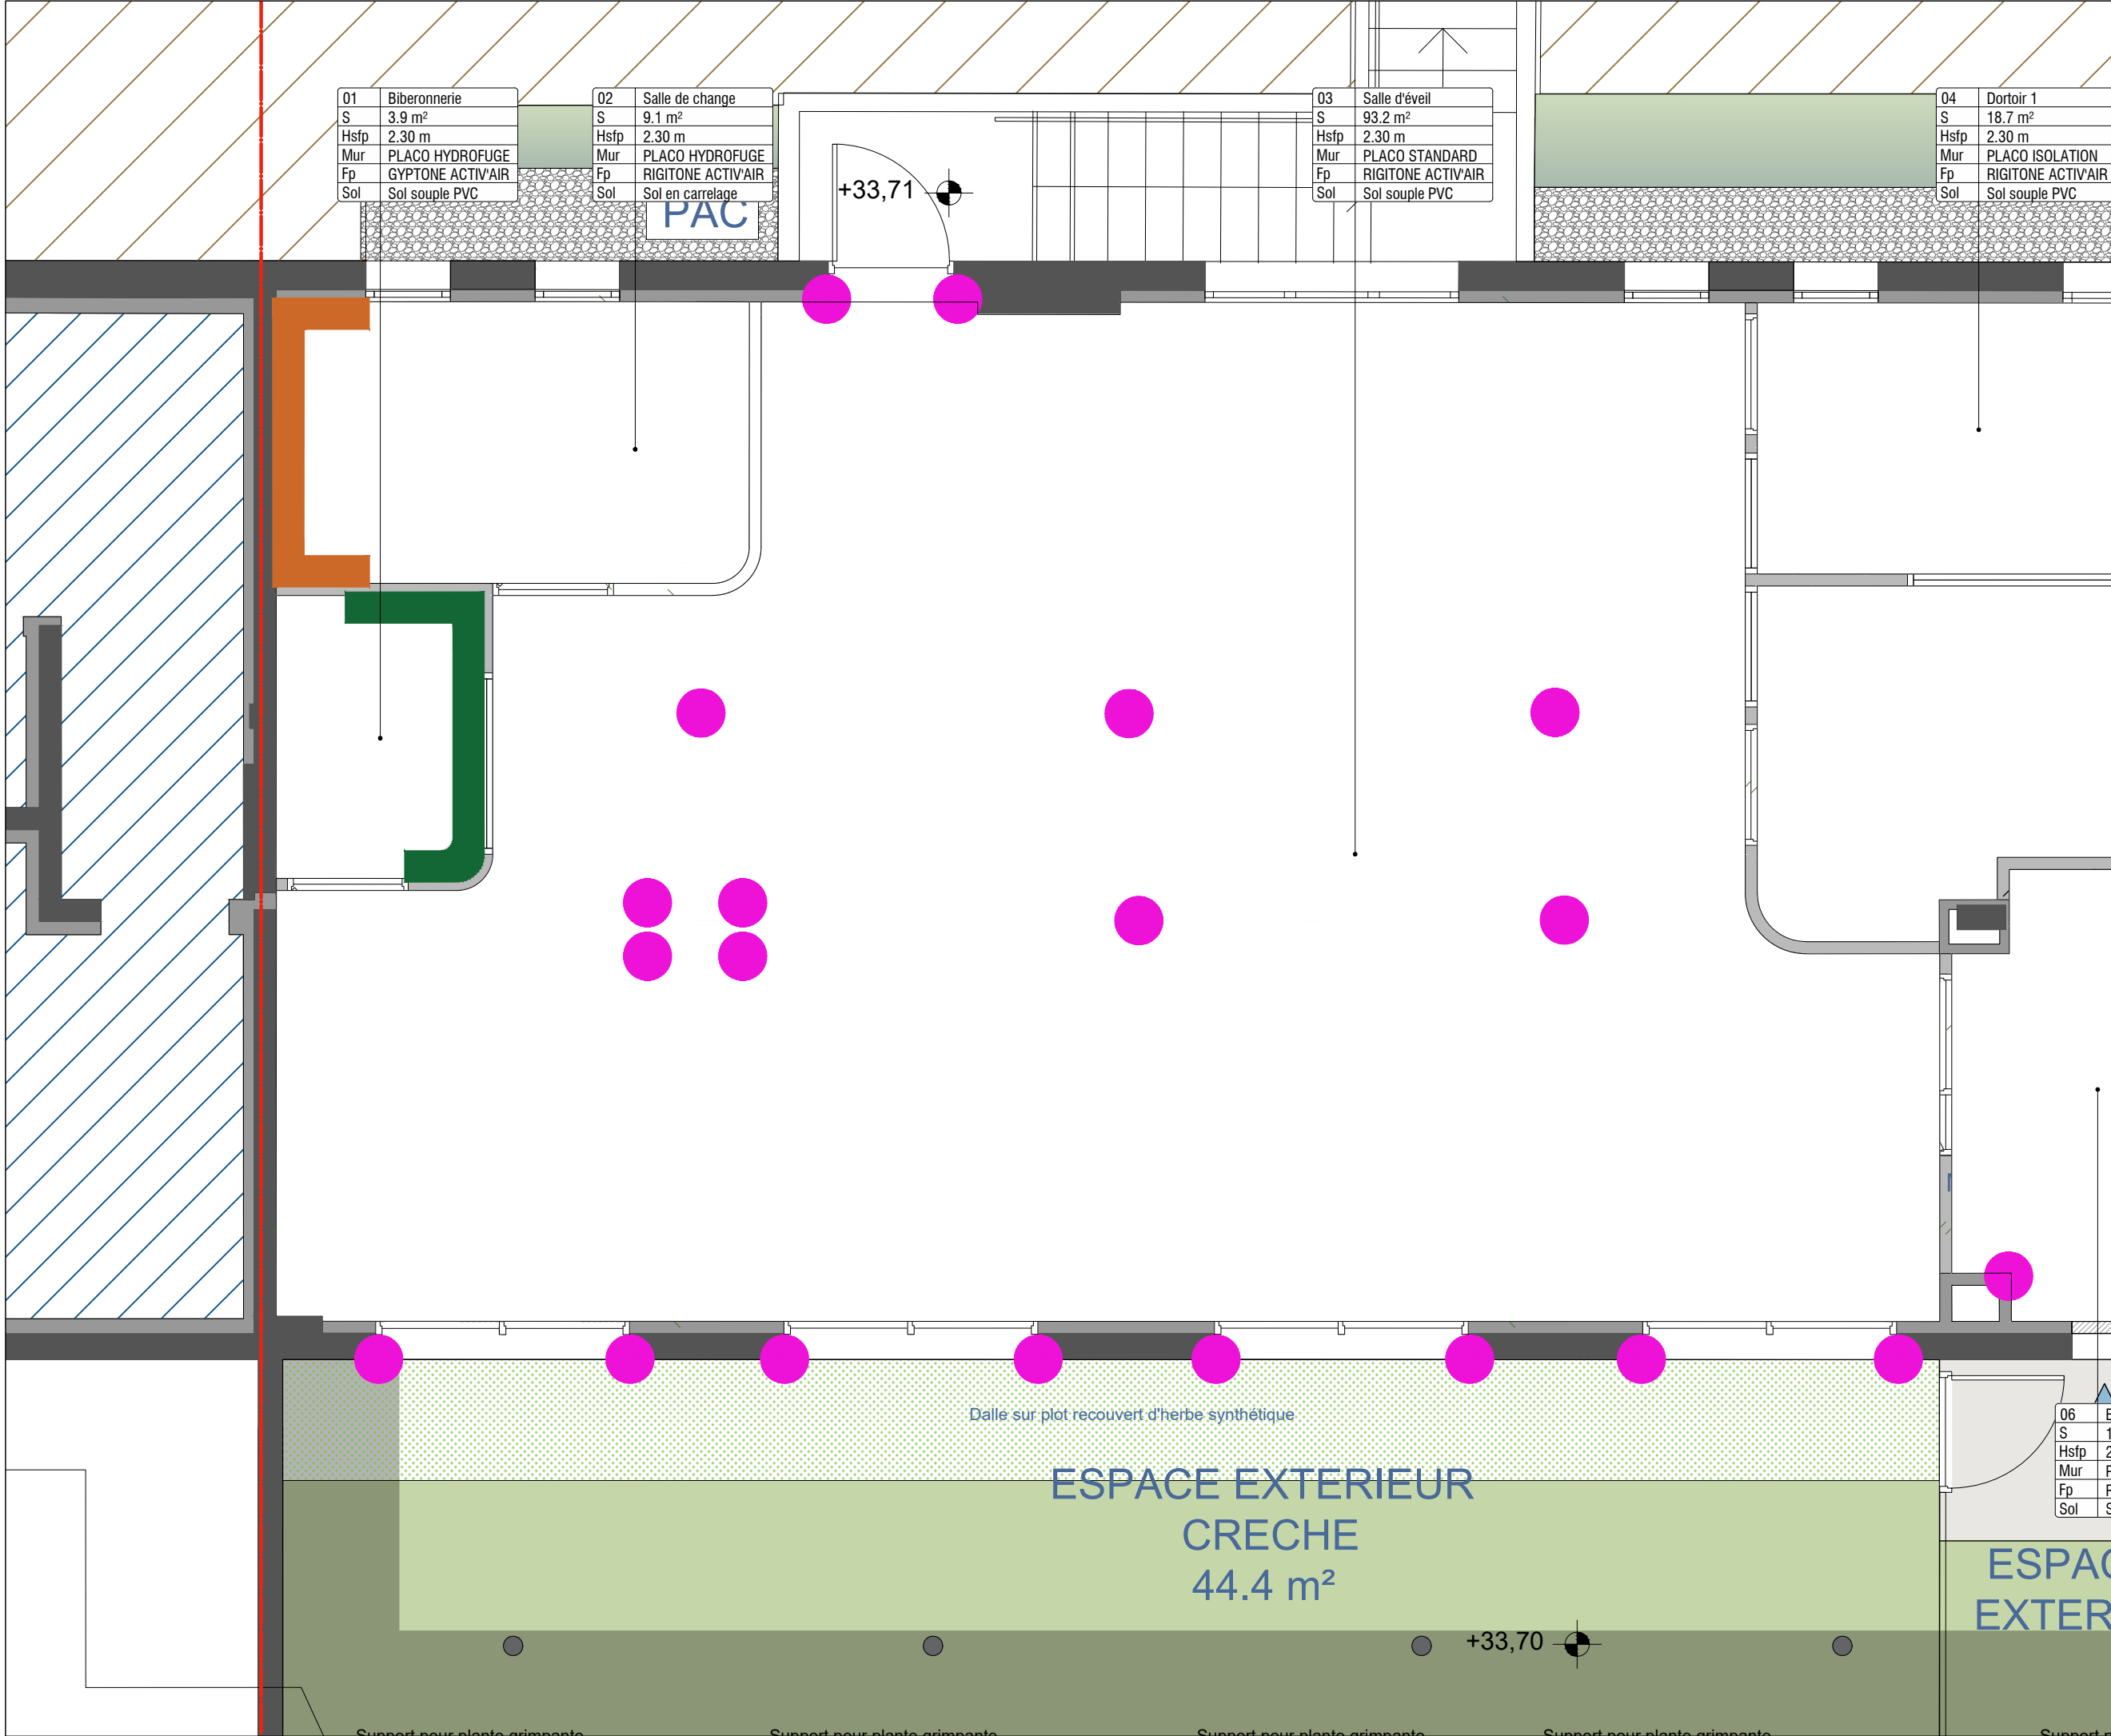

CREATION D'UN MULTI-ACCUEIL ET D'UNE MAISON MEDICALE 78400 CHATOU			
MOA	SARL LPC YVELINES 15 Rue de l'Orient78000 VERSAILLES		
MOE	NAHK ARCHITECTURE 24 Rue Yves Toudic, 75010 Paris		
NOM DU DOCUMENT			
REVETEMENT MURAL SECTEUR 1			
PHASE	PRO.DCE	ECH.	1/50
INDICE	1.1	DATE	30/06/2023
MODIFICATIONS			
INDICE DATE		OBJET	
1.1	30/06/2023	Diffusion initiale	
FAIENCE • FAIENCE TOUTE HAUTEUR SOIT JUSQU'A 250 cm • FAIENCE JUSQU'A 120 CM • FAIENCE PLAN DE TRAVAIL DE 50 cm DE HATEUR PROTECTION MURALE • PROTECTION D'ANGLE • LISSE DE PROTECTION MURALE			

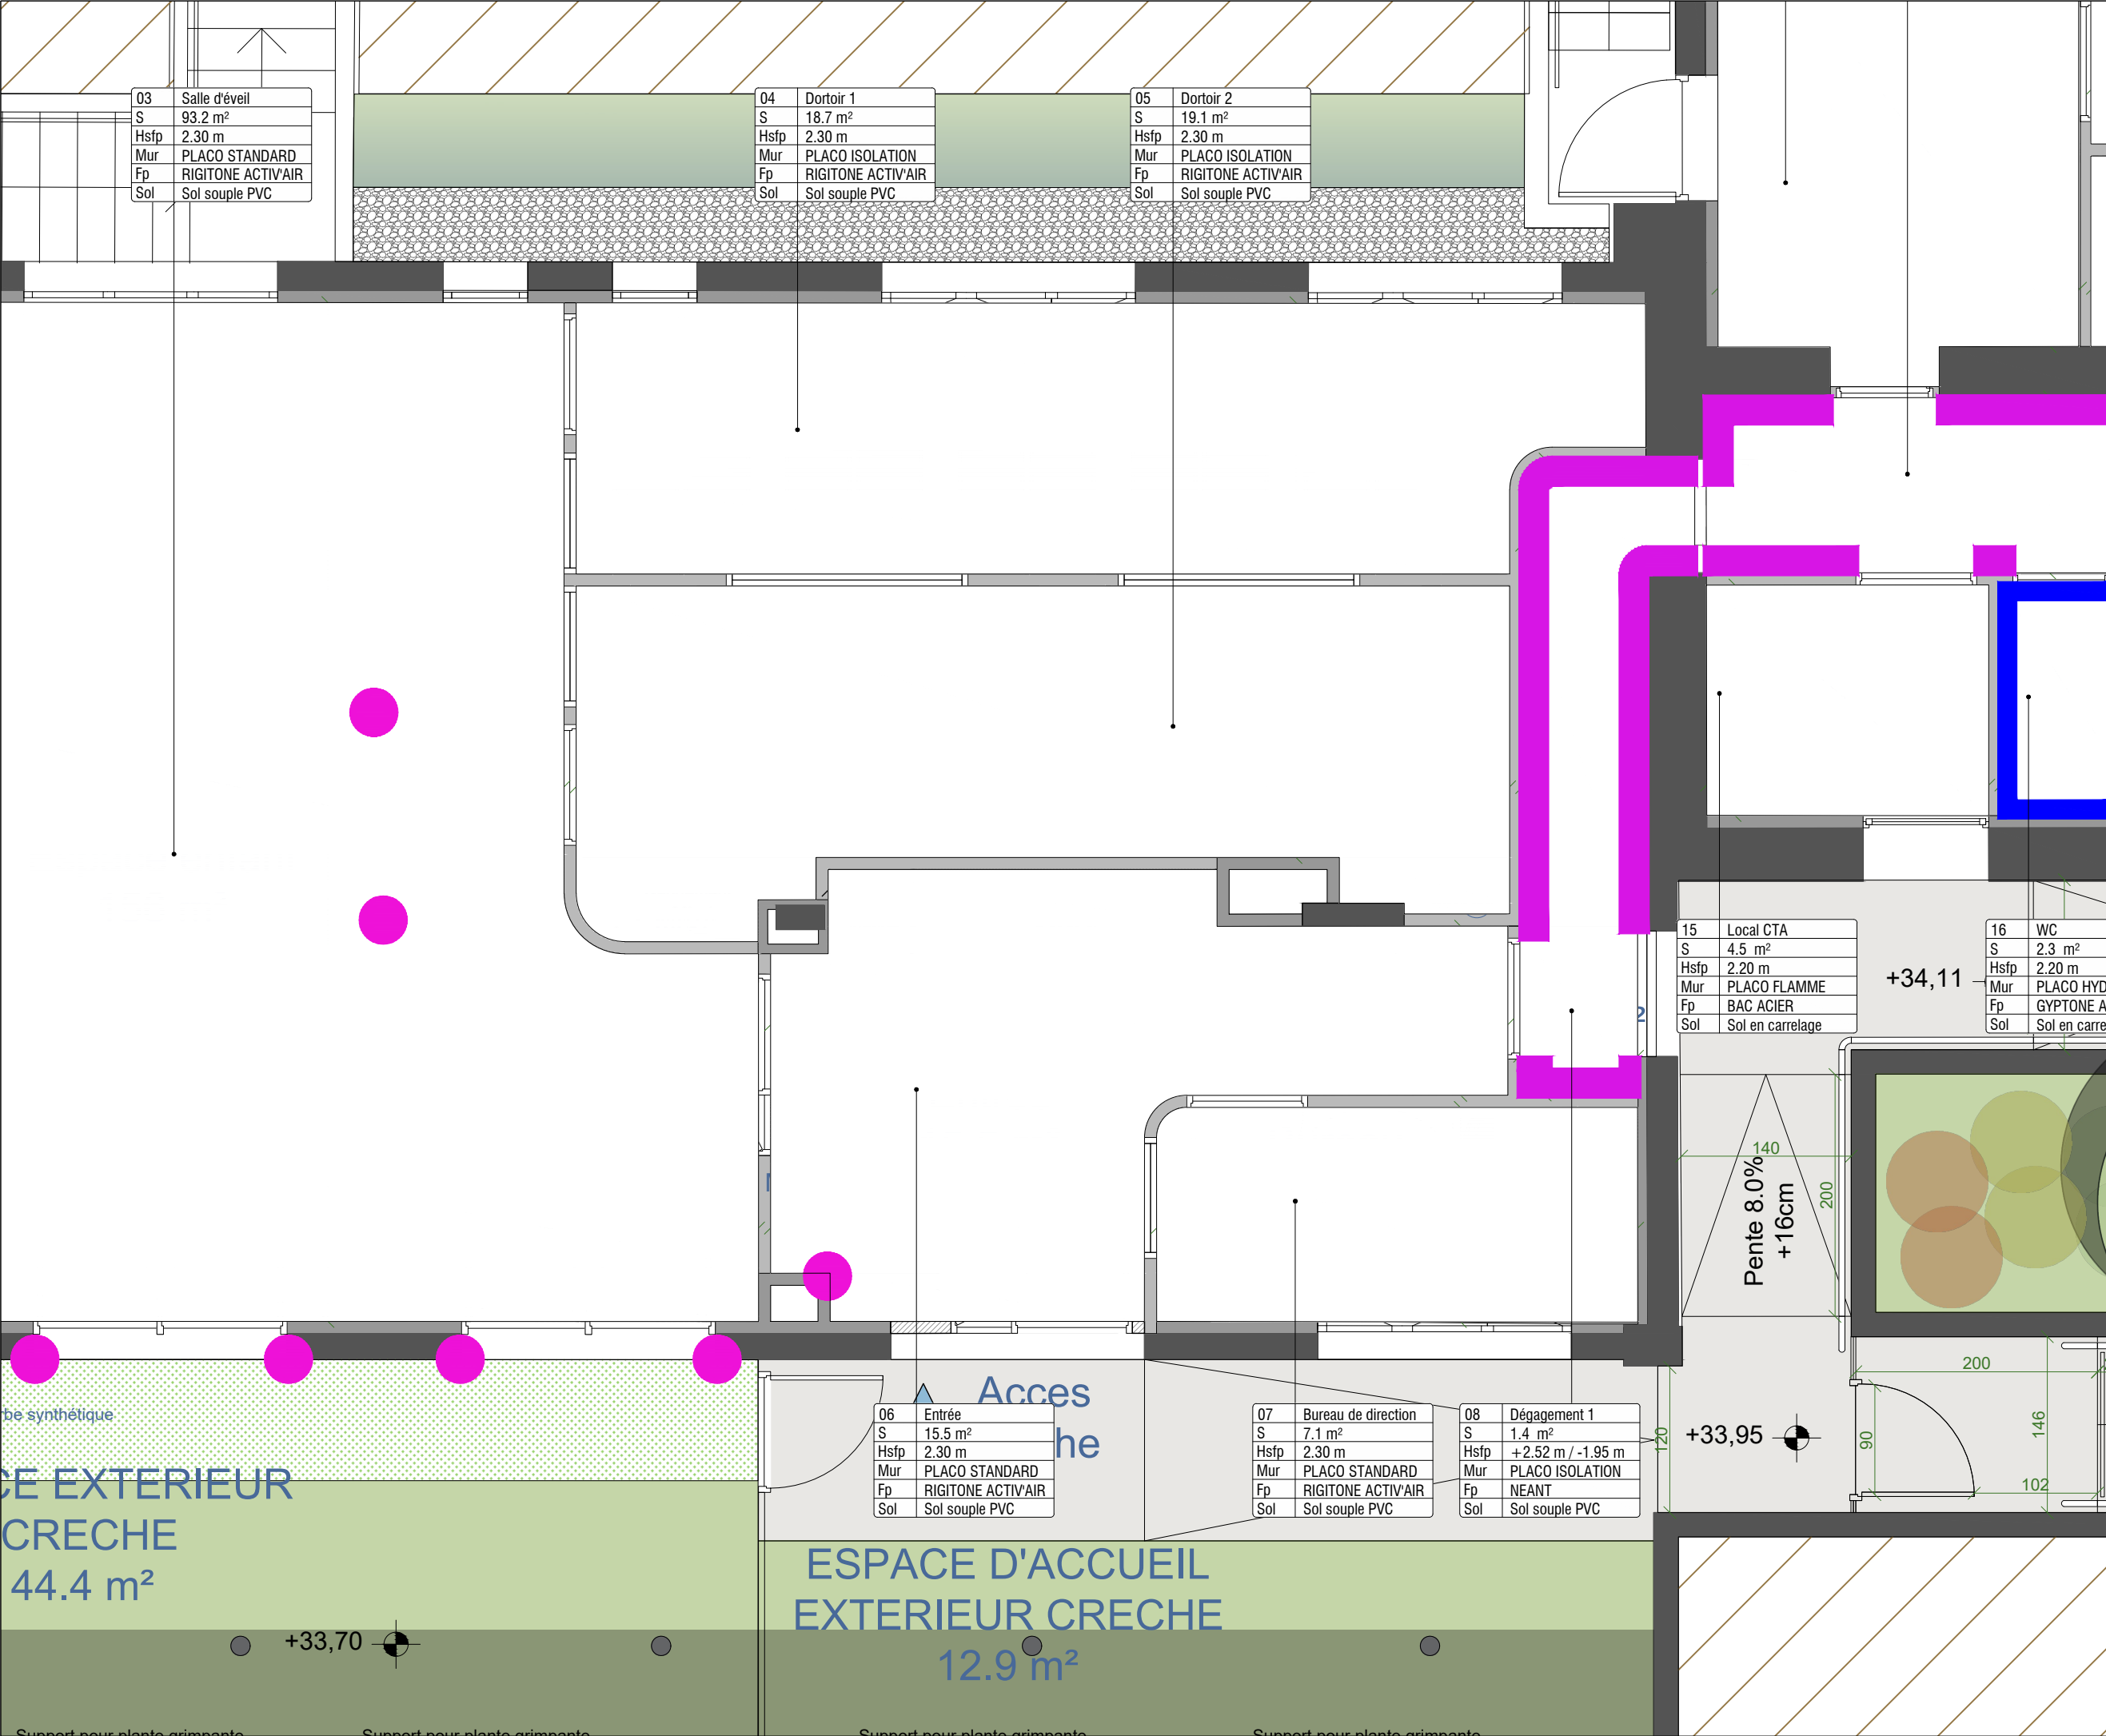

CREATION D'UN MULTI-ACCUEIL
ET D'UNE MAISON MEDICALE
78400 CHATOU

MOA

SARL LPC YVELINES
15 Rue de l'Orient78000 VERSAILLES

MOE

NAHK ARCHITECTURE
24 Rue Yves Toudic, 75010 Paris

NOM DU DOCUMENT

REVETEMENT MURAL
SECTEUR 2

PHASE

PRO.DCE

ECH.

1/50

INDICE

1.1

DATE

30/06/2023

MODIFICATIONS

INDICE

DATE

OBJET

1.1

30/06/2023

Diffusion initiale

FAIENCE

• FAIENCE TOUTE HAUTEUR
SOIT JUSQU'A 250 cm


• FAIENCE JUSQU'A 120 CM

• FAIENCE PLAN DE TRAVAIL
DE 50 cm DE HATEUR


PROTECTION MURALE

• PROTECTION D'ANGLE


• LISSE DE PROTECTION
MURALE

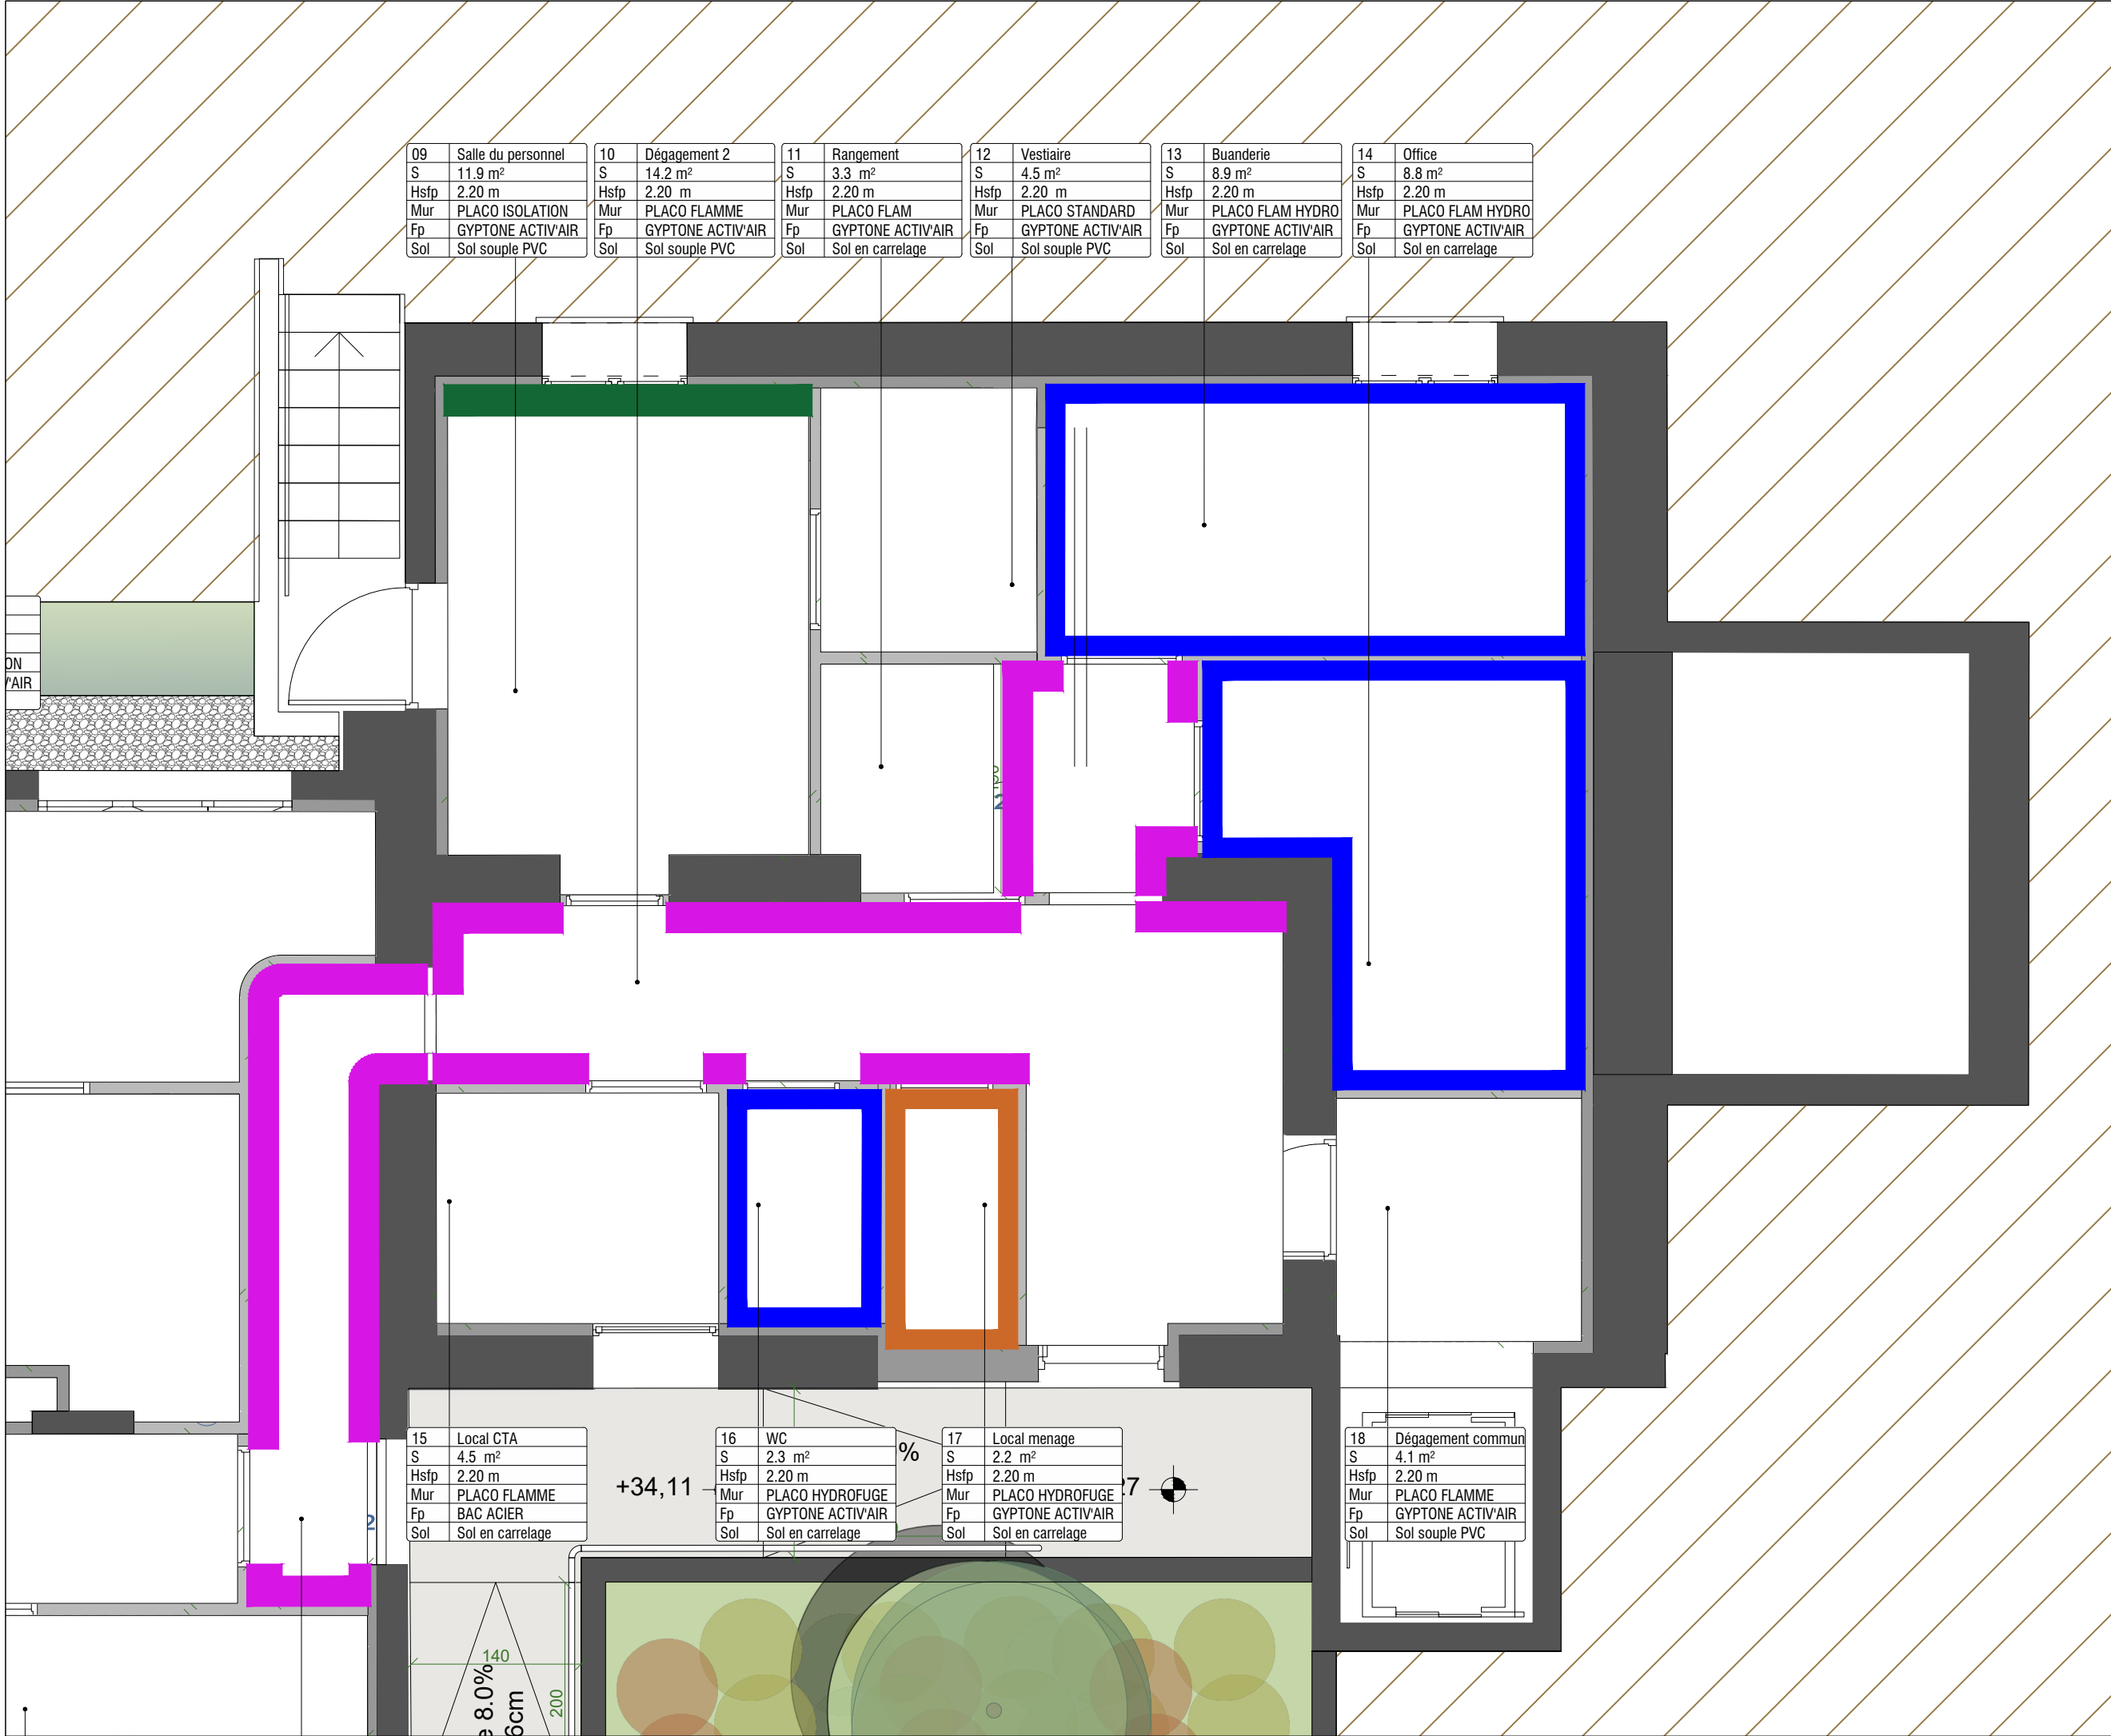


CREATION D'UN MULTI-ACCUEIL ET D'UNE MAISON MEDICALE 78400 CHATOU			
MOA	SARL LPC YVELINES 15 Rue de l'Orient78000 VERSAILLES		
MOE	NAHK ARCHITECTURE 24 Rue Yves Toudic, 75010 Paris		
NOM DU DOCUMENT			
REVETEMENT MURAL SECTEUR 3			
PHASE	PRO.DCE	ECH.	1/50
INDICE	1.1	DATE	30/06/2023
MODIFICATIONS			
INDICE DATE		OBJET	
1.1	30/06/2023	Diffusion initiale	
FAIENCE • FAIENCE TOUTE HAUTEUR SOIT JUSQU'A 250 cm • FAIENCE JUSQU'A 120 CM • FAIENCE PLAN DE TRAVAIL DE 50 cm DE HATEUR PROTECTION MURALE • PROTECTION D'ANGLE • LISSE DE PROTECTION MURALE			

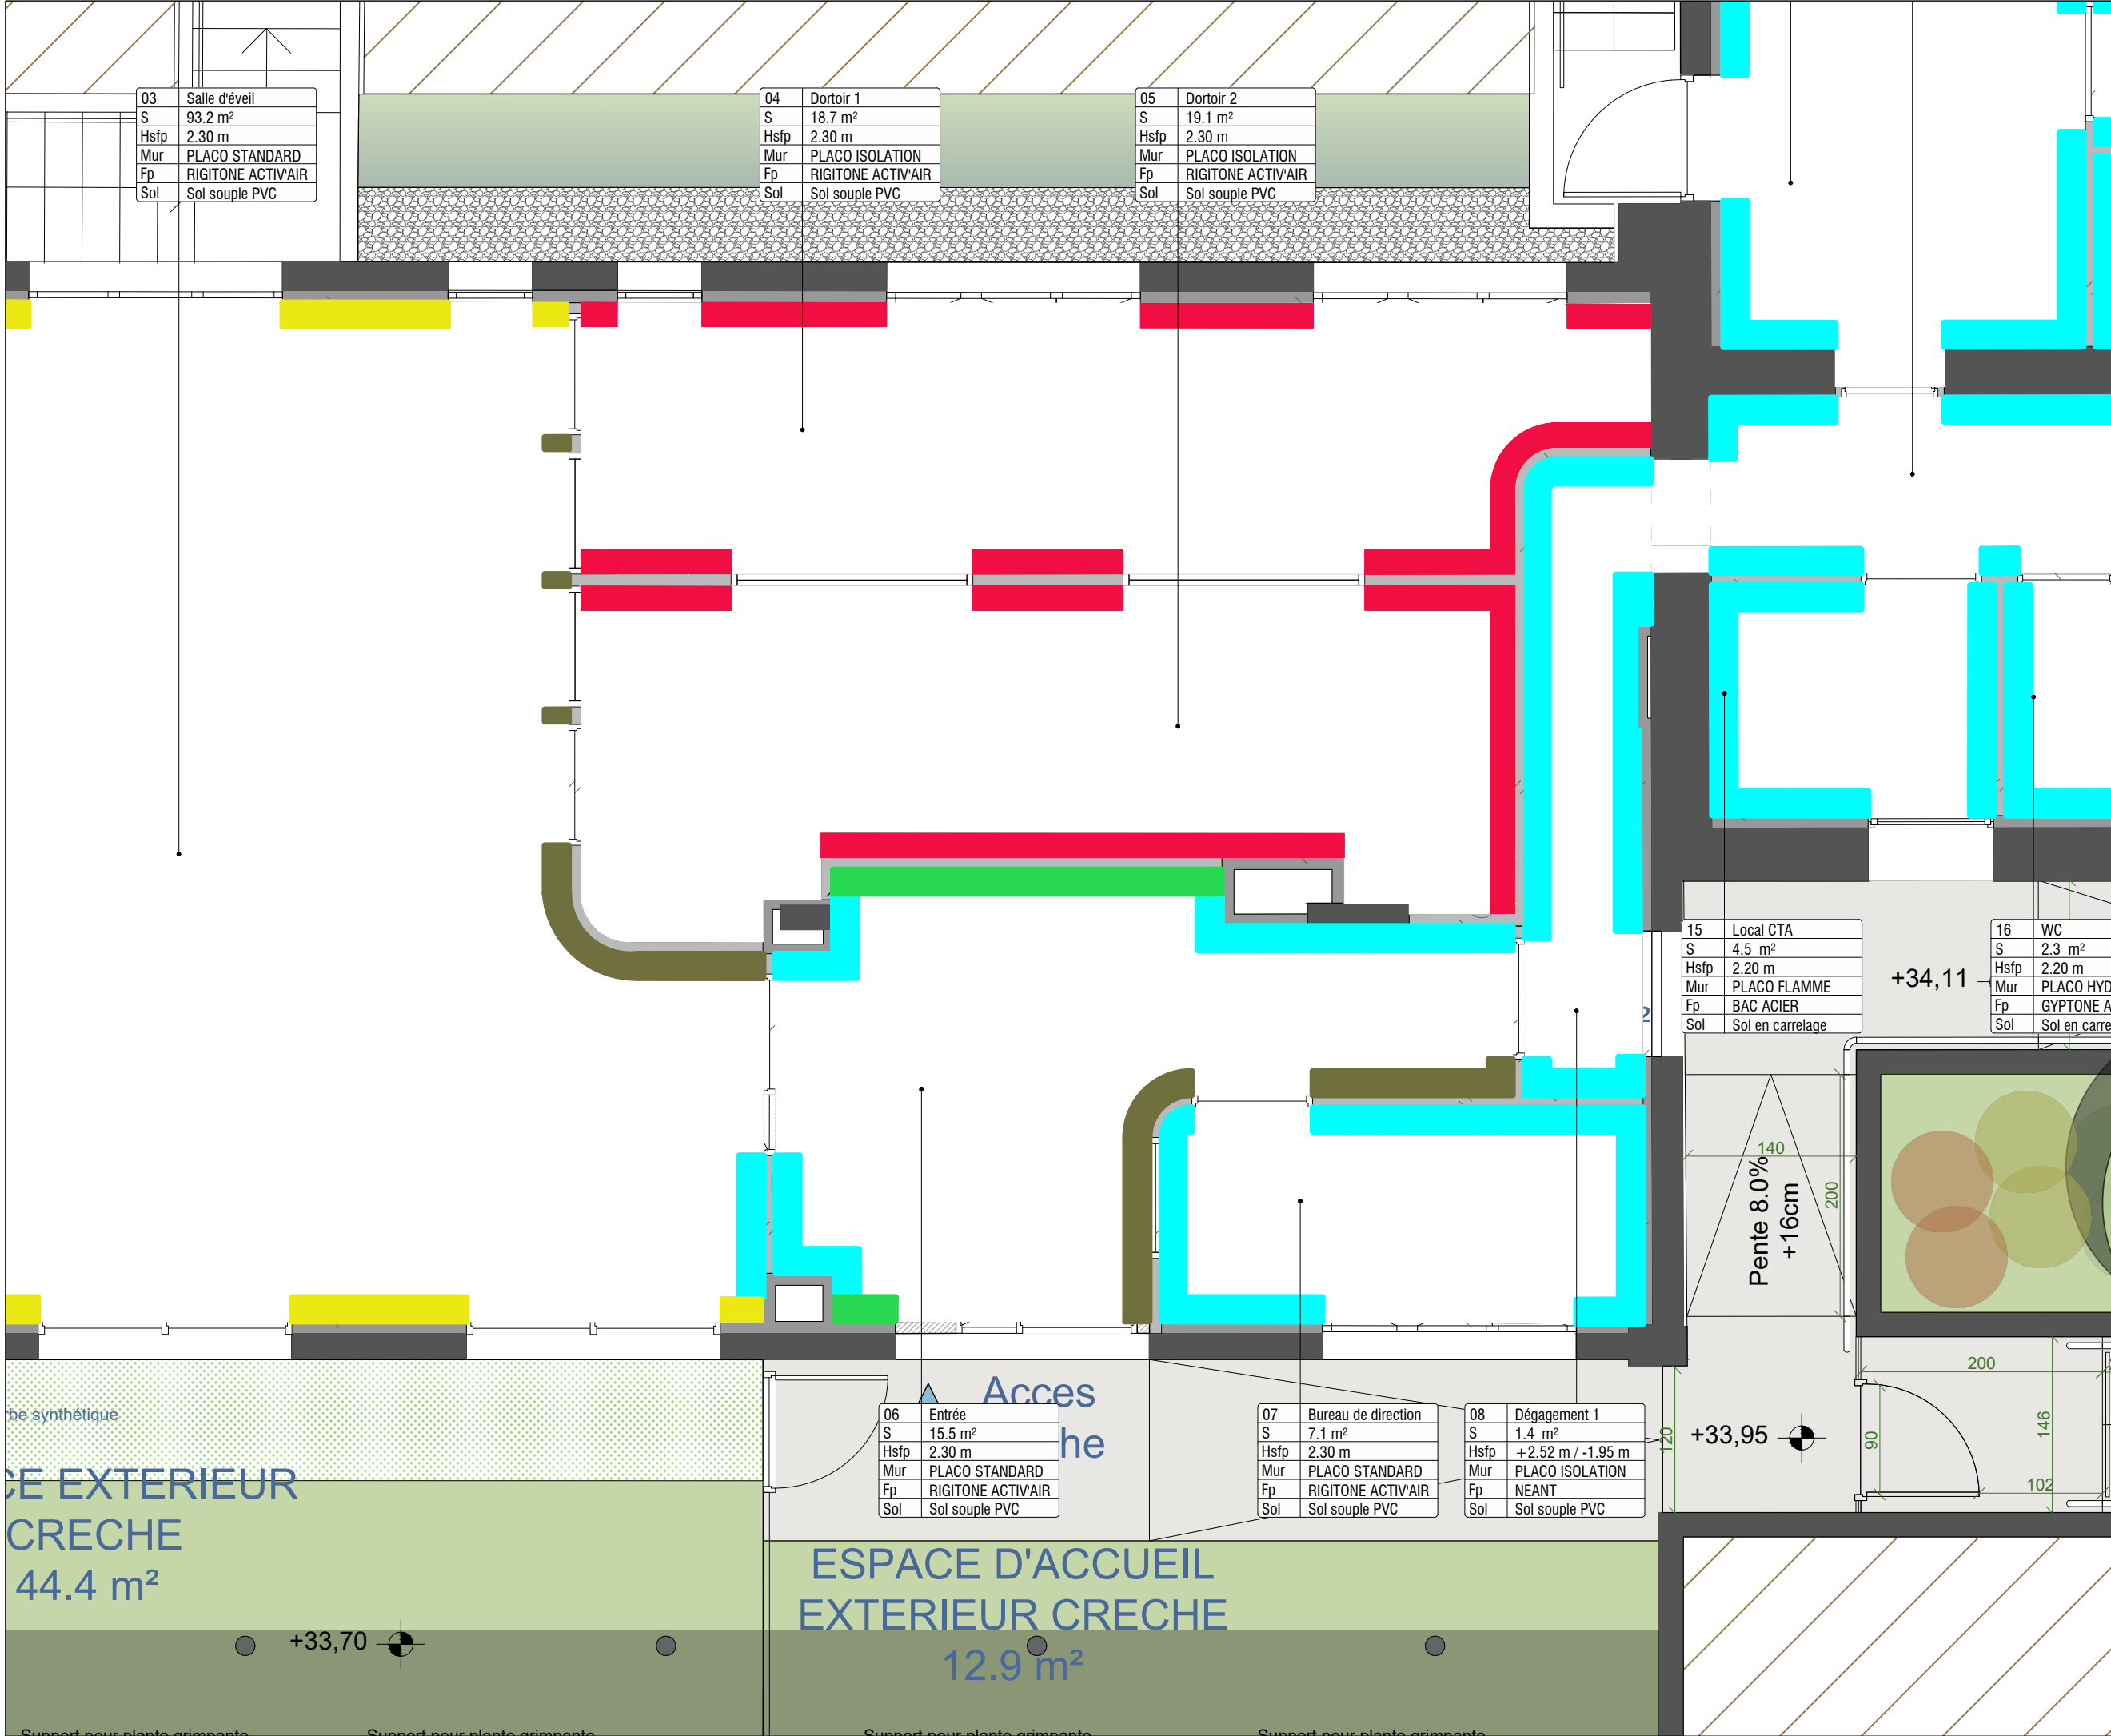

CREATION D'UN MULTI-ACCUEIL ET D'UNE MAISON MEDICALE 78400 CHATOU			
MOA	SARL LPC YVELINES 15 Rue de l'Orient78000 VERSAILLES		
MOE	NAHK ARCHITECTURE 24 Rue Yves Toudic, 75010 Paris		
NOM DU DOCUMENT			
PAPIER PEINT / PEINTURE SECTEUR 2			
PHASE	PRO.DCE	ECH.	1/50
INDICE	1.1	DATE	30/06/2023
MODIFICATIONS			
INDICE	DATE	OBJET	
1.1	30/06/2023	Diffusion initiale	
PAPIER PEINT / PEINTURE			
	• PEINTURE TOUTE HAUTEUR JUSQU'A 250 cm Ref. Champoussin CH2 0022		
	• PEINTURE JAUNE Cercle ponctuel Ref. DAYROOM YELLOW 233 FARROW & BALL		
	• PEINTURE BLEU INDIGO A l'intérieur des meubles de l'en Ref. PITCH BLUE 200 FARROW & BALL		
	• PEINTURE LONDON STONE JUSQU'A 220cm. Ref. LONDON STONE 6 FARROW & BALL		
	• PAPIER PEINT TOUTE HAUT SOIT JUSQU'A 230 cm Ref. My Greenhouse Watercolo e 30387		
	• PAPIER PEINT TOUTE HAUT SOIT JUSQU'A 230 cm Ref. Divine Cherry Blossoms e40595		

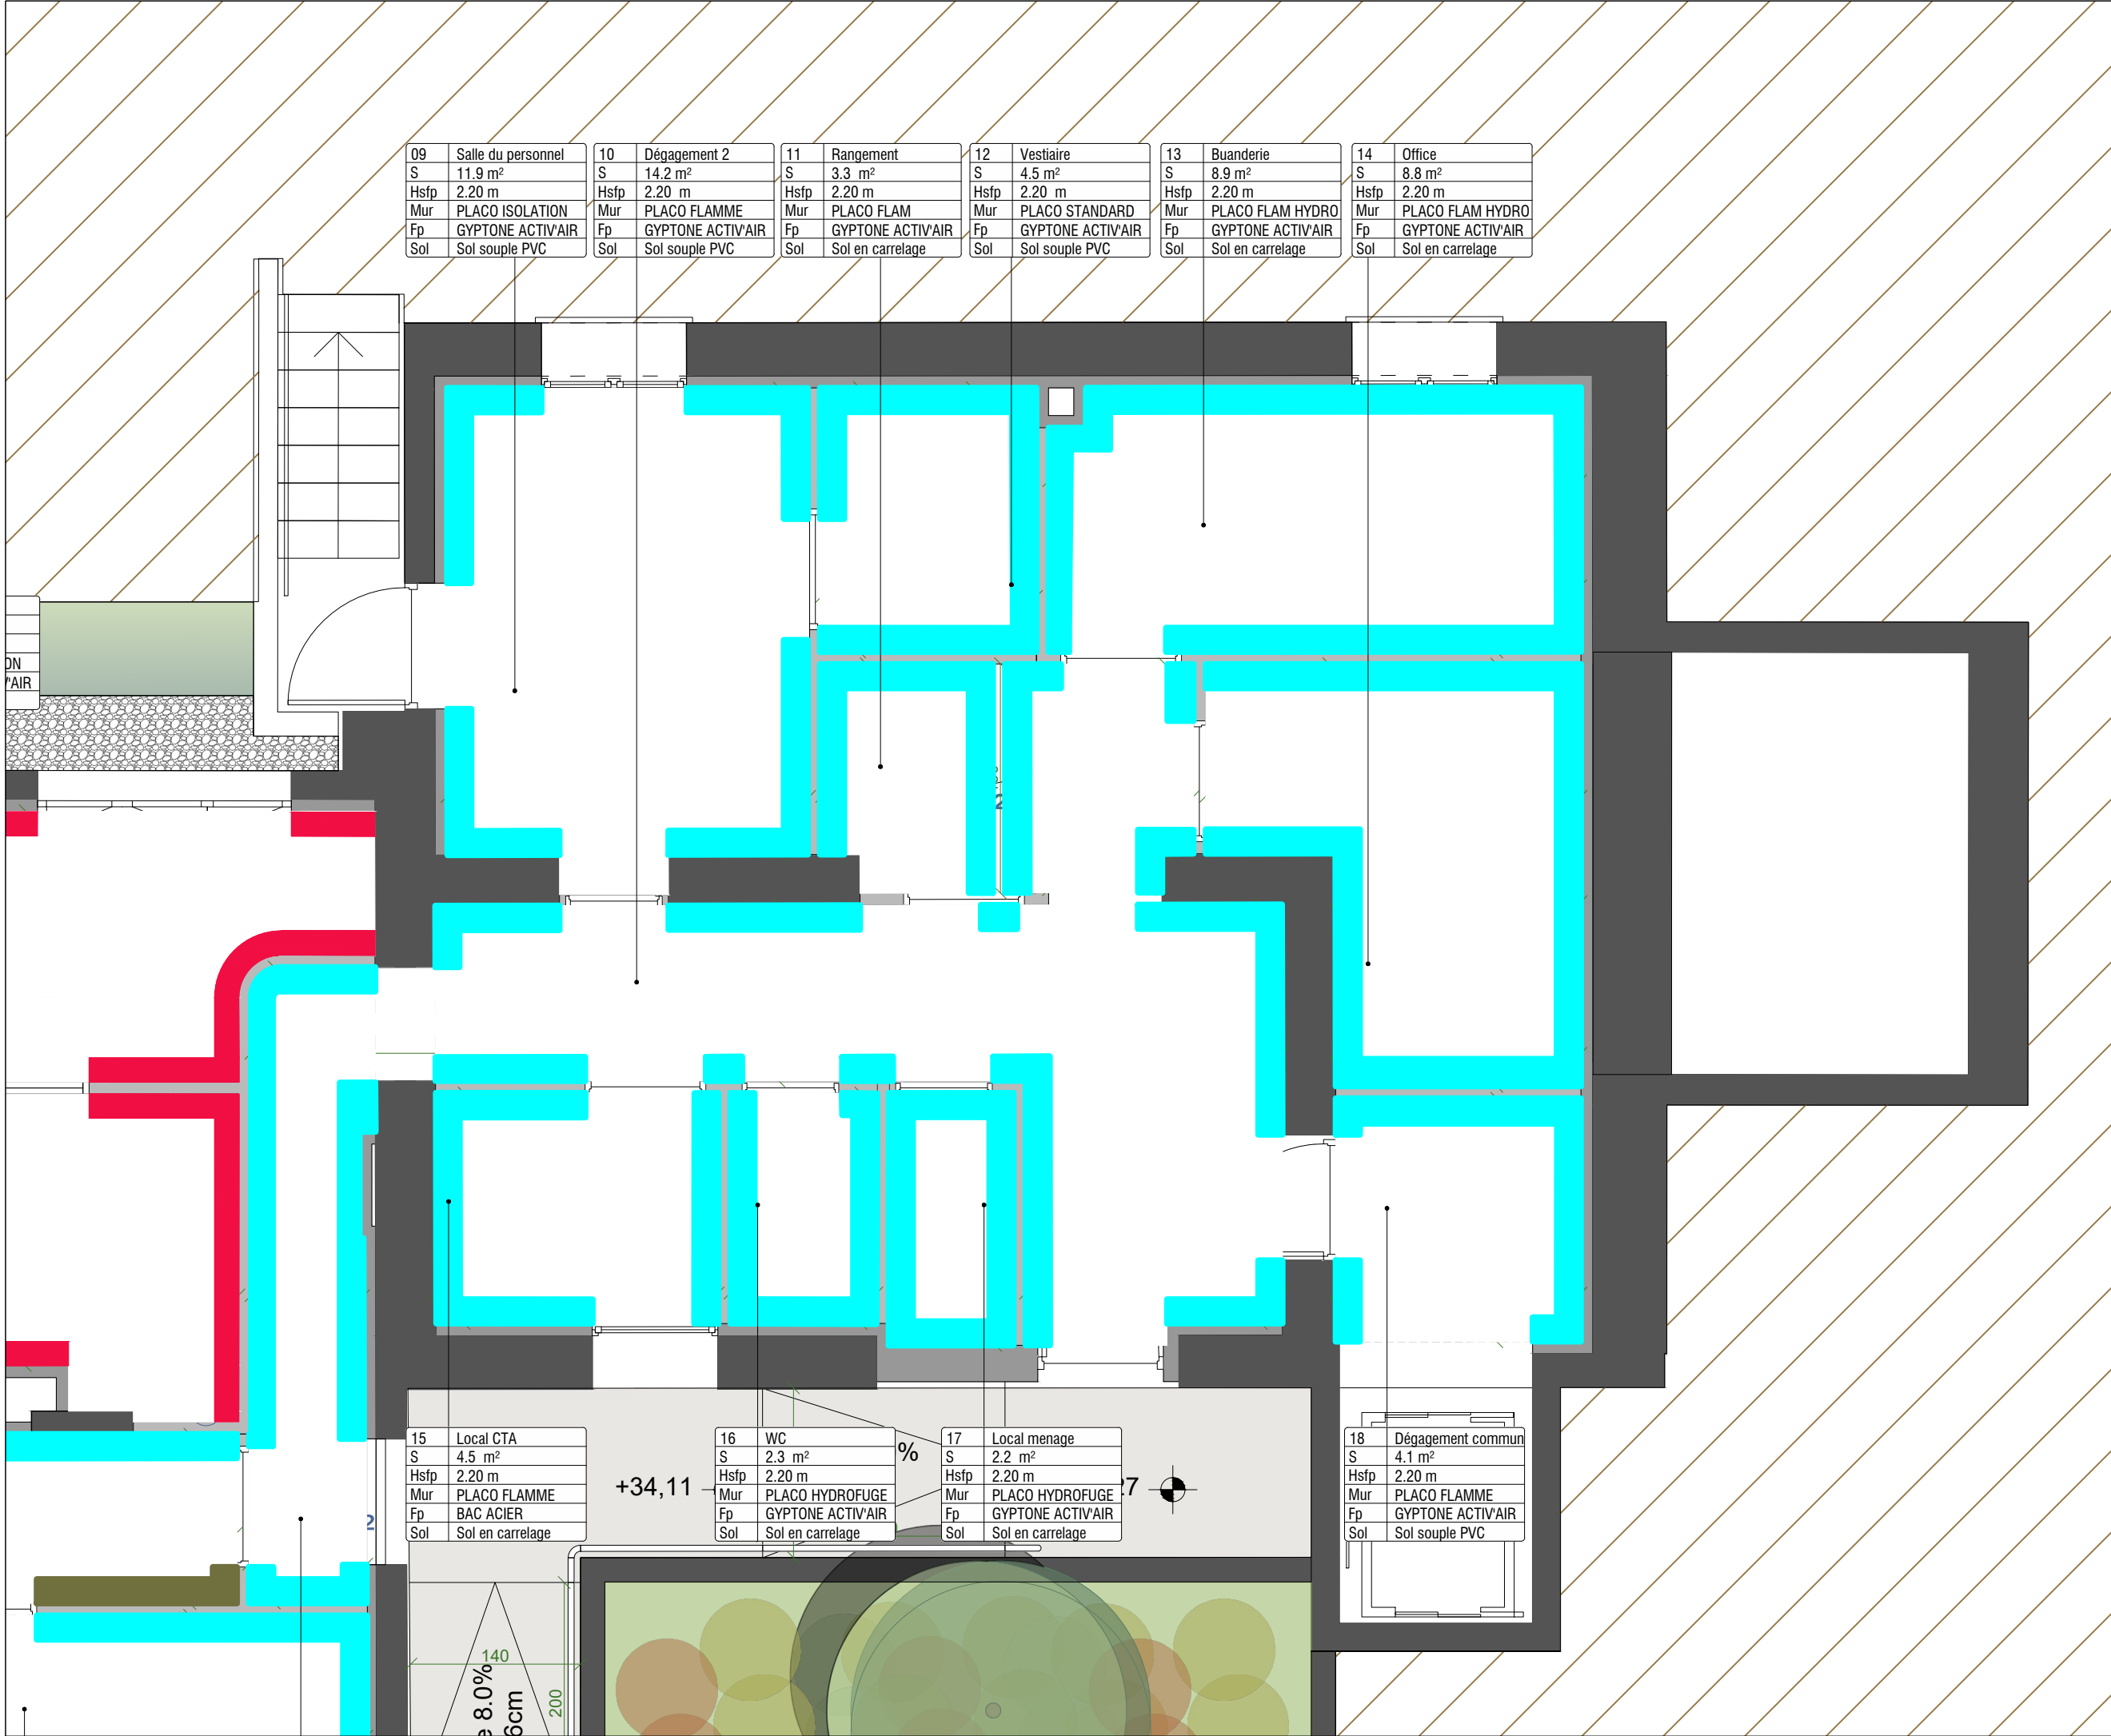

CREATION D'UN MULTI-ACCUEIL ET D'UNE MAISON MEDICALE 78400 CHATOU			
MOA	SARL LPC YVELINES 15 Rue de l'Orient78000 VERSAILLES		
MOE	NAHK ARCHITECTURE 24 Rue Yves Toudic, 75010 Paris		
NOM DU DOCUMENT			
PAPIER PEINT / PEINTURE SECTEUR 3			
PHASE	PRO.DCE	ECH.	1/50
INDICE	1.1	DATE	30/06/2023
MODIFICATIONS			
INDICE	DATE	OBJET	
1.1	30/06/2023	Diffusion initiale	
PAPIER PEINT / PEINTURE			
	• PEINTURE TOUTE HAUTEUR JUSQU'A 250 cm Ref. Champoussin CH2 0022		
	• PEINTURE JAUNE Cercle ponctuel Ref. DAYROOM YELLOW 233 FARROW & BALL		
	• PEINTURE BLEU INDIGO A l'intérieur des meubles de l'en Ref. PITCH BLUE 200 FARROW & BALL		
	• PEINTURE LONDON STONE JUSQU'A 220cm. Ref. LONDON STONE 6 FARROW & BALL		
	• PAPIER PEINT TOUTE HAUT SOIT JUSQU'A 230 cm Ref. My Greenhouse Watercolo e 30387		
	• PAPIER PEINT TOUTE HAUT SOIT JUSQU'A 230 cm Ref. Divine Cherry Blossoms e40595		

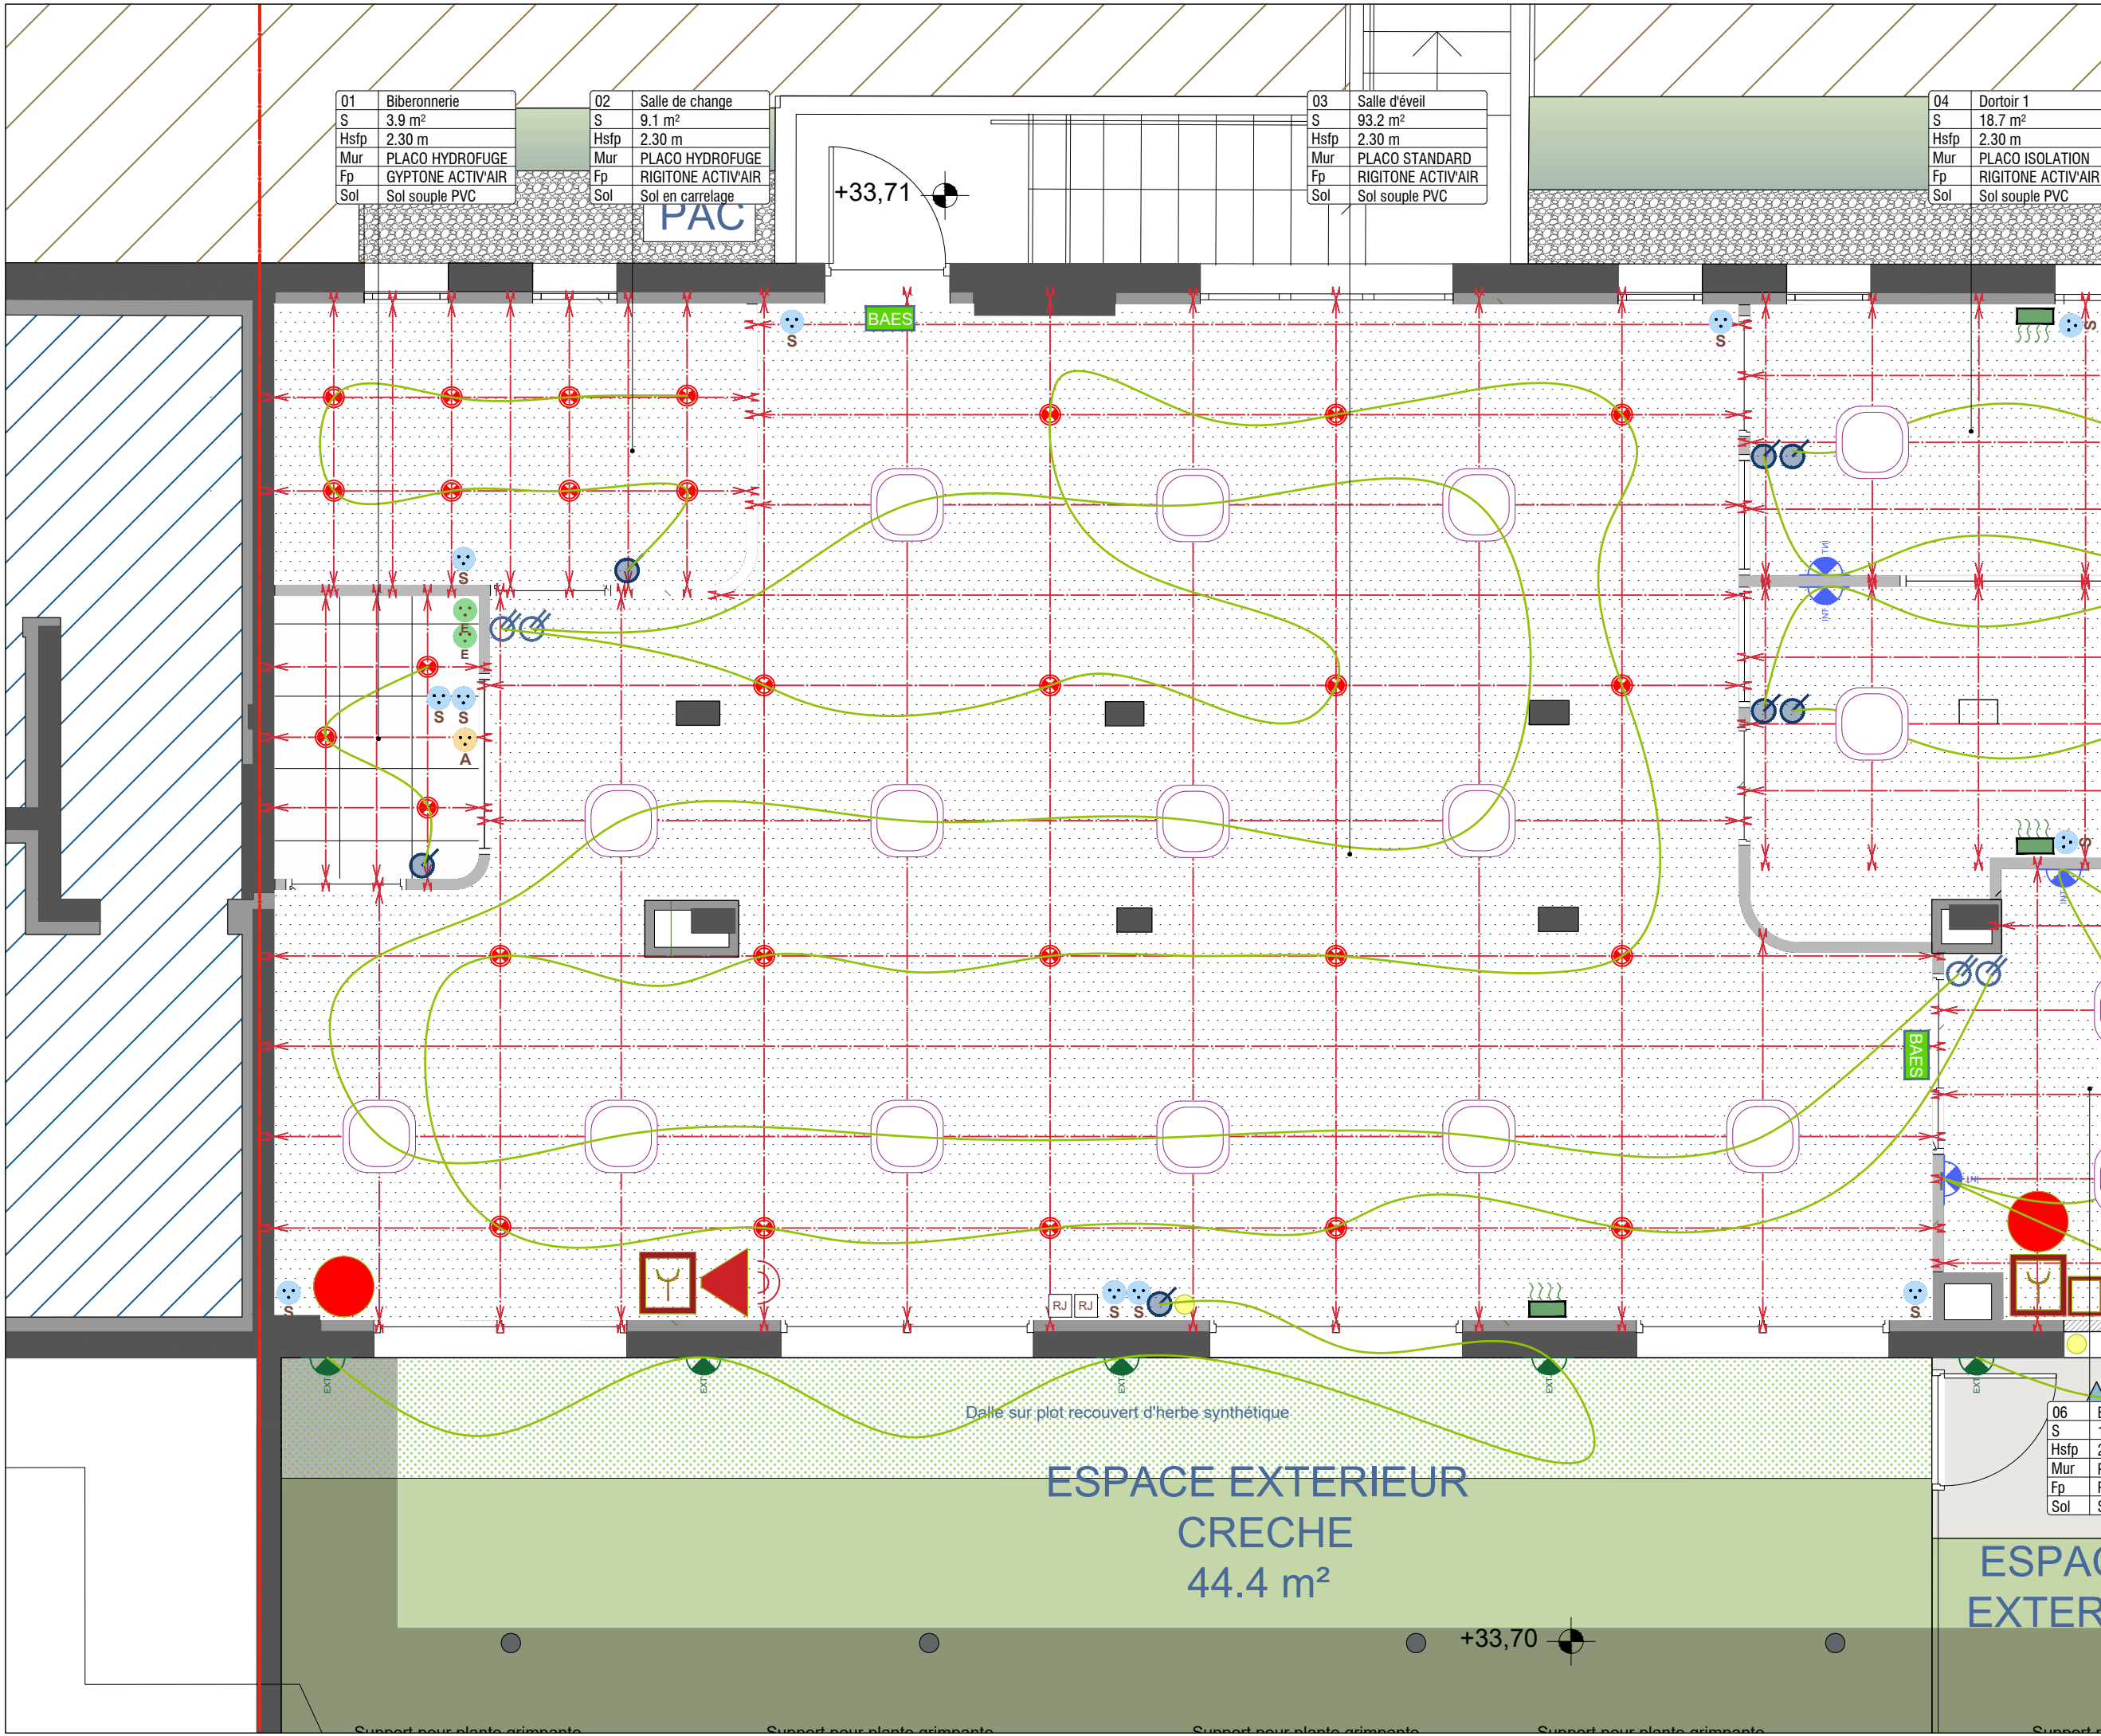

01	Biberonnerie
S	3.9 m²
Hsfp	2.30 m
Mur	PLACO HYDROFUGE
Fp	GYPTONE ACTIV'AIR
Sol	Sol souple PVC

02	Salle de change
S	9.1 m²
Hsfp	2.30 m
Mur	PLACO HYDROFUGE
Fp	RIGITONE ACTIV'AIR
Sol	Sol en carrelage

03	Salle d'éveil
S	93.2 m²
Hsfp	2.30 m
Mur	PLACO STANDARD
Fp	RIGITONE ACTIV'AIR
Sol	Sol souple PVC

04	Dortoir 1
S	18.7 m²
Hsfp	2.30 m
Mur	PLACO ISOLATION
Fp	RIGITONE ACTIV'AIR
Sol	Sol souple PVC

CREATION D'UN MULTI-ACCUEIL
ET D'UNE MAISON MEDICALE
78400 CHATOU

MOA

SARL LPC YVELINES
15 Rue de l'Orient78000 VERSAILLES

MOE

NAHK ARCHITECTURE
24 Rue Yves Toudic, 75010 Paris

NOM DU DOCUMENT

ELECTRICITE
SECTEUR 1


PHASE	PRO.DCE	ECH.	1/50
INDICE	1.1	DATE	30/06/2023

MODIFICATIONS

INDICE	DATE	OBJET
1.1	30/06/2023	Diffusion initiale

ELECTRICITE

- TYPE 1 - PLAFONNIER SLV MEDO 60 REF. #1000726
- TYPE 2 - DOWNLIGHTS TIGA 3 RD DIAM 240
- TYPE 3 - SPOT IN HOUSE LED UP007 DIAM 85
- TYPE 4 - DOWNLIGHTS TIGA 1 RD DIAM 170
- TYPE 5 - APPLIQUE MURALE DELTALIGHT TOPIX WW
- TYPE 6 - REGLETTE MURALE EXTRA-PLATE
- TYPE 7 - APPLIQUE SLV QUADRASYL
- INTERRUPTEUR SIMPLE
- INTERRUPTEUR VA-ET-VIENT
- VARIATEUR EN DALI
- DETECTEUR DE PRESENCE AVEC MINUTERIE
- PRISE ELECTRIQUE STANDARD H 130 CM DU SOL
- PRISE ETANCHE ENCASTREE 20 CM DU PLAN DE TRAVAIL
- ALIMENTATION APPAREIL
- PRISE RJ45
- BAES
- CENTRALE D'ALARME INCENDIE
- DIFFUSEUR SONORE
- DECLENCHEUR D'ALARME MANUEL
- DEVEROUILLAGE PORTE
- ARRET D'URGENCE ELECTRICITE ET VENTILATION
- EXTINCTEUR
- VISIOPHONE AVEC VENTOUSE
- DIGICODE
- SERRURE A CODE
- SONDE DE QUALITE DE L'AIR
- TGBT
- CTA AU PLAFOND
- BALLON

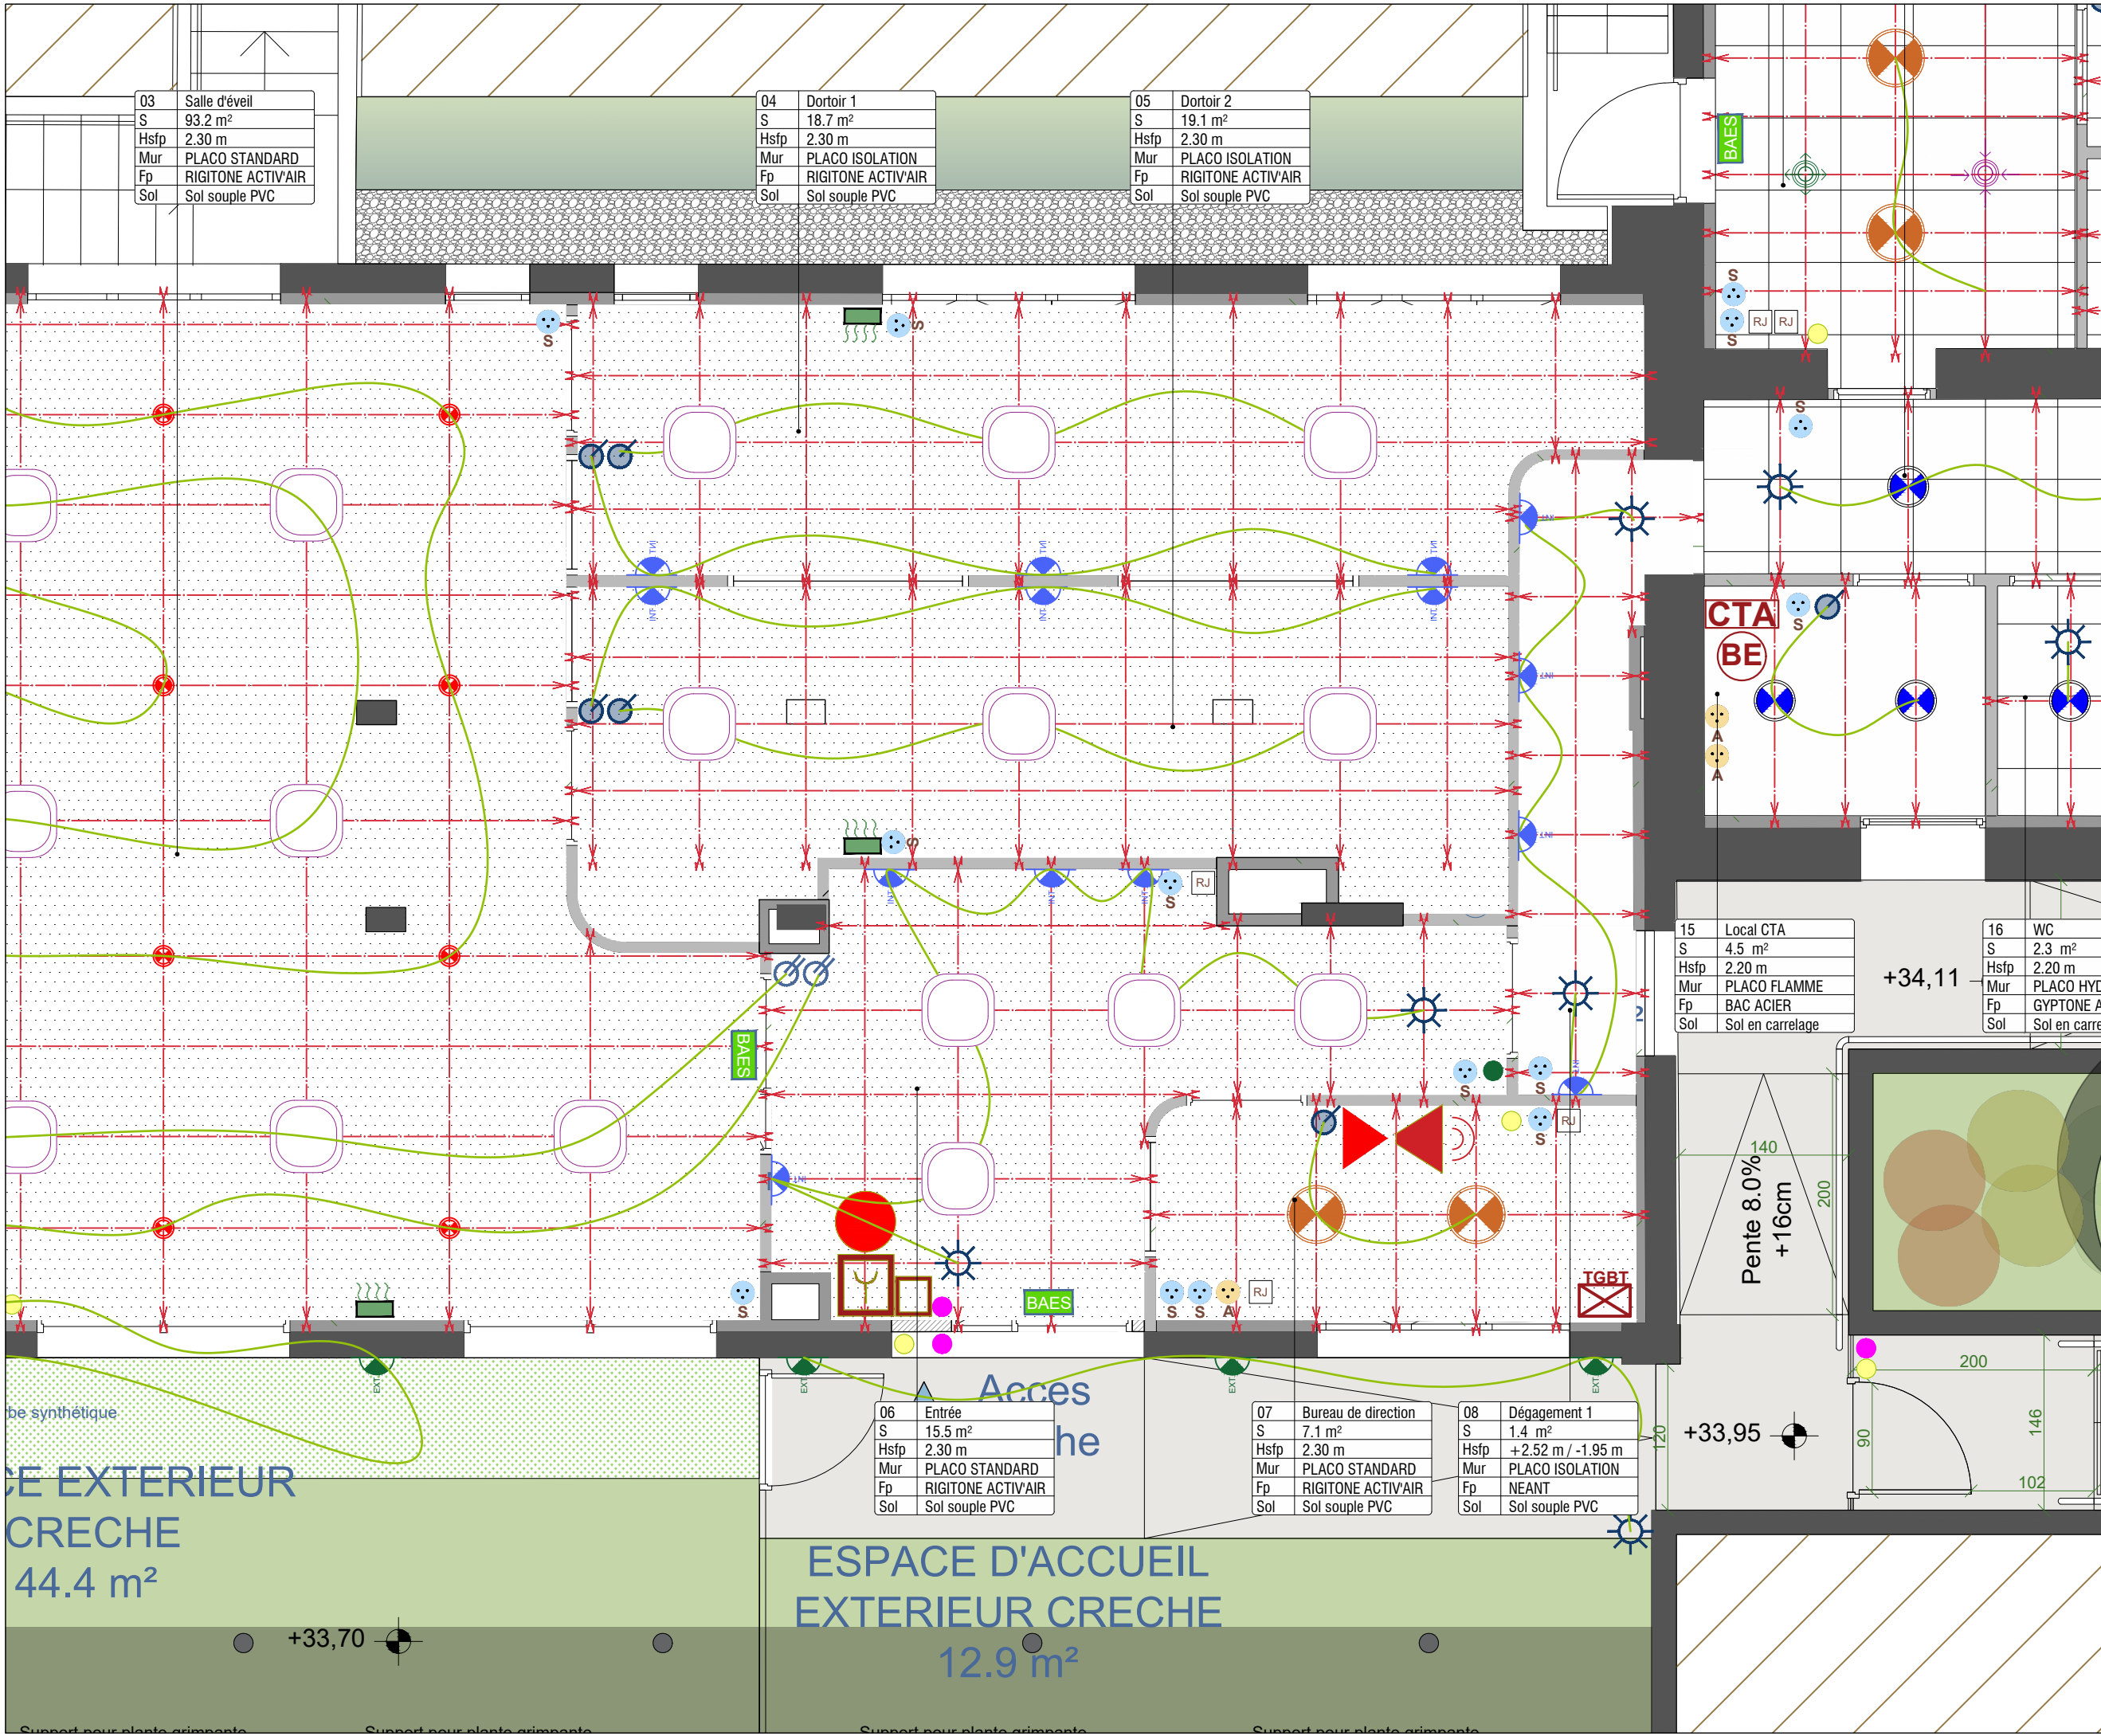

03	Salle d'éveil
S	93.2 m²
Hsfp	2.30 m
Mur	PLACO STANDARD
Fp	RIGITONE ACTIVAIR
Sol	Sol souple PVC

04	Dortoir 1
S	18.7 m²
Hsfp	2.30 m
Mur	PLACO ISOLATION
Fp	RIGITONE ACTIVAIR
Sol	Sol souple PVC

05	Dortoir 2
S	19.1 m²
Hsfp	2.30 m
Mur	PLACO ISOLATION
Fp	RIGITONE ACTIVAIR
Sol	Sol souple PVC

15	Local CTA
S	4.5 m²
Hsfp	2.20 m
Mur	PLACO FLAMME
Fp	BAC ACIER
Sol	Sol en carrelage

16	WC
S	2.3 m²
Hsfp	2.20 m
Mur	PLACO HYD
Fp	GYPTONE A
Sol	Sol en carrelage

06	Entrée
S	15.5 m²
Hsfp	2.30 m
Mur	PLACO STANDARD
Fp	RIGITONE ACTIVAIR
Sol	Sol souple PVC

07	Bureau de direction
S	7.1 m²
Hsfp	2.30 m
Mur	PLACO STANDARD
Fp	RIGITONE ACTIVAIR
Sol	Sol souple PVC

08	Dégagement 1
S	1.4 m²
Hsfp	+2.52 m / -1.95 m
Mur	PLACO ISOLATION
Fp	NEANT
Sol	Sol souple PVC

CREATION D'UN MULTI-ACCUEIL
ET D'UNE MAISON MEDICALE
78400 CHATOU

MOA

SARL LPC YVELINES
15 Rue de l'Orient78000 VERSAILLES

MOE

NAHK ARCHITECTURE
24 Rue Yves Toudic, 75010 Paris

NOM DU DOCUMENT

ELECTRICITE
SECTEUR 2

PHASE

PRO.DCE

ECH.

1/50

INDICE

1.1

DATE

30/06/2023

MODIFICATIONS

INDICE

DATE

OBJET

1.1

30/06/2023

Diffusion initiale

ELECTRICITE

• TYPE 1 - PLAFONNIER SLV
MEDO 60 REF. #1000726

• TYPE 2 - DOWNLIGHTS TIGA 3
RD DIAM 240

• TYPE 3 - SPOT IN HOUSE LED
UP007 DIAM 85

• TYPE 4 - DOWNLIGHTS TIGA 1
RD DIAM 170

• TYPE 5 - APPLIQUE MURALE
DELTALIGHT TOPIX WW

• TYPE 6 - REGLETTE MURALE
EXTRA-PLATE

• TYPE 7 - APPLIQUE
SLV QUADRASYL

• INTERRUPTEUR SIMPLE

• INTERRUPTEUR VA-ET-VIENT

• VARIATEUR EN DALI

• DETECTEUR DE PRESENCE
AVEC MINUTERIE

• PRISE ELECTRIQUE
STANDARD H 130 CM DU SOL

• PRISE ETANCHE ENCASTREE
20 CM DU PLAN DE TRAVAIL

• ALIMENTATION APPAREIL

• PRISE RJ45

• BAES

• CENTRALE D'ALARME INCENDIE

• DIFFUSEUR SONORE

• DIFFUSEUR LUMINEUX

• DECLENCHEUR D'ALARME MANUEL

• DEVEROUILLAGE PORTE

• ARRET D'URGENCE ELECTRICITE
ET VENTILATION

• EXTINCTEUR

• VISIOPHONE AVEC VENTOUSE

• DIGICODE


• SERRURE A CODE

• SONDE DE QUALITE DE L'AIR

• TGBT

• CTA AU PLAFOND

• BALLON

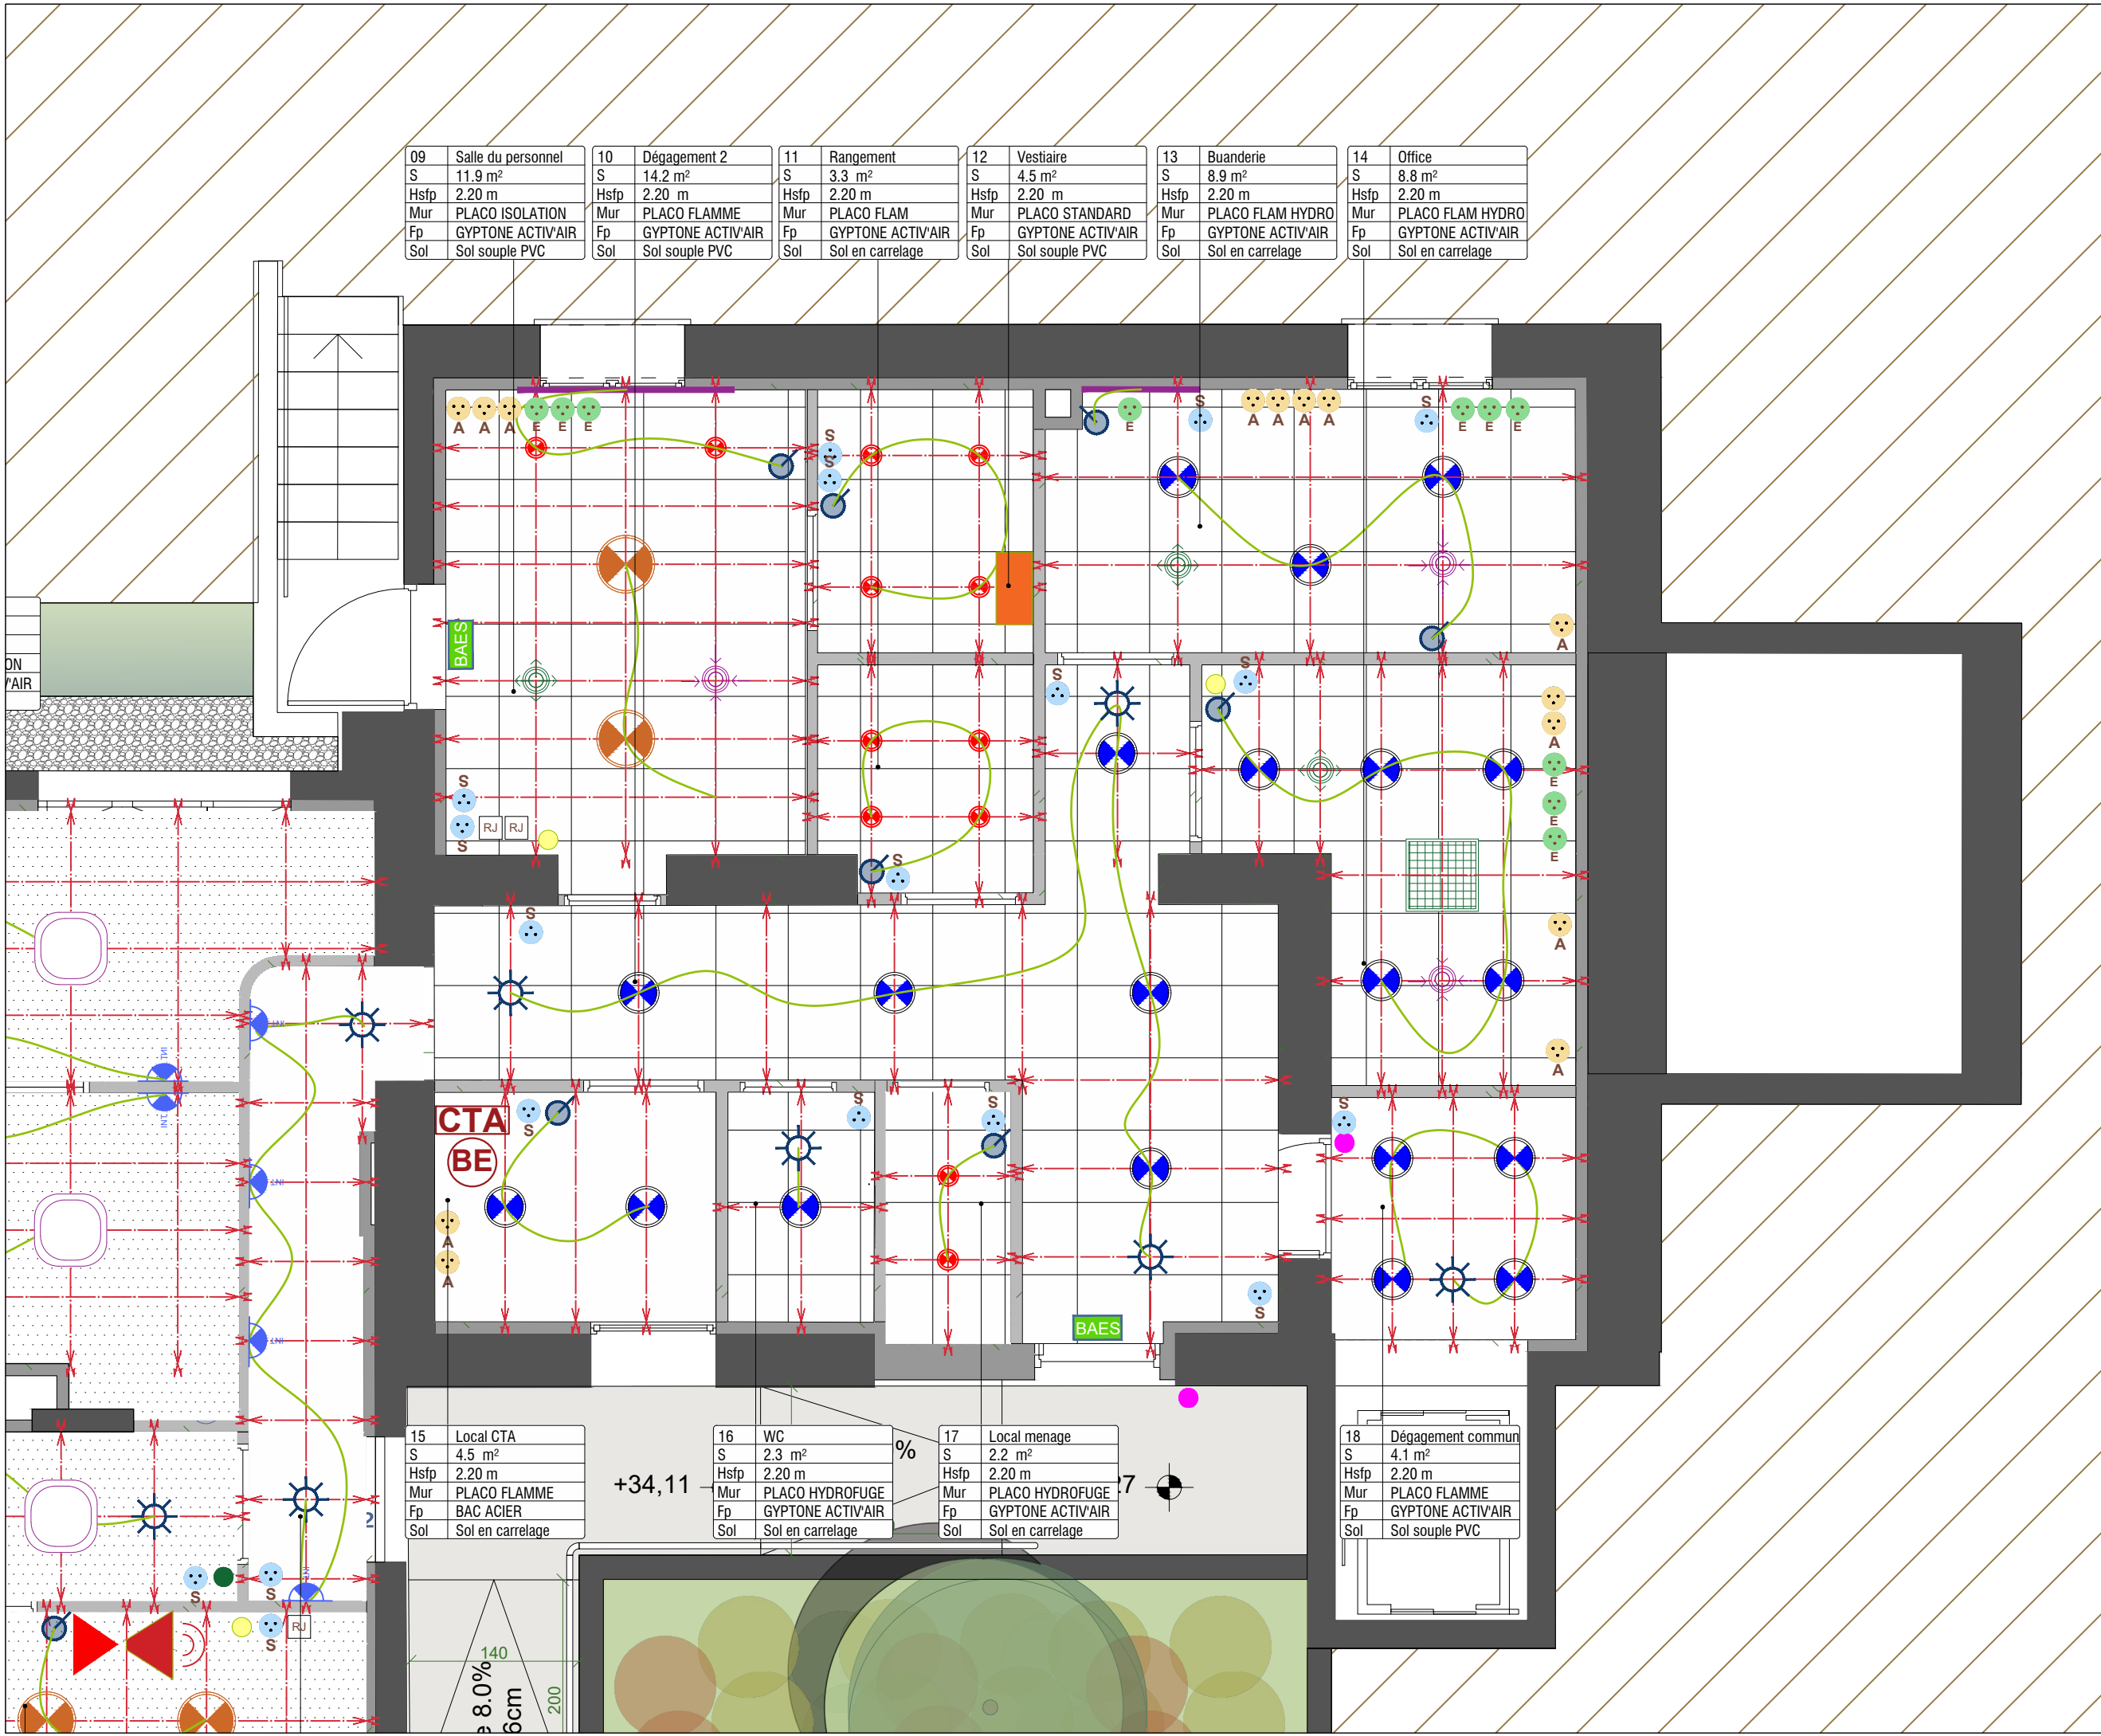

09	Salle du personnel	10	Dégagement 2	11	Rangement	12	Vestiaire	13	Buanderie	14	Office
S	11.9 m²	S	14.2 m²	S	3.3 m²	S	4.5 m²	S	8.9 m²	S	8.8 m²
Hsfp	2.20 m	Hsfp	2.20 m	Hsfp	2.20 m	Hsfp	2.20 m	Hsfp	2.20 m	Hsfp	2.20 m
Mur	PLACO ISOLATION	Mur	PLACO FLAMME	Mur	PLACO FLAM	Mur	PLACO STANDARD	Mur	PLACO FLAM HYDRO	Mur	PLACO FLAM HYDRO
Fp	GYPTONE ACTIV'AIR	Fp	GYPTONE ACTIV'AIR	Fp	GYPTONE ACTIV'AIR	Fp	GYPTONE ACTIV'AIR	Fp	GYPTONE ACTIV'AIR	Fp	GYPTONE ACTIV'AIR
Sol	Sol souple PVC	Sol	Sol souple PVC	Sol	Sol en carrelage	Sol	Sol souple PVC	Sol	Sol en carrelage	Sol	Sol en carrelage

15	Local CTA	16	WC	17	Local ménage	18	Dégagement commun
S	4.5 m²	S	2.3 m²	S	2.2 m²	S	4.1 m²
Hsfp	2.20 m	Hsfp	2.20 m	Hsfp	2.20 m	Hsfp	2.20 m
Mur	PLACO FLAMME	Mur	PLACO HYDROFUGE	Mur	PLACO HYDROFUGE	Mur	PLACO FLAMME
Fp	BAC ACIER	Fp	GYPTONE ACTIV'AIR	Fp	GYPTONE ACTIV'AIR	Fp	GYPTONE ACTIV'AIR
Sol	Sol en carrelage	Sol	Sol en carrelage	Sol	Sol en carrelage	Sol	Sol souple PVC

CREATION D'UN MULTI-ACCUEIL
ET D'UNE MAISON MEDICALE
78400 CHATOU

MOA

SARL LPC YVELINES
15 Rue de l'Orient78000 VERSAILLES

MOE

NAHK ARCHITECTURE
24 Rue Yves Toudic, 75010 Paris

NOM DU DOCUMENT

ELECTRICITE
SECTEUR 3

PHASE

PRO.DCE

ECH.

1/50

INDICE

1.1

DATE

30/06/2023

MODIFICATIONS

INDICE DATE OBJET

1.1 30/06/2023 Diffusion initiale

ELECTRICITE

• TYPE 1 - PLAFONNIER SLV
MEDO 60 REF. #1000726

• TYPE 2 - DOWNLIGHTS TIGA 3
RD DIAM 240

• TYPE 3 - SPOT IN HOUSE LED
UP007 DIAM 85

• TYPE 4 - DOWNLIGHTS TIGA 1
RD DIAM 170

• TYPE 5 - APPLIQUE MURALE
DELTALIGHT TOPIX WW

• TYPE 6 - REGLETTE MURALE
EXTRA-PLATE

• TYPE 7 - APPLIQUE
SLV QUADRASYL

• INTERRUPTEUR SIMPLE

• INTERRUPTEUR VA-ET-VIENT

• VARIATEUR EN DALI

• DETECTEUR DE PRESENCE
AVEC MINUTERIE

• PRISE ELECTRIQUE
STANDARD H 130 CM DU SOL

• PRISE ETANCHE ENCASTREE
20 CM DU PLAN DE TRAVAIL

• ALIMENTATION APPAREIL

• PRISE RJ45

• BAES

• CENTRALE D'ALARME INCENDIE

• DIFFUSEUR SONORE

• DIFFUSEUR LUMINEUX

• DECLENCHEUR D'ALARME MANUEL

• DEVEROUILLAGE PORTE

• ARRET D'URGENCE ELECTRICITE
ET VENTILATION

• EXTINCTEUR

• VISIOPHONE AVEC VENTOUSE

• DIGICODE

• SERRURE A CODE

• SONDE DE QUALITE DE L'AIR

• TGBT

• CTA AU PLAFOND


• BALLON

06	
S	
Hsfp	
Mur	
Fp	
Sol	

ESPA
EXTER

+33,71 

+33,70 

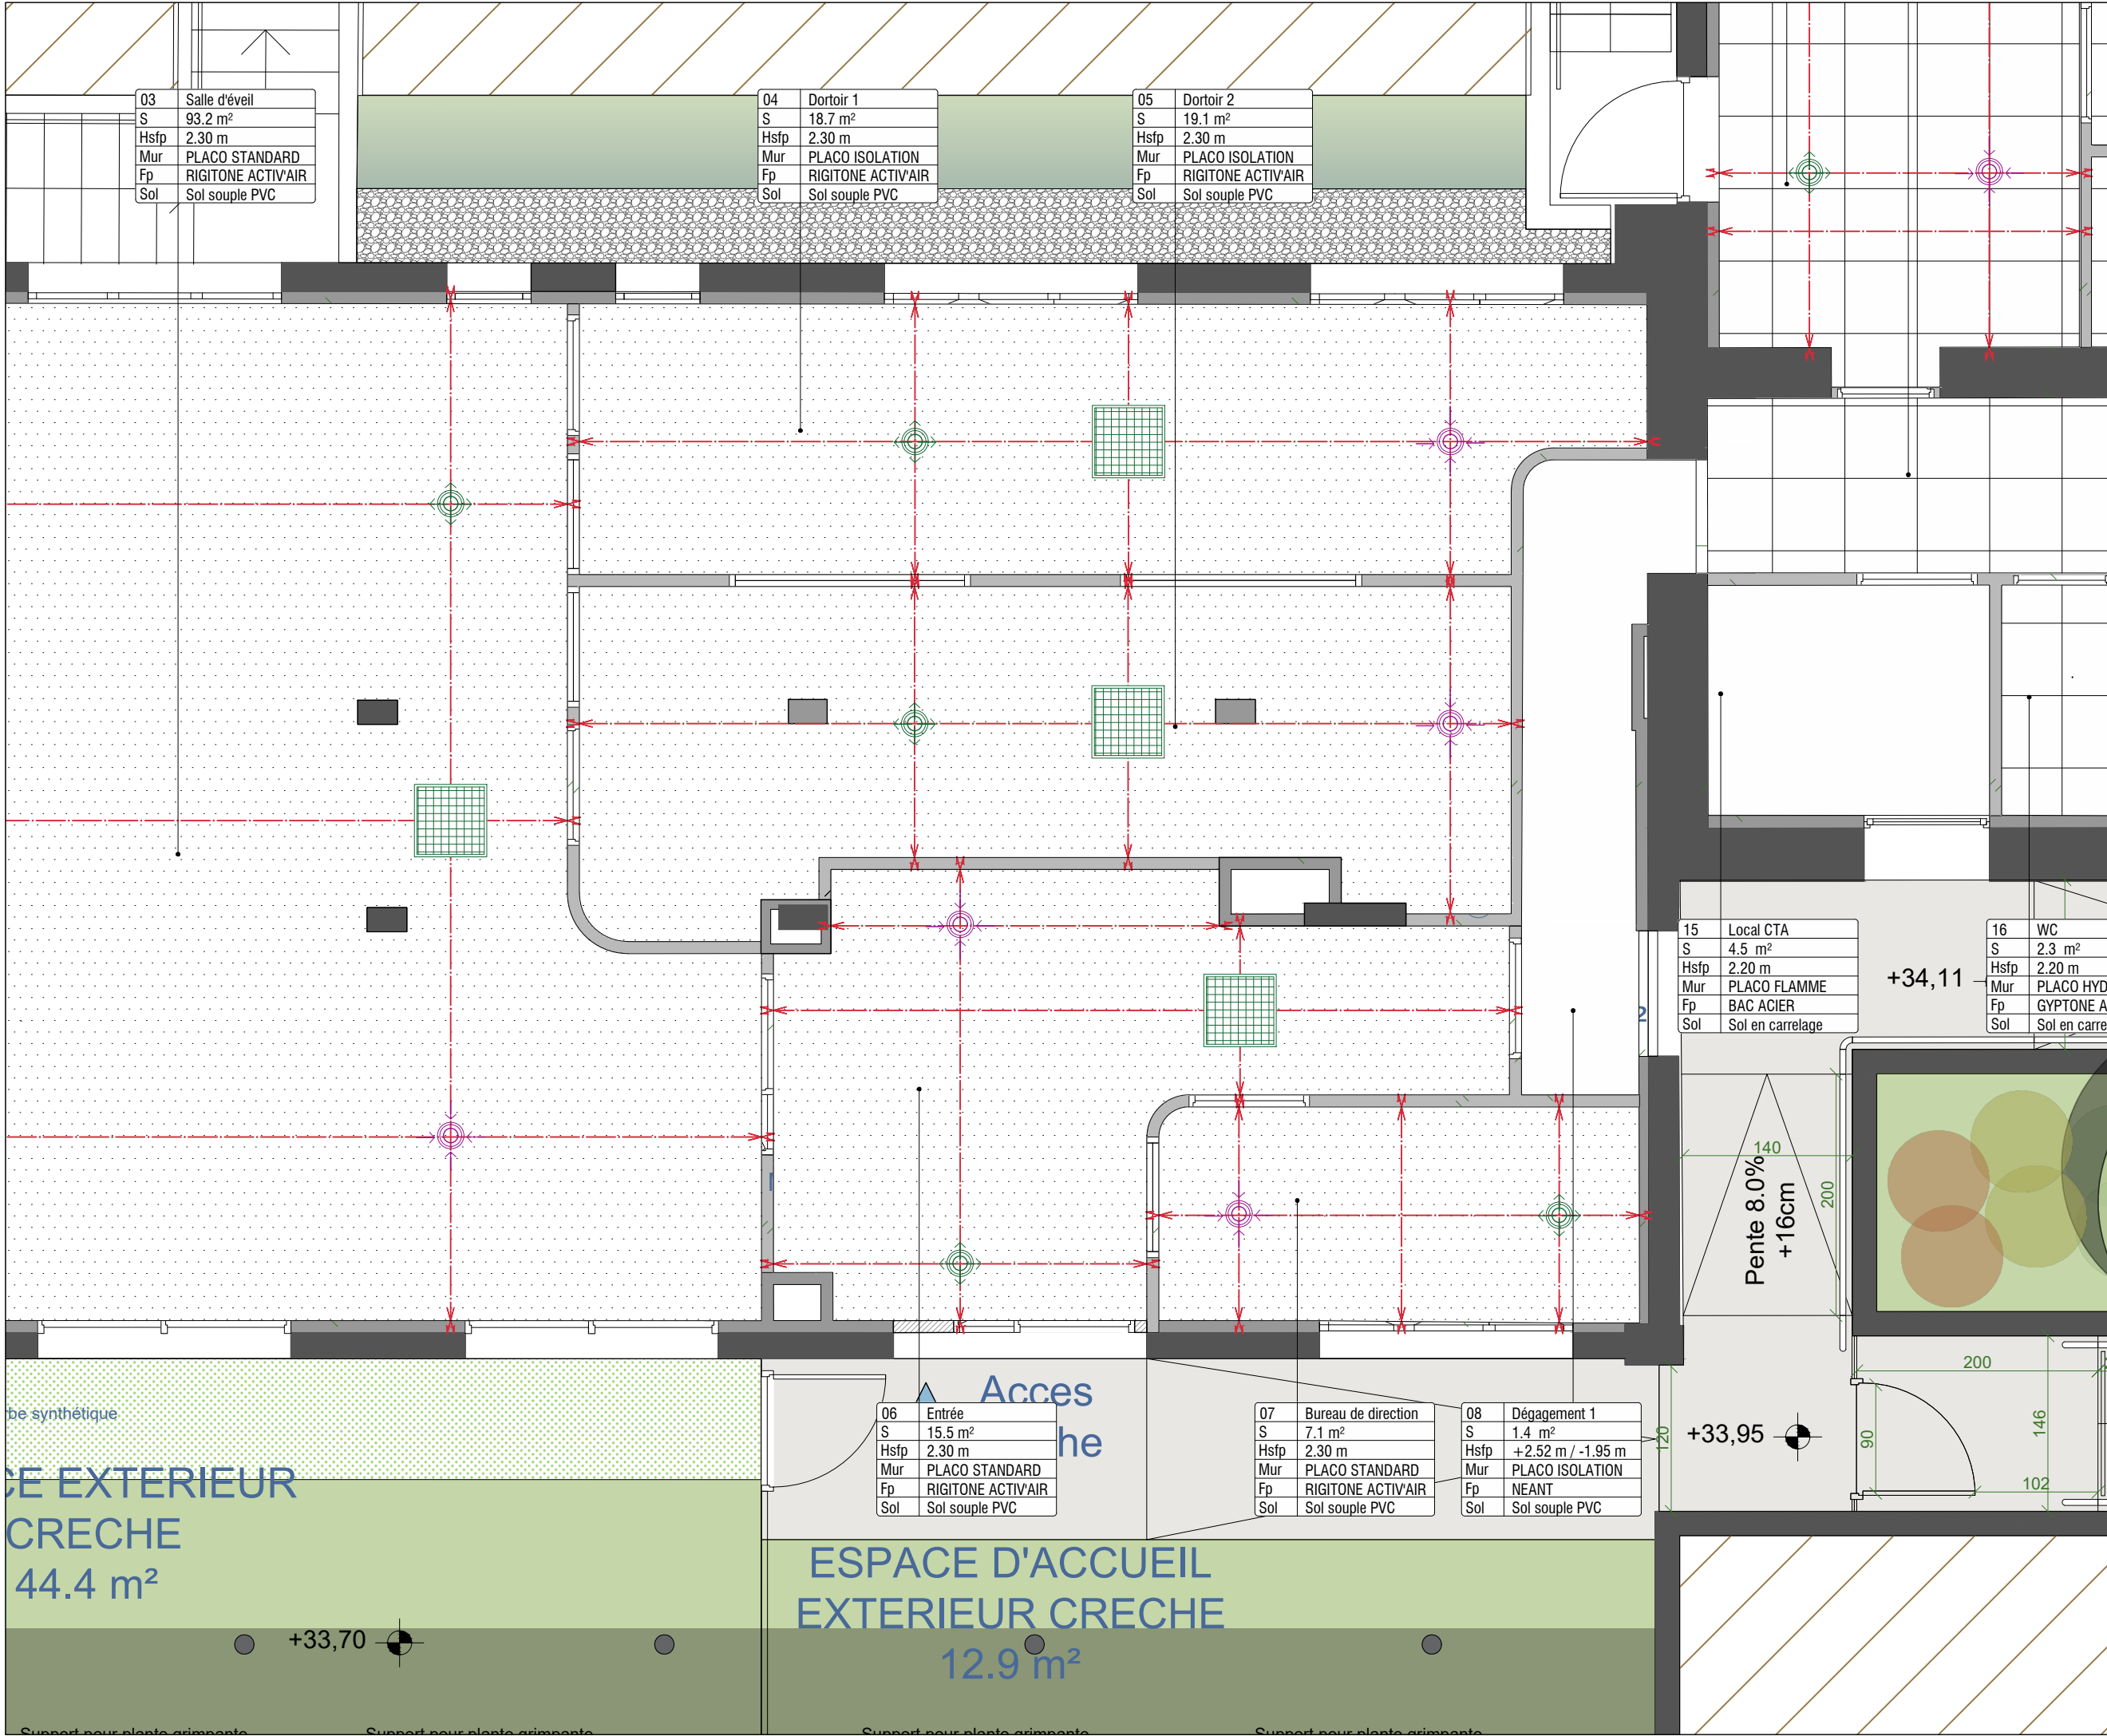

CREATION D'UN MULTI-ACCUEIL
ET D'UNE MAISON MEDICALE
78400 CHATOU

MOA

SARL LPC YVELINES
15 Rue de l'Orient78000 VERSAILLES

MOE

NAHK ARCHITECTURE
24 Rue Yves Toudic, 75010 Paris

NOM DU DOCUMENT

C.V.C
SECTEUR 2

PHASE

PRO.DCE

ECH.

1/50

INDICE

1.1

DATE

30/06/2023

MODIFICATIONS

INDICE

DATE

OBJET

1.1

30/06/2023

Diffusion initiale

CLIMATISATION / VENTILATION


• DIFFUSEUR REGLABLE CA
60 x 60 cm SOUFFLAGE / REP

• DIFFUSEUR CIRCULAIRE
SOUFFLAGE

• DIFFUSEUR CIRCULAIRE
REPRISE

• BOUCHE D'EXTRACTION

• CTA au plafond

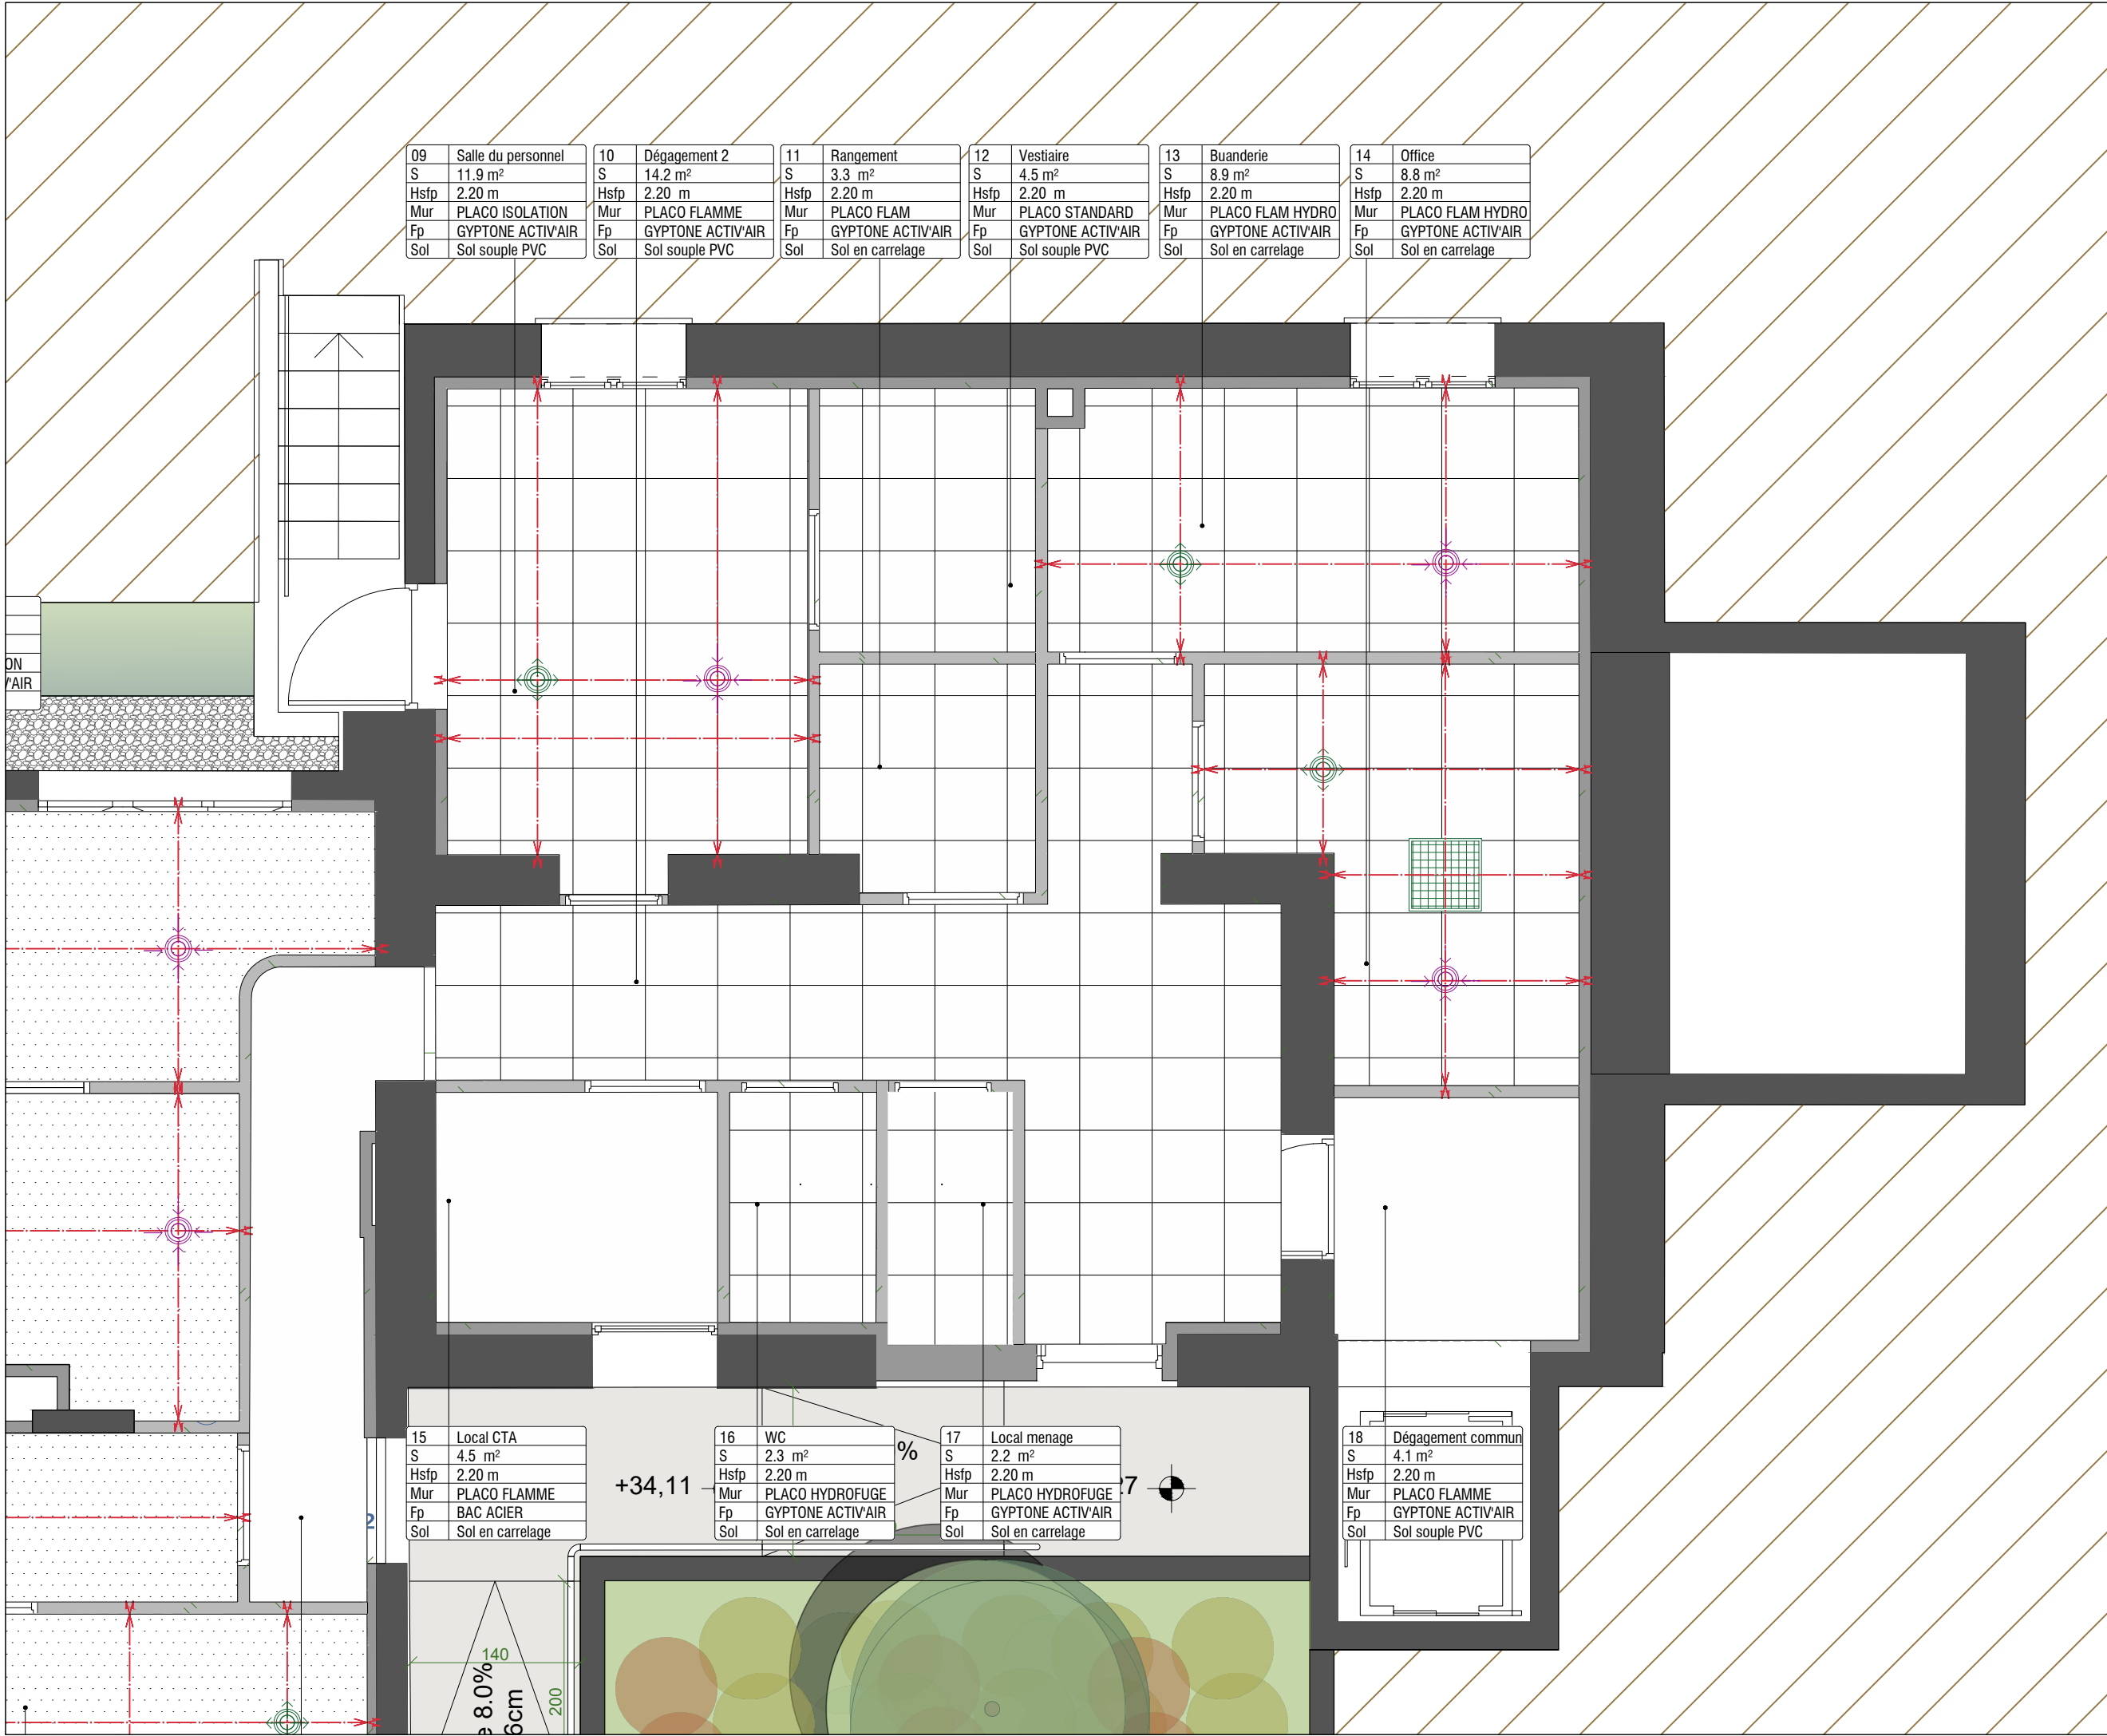

CREATION D'UN MULTI-ACCUEIL
ET D'UNE MAISON MEDICALE
78400 CHATOU

MOA

SARL LPC YVELINES
15 Rue de l'Orient78000 VERSAILLES

MOE

NAHK ARCHITECTURE
24 Rue Yves Toudic, 75010 Paris

NOM DU DOCUMENT

C.V.C
SECTEUR 3

PHASE

PRO.DCE

ECH.

1/50

INDICE

1.1

DATE

30/06/2023

MODIFICATIONS

INDICE

DATE

OBJET

1.1

30/06/2023

Diffusion initiale

CLIMATISATION / VENTILATION


• DIFFUSEUR REGLABLE CA
60 x 60 cm SOUFFLAGE / REP

• DIFFUSEUR CIRCULAIRE
SOUFFLAGE

• DIFFUSEUR CIRCULAIRE
REPRISE

• BOUCHE D'EXTRACTION

• CTA au plafond

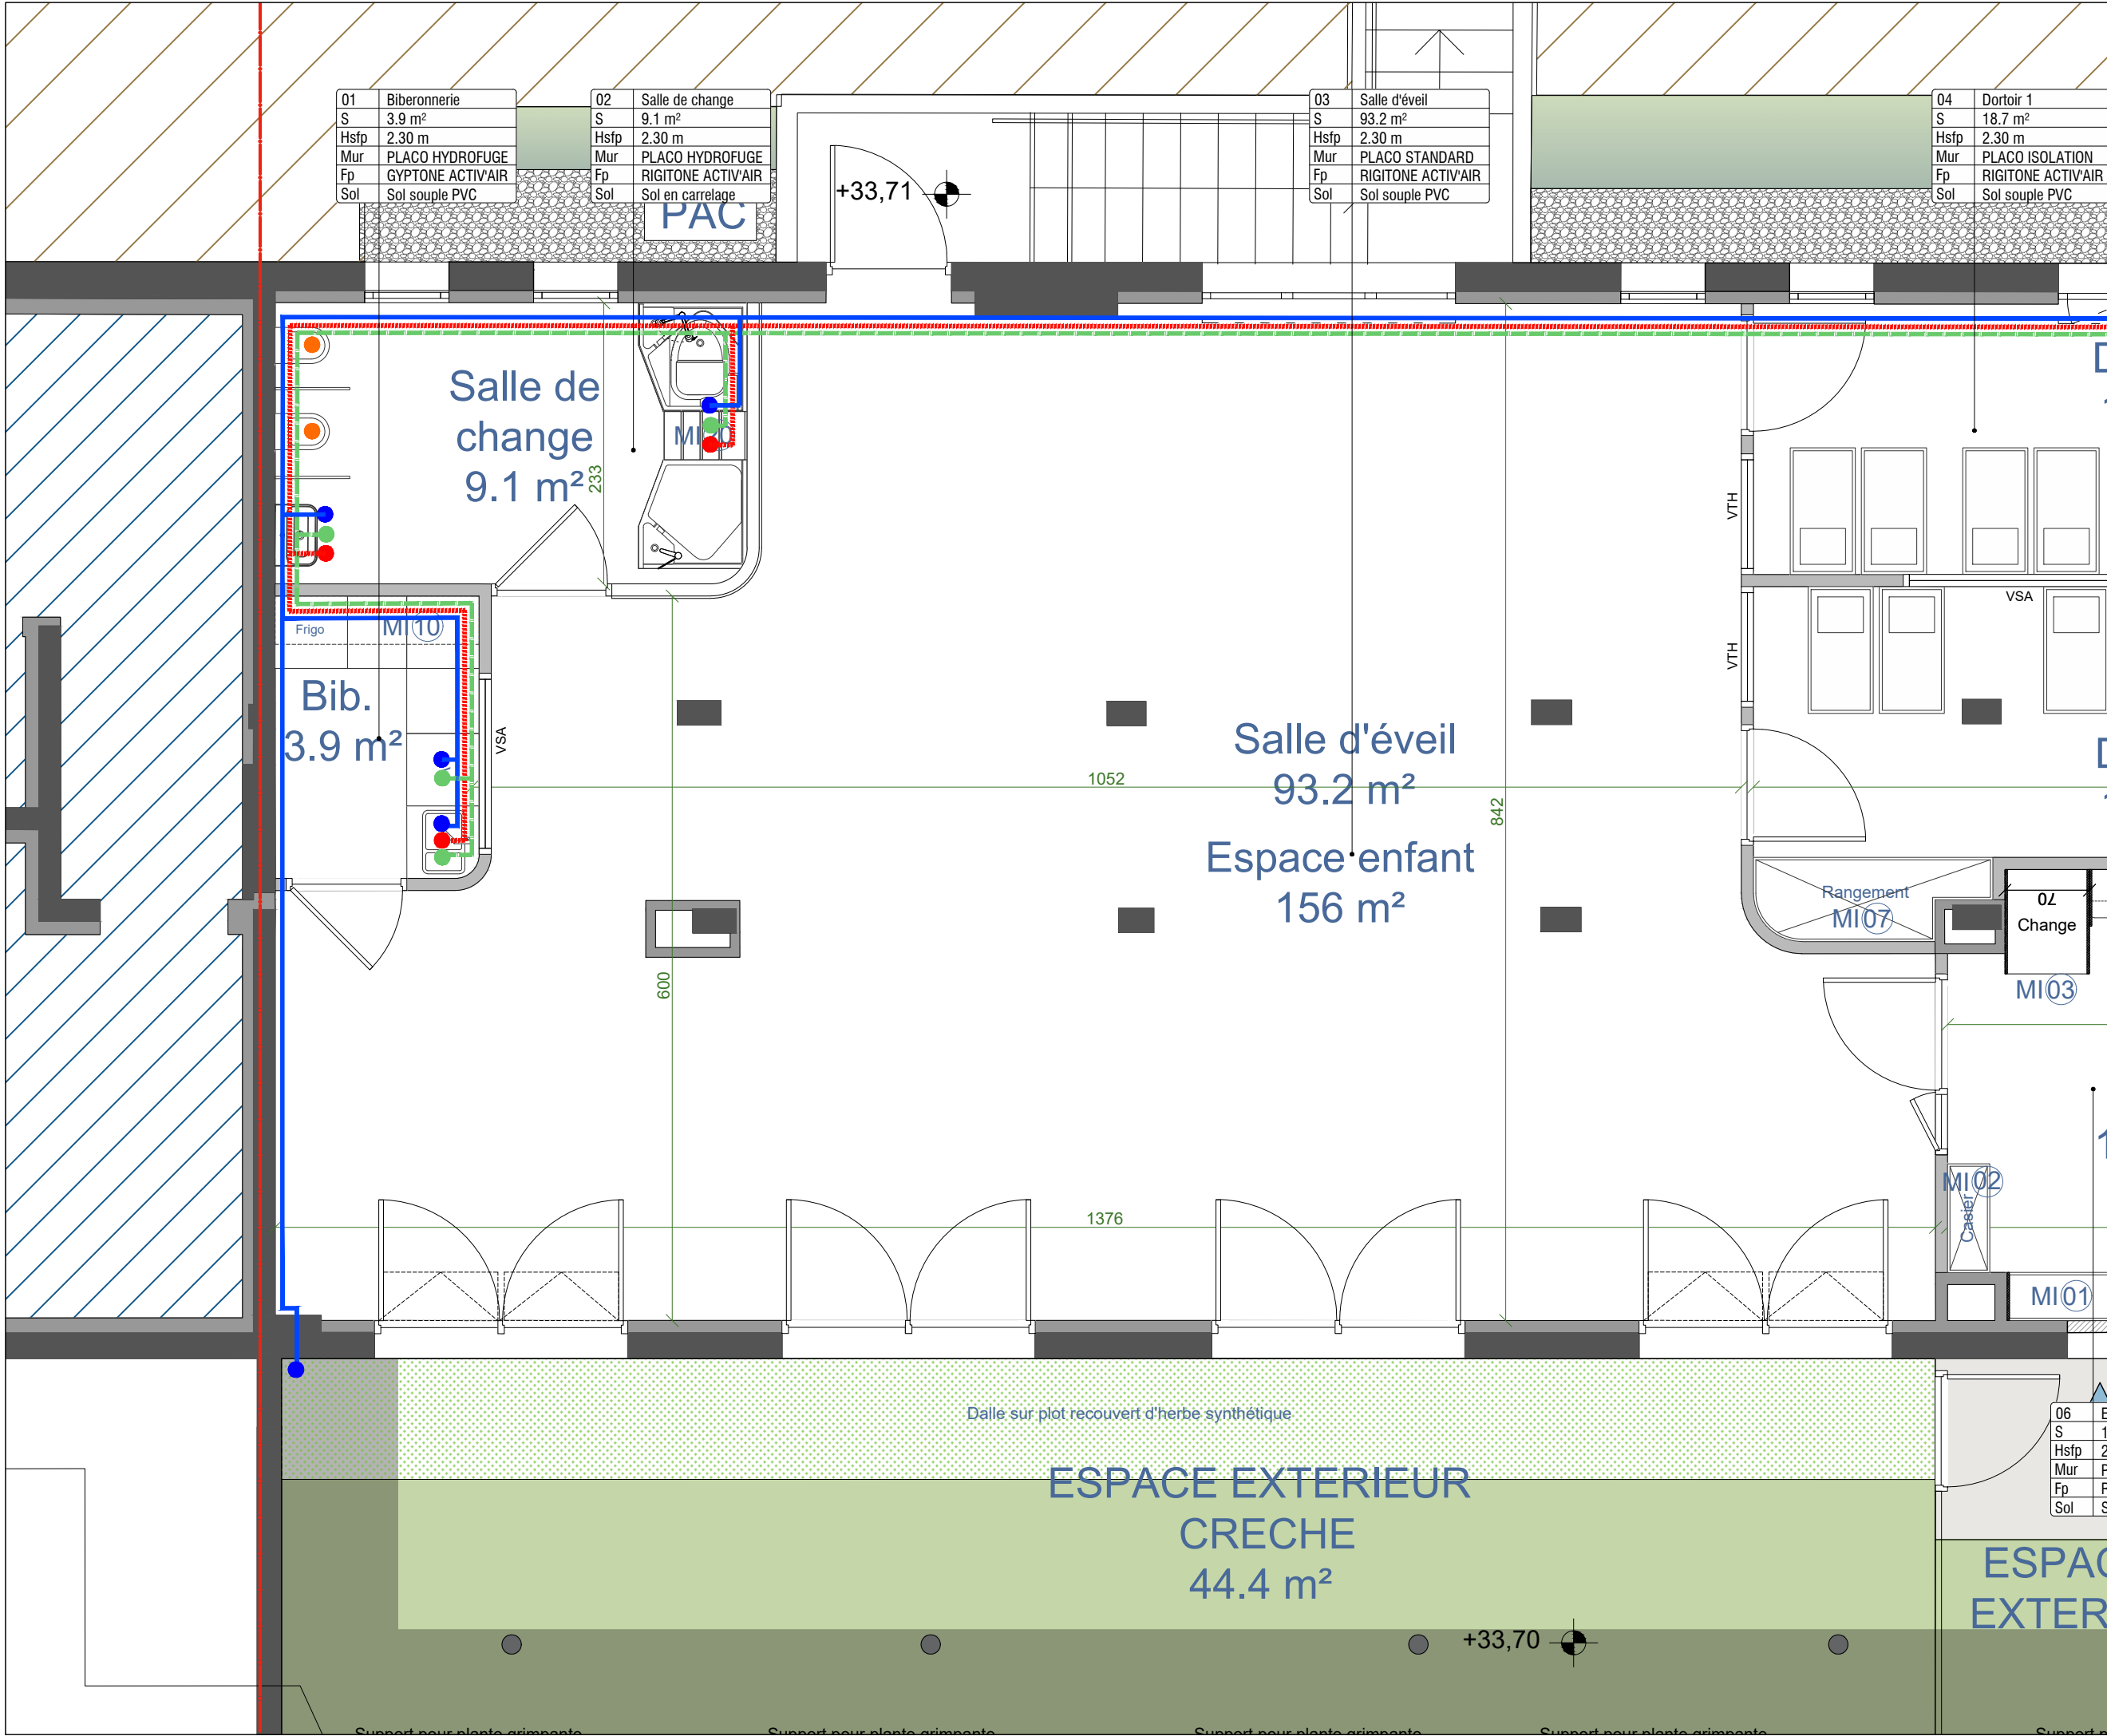

01	Biberonnerie
S	3.9 m²
Hsfp	2.30 m
Mur	PLACO HYDROFUGE
Fp	GYPTONE ACTIVAIR
Sol	Sol souple PVC

02	Salle de change
S	9.1 m²
Hsfp	2.30 m
Mur	PLACO HYDROFUGE
Fp	RIGITONE ACTIVAIR
Sol	Sol en carrelage

03	Salle d'éveil
S	93.2 m²
Hsfp	2.30 m
Mur	PLACO STANDARD
Fp	RIGITONE ACTIVAIR
Sol	Sol souple PVC

04	Dortoir 1
S	18.7 m²
Hsfp	2.30 m
Mur	PLACO ISOLATION
Fp	RIGITONE ACTIVAIR
Sol	Sol souple PVC

06	Espace extérieur
S	44.4 m²
Hsfp	2.30 m
Mur	PLACO STANDARD
Fp	RIGITONE ACTIVAIR
Sol	Sol en carrelage

CREATION D'UN MULTI-ACCUEIL
ET D'UNE MAISON MEDICALE
78400 CHATOU

MOA

SARL LPC YVELINES
15 Rue de l'Orient78000 VERSAILLES

MOE

NAHK ARCHITECTURE
24 Rue Yves Toudic, 75010 Paris

NOM DU DOCUMENT

PLOMBERIE
SECTEUR 1

PHASE	PRO.DCE	ECH.	1/50
INDICE	1.1	DATE	30/06/2023

MODIFICATIONS

INDICE	DATE	OBJET
1.1	30/06/2023	Diffusion initiale

PLOMBERIE

• CHAUFFE-EAU

• ATTENTE EAU FROIDE

• RESEAU EAU FROIDE

• RESEAU EAU CHAUDE

• RESEAU EAU USEES

• RESEAU EAU VANNES


• DESCENTE CONDUIT
EVACUATION EV

• ARRIVEE PAR LE HAUT CONDUIT
EVACUATION EV

• DESCENTE CONDUIT
EVACUATION EU

• ARRIVEE PAR LE HAUT CONDUIT
EVACUATION EU

• CARROTAGE REALISE

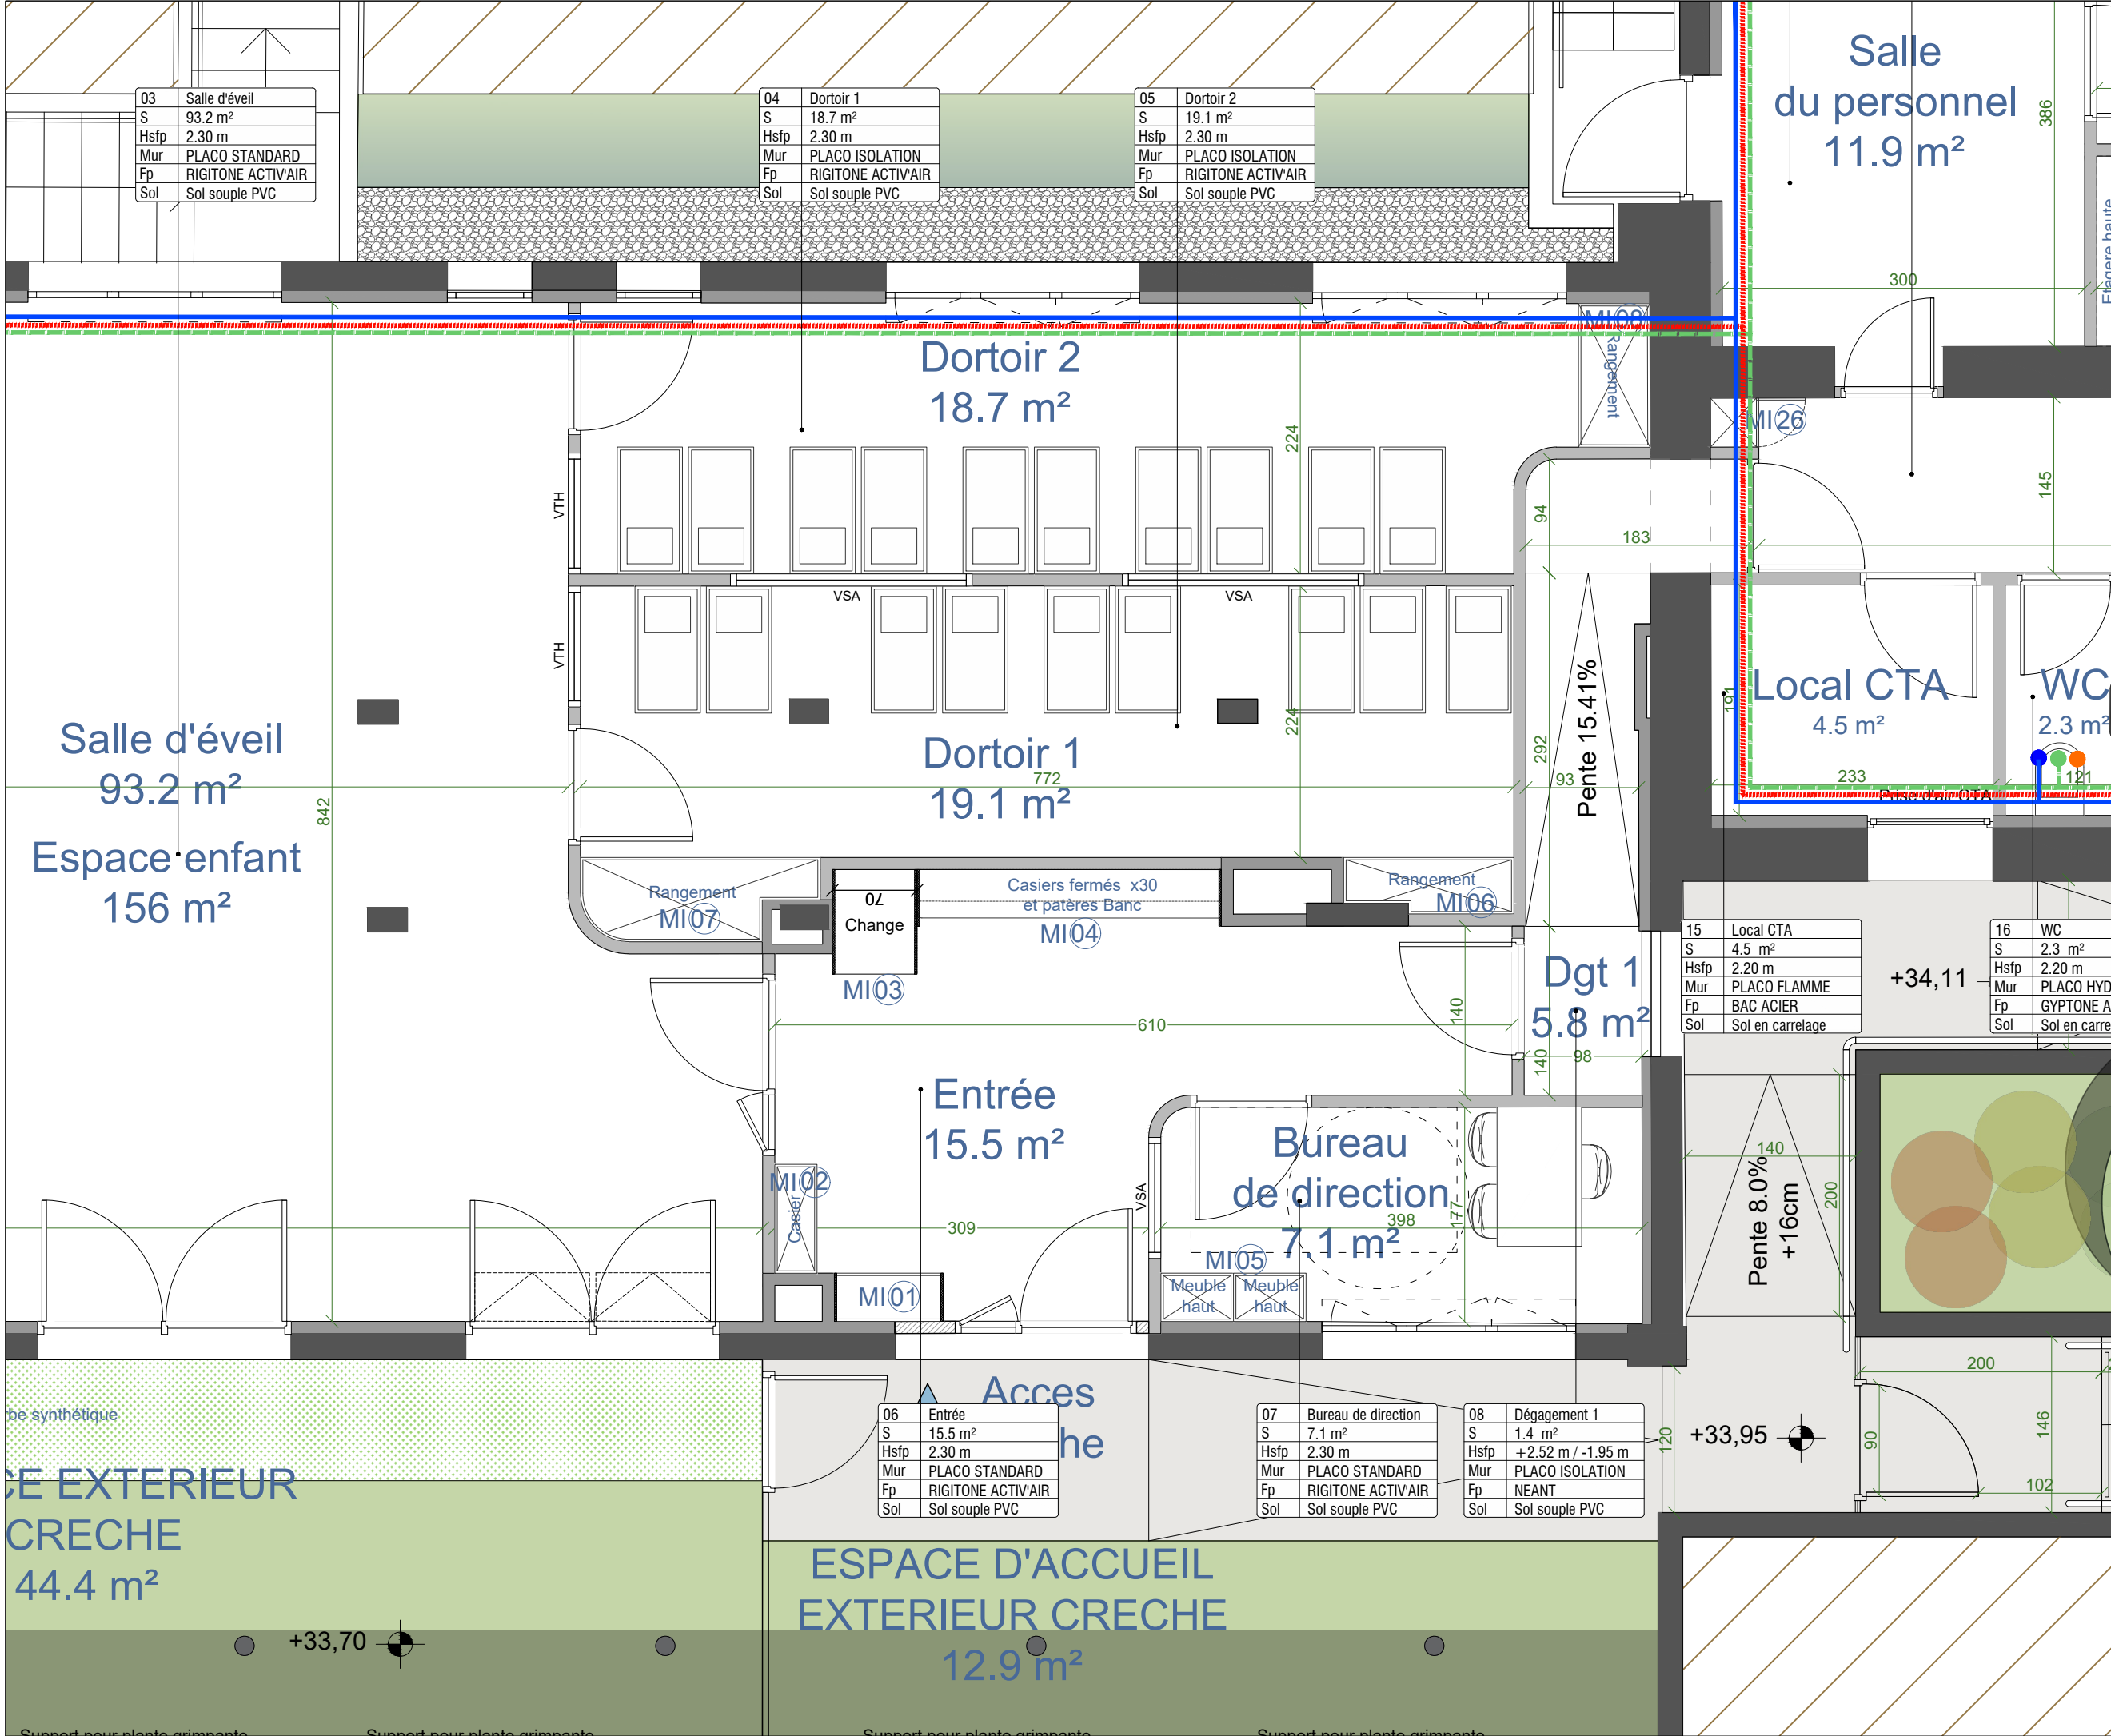

CREATION D'UN MULTI-ACCUEIL
ET D'UNE MAISON MEDICALE
78400 CHATOU

MOA

SARL LPC YVELINES
15 Rue de l'Orient78000 VERSAILLES

MOE

NAHK ARCHITECTURE
24 Rue Yves Toudic, 75010 Paris

NOM DU DOCUMENT

PLOMBERIE
SECTEUR 2

PHASE

PRO.DCE

ECH.

1/50

INDICE

1.1

DATE

30/06/2023

MODIFICATIONS

INDICE

DATE

OBJET

1.1

30/06/2023

Diffusion initiale

PLOMBERIE

• CHAUFFE-EAU

• ATTENTE EAU FROIDE

• RESEAU EAU FROIDE

• RESEAU EAU CHAUDE

• RESEAU EAU USEES

• RESEAU EAU VANNES


• DESCENTE CONDUIT
EVACUATION EV

• ARRIVEE PAR LE HAUT CONDUIT
EVACUATION EV

• DESCENTE CONDUIT
EVACUATION EU

• ARRIVEE PAR LE HAUT CONDUIT
EVACUATION EU

• CARROTAGE REALISE

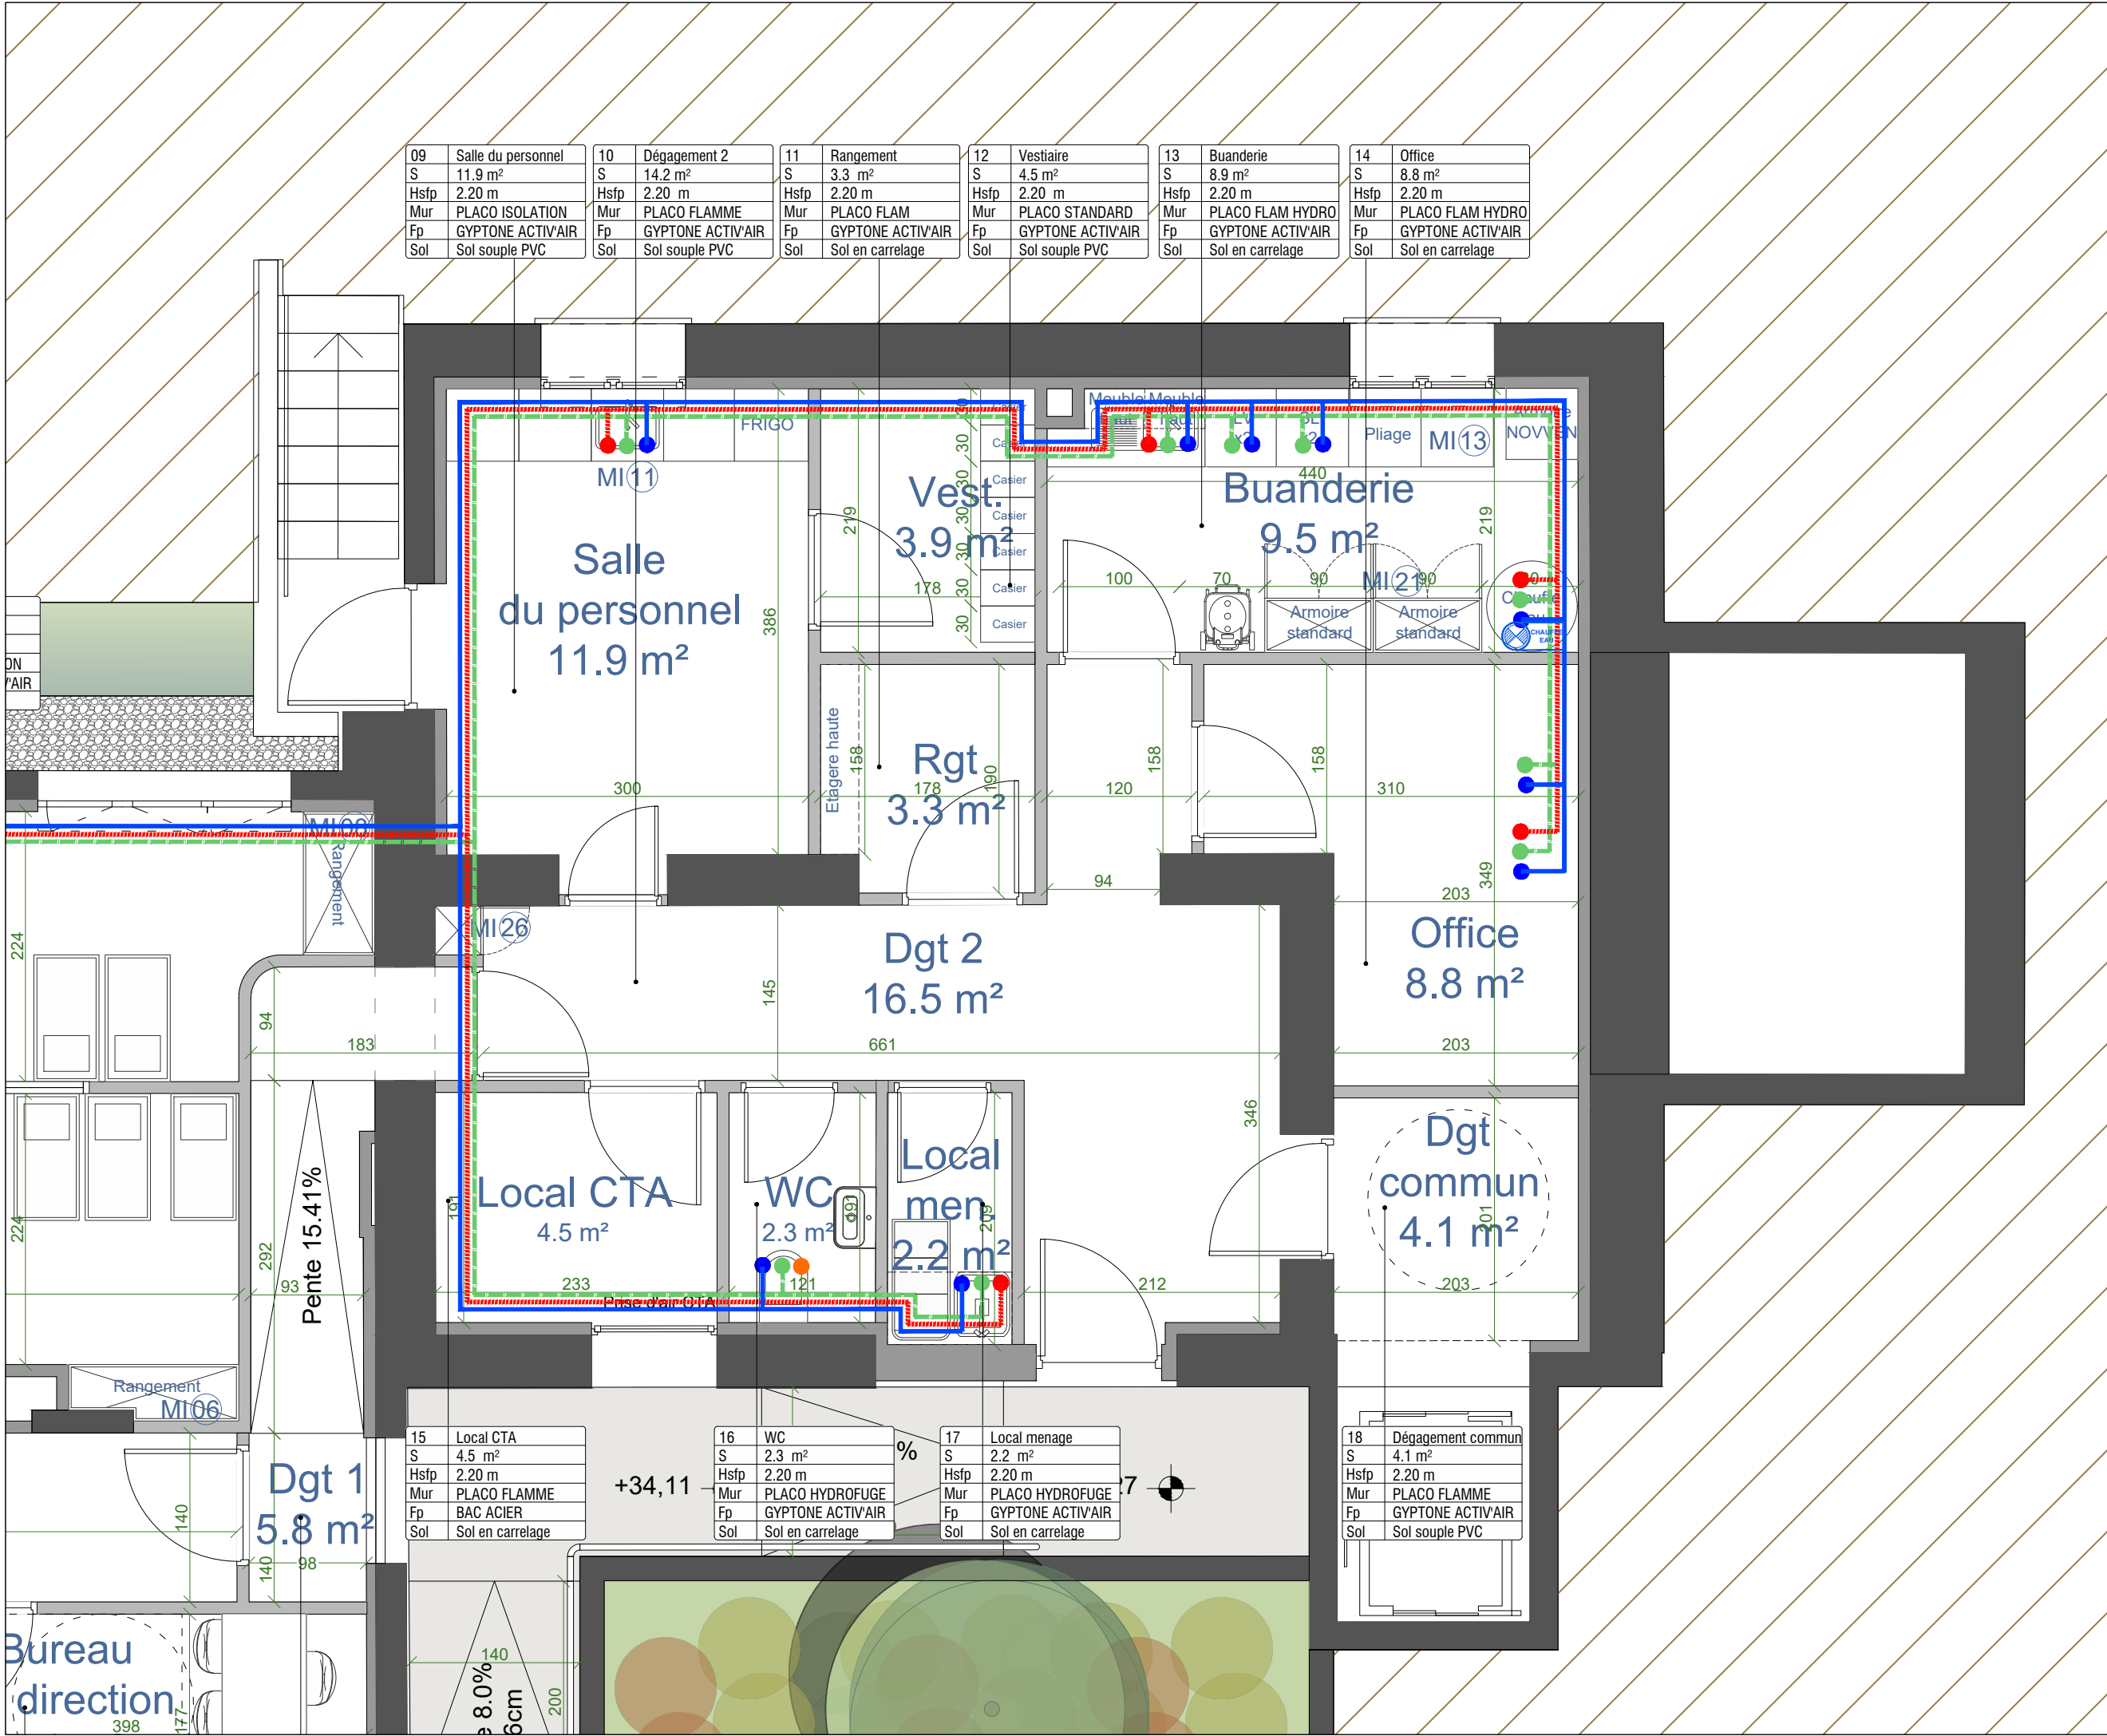

09	Salle du personnel	10	Dégagement 2	11	Rangement	12	Vestiaire	13	Buanderie	14	Office
S	11.9 m²	S	14.2 m²	S	3.3 m²	S	4.5 m²	S	8.9 m²	S	8.8 m²
Hsfp	2.20 m	Hsfp	2.20 m	Hsfp	2.20 m	Hsfp	2.20 m	Hsfp	2.20 m	Hsfp	2.20 m
Mur	PLACO ISOLATION	Mur	PLACO FLAMME	Mur	PLACO FLAM	Mur	PLACO STANDARD	Mur	PLACO FLAM HYDRO	Mur	PLACO FLAM HYDRO
Fp	GYPTONE ACTIV'AIR	Fp	GYPTONE ACTIV'AIR	Fp	GYPTONE ACTIV'AIR	Fp	GYPTONE ACTIV'AIR	Fp	GYPTONE ACTIV'AIR	Fp	GYPTONE ACTIV'AIR
Sol	Sol souple PVC	Sol	Sol souple PVC	Sol	Sol en carrelage	Sol	Sol souple PVC	Sol	Sol en carrelage	Sol	Sol en carrelage

15	Local CTA
S	4.5 m²
Hsfp	2.20 m
Mur	PLACO FLAMME
Fp	BAC ACIER
Sol	Sol en carrelage

16	WC
S	2.3 m²
Hsfp	2.20 m
Mur	PLACO HYDROFUGE
Fp	GYPTONE ACTIV'AIR
Sol	Sol en carrelage

17	Local menage
S	2.2 m²
Hsfp	2.20 m
Mur	PLACO HYDROFUGE
Fp	GYPTONE ACTIV'AIR
Sol	Sol en carrelage

18	Dégagement commun
S	4.1 m²
Hsfp	2.20 m
Mur	PLACO FLAMME
Fp	GYPTONE ACTIV'AIR
Sol	Sol souple PVC

CREATION D'UN MULTI-ACCUEIL
ET D'UNE MAISON MEDICALE
78400 CHATOU

MOA

SARL LPC YVELINES
15 Rue de l'Orient78000 VERSAILLES

MOE

NAHK ARCHITECTURE
24 Rue Yves Toudic, 75010 Paris

NOM DU DOCUMENT

PLOMBERIE
SECTEUR 3

PHASE

PRO.DCE

ECH.

1/50

INDICE

1.1

DATE

30/06/2023

MODIFICATIONS

INDICE

DATE

OBJET

1.1

30/06/2023

Diffusion initiale

PLOMBERIE

• CHAUFFE-EAU

• ATTENTE EAU FROIDE

• RESEAU EAU FROIDE

• RESEAU EAU CHAUDE

• RESEAU EAU USEES

• RESEAU EAU VANNES


• DESCENTE CONDUIT
EVACUATION EV

• ARRIVEE PAR LE HAUT CONDUIT
EVACUATION EV

• DESCENTE CONDUIT
EVACUATION EU

• ARRIVEE PAR LE HAUT CONDUIT
EVACUATION EU

• CARROTAGE REALISE

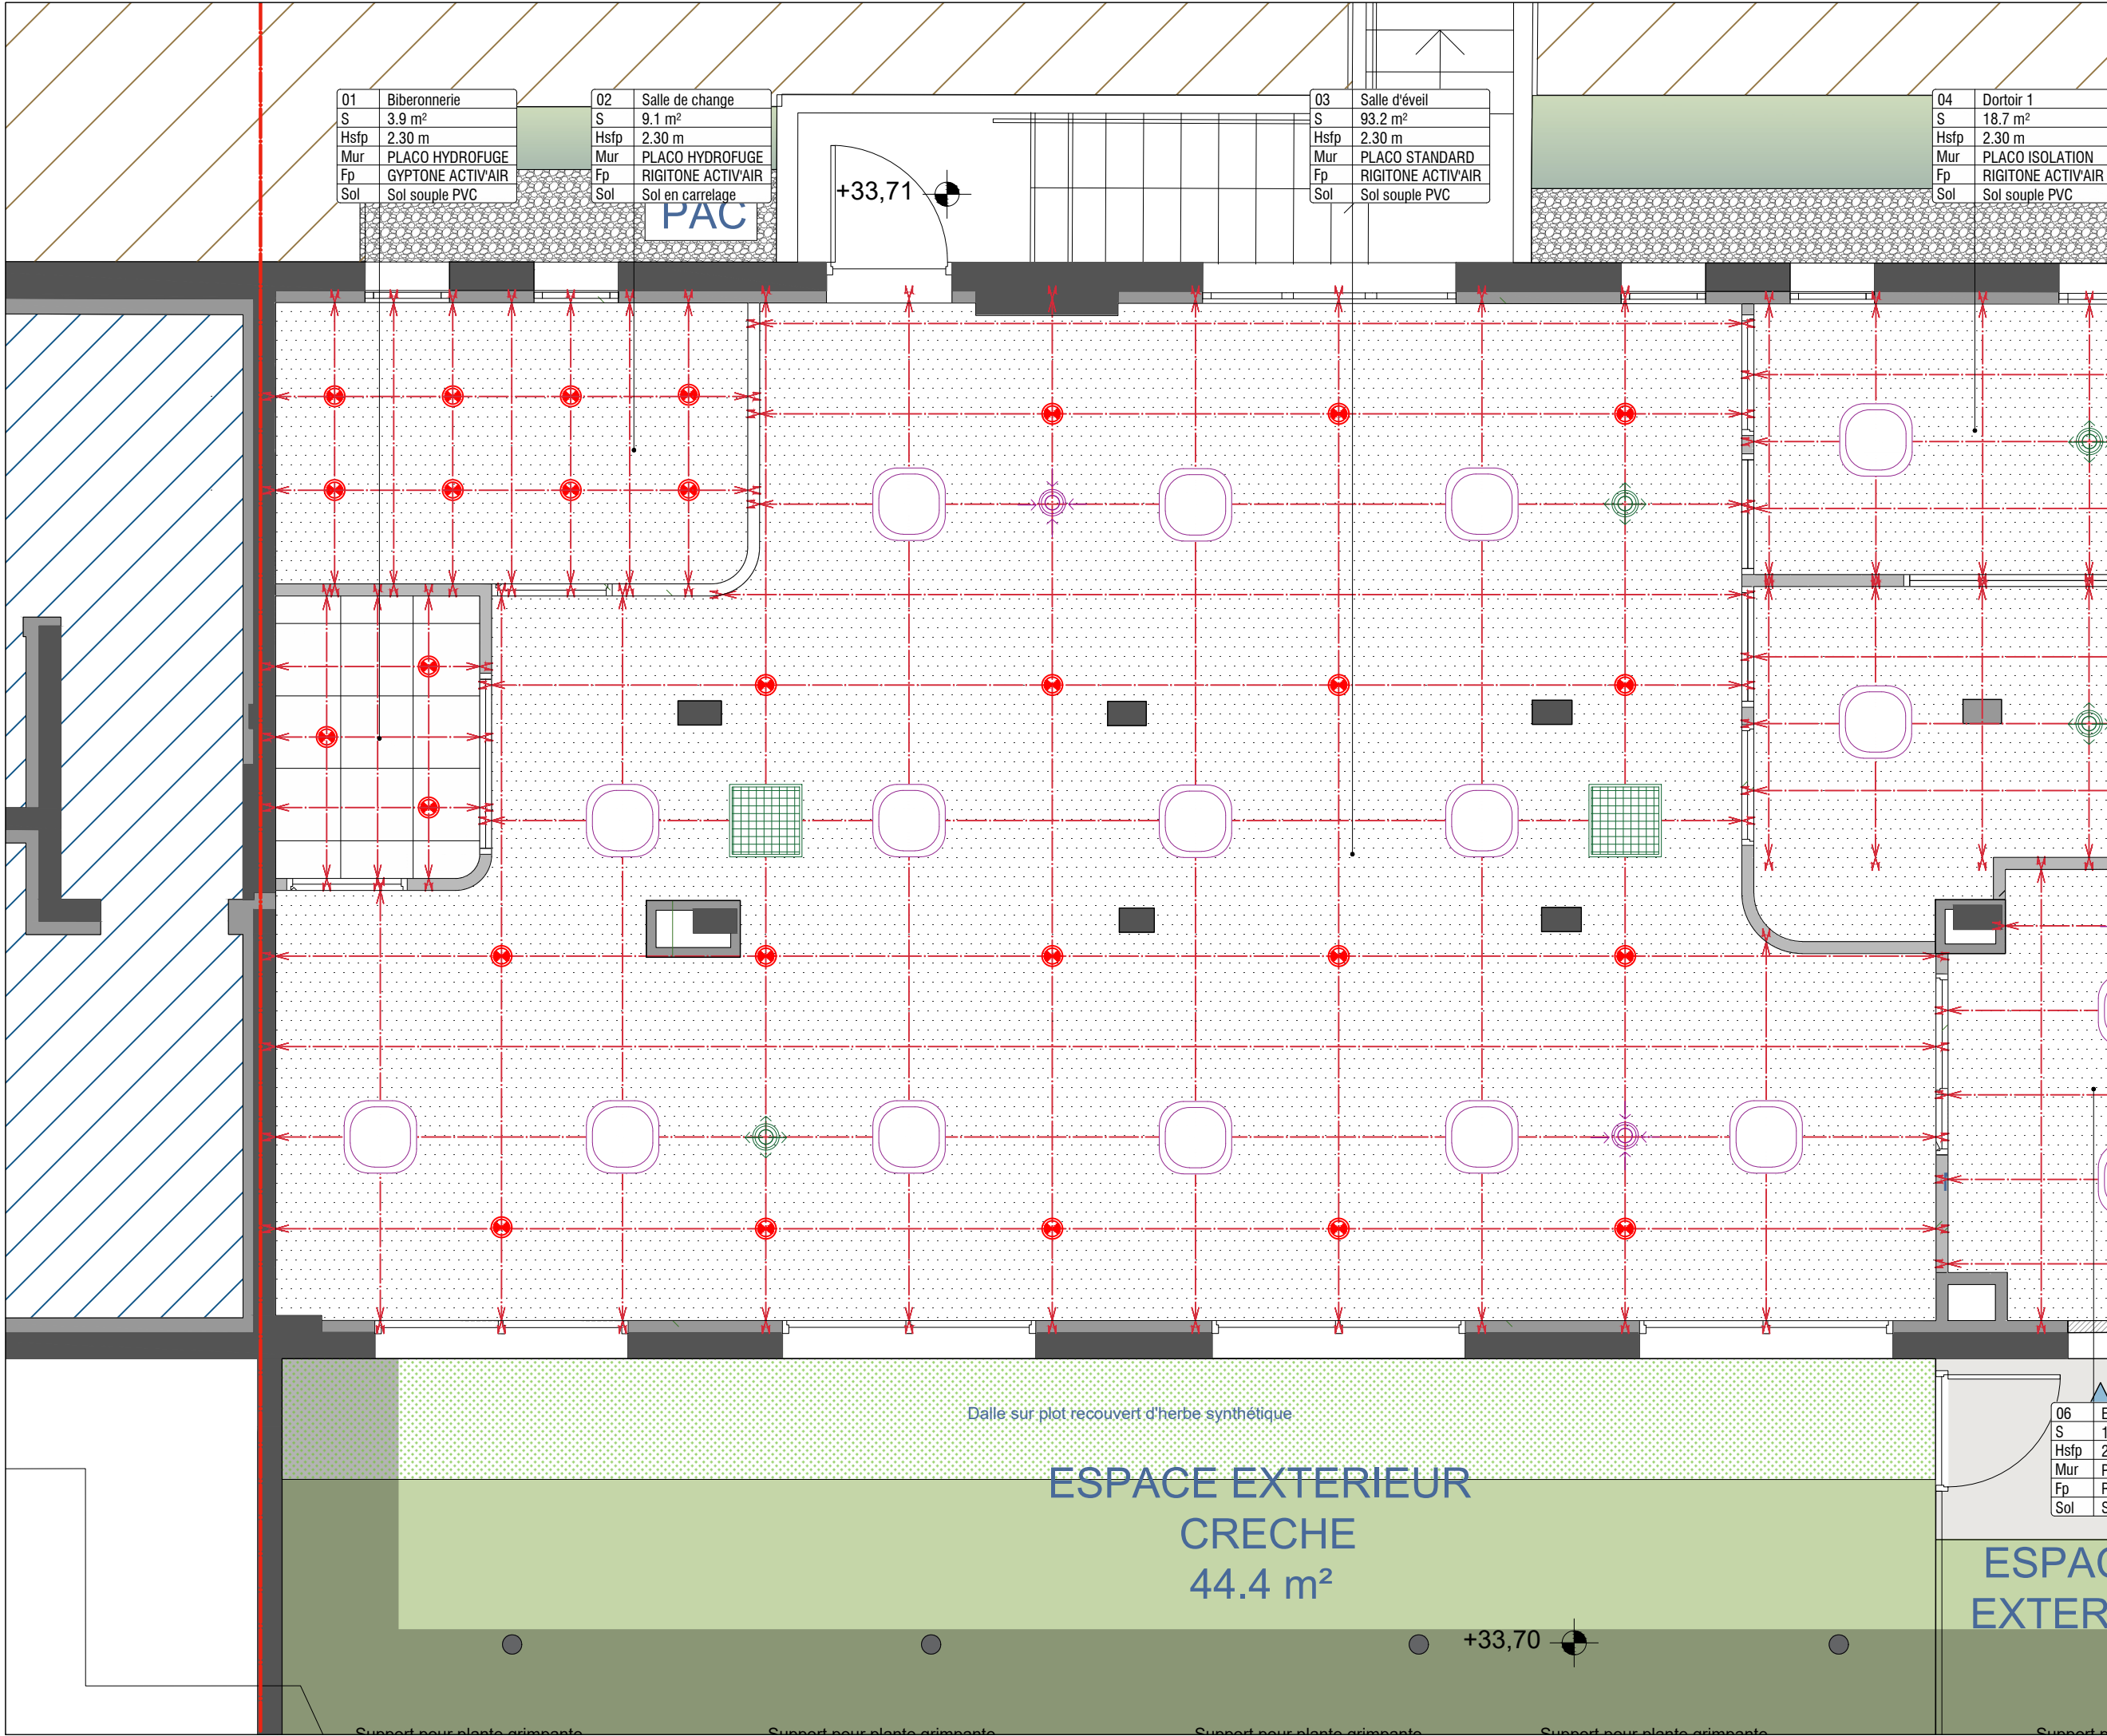

CREATION D'UN MULTI-ACCUEIL
ET D'UNE MAISON MEDICALE
78400 CHATOU

MOA

SARL LPC YVELINES
15 Rue de l'Orient78000 VERSAILLES

MOE

NAHK ARCHITECTURE
24 Rue Yves Toudic, 75010 Paris

NOM DU DOCUMENT

REVETEMENT
FAUX PLAFOND
SECTEUR 1

PHASE

PRO.DCE

ECH.

1/50

INDICE

1.1

DATE

30/06/2023

MODIFICATIONS

INDICE

DATE

OBJET

1.1

30/06/2023


Diffusion initiale

FAUX PLAFOND

• GYPTONE ACTIV' AIR
BASE 31 E 24- 60 x 60 cm

• RIGITONE ACTIV'AIR
8-15 /20

• BAC ACIER

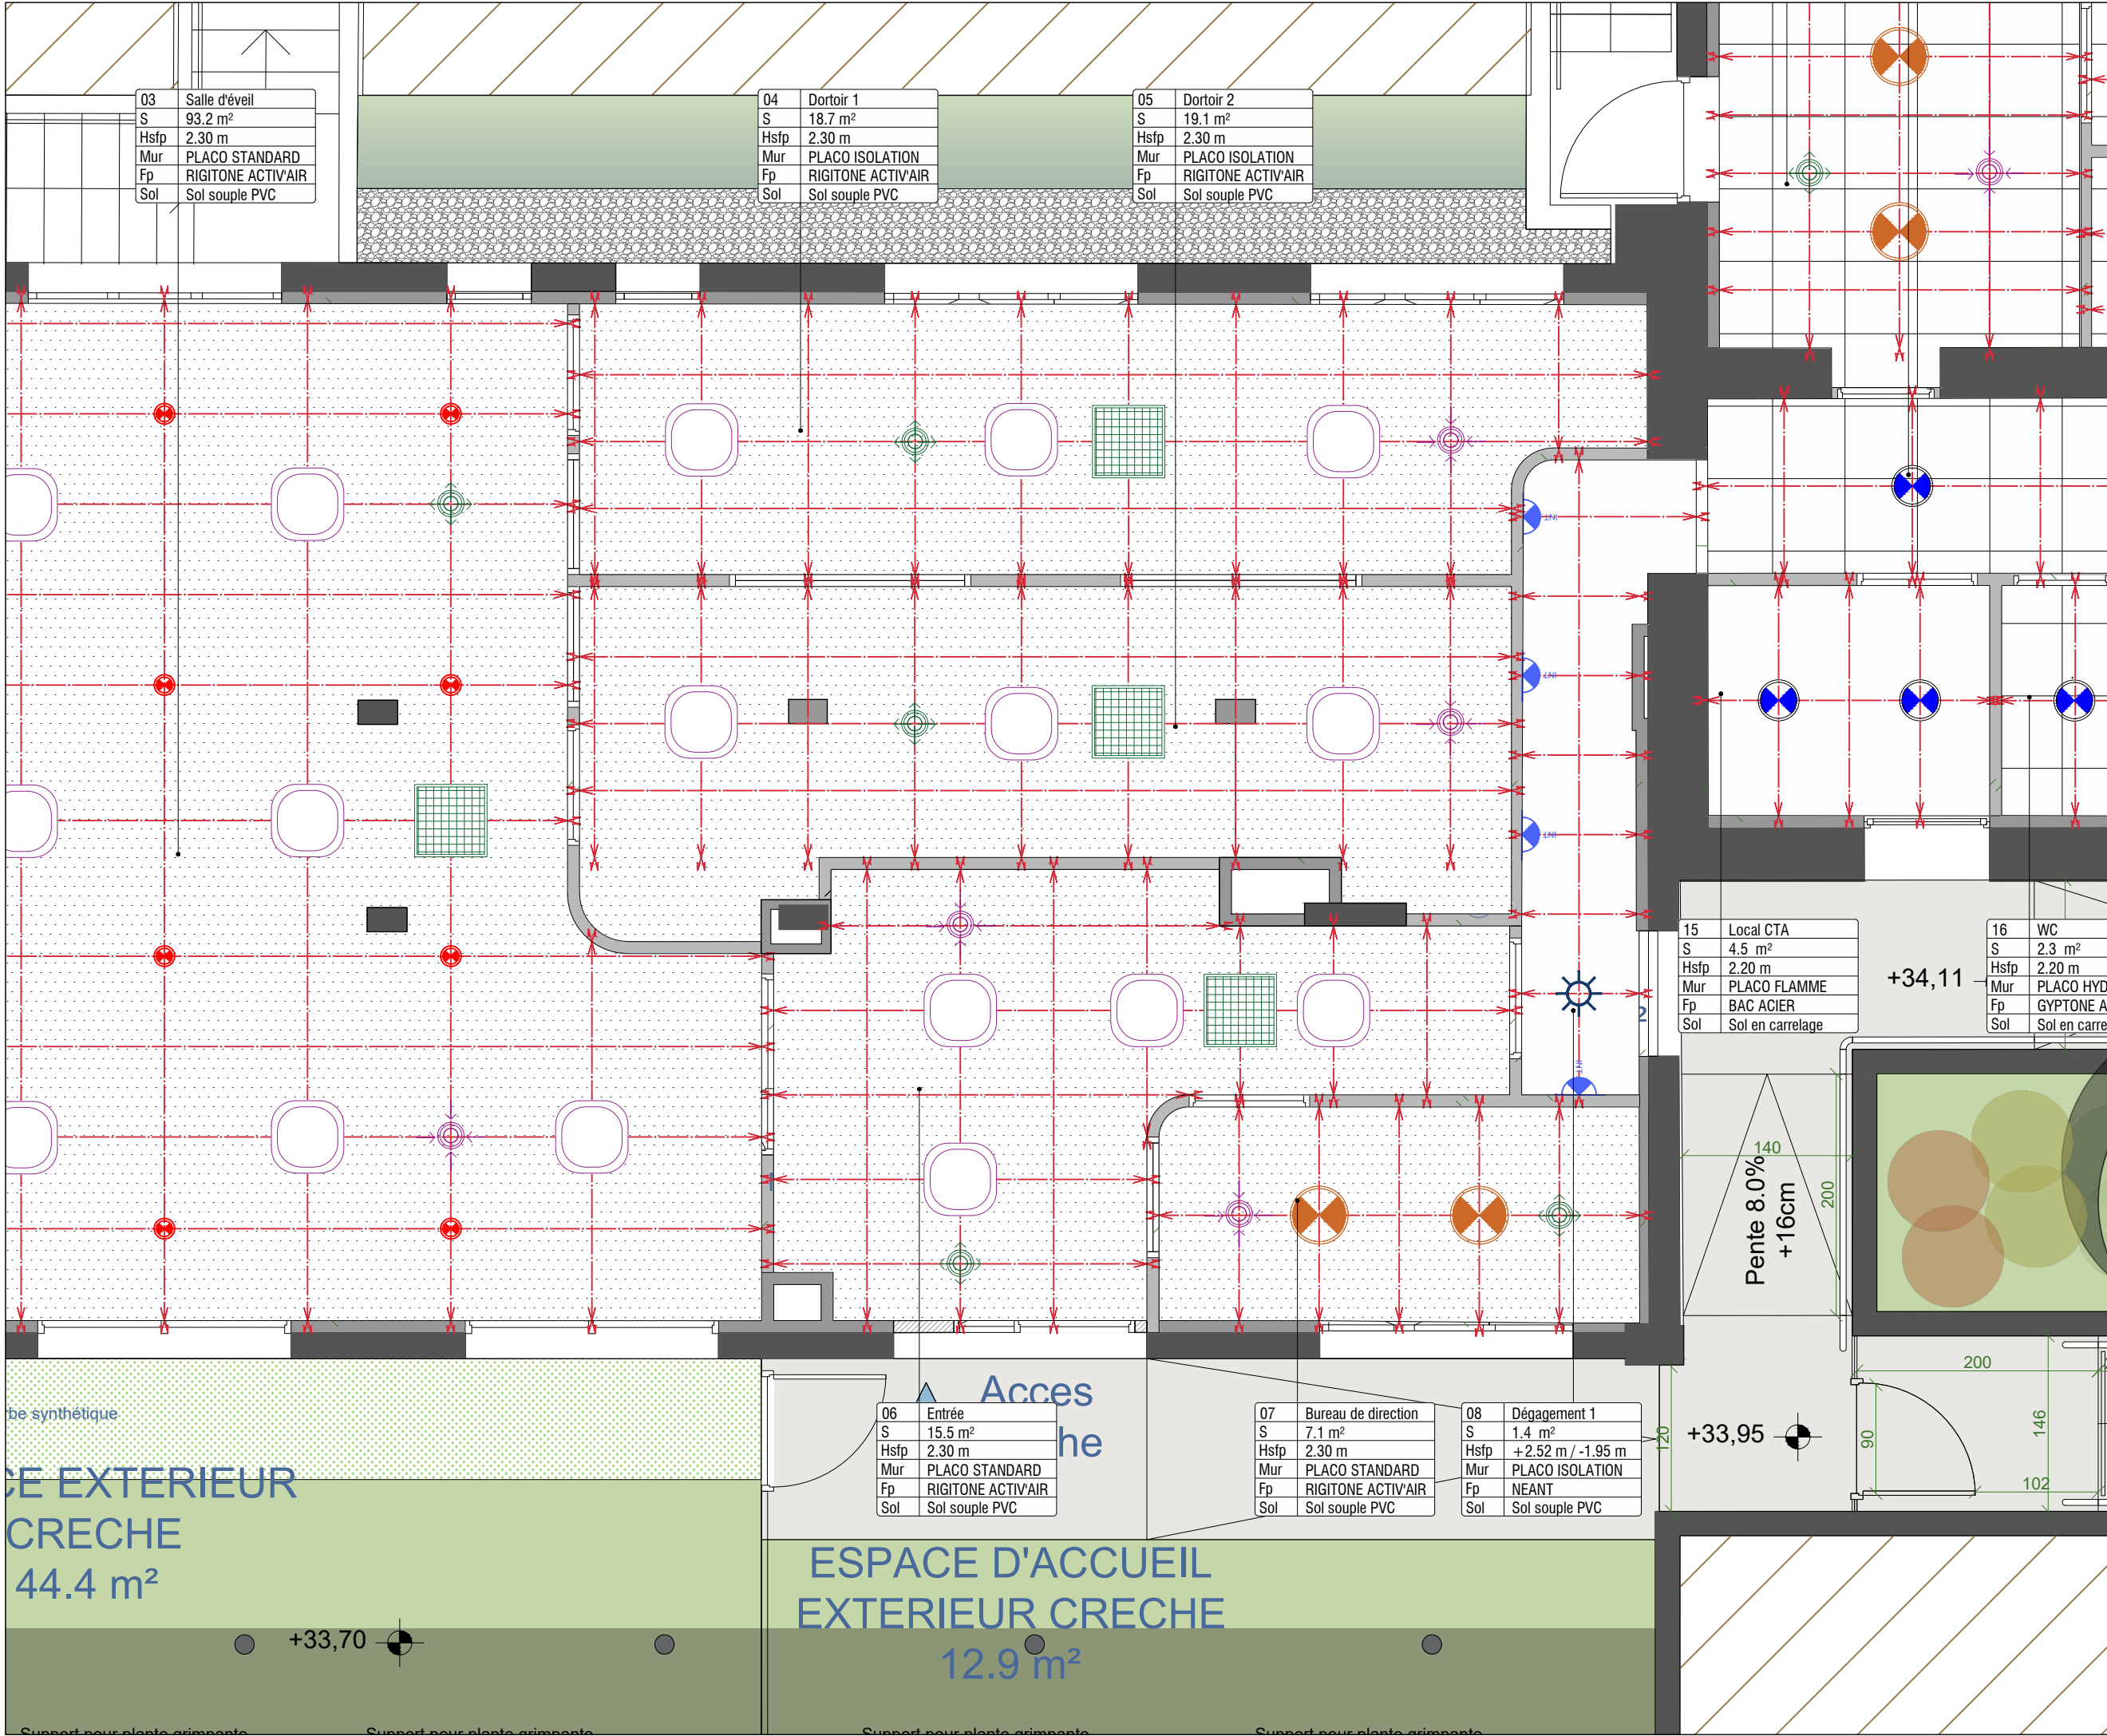

CREATION D'UN MULTI-ACCUEIL
ET D'UNE MAISON MEDICALE
78400 CHATOU

MOA

SARL LPC YVELINES
15 Rue de l'Orient78000 VERSAILLES

MOE

NAHK ARCHITECTURE
24 Rue Yves Toudic, 75010 Paris

NOM DU DOCUMENT

REVETEMENT
FAUX PLAFOND
SECTEUR 2

PHASE

PRO.DCE

ECH.

1/50

INDICE

1.1

DATE

30/06/2023

MODIFICATIONS

INDICE

DATE

OBJET

1.1

30/06/2023


Diffusion initiale

FAUX PLAFOND

• GYPTONE ACTIV' AIR
BASE 31 E 24- 60 x 60 cm

• RIGITONE ACTIV'AIR
8-15 /20

• BAC ACIER

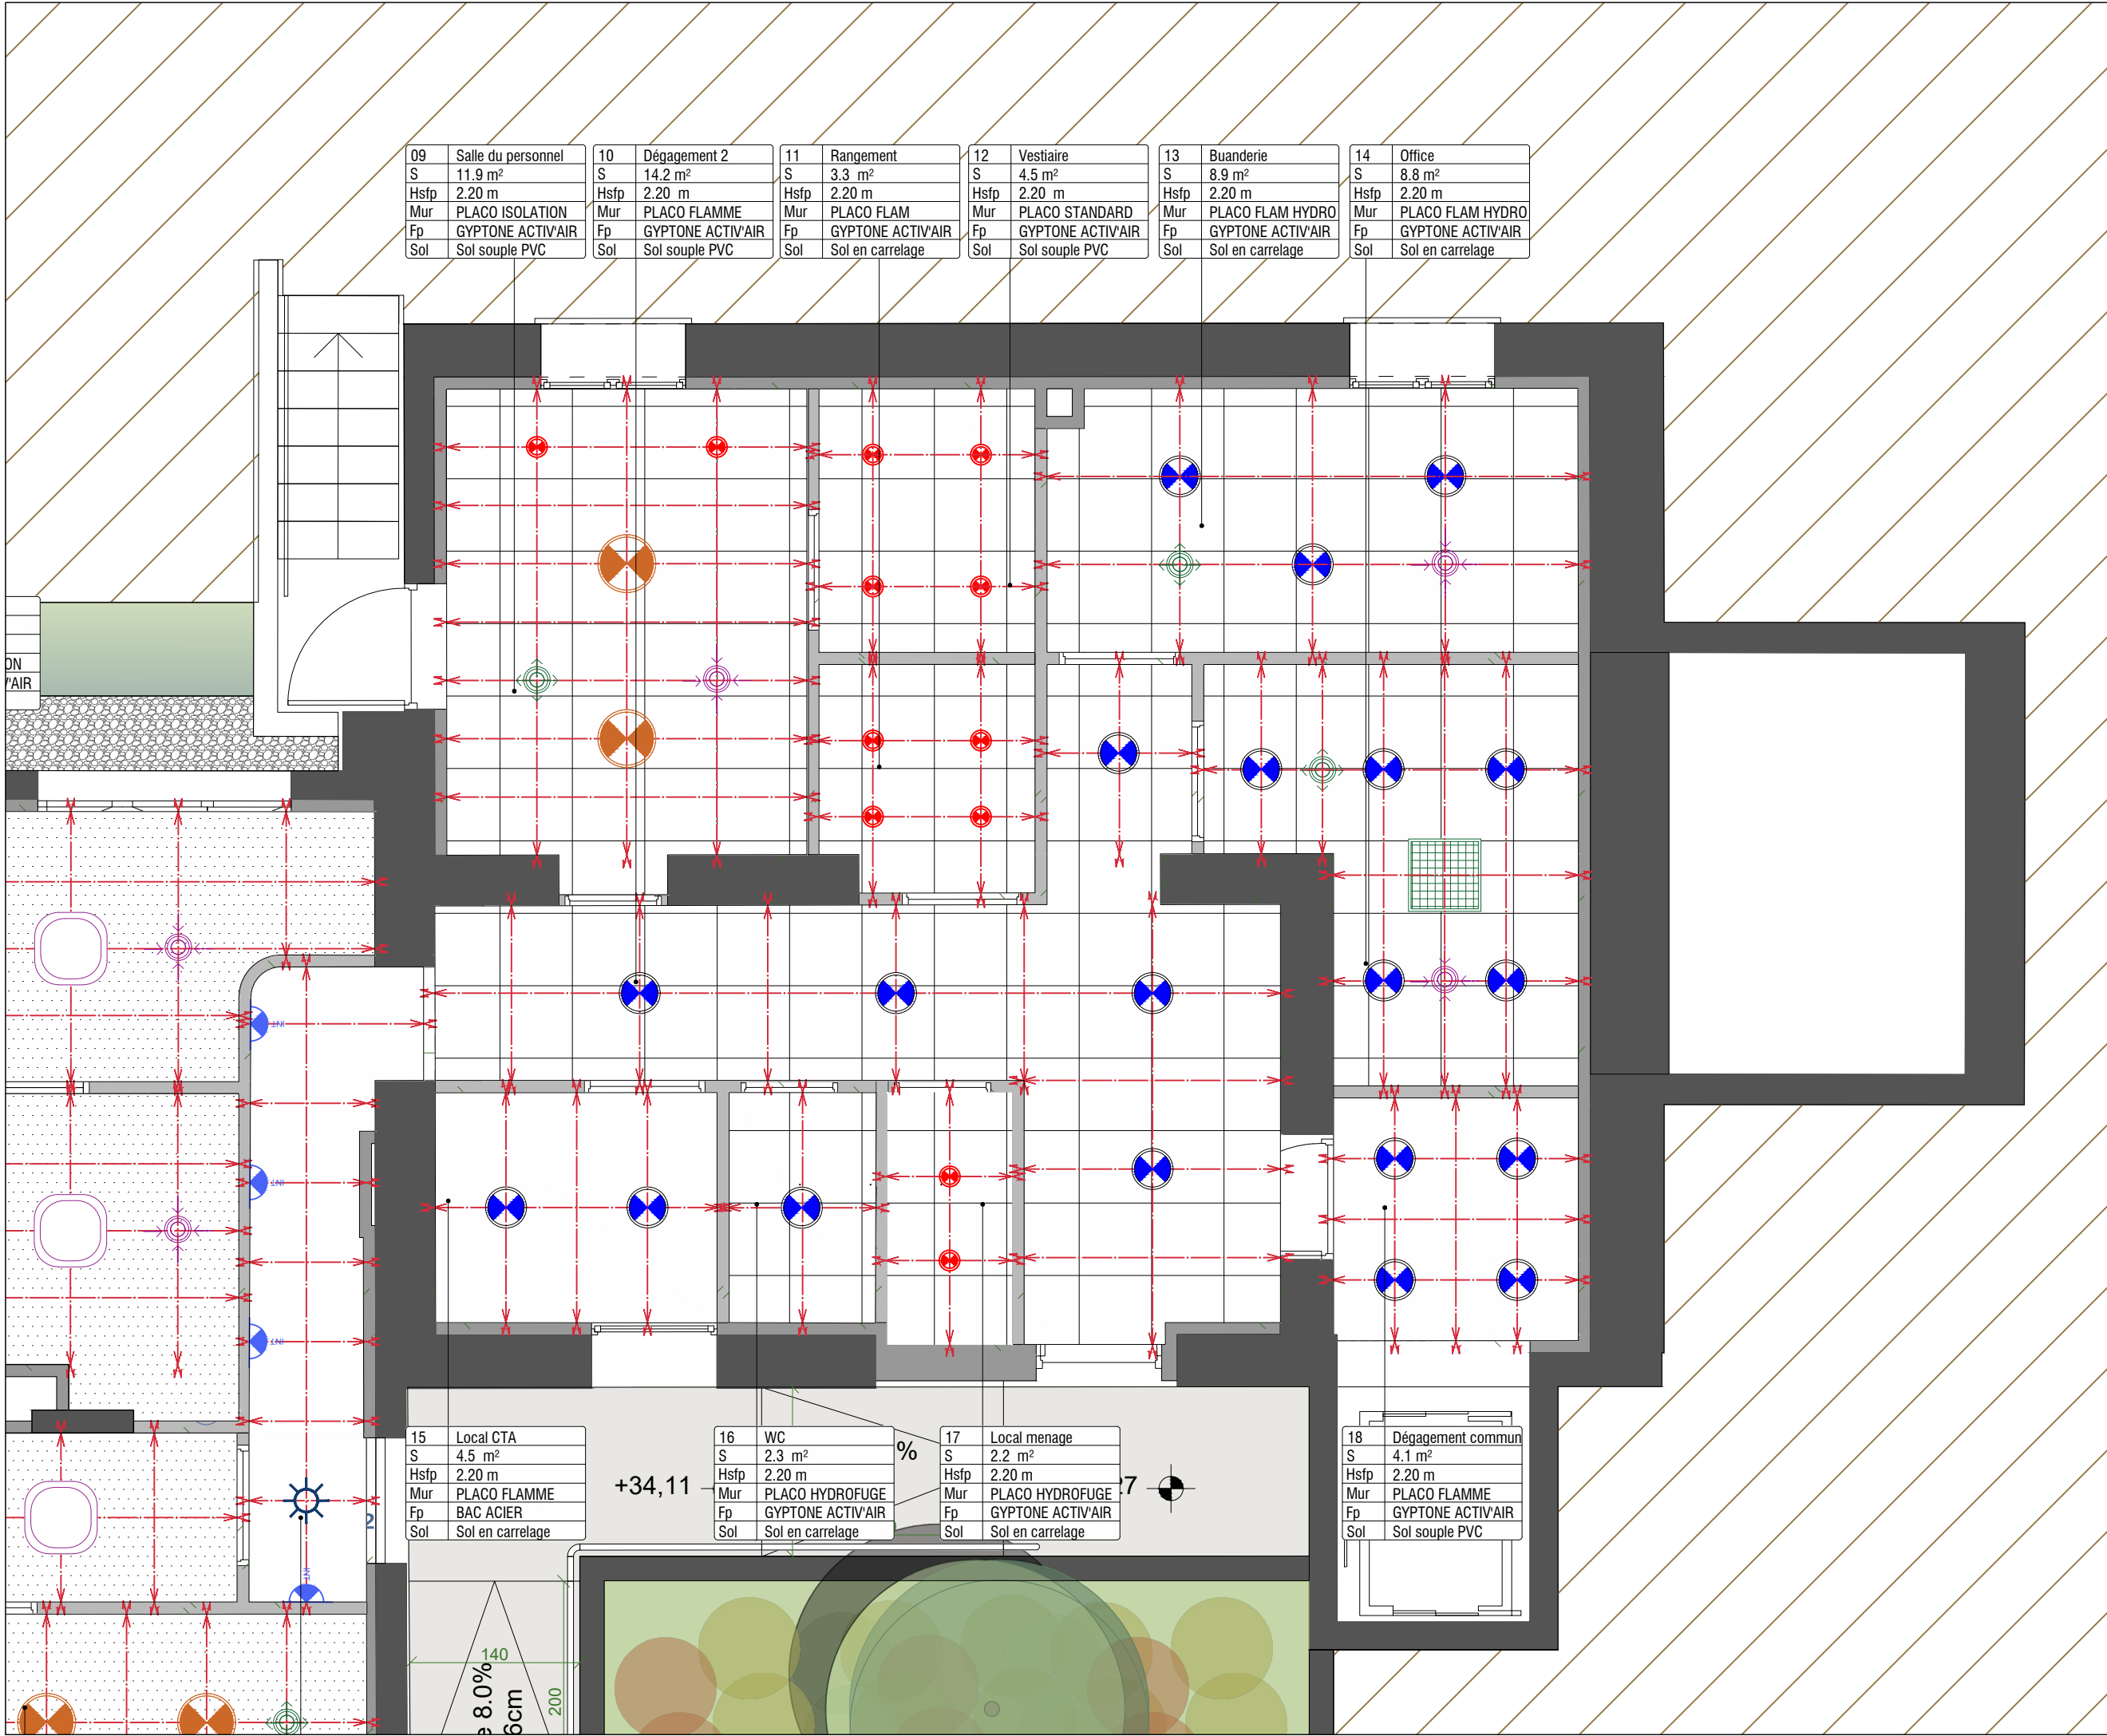

CREATION D'UN MULTI-ACCUEIL
ET D'UNE MAISON MEDICALE
78400 CHATOU

MOA

SARL LPC YVELINES
15 Rue de l'Orient78000 VERSAILLES

MOE

NAHK ARCHITECTURE
24 Rue Yves Toudic, 75010 Paris

NOM DU DOCUMENT

REVETEMENT
FAUX PLAFOND
SECTEUR 3

PHASE

PRO.DCE

ECH.

1/50

INDICE

1.1

DATE

30/06/2023

MODIFICATIONS
INDICE DATE OBJET

1.1

30/06/2023


Diffusion initiale

FAUX PLAFOND

• GYPTONE ACTIV' AIR
BASE 31 E 24- 60 x 60 cm

• RIGITONE ACTIV' AIR
8-15 /20

• BAC ACIER

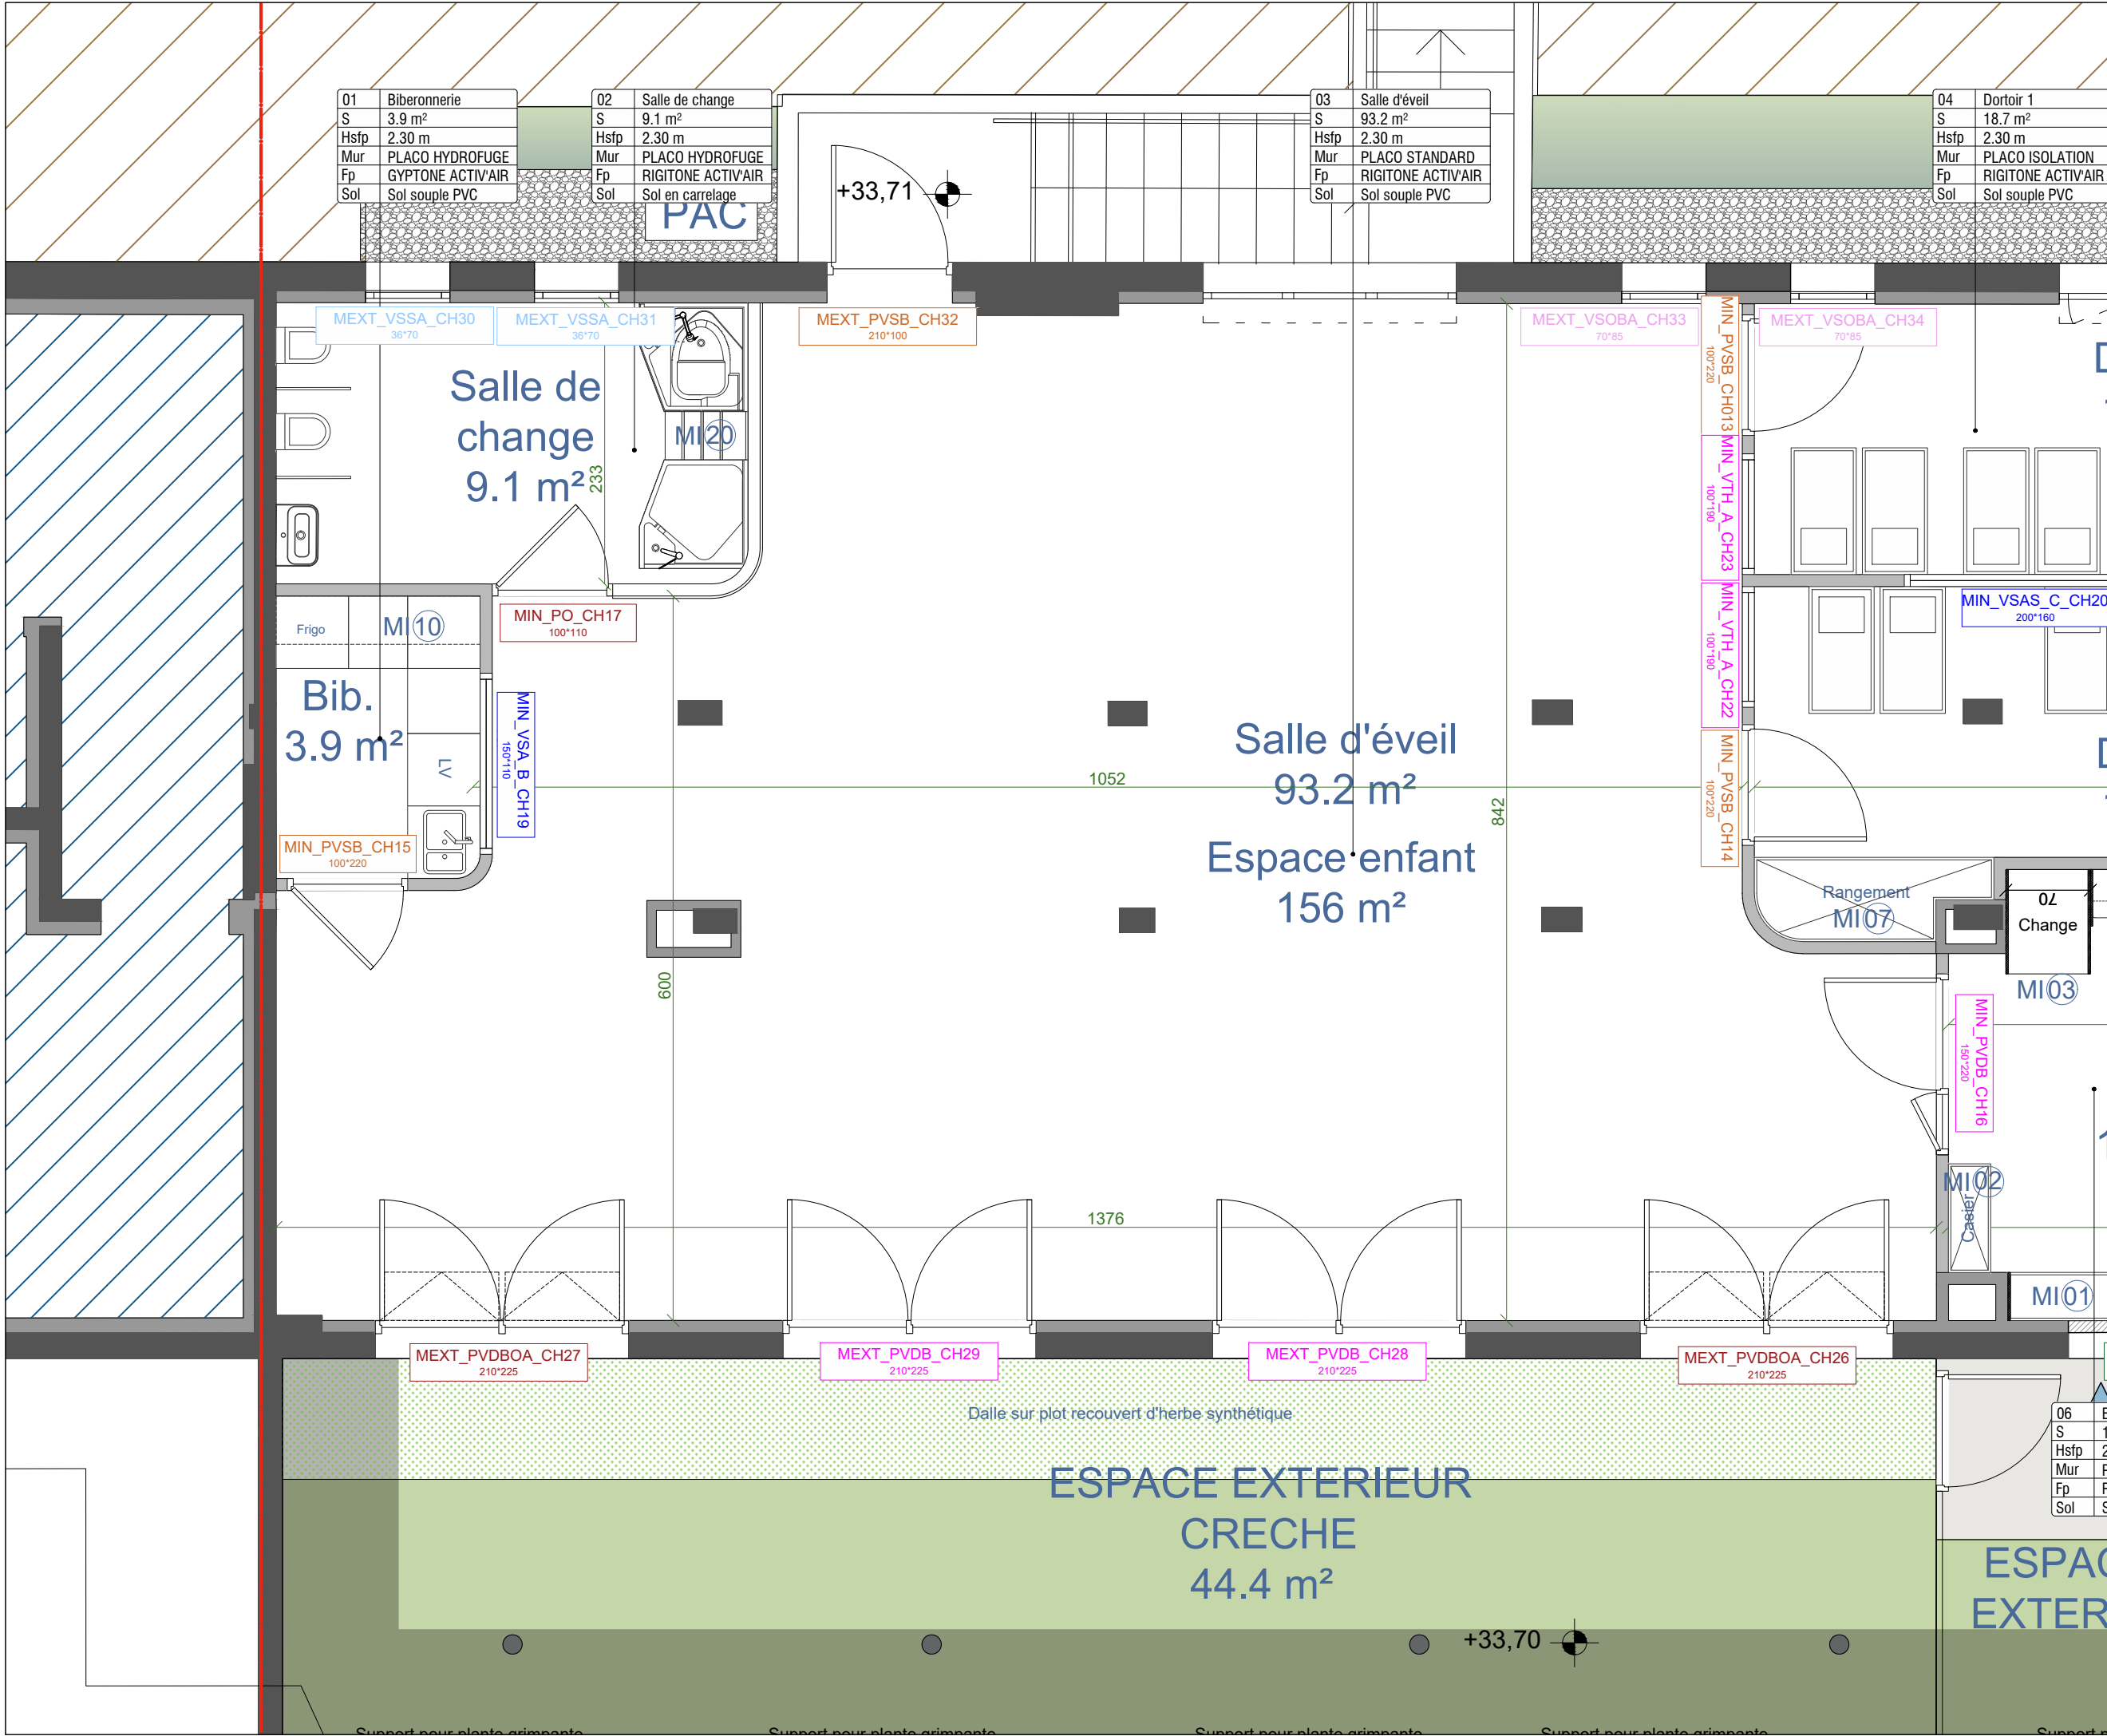

CREATION D'UN MULTI-ACCUEIL ET D'UNE MAISON MEDICALE 78400 CHATOU			
MOA	SARL LPC YVELINES 15 Rue de l'Orient78000 VERSAILLES		
MOE	NAHK ARCHITECTURE 24 Rue Yves Toudic, 75010 Paris		
NOM DU DOCUMENT			
MENUISERIE SECTEUR 1			
PHASE	PRO.DCE	ECH.	1/50
INDICE	1.1	DATE	30/06/2023
MODIFICATIONS			
INDICE DATE OBJET			
1.1	30/06/2023	Diffusion initiale	

05	Dortoir 2
S	19.1 m ²
Hsfp	2.30 m
Mur	PLACO ISOLATION
Fp	RIGITONE ACTIV'AIR
Sol	Sol souple PVC

CREATION D'UN MULTI-ACCUEIL
ET D'UNE MAISON MEDICALE
78400 CHATOU

NOM DU DOCUMENT

PHASE	PRO.DCE	ECH.	1/50
INDICE	1.1	DATE	30/06/2023

1.1	30/06/2023	Diffusion initiale
-----	------------	--------------------

WC
2.3 m²


Dg
5.8

+33,95 — 

16	WC
S	2.3 m ²
Hsfp	2.20 m
Mur	PLACO HYD
Fp	GYPTONE A
Sol	Sol en carre

08	Dégagement 1
S	1.4 m ²
Hsfp	+2.52 m / -1.95 m
Mur	PLACO ISOLATION
Fp	NEANT
Sol	Sol souple PVC

CE EXTERIEUR
CRECHE
44.4 m²

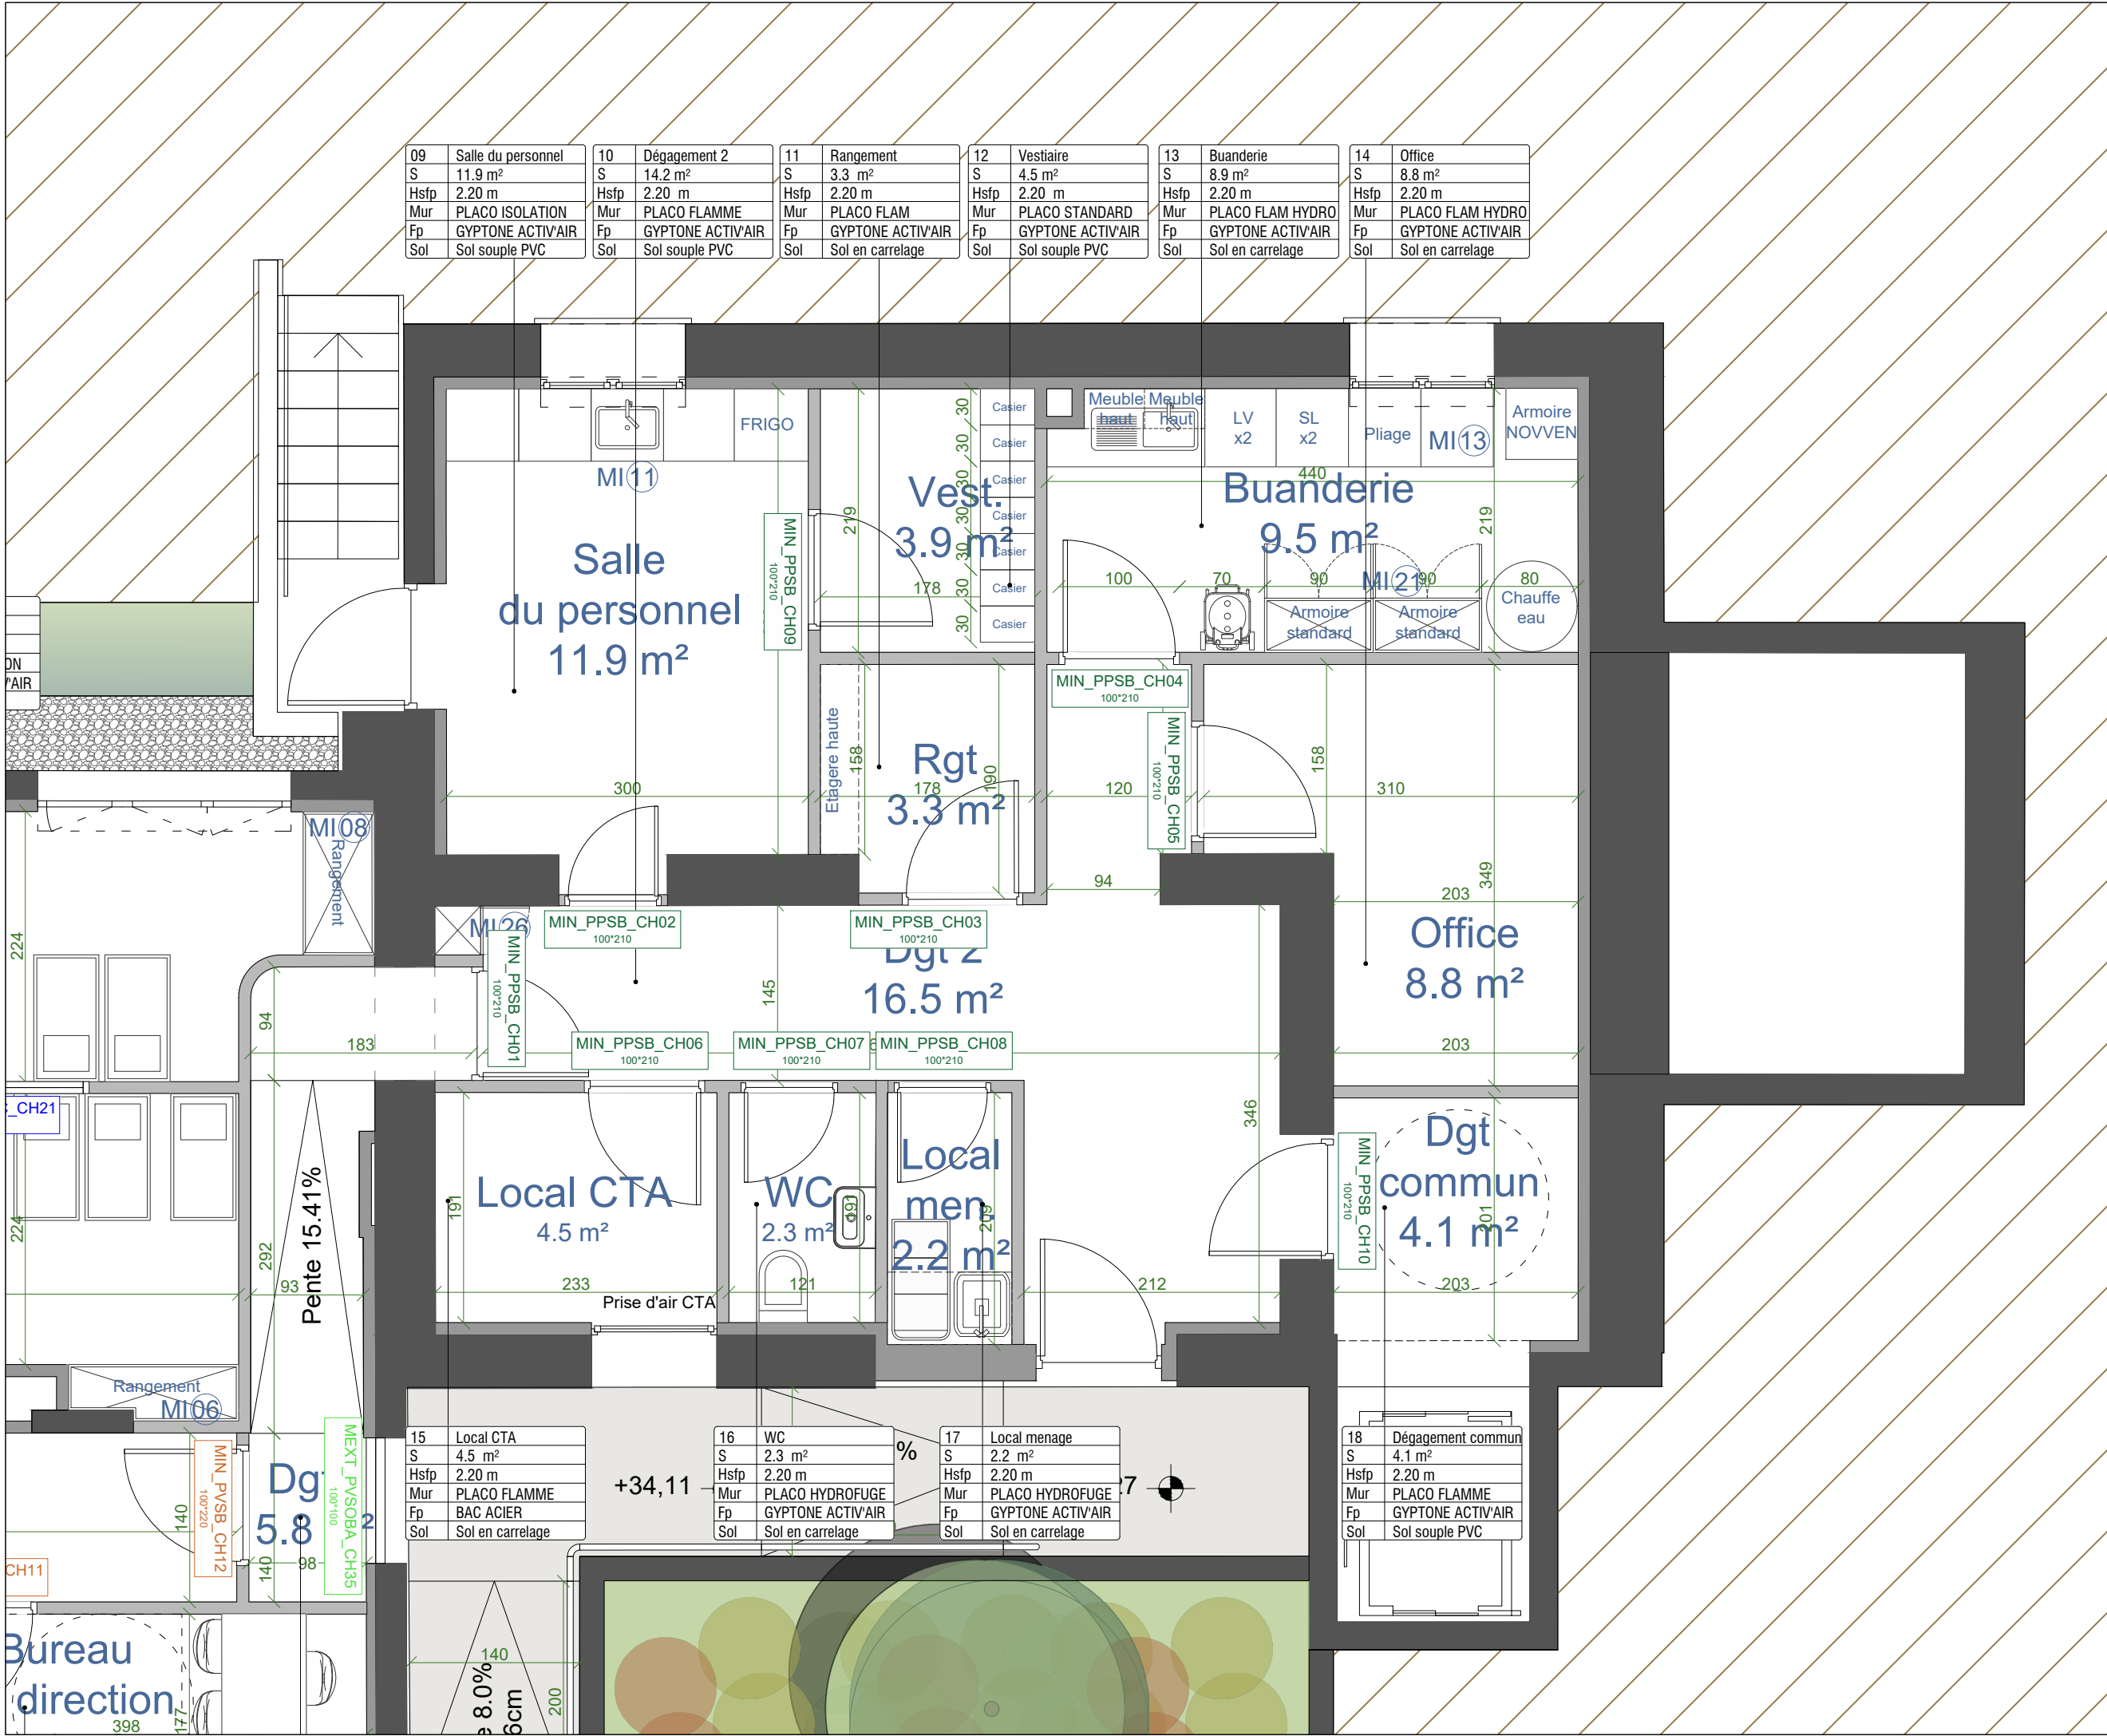

CREATION D'UN MULTI-ACCUEIL ET D'UNE MAISON MEDICALE 78400 CHATOU			
MOA	SARL LPC YVELINES 15 Rue de l'Orient78000 VERSAILLES		
MOE	NAHK ARCHITECTURE 24 Rue Yves Toudic, 75010 Paris		
NOM DU DOCUMENT			
MENUISERIE SECTEUR 3			
PHASE	PRO.DCE	ECH.	1/50
INDICE	1.1	DATE	30/06/2023
MODIFICATIONS			
INDICE DATE OBJET			
1.1	30/06/2023	Diffusion initiale	


PSB. Simple battant Dimensions : 100 x 210cm Quantité : 3 Battants : <i>Simple à âme pleine</i> Localisation : Buanderie, Local ménage,WC, Salle du personnel, Local CTA, Dégagement 2, Dégagement 3, commun, Rangement. Remarques : serrure, ferme porte intégré, anti-pince doigts, H poignée 130cm	MIN_PPSB. Simple battant Dimensions : 80 x 210cm Quantité : 3 Battants : <i>Simple à âme pleine</i> Localisation : Dégagement 2, Remarques : serrure, serrure à code pour la salle du personnel (CH02), ferme porte intégré, anti-pince doigts, H poignée 130cm	MIN_PVSB. Simple battant vitré Dimensions : 100 x 220cm Quantité : 5 Battants : <i>Simple battant vitré</i> Localisation : Dortoirs 1 et 2, biberonnerie, bureau de direction, entrée Remarques : Vitrée, serrure, ferme porte intégré, anti-pince doigts, H poignée 130cm, bouton moleté côté intérieur des dortoirs (CH10 et CH12)	MIN_PVDB. Double battant vitrée Dimensions : 160 x 220cm Quantité : 1 Battants : <i>Double - 90cm (à oculus) + 50cm (à oculus)</i> Localisation : Accueil Remarques : serrure, ferme porte intégré, anti-pince doigts, H poignée 130cm	MIN_PO. Portillon Dimensions : 100x 110 cm Quantité : 1 Battants: <i>Simple à âme pleine.</i> Localisation : Salle de change Remarques : serrure
PPSB_CH01 100*210 MIN_PPSB_CH03 100*210 PPSB_CH04 100*210 MIN_PPSB_CH05 100*210 PPSB_CH06 100*210 MIN_PPSB_CH09 100*210 PPSB_CH10 100*210	MIN_PPSB_CH02 100*210 MIN_PPSB_CH07 100*210 MIN_PPSB_CH08 100*210	MIN_PVSB_CH11 100*220 MIN_PVSB_CH12 100*220 MIN_PVSB_CH13 100*220 MIN_PVSB_CH14 100*220 MIN_PVSB_CH15 100*220	MIN_PVDB_CH16 160*220	MIN_PO_CH17 100*110
Vue en plan : Élévation : 	Vue en plan : Élévation : 	Vue en plan : Élévation : 	Vue en plan : Élévation : 	Vue en plan : Élévation :
MIN_VSA_A. Vitrage fixe Dimensions : 100x 110 cm Allège=110cm Quantité : 1 Battants : <i>Vitrage fixe</i> Localisation : Bureau de direction Remarques : Vitrage sur allège	MIN_VSA_B. Vitrage fixe Dimensions : 150x 110 cm Allège=110cm Quantité : 1 Battants : <i>Vitrage fixe</i> Localisation : Biberonnerie Remarques : Vitrage sur allège	MIN_VSAS_C. Vitrages fixes Dimensions : 200 x 160cm Quantité : 2 Battants : <i>Vitrage fixe avec partie haute ouvrable à soufflet</i> Localisation : Dortoir 1 et dortoir 2 Remarques : Vitrage sur allège	MIN_VTH_A. Vitrages fixes Dimensions : 100x 220cm Quantité : 2 Battants : <i>Vitrage fixe</i> Localisation : Dortoir 1 et 2 Remarques : Vitrage toute hauteur	
MIN_VSA_A_CH18 100*110	MIN_VSA_B_CH19 150*110	MIN_VSAS_C_CH20 200*160 MIN_VSAS_C_CH21 200*160	MIN_VTH_A_CH22 100*190 MIN_VTH_A_CH23 100*190	
Vue en plan : Élévation : 	Vue en plan : Élévation : 	Vue en plan : Élévation : 	Vue en plan : Élévation : 	

CREATION D'UN MULTI-ACCUEIL ET D'UNE MAISON MEDICALE 78400 CHATOU			
MOA	SARL LPC YVELINES 15 Rue de l'Orient78000 VERSAILLES		
MOE	NAHK ARCHITECTURE 24 Rue Yves Toudic, 75010 Paris		
NOM DU DOCUMENT			
TABLEAU DES MENUISERIES INTERIEURES			
PHASE	PRO.DCE	ECH.	1/50
INDICE	1.1	DATE	30/06/2023
MODIFICATIONS			
INDICE DATE		OBJET	
1.1	30/06/2023	Diffusion initiale	


MEXT_VTOBA. Vitrage triple oscillo battant aluminium
Dimensions : 135 x 210 cm
Quantité : 1
Battants : *Triple oscillos battants*
Localisation : Bureau de direction
Remarques :

MEXT_VTOBA_CH24
210*135

Vue en plan :

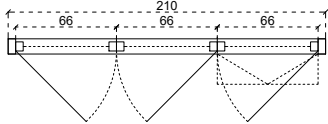


Élévation :

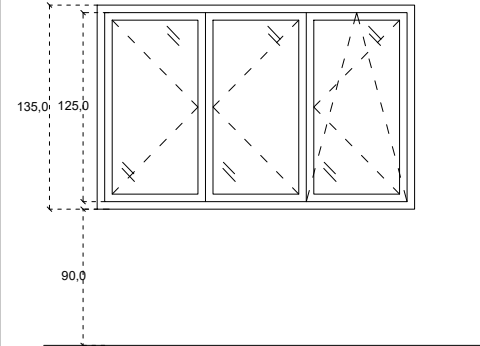


MEXT_PVDB. Porte vitré double battant aluminium
Dimensions : 210 x 225 cm
Quantité : 1
Battants : *Double - 90cm (à oculus) + 50cm (à oculus)*
Localisation : Accueil
Remarques : serrure, ferme porte intégré, anti-pince doigts de niveau 2, bâton maréchal, (voir fiche technique)

MEXT_PVDB_CH25
210*225

Vue en plan :

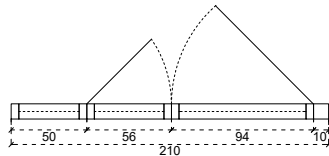

Élévation :

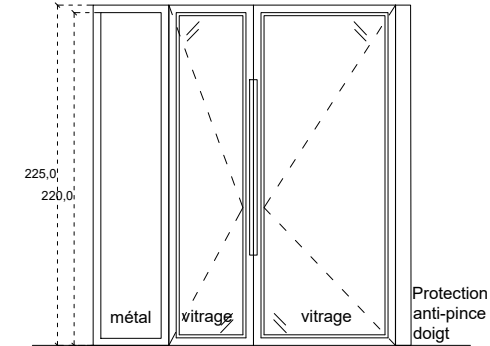


MEXT_PVDBOA. Double battants + oscillo battants sur allège aluminium
Dimensions : 210 x 225 cm *Allège de 95 cm*
Quantité : 2
Battants : *vitrage double battant avec oscillo-battant sur allège vitrée fixe*
Localisation : Salle d'éveil
Remarques : H poignée 130cm (voir fiche technique), serrure, ferme porte intégré, anti-pince doigts de niveau 2.


MEXT_PVDBOA_CH26
210*225

MEXT_PVDBOA_CH27
210*225

Vue en plan :

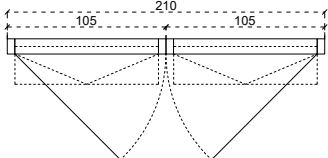

Élévation :

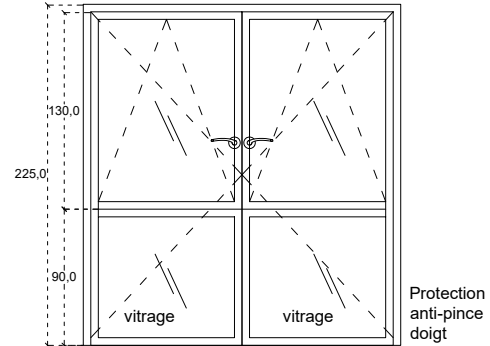


MEXT_PVDB. Double battant aluminium
Dimensions : 210 x 225 cm
Quantité : 2
Battants : *Double battant vitrée*
Localisation : Salle d'éveil
Remarques : serrure, ferme porte intégré, anti-pince doigts de niveau 2, H poignée 130cm (voir fiche technique)


MEXT_PVDB_CH28
210*225

MEXT_PVDB_CH29
210*225

Vue en plan :

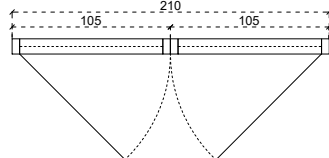

Élévation :

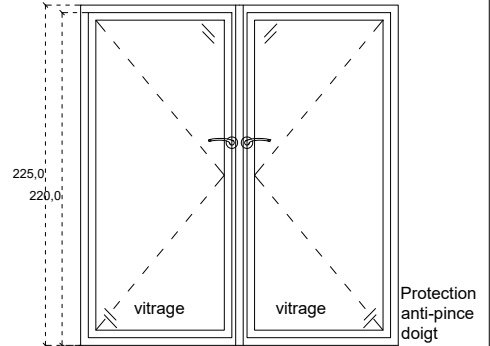


MEXT_VSSA. Vitrage simple à soufflet aluminium
Dimensions : 36 x 70 cm
Quantité : 2
Battants : *vitrage à soufflet*
Localisation : Salle de change
Remarques :


MEXT_VSSA_CH30
36*70

MEXT_VSSA_CH31
36*70

Vue en plan :

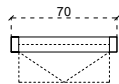


Élévation :

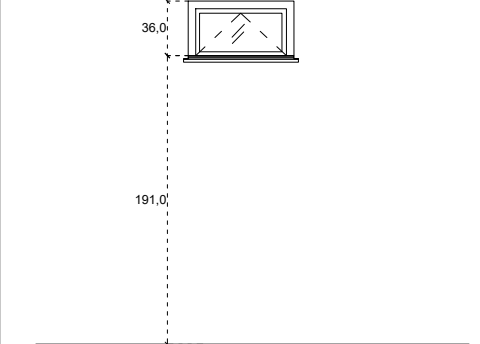


MEXT_PVSB. Porte vitrée à simple battant aluminium
Dimensions : 100 x 210 cm
Quantité : 1
Battants : *Simple battant vitré*
Localisation : Salle d'éveil
Remarques : serrure, ferme porte intégré, anti-pince doigts de niveau 2, H poignée 130cm (voir fiche technique)

MEXT_PVSB_CH32
210*100

Vue en plan :

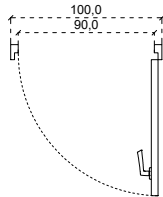

Élévation :

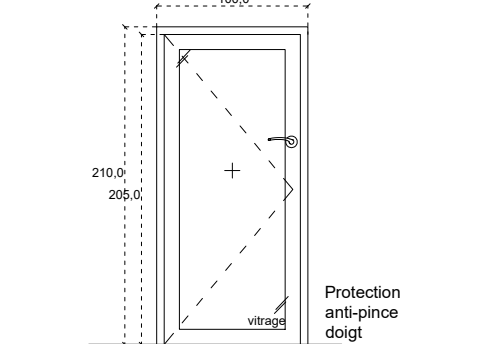


MEXT_VSOBA. Vitrage simple oscillo battant aluminium
Dimensions : 70 x 85 cm
Quantité : 2
Battants : *vitrage oscillo-battant sur allège vitée fixe*
Localisation : Salle d'éveil
Remarques : , H poignée (voir fiche technique)


MEXT_VSOBA_CH33
70*85

MEXT_VSOBA_CH34
70*85

Vue en plan :

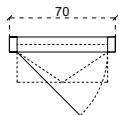


Élévation :

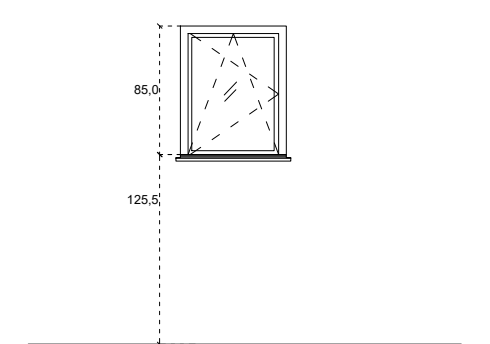


MEXT_VFA. Vitrage Fixe Alluminium
Dimensions : 100 x 100 cm *Allège de 100 cm*
Quantité : 1
Fixe : *vitrage*
Localisation : Dégagement 1
Remarques :

MEXT_VFA_CH35
100*100

Vue en plan :

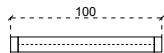

Élévation :

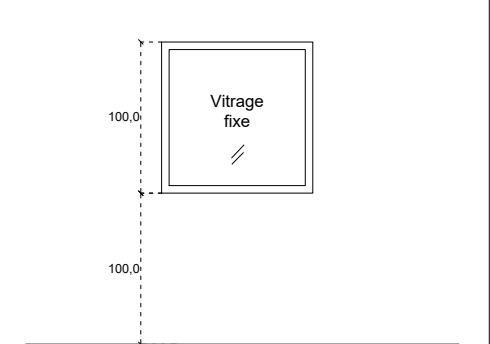

CREATION D'UN MULTI-ACCUEIL
ET D'UNE MAISON MEDICALE
78400 CHATOU

MOA SARL LPC YVELINES
15 Rue de l'Orient78000 VERSAILLES

MOE NAHK ARCHITECTURE
24 Rue Yves Toudic, 75010 Paris

NOM DU DOCUMENT

TABLEAU DES
MENUISERIES EXTERIEURES

PHASE	PRO.DCE	ECH.	1/50
INDICE	1.1	DATE	30/06/2023

MODIFICATIONS
INDICE DATE OBJET

1.1 30/06/2023 Diffusion initiale