

DOS-
SIER
DCE

LOCAL POUSETTE

78 400 CHATOU


MOA : SARL LPC YVELINES

15 Rue de l'Orient 78000 VERSAILLES




Les Petites Canailles


MAITRE D'OEUVRE  NAHK ARCHITECTURE 24 rue Yves Toudic - 75010 PARIS	PHASE	VERSION	DATE	OPÉRATION	MAITRE D'OUVRAGE	N° DOC	NOM DU DOCUMENT	ÉCHELLE
	DCE	01	30/06/2023	CREATION D'UN MULTI ACCUEIL DE 30 BERCEAUX ET REAMENAGEMENT D'UNE MAISON MEDICALE 30 ter Avenue de Brimont 78400 CHATOU	SARL LPC YVELINES 15 Rue de l'Orient78000 VERSAILLES	--		--

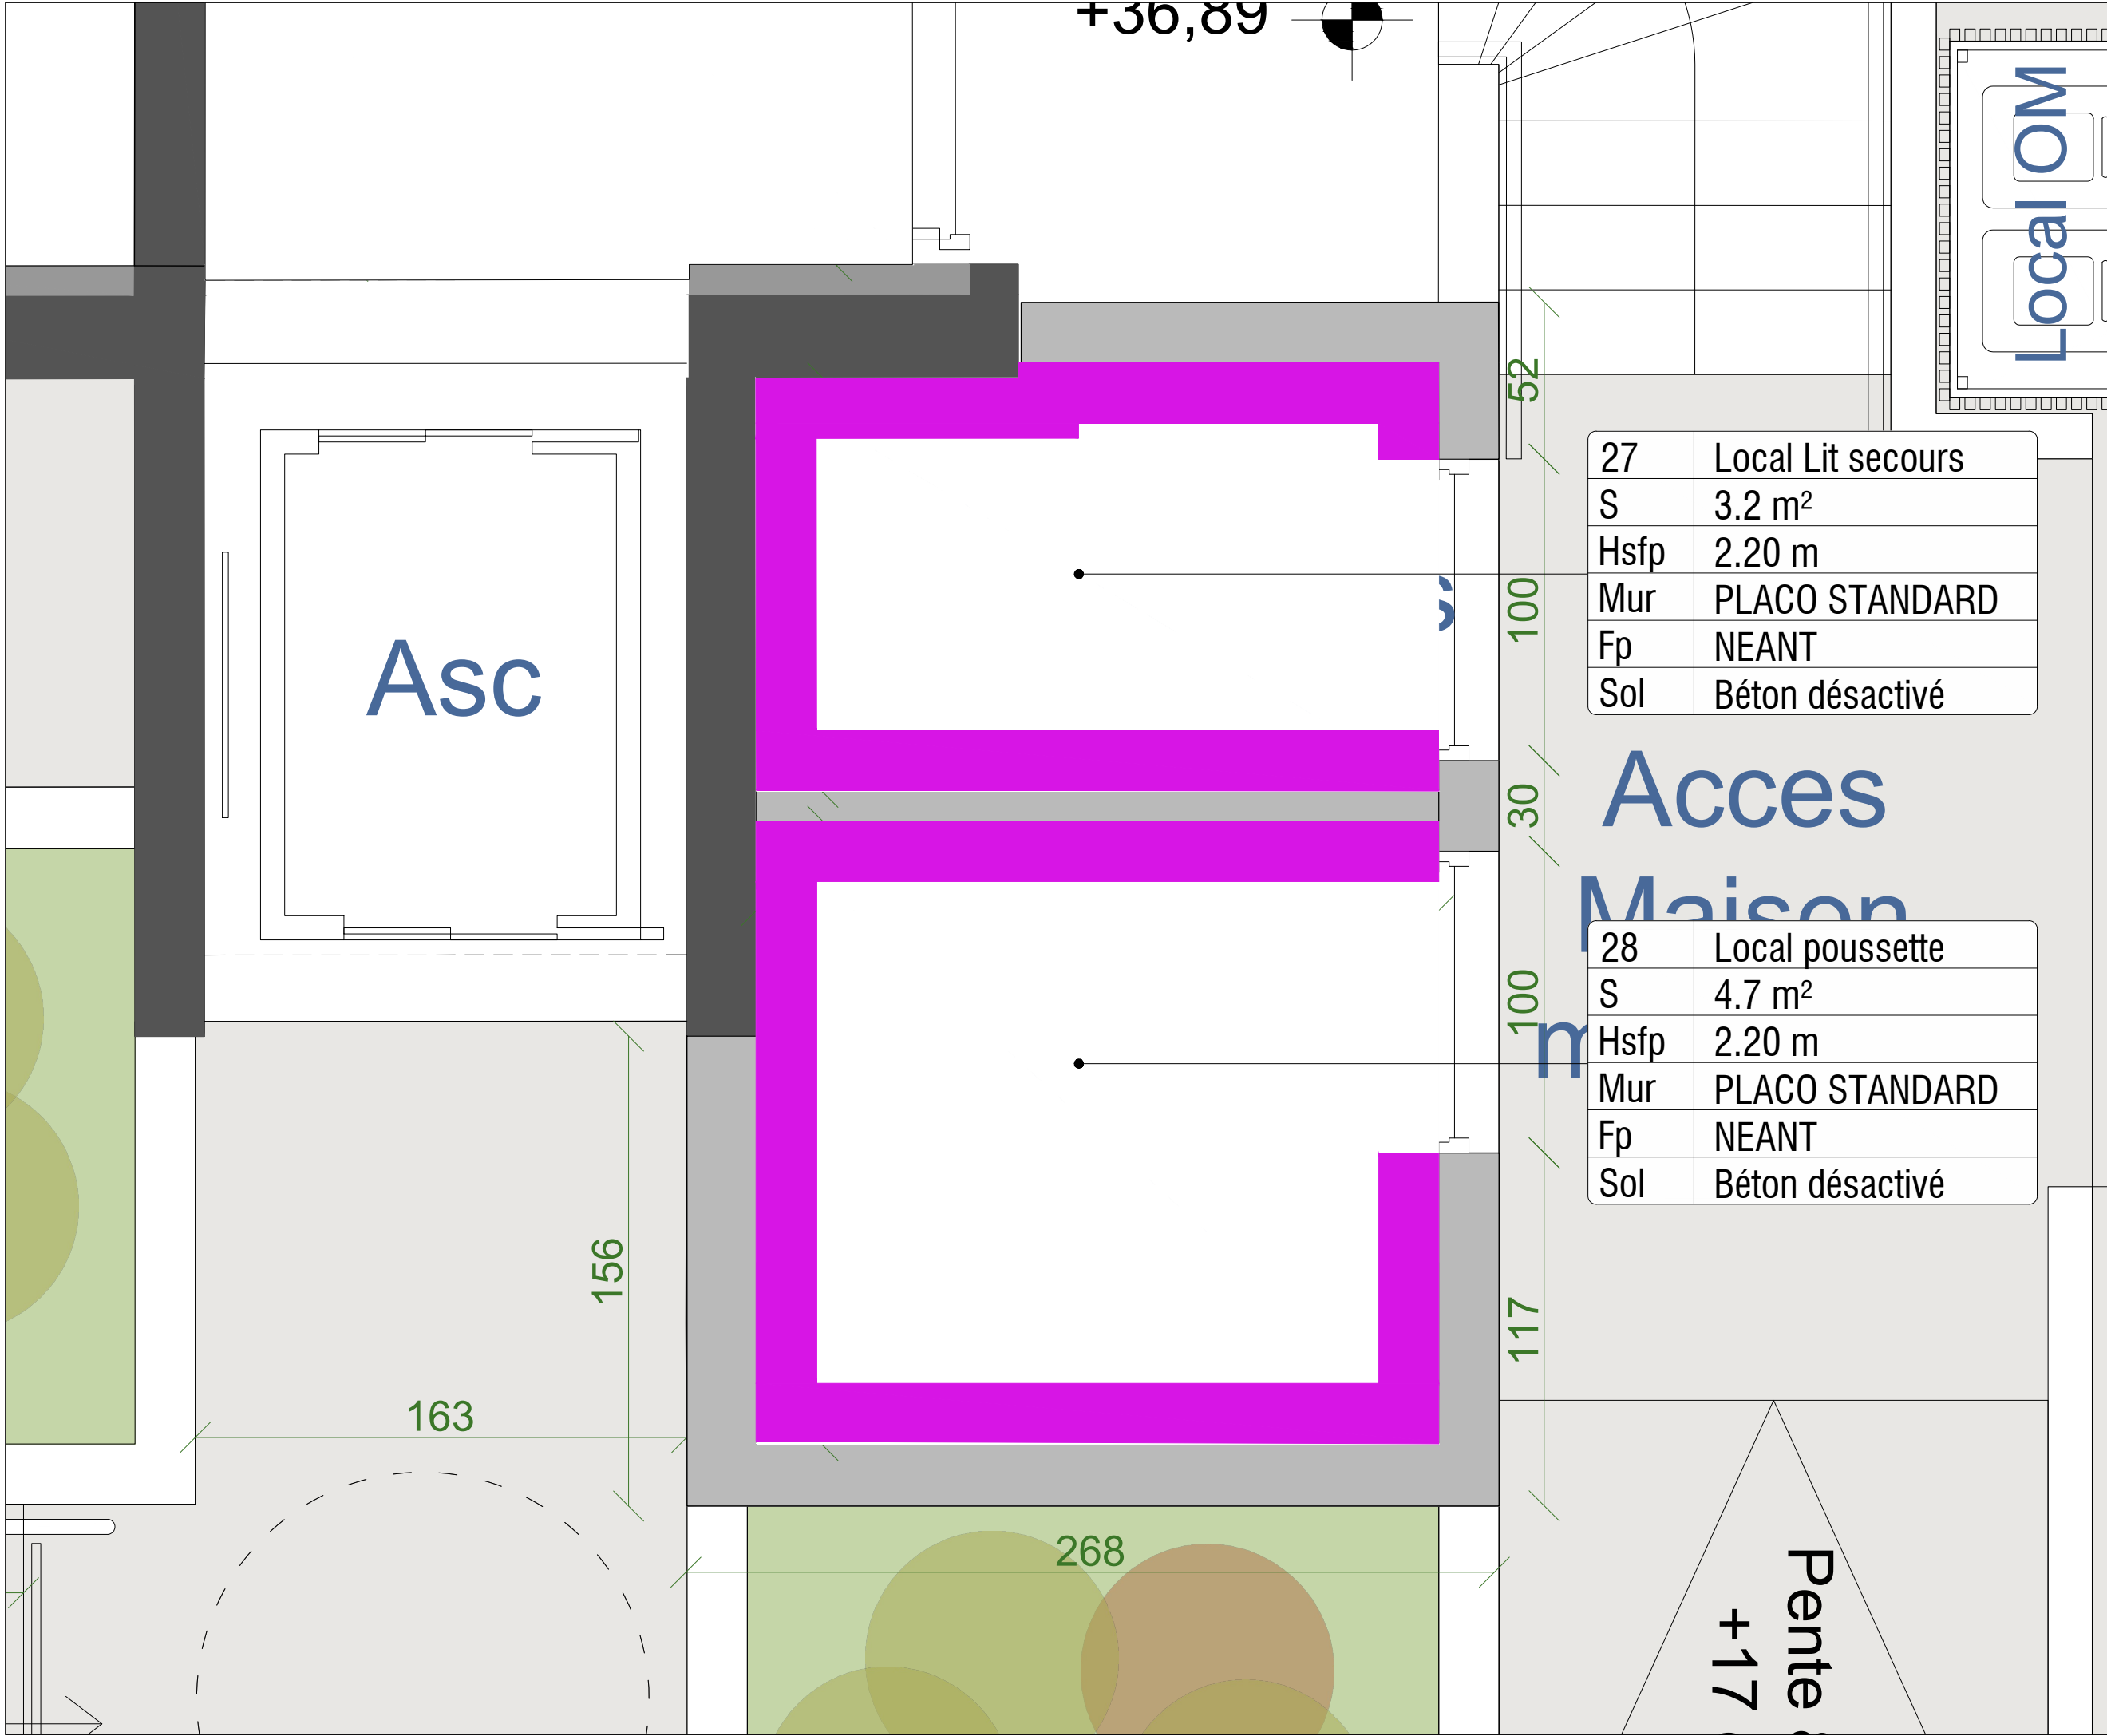

CREATION D'UN MULTI-ACCUEIL ET D'UNE MAISON MEDICALE 78400 CHATOU			
MOA	SARL LPC YVELINES 15 Rue de l'Orient78000 VERSAILLES		
MOE	NAHK ARCHITECTURE 24 Rue Yves Toudic, 75010 Paris		
NOM DU DOCUMENT			
REVETEMENT MURAL LOCAL POUSSETTE			
PHASE	PRO.DCE	ECH.	1/20
INDICE	1.1	DATE	30/06/2023
MODIFICATIONS			
INDICE DATE OBJET			
1.1	30/06/2023	Diffusion initiale	
PROTECTION MURALE • LISSE DE PROTECTION MURALE			

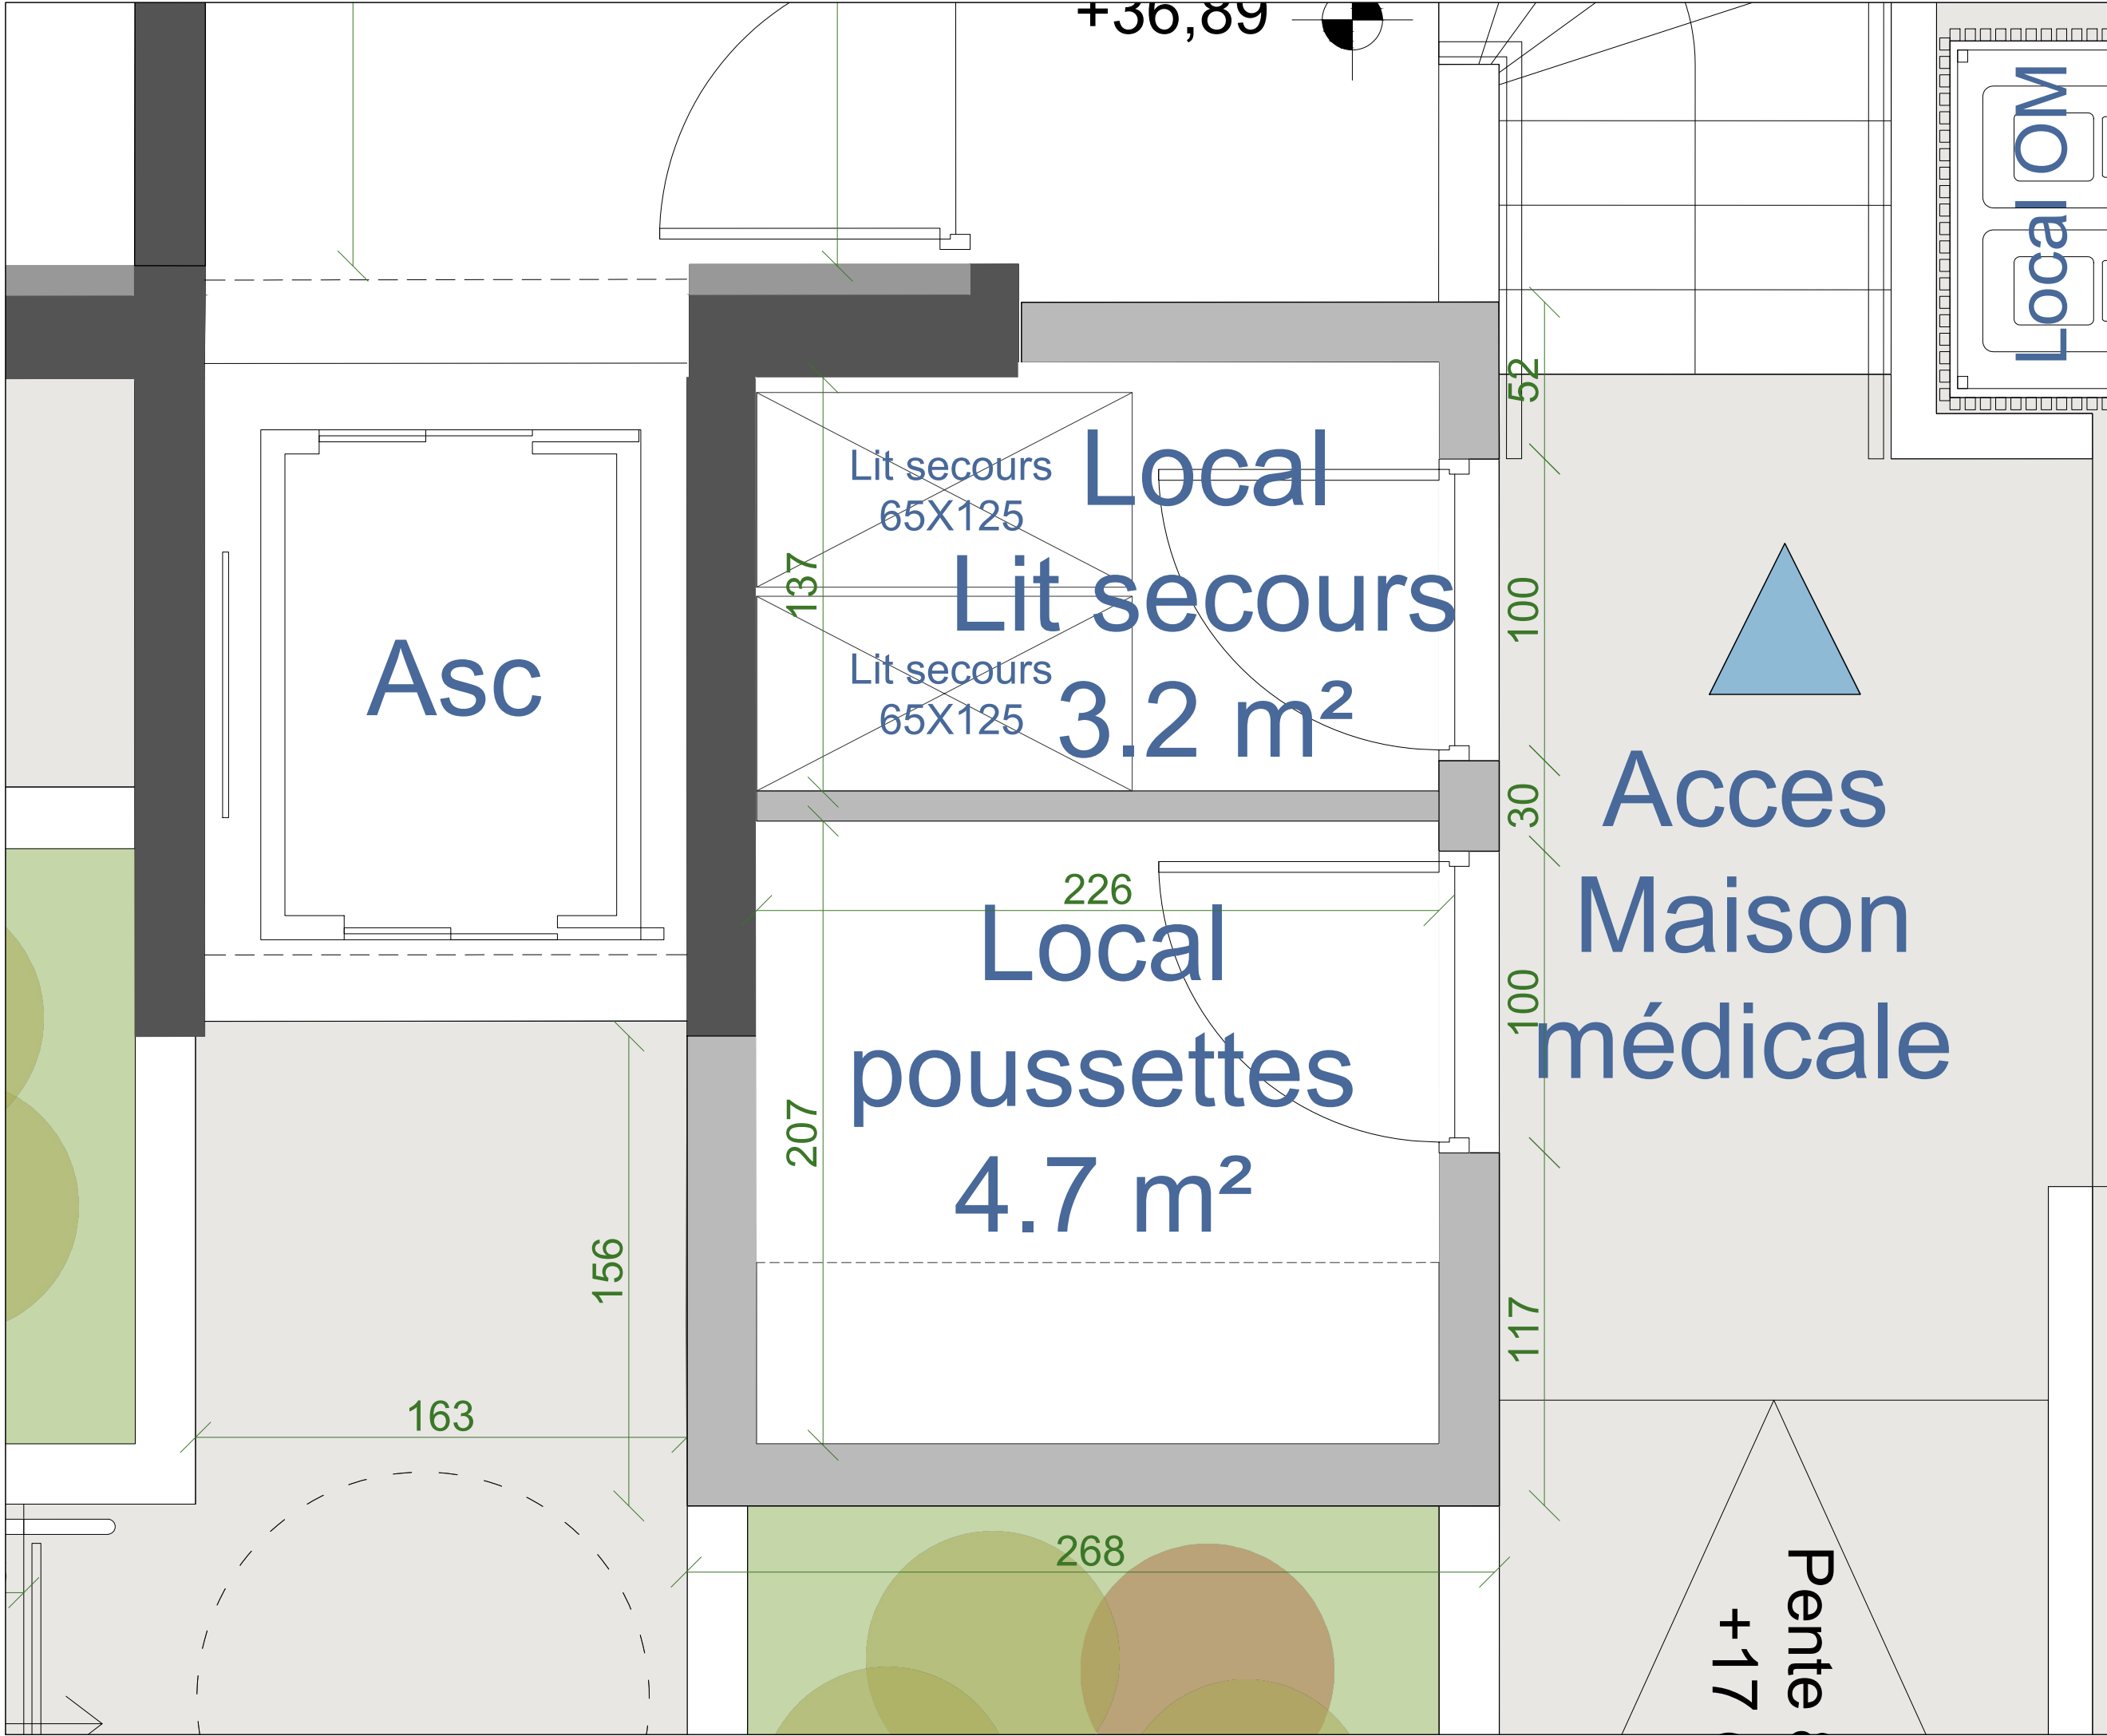

CREATION D'UN MULTI-ACCUEIL ET D'UNE MAISON MEDICALE 78400 CHATOU			
MOA	SARL LPC YVELINES 15 Rue de l'Orient78000 VERSAILLES		
MOE	NAHK ARCHITECTURE 24 Rue Yves Toudic, 75010 Paris		
NOM DU DOCUMENT			
PLAN LOCAL POUSSETTE			
PHASE	PRO.DCE	ECH.	1/50
INDICE	1.1	DATE	30/06/2023
MODIFICATIONS			
INDICE DATE		OBJET	
1.1	30/06/2023	Diffusion initiale	

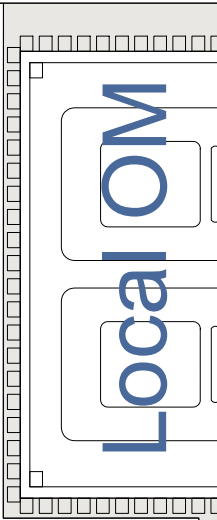



CREATION D'UN MULTI-ACCUEIL ET
D'UNE MAISON MEDICALE
78400 CHATOU

MOA SARL LPC YVELINES
15 Rue de l'Orient78000 VERSAILLES


MOE NAHK ARCHITECTURE
24 Rue Yves Toudic, 75010 Paris

NOM DU DOCUMENT

REVETEMENTS DE SOL
SECTEUR 1

27	Local Lit secours
S	3.2 m²
Hsfp	2.20 m
Mur	PLACO STANDARD
Fp	NEANT
Sol	Béton désactivé

28	Local poussette
S	4.7 m²
Hsfp	2.20 m
Mur	PLACO STANDARD
Fp	NEANT
Sol	Béton désactivé

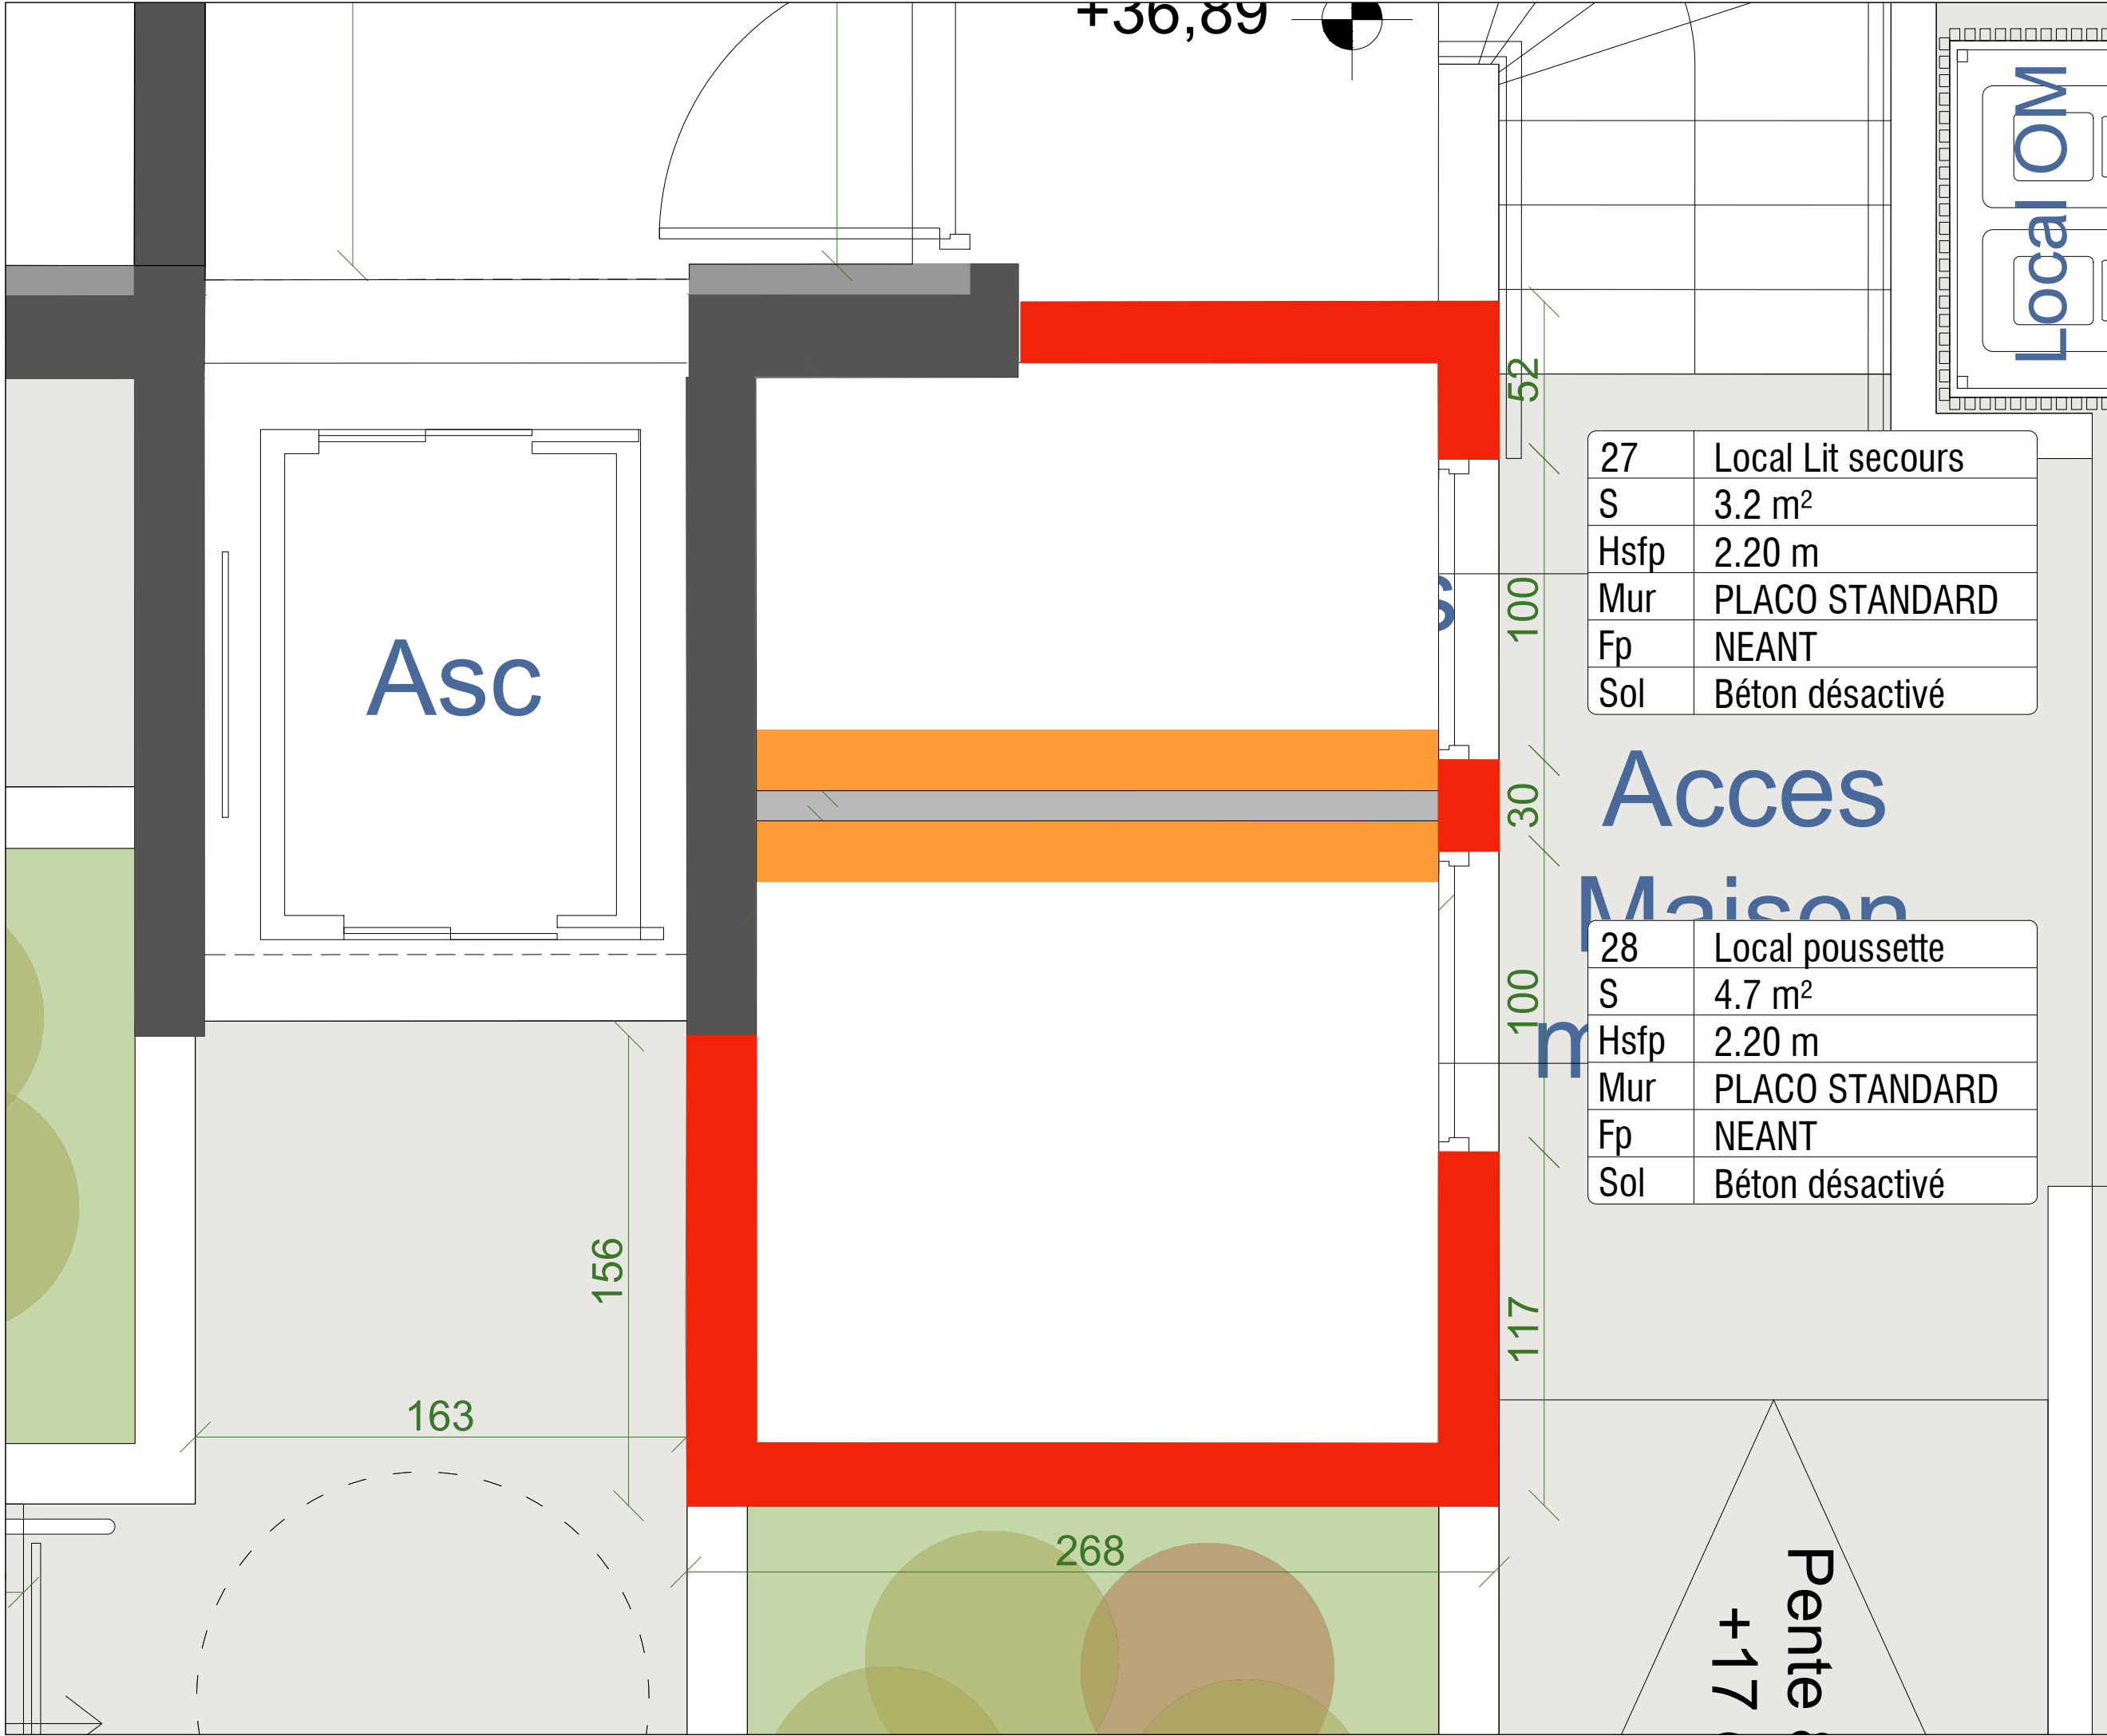

27	Local Lit secours
S	3.2 m²
Hsfp	2.20 m
Mur	PLACO STANDARD
Fp	NEANT
Sol	Béton désactivé

28	Local poussette
S	4.7 m²
Hsfp	2.20 m
Mur	PLACO STANDARD
Fp	NEANT
Sol	Béton désactivé

CREATION D'UN MULTI-ACCUEIL ET D'UNE MAISON MEDICALE
78400 CHATOU

MOA

SARL LPC YVELINES
15 Rue de l'Orient78000 VERSAILLES

MOE

NAHK ARCHITECTURE
24 Rue Yves Toudic, 75010 Paris

NOM DU DOCUMENT

MACONNERIE / CLOISON
LOCAL POUSSETTE

PHASE

PRO.DCE

ECH.

1/50

INDICE

1.1

DATE

30/06/2023

MODIFICATIONS

INDICE

DATE

OBJET

1.1


30/06/2023

Diffusion initiale


DOUBLAGE MURAL

• PLACOSTIL STANDART
CLOISON EP 10 cm

• MUR MACONNE 20 CM

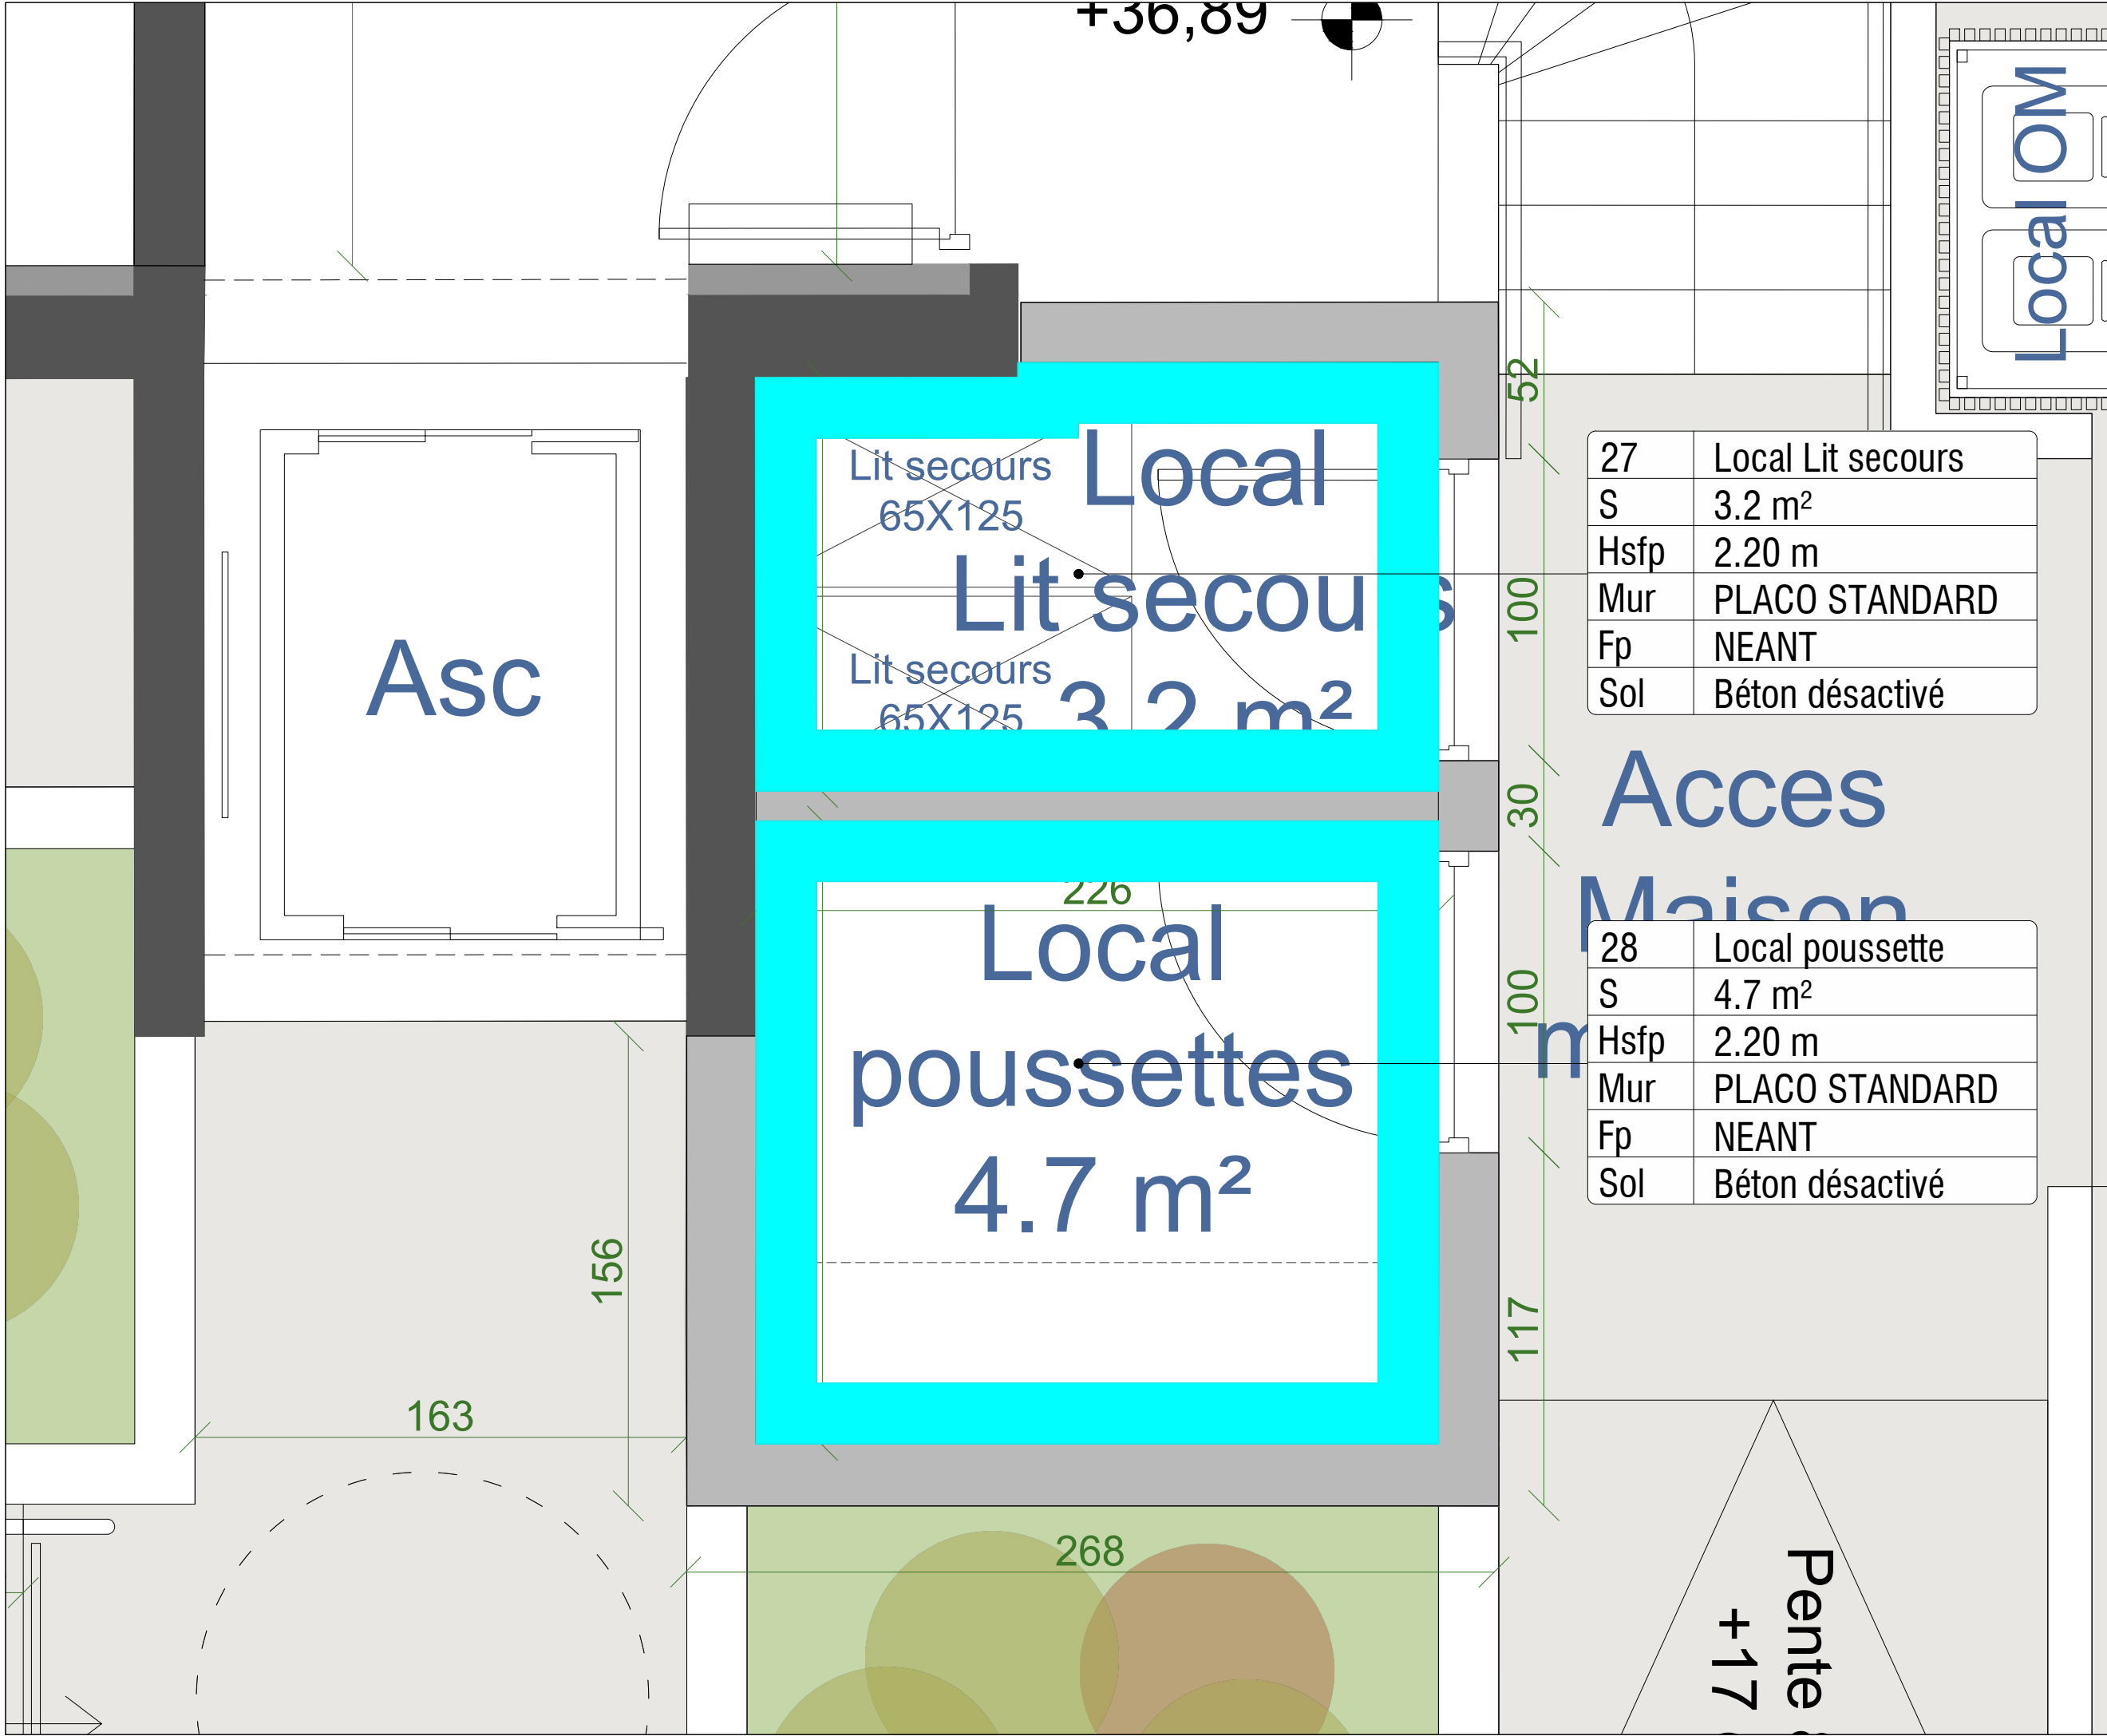

CREATION D'UN MULTI-ACCUEIL ET D'UNE MAISON MEDICALE 78400 CHATOU			
MOA	SARL LPC YVELINES 15 Rue de l'Orient78000 VERSAILLES		
MOE	NAHK ARCHITECTURE 24 Rue Yves Toudic, 75010 Paris		
NOM DU DOCUMENT			
PEINTURE LOCAL POUSSETTE			
PHASE	PRO.DCE	ECH.	1/20
INDICE	1.1	DATE	30/06/2023
MODIFICATIONS			
INDICE DATE OBJET			
1.1	30/06/2023	Diffusion initiale	
PEINTURE • PEINTURE TOUTE HAUTEUR SOIT JUSQU'A 220 cm RAL 9003			

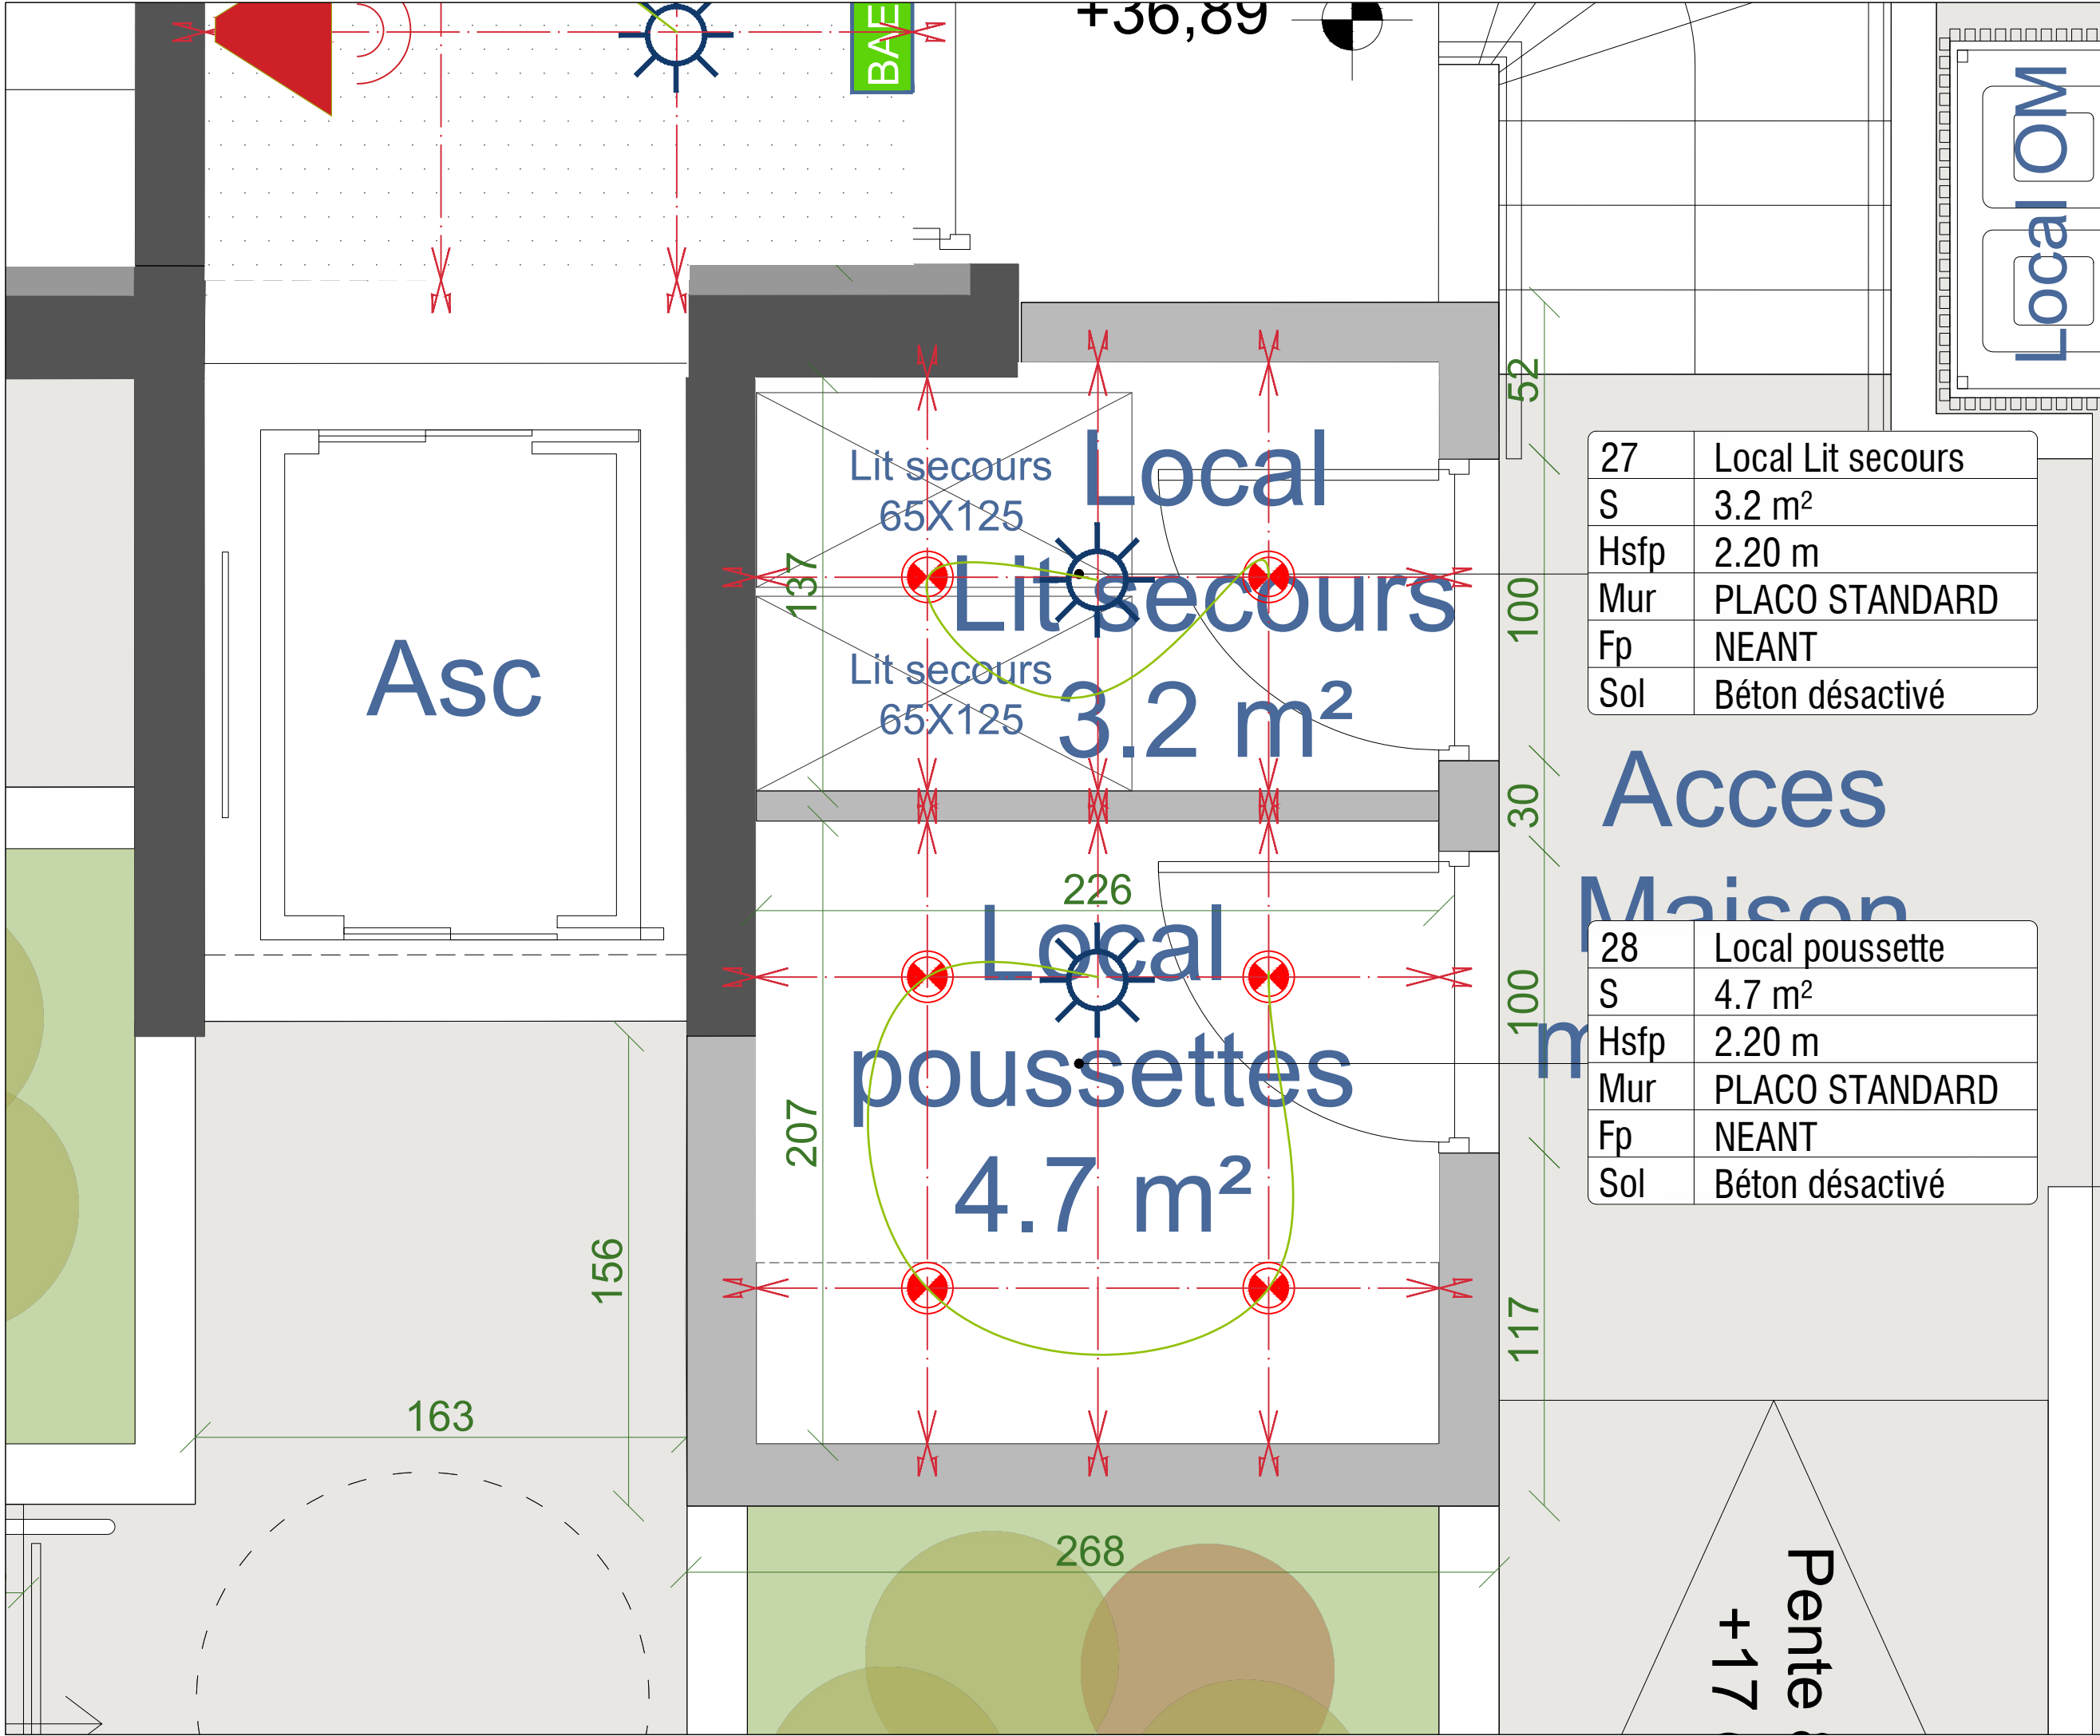

CREATION D'UN MULTI-ACCUEIL ET D'UNE MAISON MEDICALE
78400 CHATOU

MOA

SARL LPC YVELINES
15 Rue de l'Orient78000 VERSAILLES

MOE

NAHK ARCHITECTURE
24 Rue Yves Toudic, 75010 Paris

NOM DU DOCUMENT

ELECTRICITE
SECTEUR 1

PHASE

PRO.DCE

ECH.

1/50

INDICE

1.1

DATE

30/06/2023

MODIFICATIONS
INDICE DATE OBJET

1.1

30/06/2023

Diffusion initiale

ELECTRICITE

• TYPE 1 - PLAFONNIER SLV
MEDO 60 REF. #1000726

• TYPE 1 - DOWNLIGHTS TIGA 3
RD DIAM 240

• TYPE 2 - SPOT IN HOUSE LED
UP007 DIAM 85

• TYPE 3 - DOWNLIGHTS TIGA 1
RD DIAM 170

• TYPE 4 - APPLIQUE MURALE
DELTALIGHT TOPIX WW

• TYPE 5 - REGLETTE MURALE
EXTRA-PLATE

• TYPE 5 - APPLIQUE
SLV QUADRASYL

• INTERRUPTEUR SIMPLE

• INTERRUPTEUR VA-ET-VIENT

• VARIATEUR EN DALI

• DETECTEUR DE PRESENCE
AVEC MINUTERIE

• PRISE ELECTRIQUE
STANDARD H 130 CM DU SOL

• PRISE ETANCHE ENCASTREE
20 CM DU PLAN DE TRAVAIL

• ALIMENTATION APPAREIL

• PRISE RJ45

BAES

• BAES

• CENTRALE D'ALARME INCENDIE

• DIFFUSEUR SONORE

• DIFFUSEUR LUMINEUX

• DECLENCHEUR D'ALARME MANUEL

• DEVEROUILLAGE PORTE

• ARRET D'URGENCE ELECTRICITE
ET VENTILATION

• EXTINCTEUR

• VISIOPHONE AVEC VENTOUSE

• DIGICODE

• SERRURE A CODE

• SONDE DE QUALITE DE L'AIR


• TGBT

CTA

• CTA AU PLAFOND

BE

• BALLON

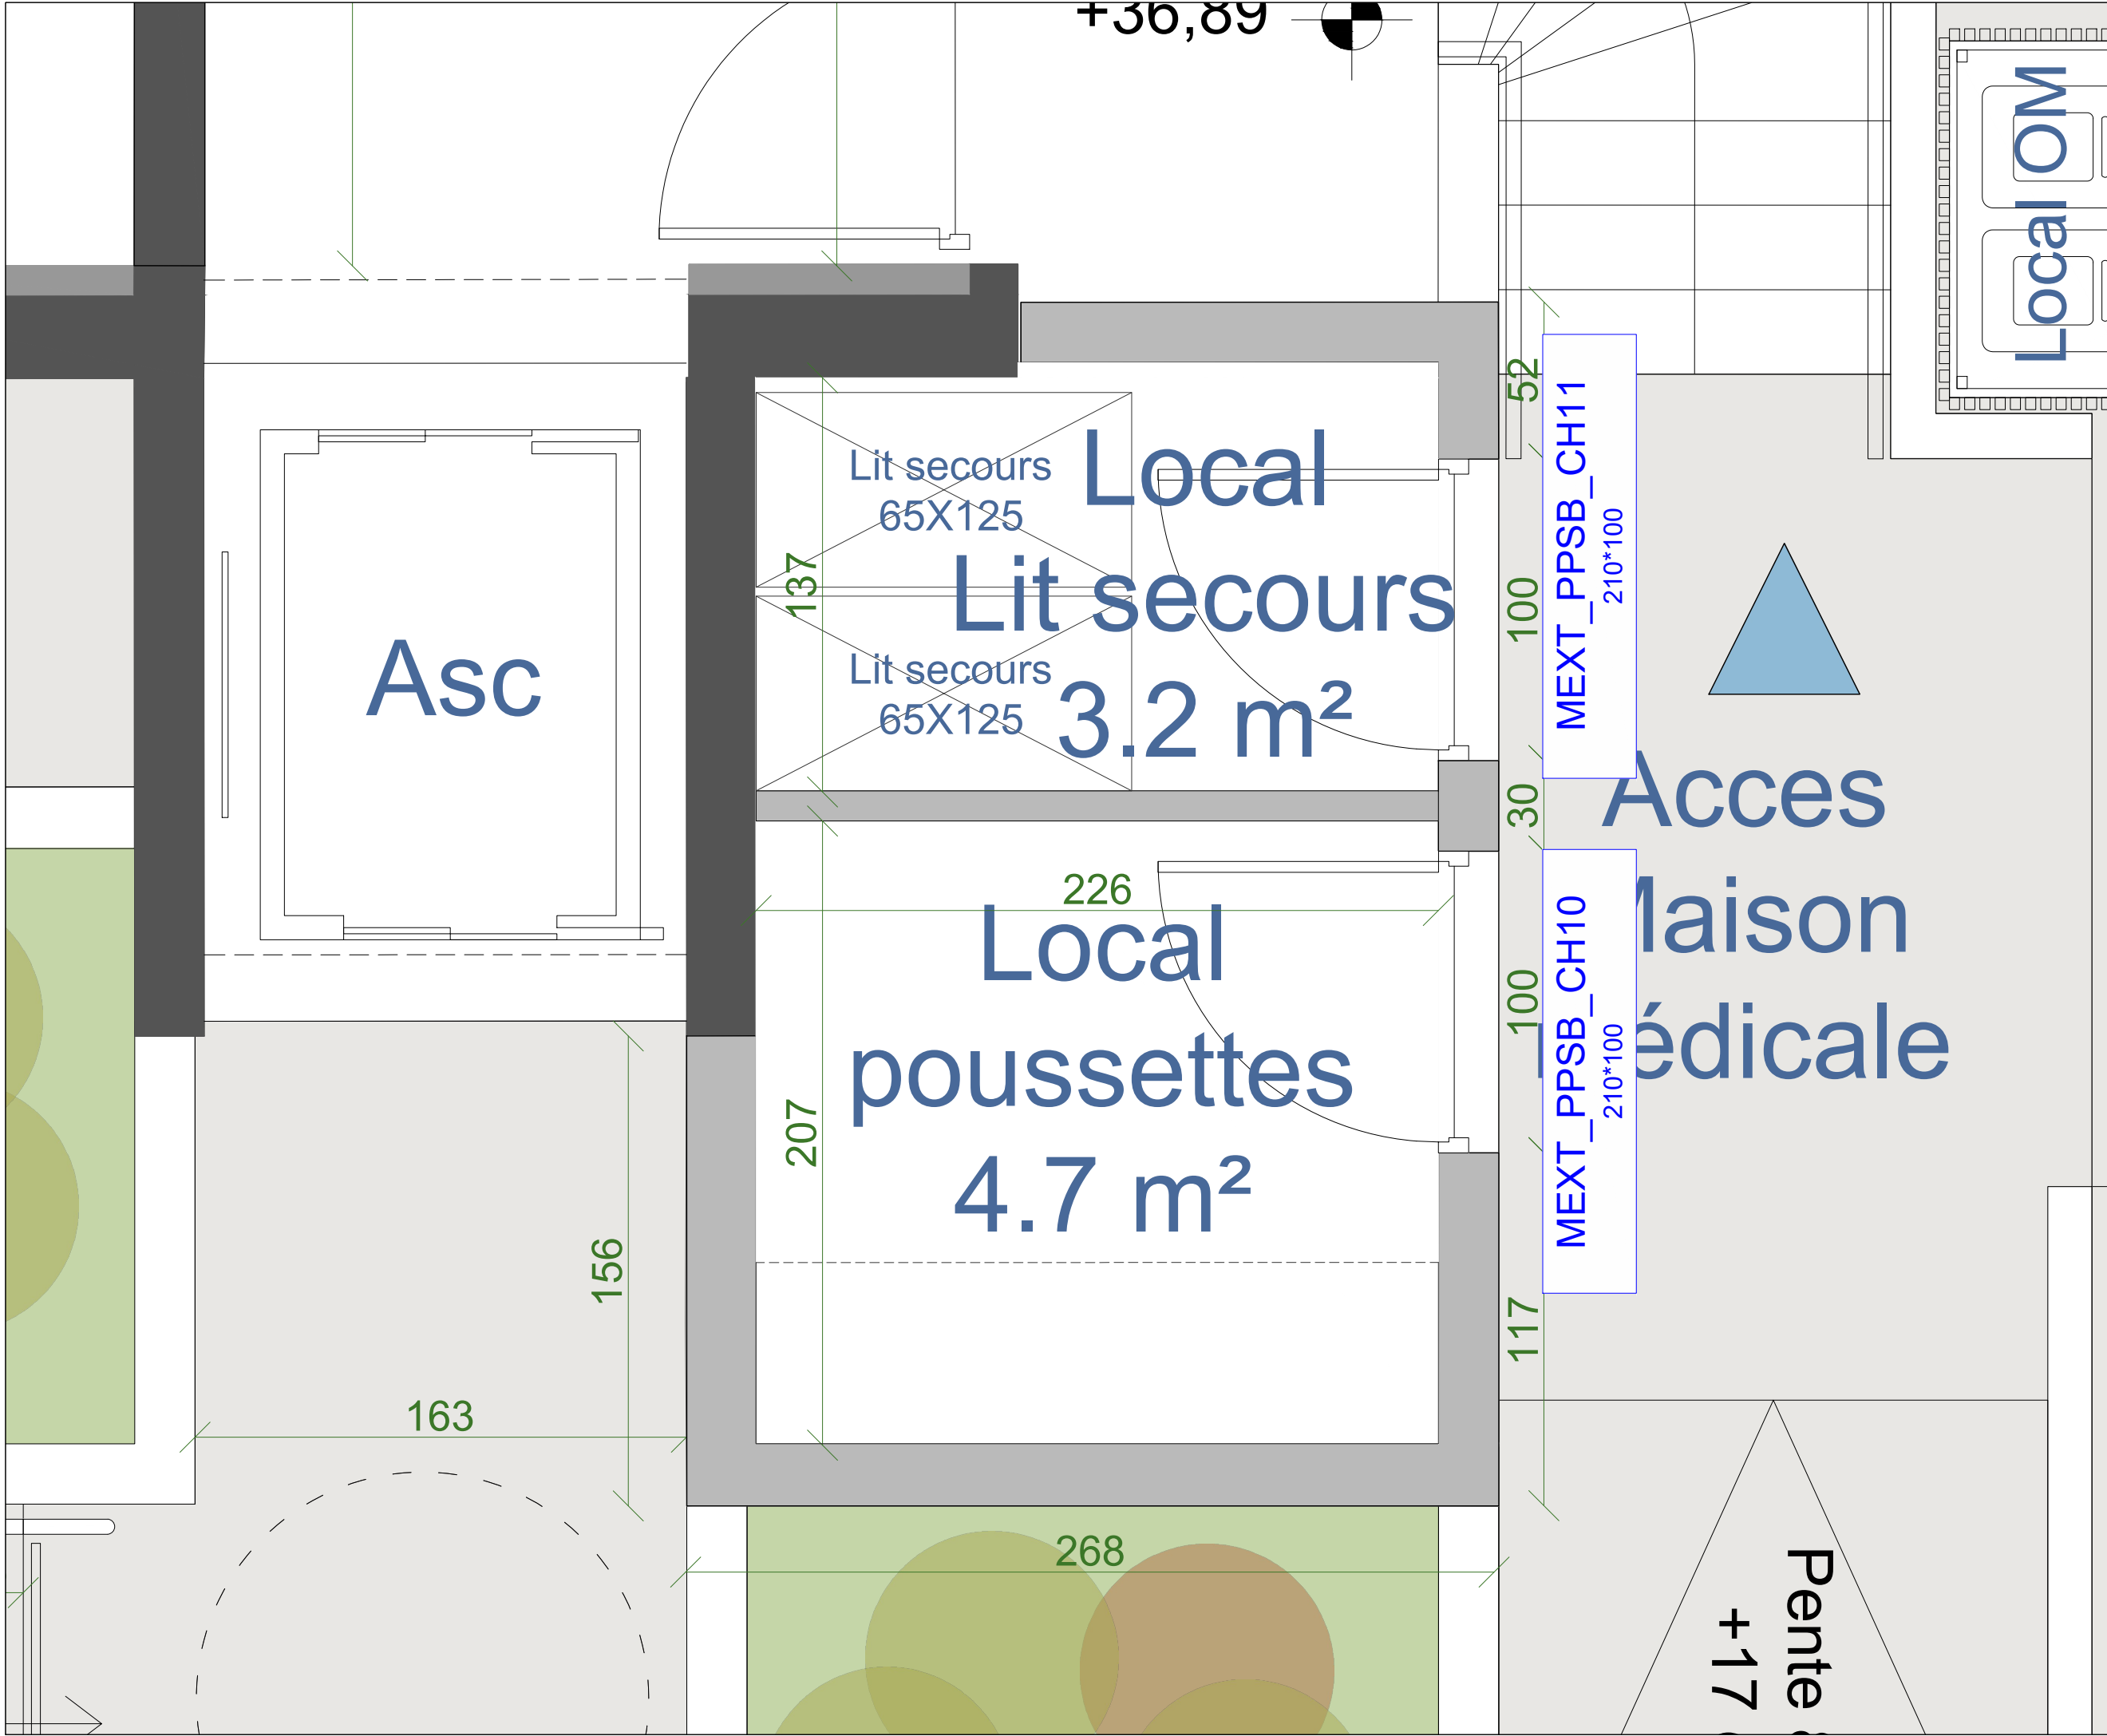

CREATION D'UN MULTI-ACCUEIL ET D'UNE MAISON MEDICALE 78400 CHATOU			
MOA	SARL LPC YVELINES 15 Rue de l'Orient78000 VERSAILLES		
MOE	NAHK ARCHITECTURE 24 Rue Yves Toudic, 75010 Paris		
NOM DU DOCUMENT			
MENUISERIE LOCAL POUSSETTE			
PHASE	PRO.DCE	ECH.	1/20
INDICE	1.1	DATE	30/06/2023
MODIFICATIONS			
INDICE DATE OBJET			
1.1	30/06/2023	Diffusion initiale	


MEXT_PPSB. Simple battant aluminium

Dimensions : 100 x 210 cm
Quantité : 2
Battants : Simple à âme pleine
Localisation : Local poussettes, Local lit secours
Remarques : serrure, ferme porte intégré, H poignée 100cm


MEXT_PPSB_CH10
210*100

MEXT_PPSB_CH11
210*100

Vue en plan :

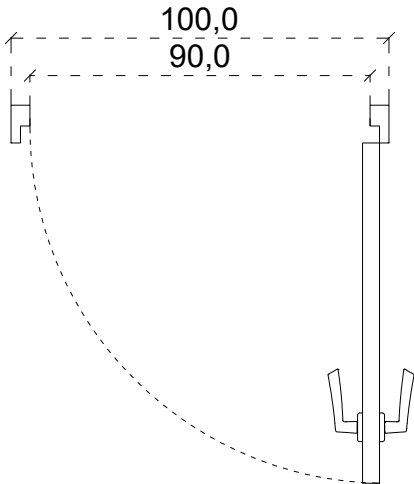

Élévation :

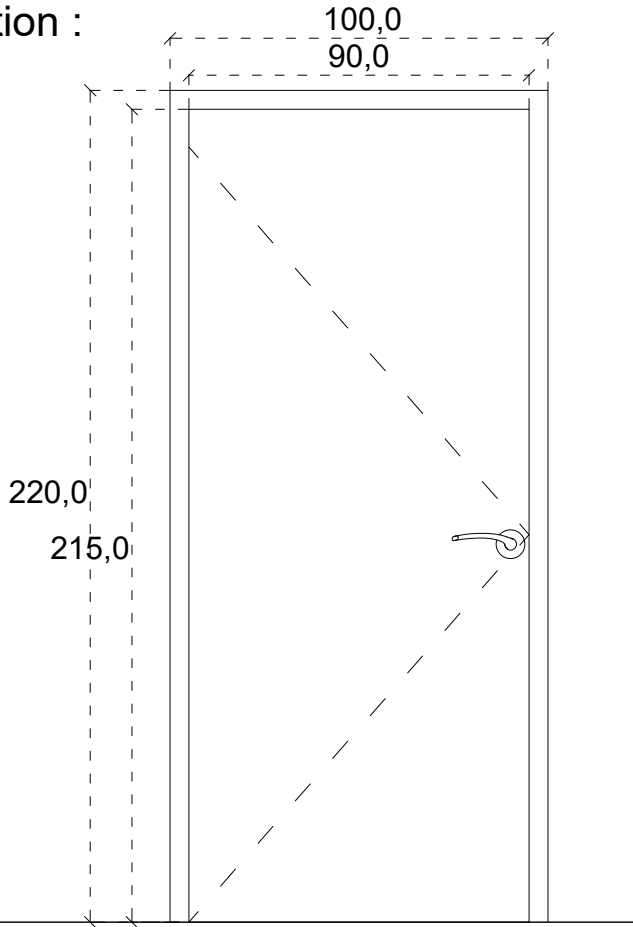

CREATION D'UN MULTI-ACCUEIL ET
D'UNE MAISON MEDICALE
78400 CHATOU

MOA SARL LPC YVELINES
15 Rue de l'Orient78000 VERSAILLES

MOE NAHK ARCHITECTURE
24 Rue Yves Toudic, 75010 Paris

NOM DU DOCUMENT

TABLEAU DES MENUISERIES
EXTERIEURES

PHASE	PRO.DCE	ECH.	1/20
-------	---------	------	------

INDICE	1.1	DATE	30/06/2023
--------	-----	------	------------

MODIFICATIONS
INDICE DATE OBJET

1.1 30/06/2023 Diffusion initiale

CREATION D'UN MULTI-ACCUEIL ET D'UNE MAISON MEDICALE 78400 CHATOU			
MOA	SARL LPC YVELINES 15 Rue de l'Orient78000 VERSAILLES		
MOE	NAHK ARCHITECTURE 24 Rue Yves Toudic, 75010 Paris		
NOM DU DOCUMENT			
ELEVATION / COUPE LOCAL POUSSETTE			
PHASE	PRO.DCE	ECH.	1/50
INDICE	1.1	DATE	30/06/2023
MODIFICATIONS			
INDICE DATE		OBJET	
1.1	30/06/2023	Diffusion initiale	

