



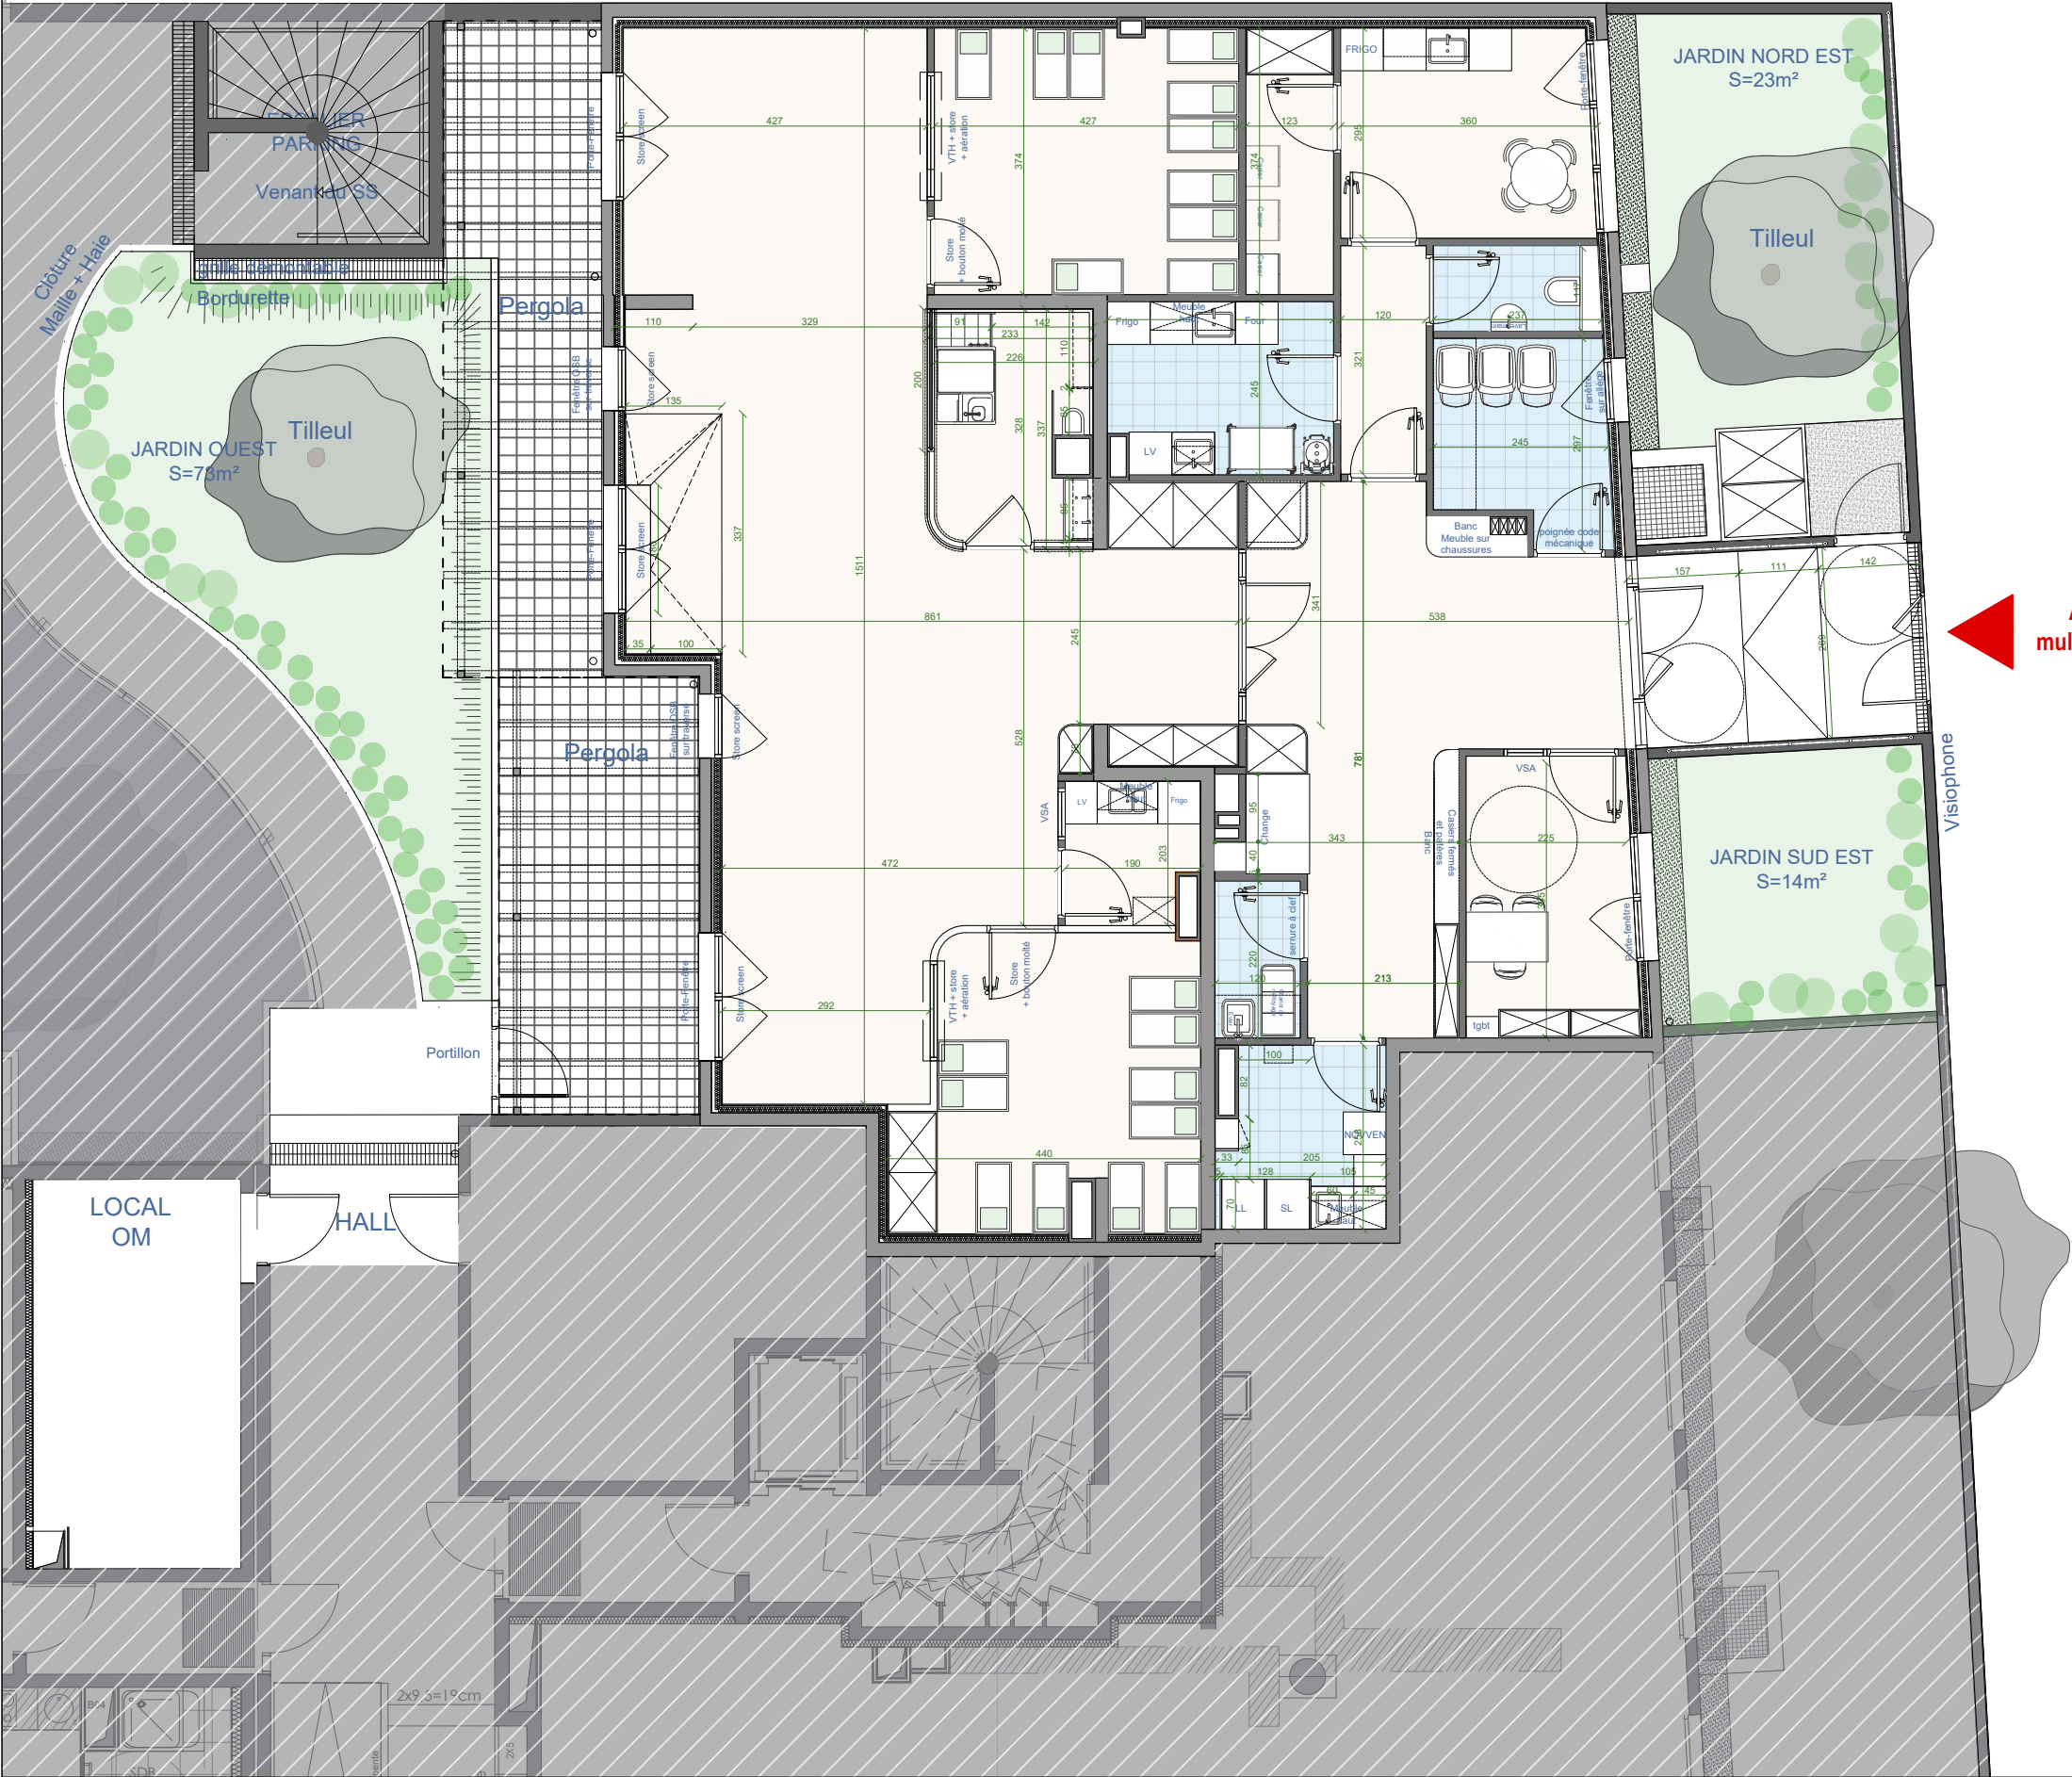

TROTTOIR

RUE ARISTIDE BRIAND

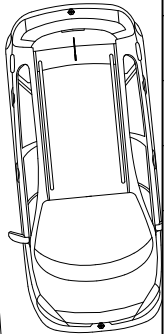

CREATION D'UN MULTI-ACCUEIL 49 RUE ARISTIDE BRIAND 94430 CHENNEVIERES-SUR-MARNE			
MOA	SARL LPC-033 LQB 1 Avenue André Gide, 94510 La Queue-en-Brie		
MOE	NAHK ARCHITECTURE 24 Rue Yves Toudic, 75010 Paris		
NOM DU DOCUMENT			
PLAN RDC MULTI-ACCUEIL			
PHASE	PMI		
INDICE	1.2	DATE	11/01/2024
MODIFICATIONS			
INDICE	DATE	OBJET	
1.1	06/12/2023	Diffusion initiale	
1.2	11/01/2024	Diffusion initiale	
<			