


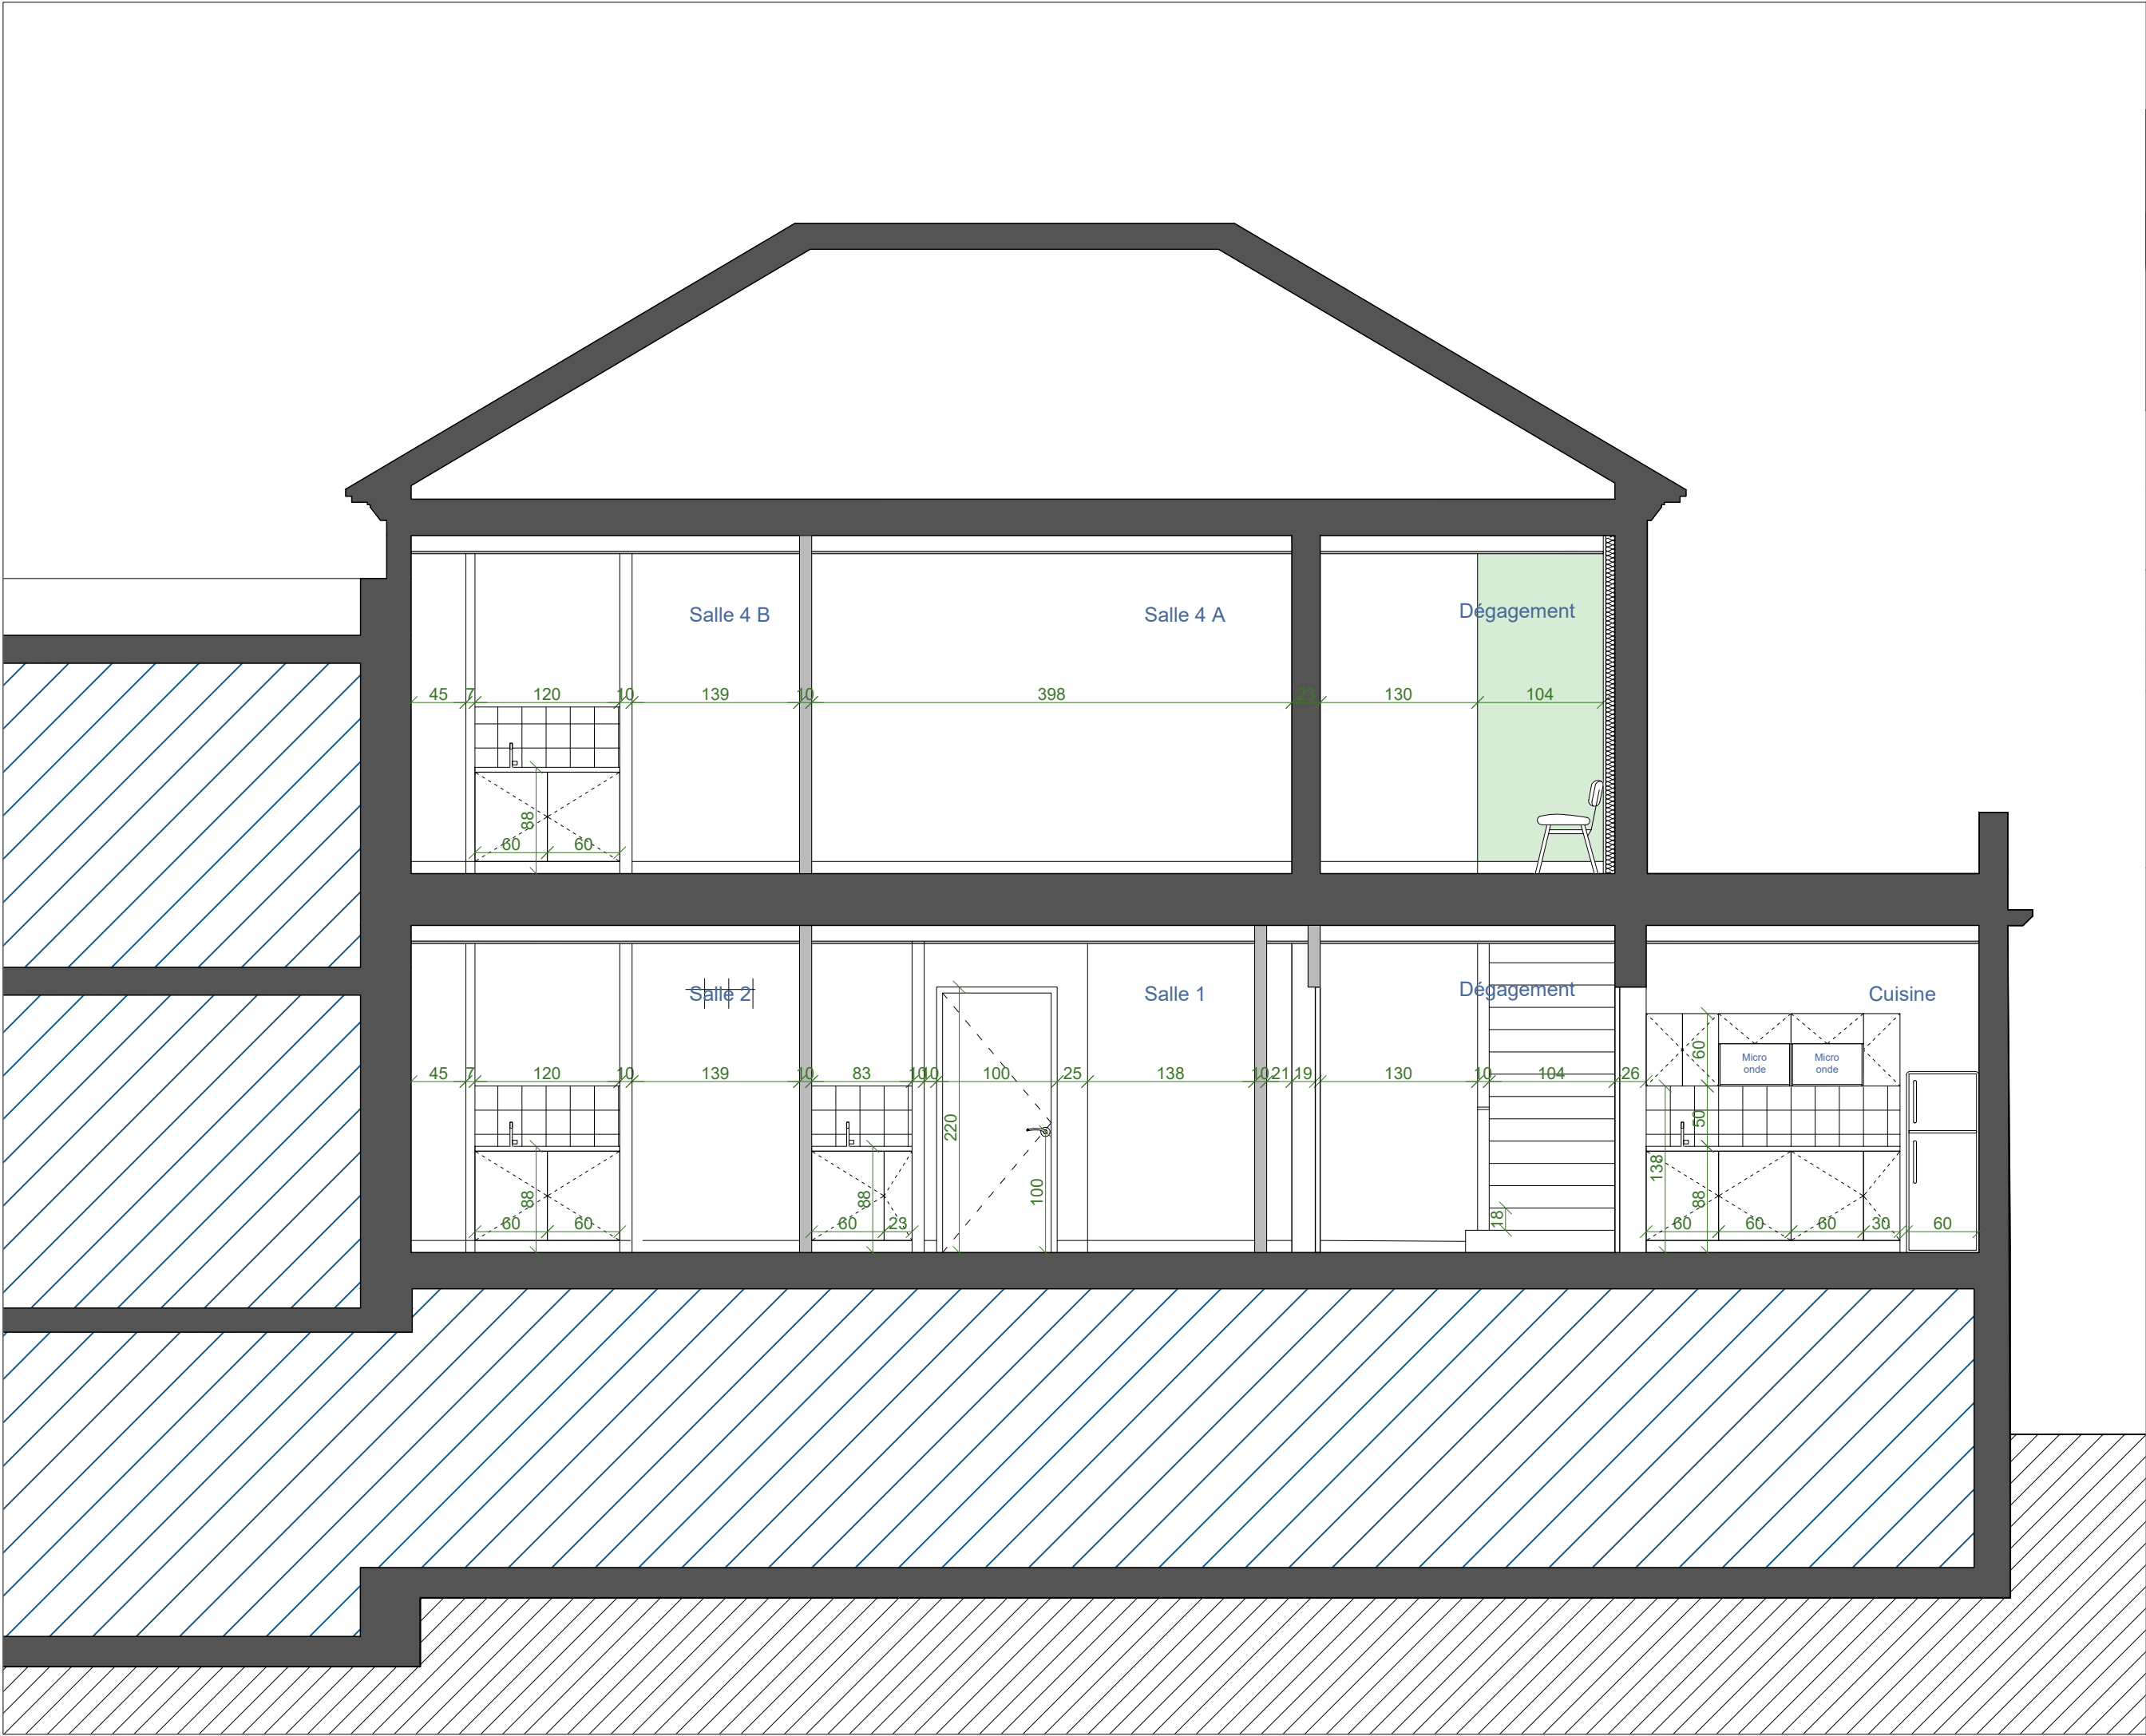

CREATION D'UN MULTI-ACCUEIL ET
D'UNE MAISON MEDICALE
30 ter Avenue de Brimont
78400 CHATOU

MOA

SARL LPC YVELINES
15 Rue de l'Orient78000 VERSAILLES

MOE

NAHK ARCHITECTURE
24 Rue Yves Toudic, 75010 Paris

NOM DU DOCUMENT

COUPE AA'

PHASE

PRO.DCE

ECH.

1/50

INDICE

1.1

DATE

09/06/2023

MODIFICATIONS

INDICE

DATE

OBJET

1.1

09/06/2023

Diffusion initiale

PLAN DE REPERAGE

B

A

D

C

B'

A'

D'

C'

R+1

B

A

D

C


B'

A'

D'

C'

RDC

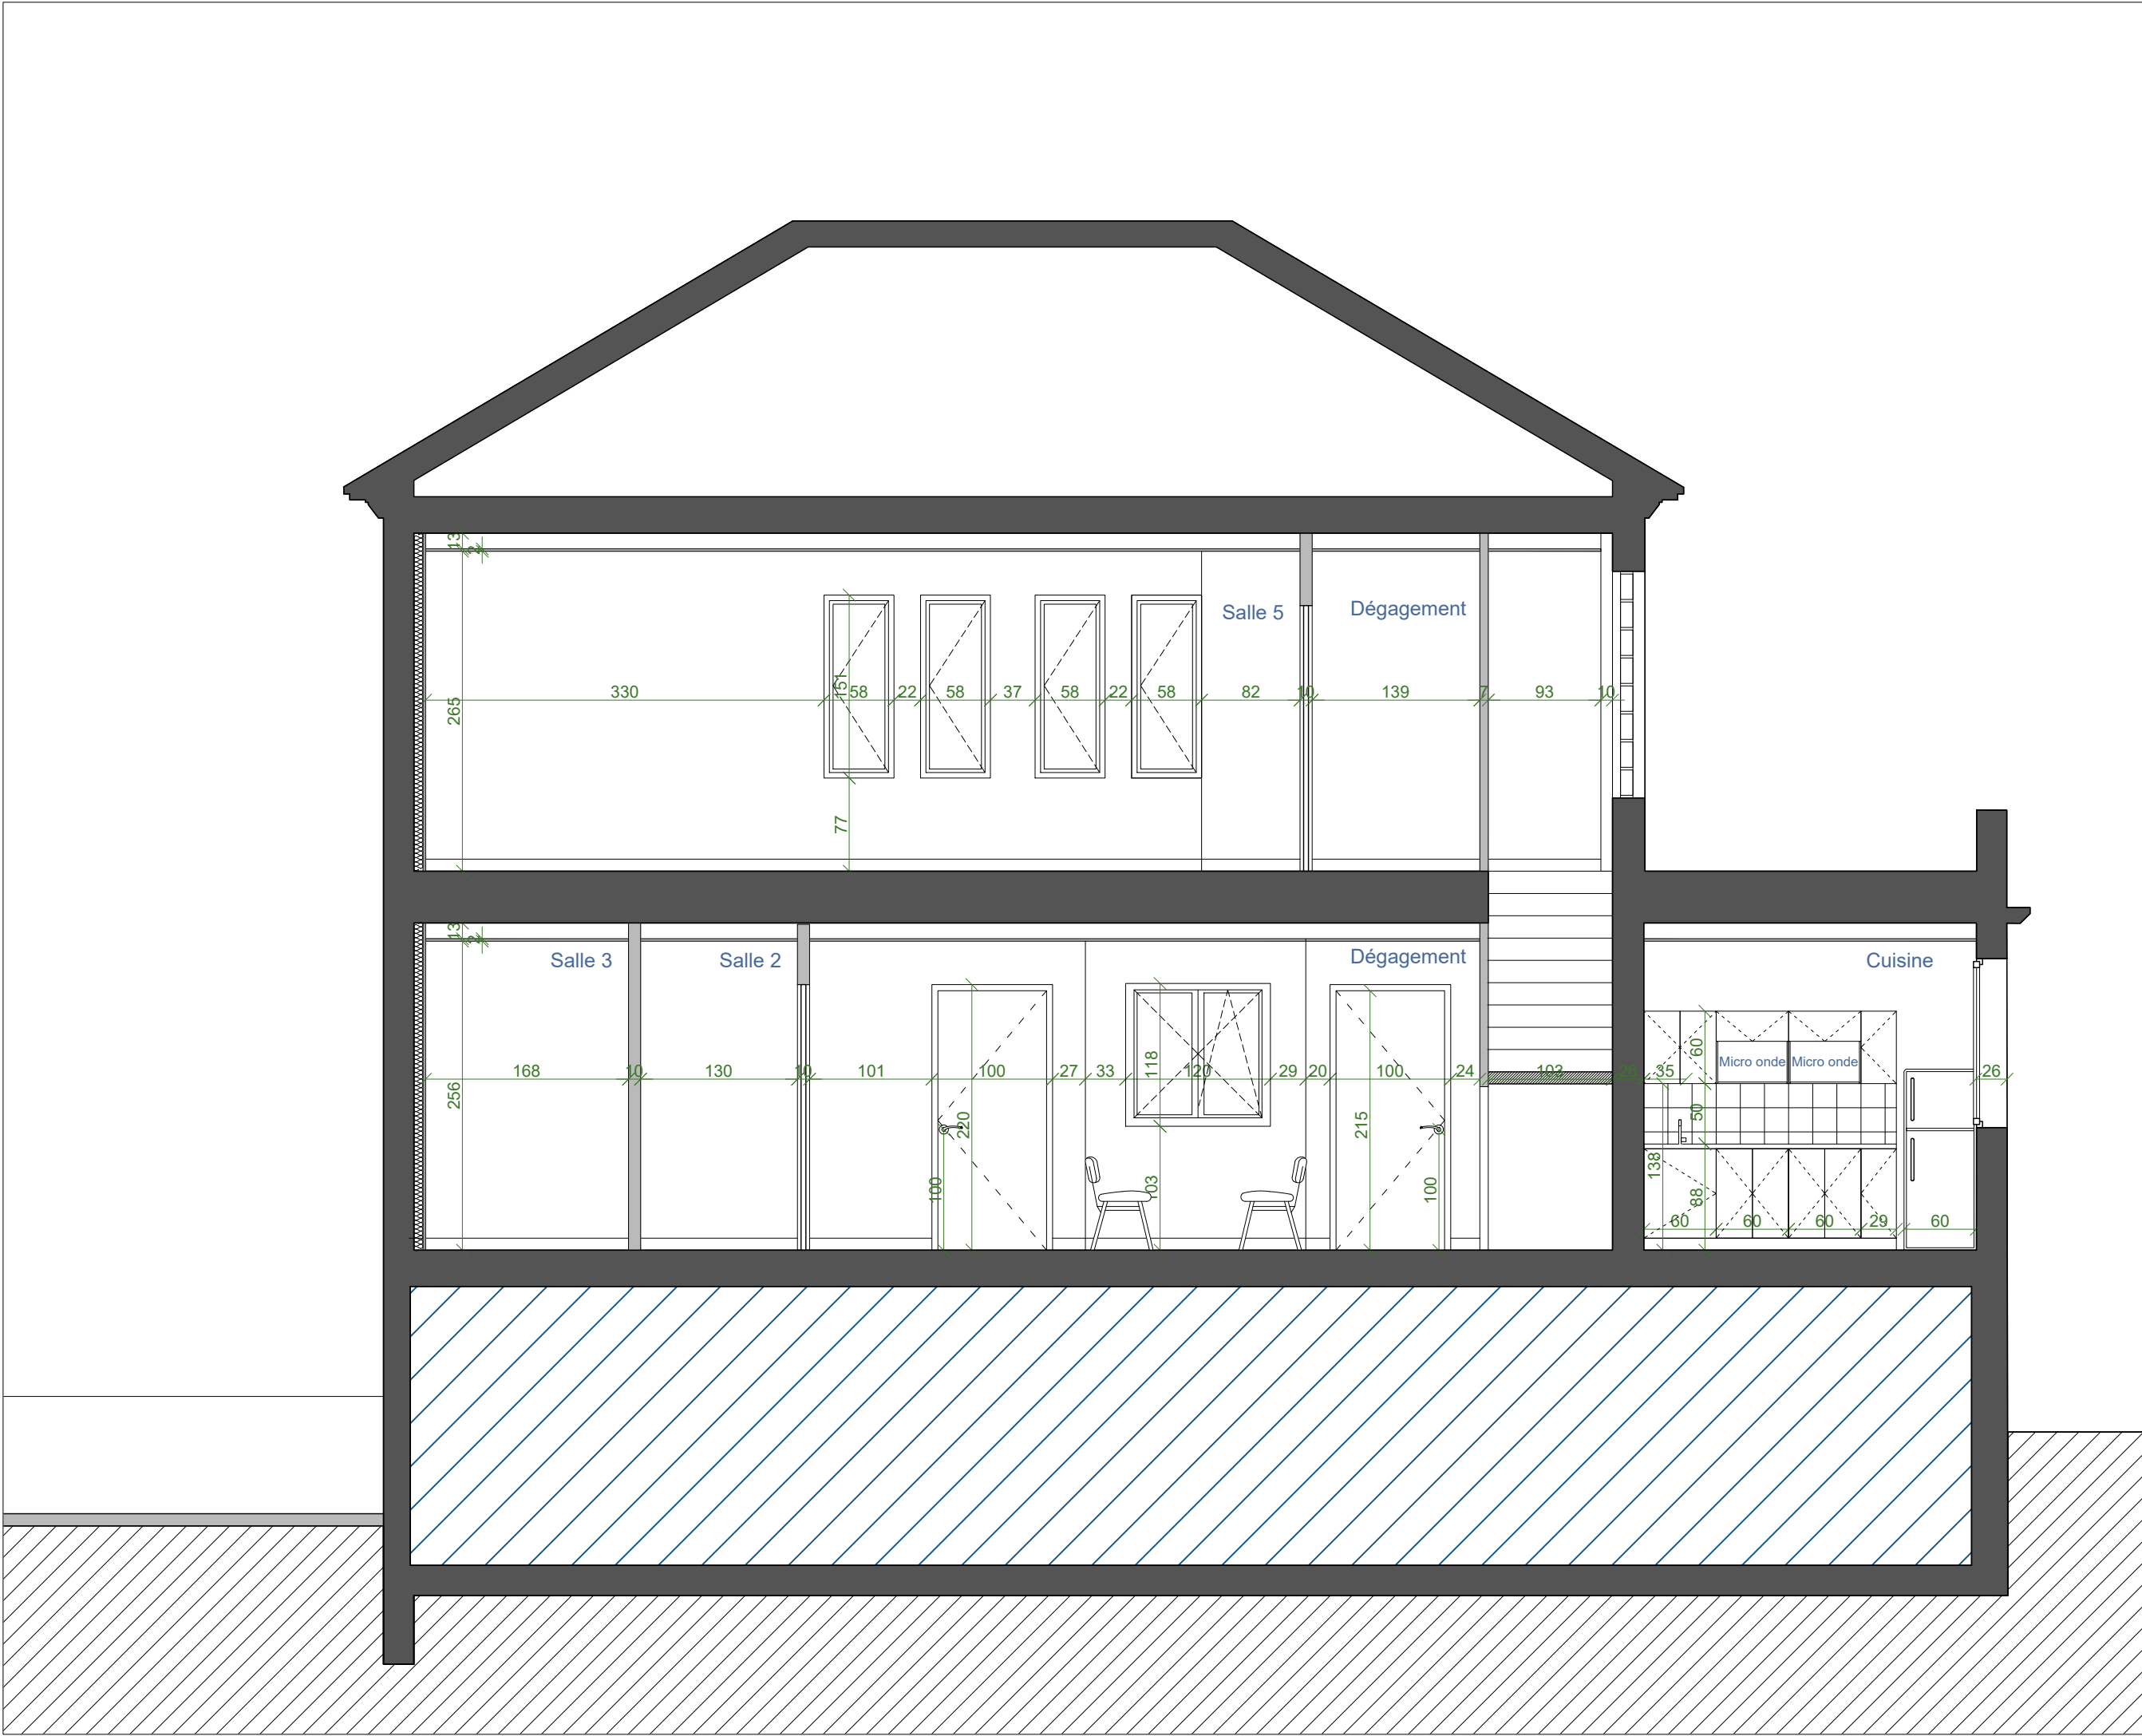

CREATION D'UN MULTI-ACCUEIL ET
D'UNE MAISON MEDICALE
30 ter Avenue de Brimont
78400 CHATOU

MOA

SARL LPC YVELINES
15 Rue de l'Orient78000 VERSAILLES

MOE

NAHK ARCHITECTURE
24 Rue Yves Toudic, 75010 Paris

NOM DU DOCUMENT

COUPE BB'

PHASE

PRO.DCE

ECH.

1/50

INDICE

1.1

DATE

09/06/2023

MODIFICATIONS
INDICE DATE OBJET

1.1

09/06/2023

Diffusion initiale

PLAN DE REPERAGE

B

A

D

C

B'

A'

D'

C'

R+1

B

A

D

C

B'


A'

D'

C'

ACCES

RDC

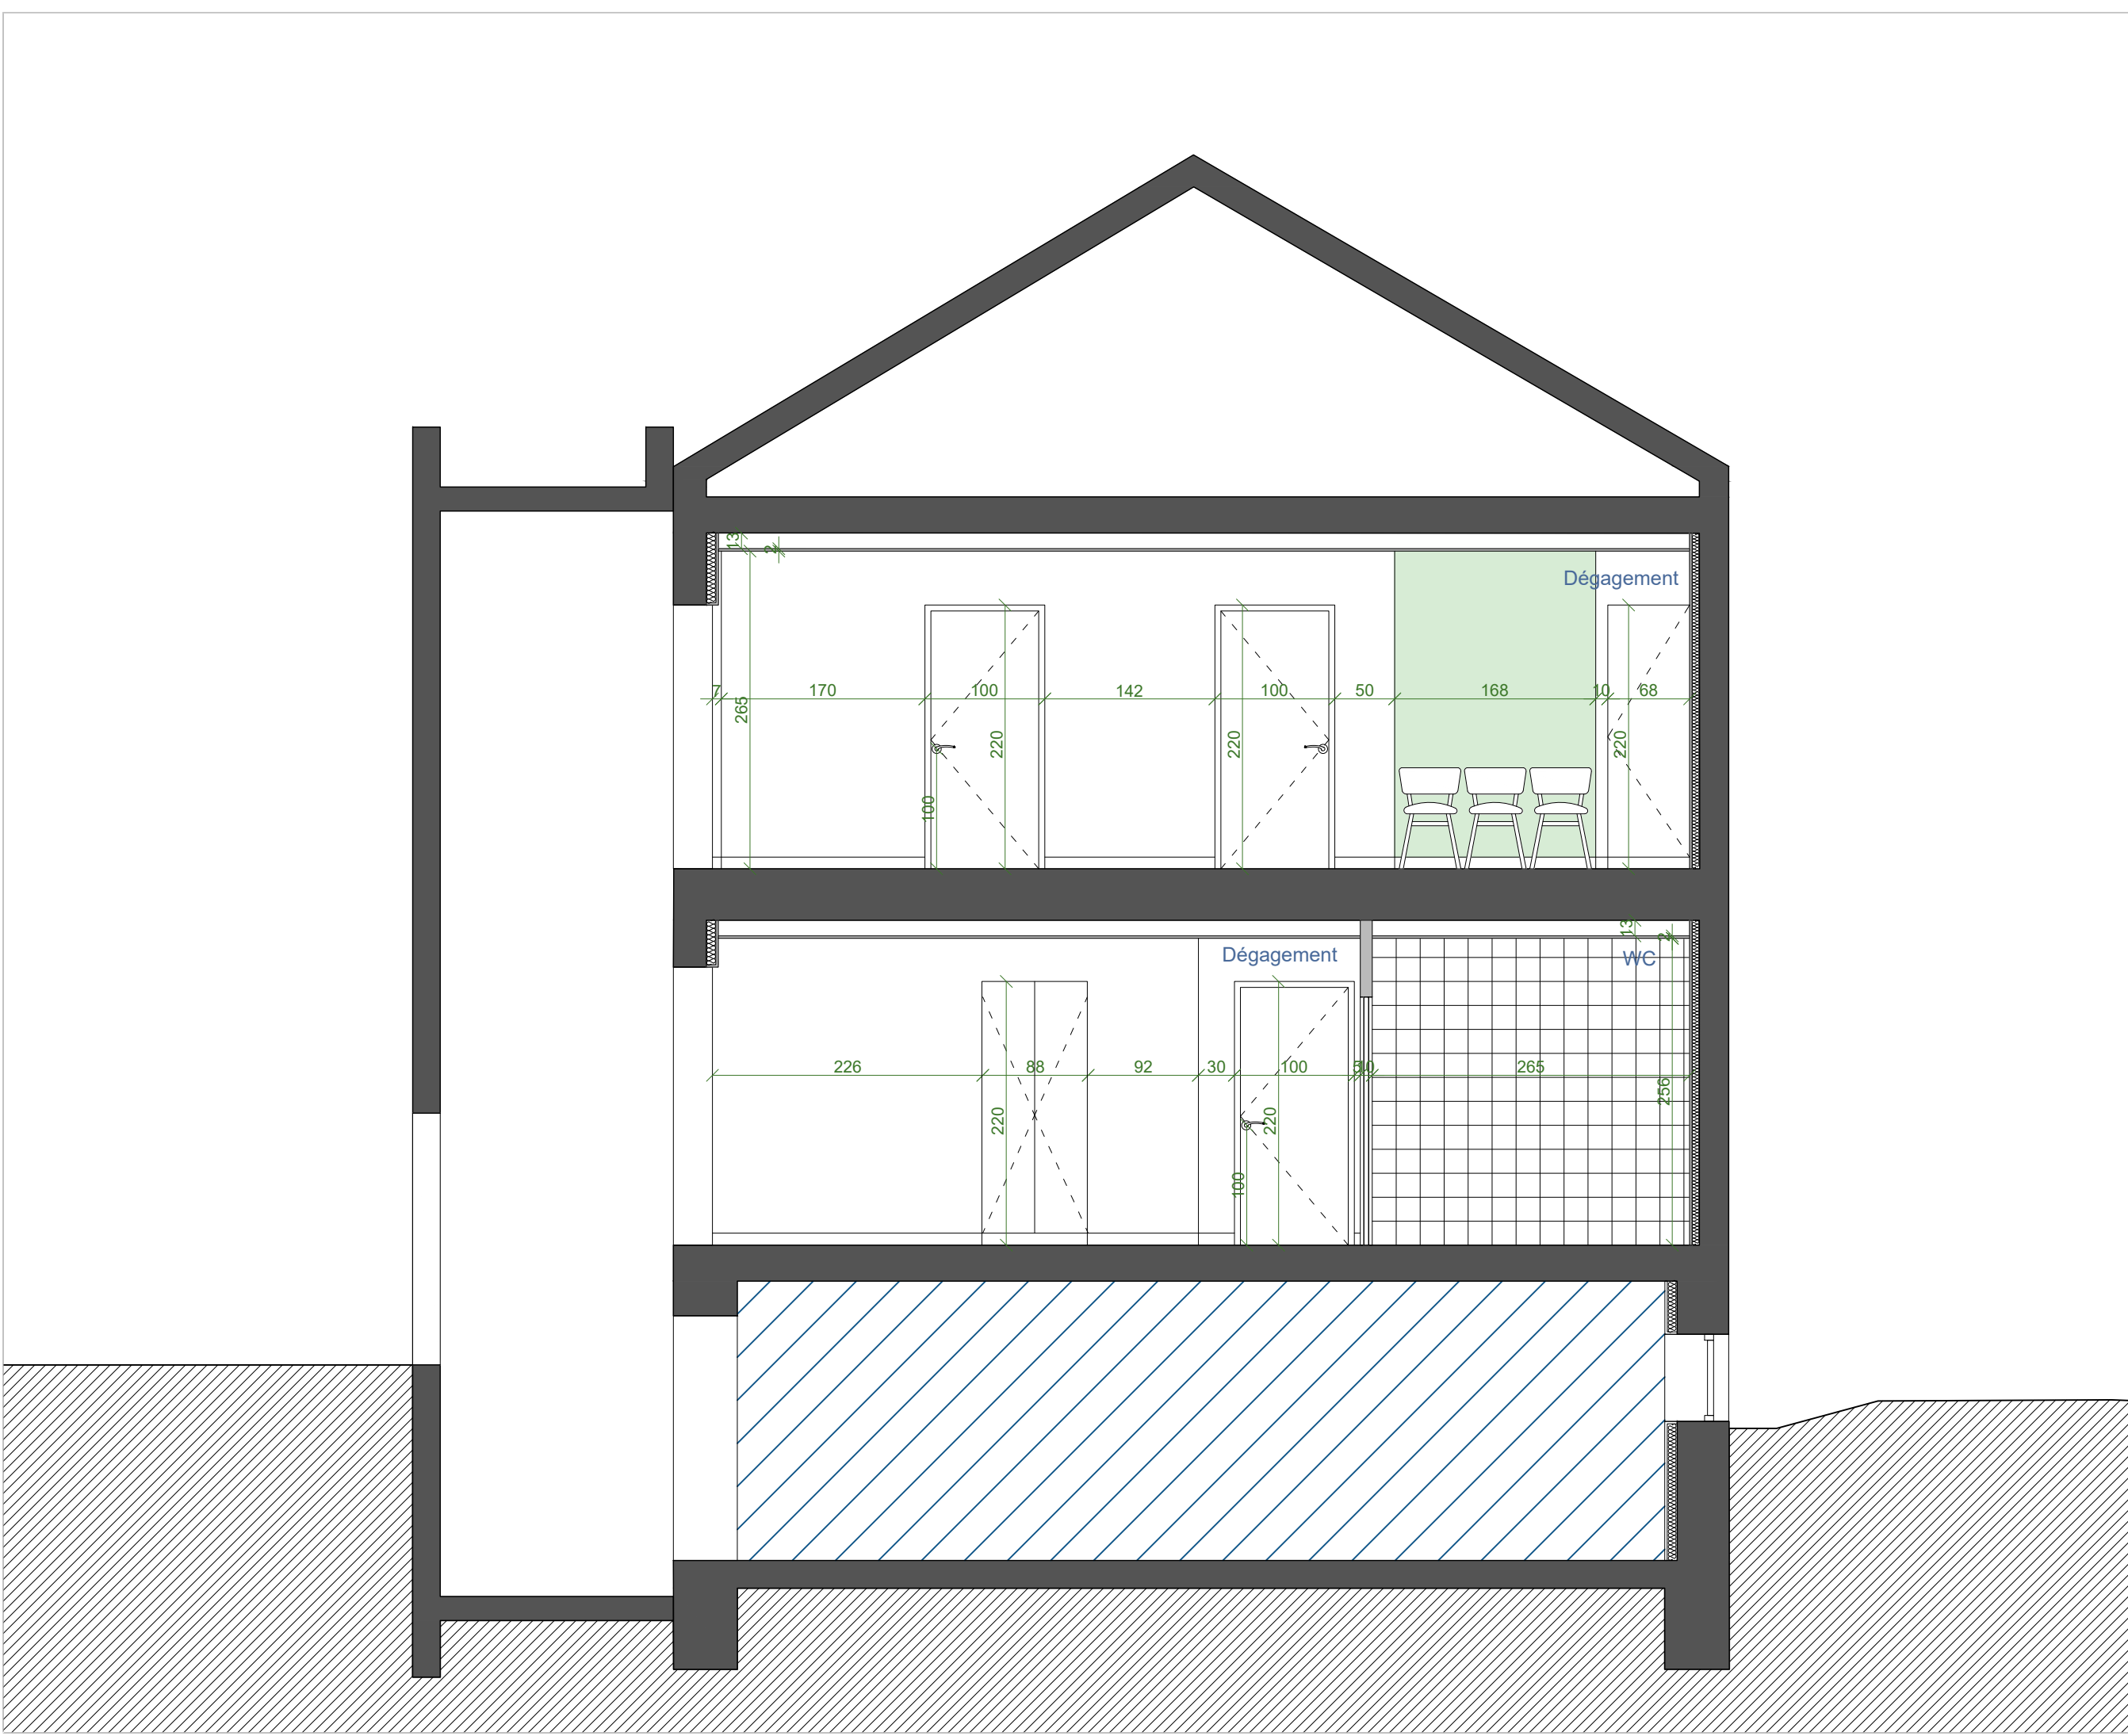

CREATION D'UN MULTI-ACCUEIL ET
D'UNE MAISON MEDICALE
30 ter Avenue de Brimont
78400 CHATOU

MOA

SARL LPC YVELINES
15 Rue de l'Orient78000 VERSAILLES

MOE

NAHK ARCHITECTURE
24 Rue Yves Toudic, 75010 Paris

NOM DU DOCUMENT

COUPE CC'

PHASE	PRO.DCE	ECH.	1/100
INDICE	1.1	DATE	09/06/2023


MODIFICATIONS
INDICE DATE OBJET

1.1	09/06/2023	Diffusion initiale
-----	------------	--------------------

PLAN DE REPERAGE

R+1

RDC

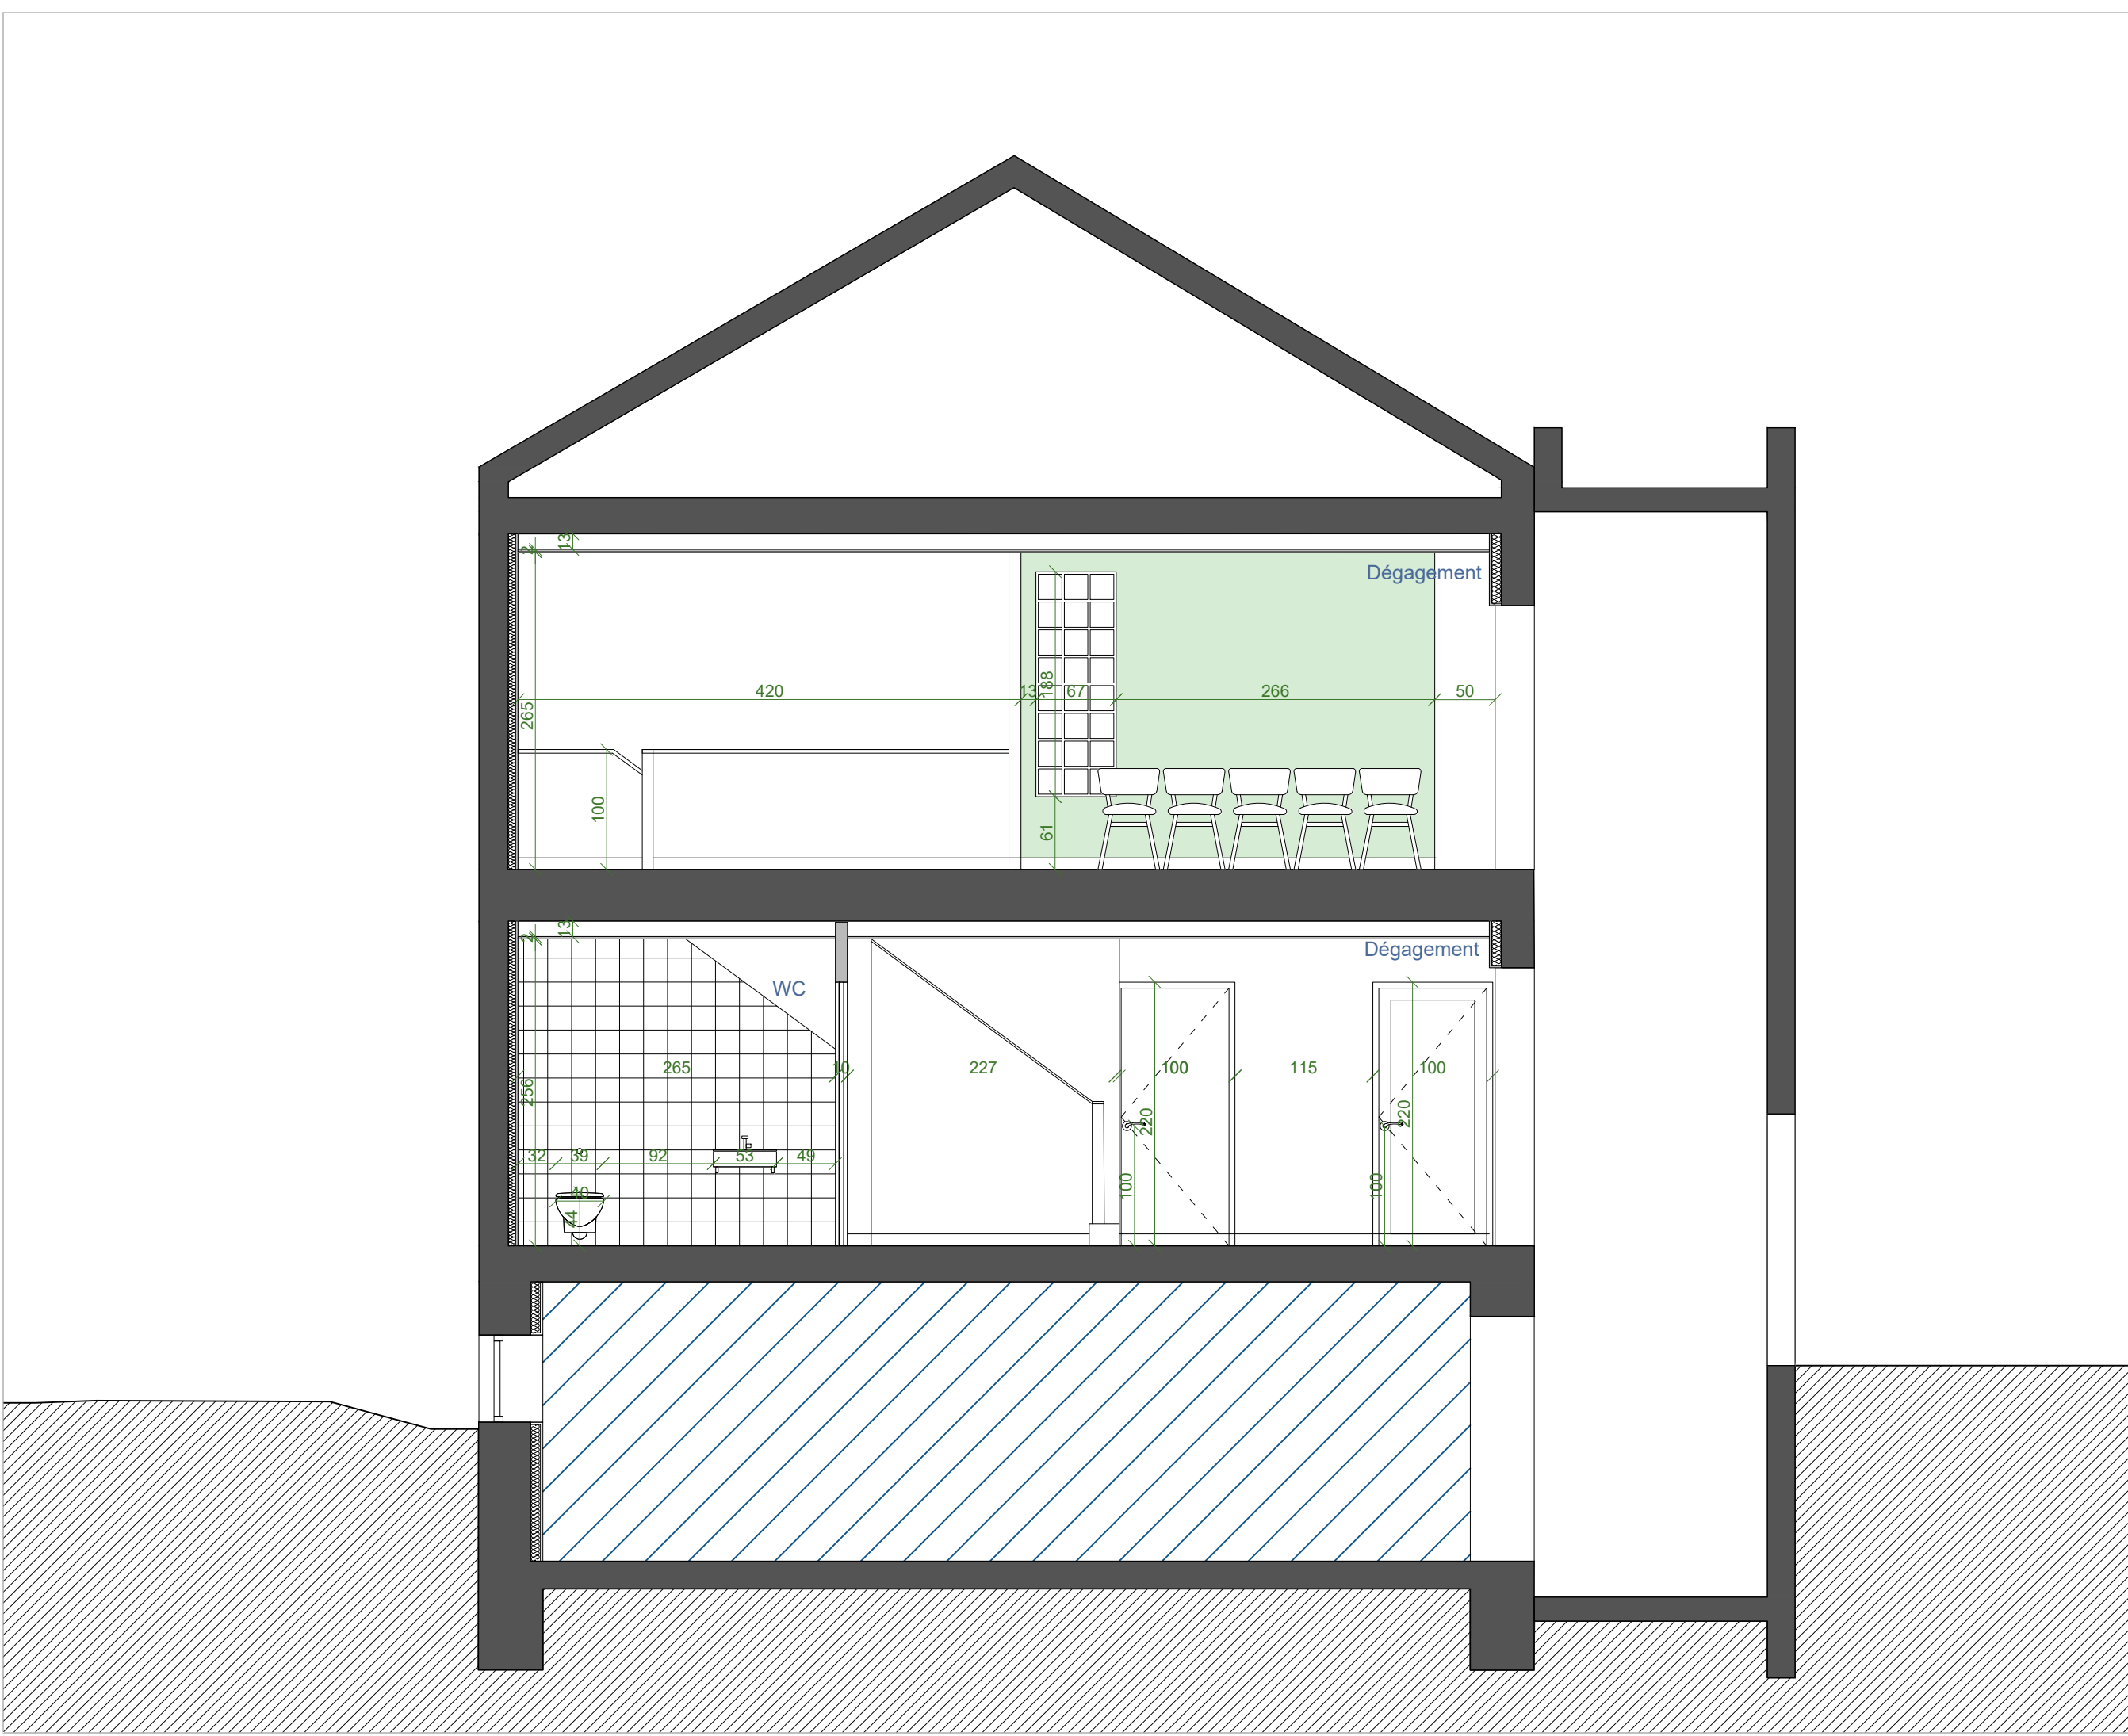

CREATION D'UN MULTI-ACCUEIL ET
D'UNE MAISON MEDICALE
30 ter Avenue de Brimont
78400 CHATOU

MOA

SARL LPC YVELINES
15 Rue de l'Orient78000 VERSAILLES

MOE

NAHK ARCHITECTURE
24 Rue Yves Toudic, 75010 Paris

NOM DU DOCUMENT

COUPE DD'

PHASE

PRO.DCE

ECH.

1/100

INDICE

1.1

DATE

09/06/2023

MODIFICATIONS

INDICE

DATE

OBJET

1.1

09/06/2023

Diffusion initiale

PLAN DE REPERAGE

B

A

D

C

B'

A'

D'

C'

R+1

B

A

D

C

B'

A'

D'

C'

ACCES

RDC