

Demande d'autorisation de construire, d'aménager ou de modifier un établissement recevant du public (ERP)

cerfa
N° 13824*04

Cette demande fait suite à un agenda d'accessibilité programmée (Ad'AP) approuvé : Oui ☐ Non ☐

Articles L. 111-8 et D. 111-19-34 du code de la construction et de l'habitation

Cadres 1 à 3	informations nécessaires à l'instruction de l'autorisation de construire, d'aménager ou de modifier un établissement recevant du public
Cadre 4	informations nécessaires à la vérification de la conformité aux règles de sécurité et d'accessibilité en application de l'article R. 111-19-17, R. 123-22 du code de la construction et de l'habitation
Cadre 5	Informations nécessaires à l'instruction des dérogations ou modalités particulières d'application des règles de sécurité ou d'accessibilité
Cadre 6	engagement du demandeur

Vous pouvez utiliser ce formulaire si :

- vous souhaitez construire, aménager ou modifier un établissement recevant de public
- vous souhaitez réaliser les travaux de mise en accessibilité d'un établissement recevant du public dans le cadre d'un agenda d'accessibilité programmée
- Les travaux projetés ne sont pas soumis ni à un permis de construire ni à un permis d'aménager

Cette demande vous permet d'accomplir les formalités nécessaires

CADRE RÉSERVÉ À L'ADMINISTRATION

N° de l'autorisation

AT _____

Le cas échéant, n° de la déclaration préalable¹ effectuée au titre du code de l'urbanisme :

Date de dépôt en mairie : / /

1 - Identité du demandeur. Le demandeur indiqué dans le cadre ci-dessous sera le titulaire de la future autorisation

Si la demande est présentée par plusieurs personnes, indiquez leurs coordonnées sur papier libre ⁽¹⁾

Vous êtes un particulier

Madame ☐ Monsieur ☐

Nom : Prénom : Date de naissance : | | | | | | | | | |

Vous êtes une personne morale

Raison sociale et dénomination :

N° Siret :

Représentant de la personne morale : Madame ☐ Monsieur ☐

Nom : Prénom : Date de naissance à défaut de N° Siret : | | | | | | | | | |

2 - Coordonnées des ou du demandeur(s) *Si la demande est présentée par plusieurs personnes, indiquez leurs coordonnées sur papier libre²*

Adresse Numéro : Voie :

Lieu-dit : Localité :

Code postal BP cedex

Si le demandeur habite à l'étranger : Pays : Division territoriale :

Téléphone fixe : _____ Portable : _____

Indicatif si pays étranger : Courriel :@.....

1 Votre projet peut également être soumis au respect de la réglementation de l'urbanisme et nécessiter l'obtention d'une déclaration préalable notamment s'il entraîne un changement de destination du bâtiment, modifie des structures porteuses ou le volume d'une construction existante. Si une déclaration préalable est nécessaire, elle sera instruite en parallèle de la présente autorisation.

2 Les décisions prises par l'administration seront notifiées au demandeur indiqué ci-dessus. Une copie des décisions concernant les autorisations de travaux sera adressée aux autres demandeurs, lesquels seront co-titulaires de l'autorisation.

3 - Auteur du projet ou maître d'œuvre

Madame ☐ Monsieur ☐ Personne morale ☐

Nom : Prénom :

Et/ou :

Raison sociale et dénomination de la personne morale, le cas échéant :

N° Siret :
.....

Adresse Numéro : Voie :

Lieu-dit : Localité :

Code postal BP cedex

Si le maître d'œuvre habite à l'étranger/ Pays : Division territoriale :

Téléphone fixe : Téléphone portable :

Indicatif si pays étranger : Courriel : @

☐ Je souhaite que les courriers de l'administration (autres que les décisions) lui soient adressés

4 - Le projet

4.1 – Adresse du terrain

Nom de l'établissement :

Numéro : Voie :

Lieu-dit : Localité :

Code postal BP cedex

N° de section(s) cadastrale(s) : N° de parcelle (s) :

4.2 – Activité

AVANT TRAVAUX, le cas échéant :

Activité principale exercée dans l'établissement (par étage(s)) :

.....
.....
.....
.....

Activité(s) annexe(s) ou secondaire(s) (par étage(s)) :

.....
.....
.....
.....

Classement sécurité incendie de l'ERP :

(Catégorie et type d'exploitation en application de l'article R. 123-19 du code de la construction et de l'habitation)

.....
.....
.....
.....

Identité de l'exploitant (s'il est connu au moment du projet) :

.....
.....
.....
.....

APRÈS TRAVAUX :

Activité principale (par étage(s)) :

.....
.....
.....
.....

Activité(s) annexe(s) (par étage(s)) :

.....
.....
.....
.....

Proposition de classement sécurité incendie de l'ERP :

(Catégorie et type d'exploitation en application de l'article R. 123-19 du code de la construction et de l'habitation)

.....
.....
.....
.....

Identité de l'exploitant (s'il est connu au moment du projet) :

.....
.....
.....
.....

Veuillez compléter sur papier libre, si nécessaire.

4.3 – Nature des travaux (*plusieurs cases possibles*)

- ☐ Construction neuve
☐ Travaux de mise en conformité totale aux règles d'accessibilité
☐ Extension
☐ Réhabilitation
☐ Travaux d'aménagement (remplacement de revêtements, rénovation électrique, création d'une rampe, par exemple)
☐ Création de volumes nouveaux dans des volumes existants (modification du cloisonnement, par exemple)

Surface de plancher avant travaux : Surface de plancher après travaux :

☐ Modification des accès en façades

Le cas échéant, préciser si ces travaux mettent en œuvre des engagements d'un Ad'AP déposé antérieurement.

☐ Oui : Ad'AP n° validé le :
☐ Non

Cette demande fait l'objet d'une déclaration ou autorisation au titre du code de l'environnement (produits dangereux stockés ou utilisés) : Oui ☐ Non ☐

4.4 – Effectif

Effectif maximum susceptible d'être admis même temporairement par niveau (suivant le calcul réglementaire défini par le règlement incendie) en indiquant les principaux locaux accessibles au public

	Types de locaux (activité/prestation)	Public	Personnel	TOTAL
Sous-sol				
Rez-de-chaussée				
1 ^{er} étage				
2 ^e étage				
3 ^e étage				
Effectif cumulé				

Veuillez joindre une note annexe si le projet le nécessite (nombre d'étages supérieur à 3, présence d'une mezzanines, etc)

4.5 - Stationnement

Stationnement couvert ☐ Parcs de stationnement intégrés ☐ ou isolés ☐

Si parc existant, préciser son année de permis de construire (PC) initial :

	Avant réalisation du projet	Après réalisation du projet
Nombre de places de stationnement		
Dont nombre de places réservées aux personnes handicapées		

5 - Dérogations et/ou adaptations mineures**5.1 – Dérogations**

Ce projet comporte une demande de dérogation :

☐ Au titre de la sécurité incendie (Article R.123-13 du CCH) : Nombre de dérogations demandées :

Chaque demande doit faire l'objet d'une fiche détaillée rédigée sur papier libre indiquant notamment les règles auxquelles il est demandé de déroger (référence article et libellé), les éléments du projet auxquels elles s'appliquent (localisation sur les plans) et leur justification (motivation et mesures compensatoires proposées)

☐ Au titre de l'accessibilité (Article R. 111-19-10 du CCH) : Nombre de dérogations demandées :

Chaque demande doit faire l'objet d'une fiche détaillée rédigée sur papier libre indiquant notamment les règles auxquelles il est demandé de déroger (référence article et libellé), les éléments du projet auxquels elles s'appliquent (localisation sur les plans) et leur justification (motivation et mesures de substitution proposées pour les ERP exerçant une mission de service public)

5.2 – Modalités particulières d'application

☐ Le projet présente des contraintes liées à la structure du bâtiment qui justifient des modalités d'application particulières telles que définies par l'arrêté prévu à l'article R. 111-19-7 IV du Code de la construction et de l'habitation

(veuillez expliciter les adaptations prévues et les contraintes structurelles dont elles découlent)

Veuillez joindre une note annexe si le projet le nécessite

.....

.....

.....

.....

6 - Engagement du ou des demandeur(s)

J'atteste avoir qualité pour demander cette autorisation :

Je (nous) soussigné(és), auteur(s) de la demande, certifie(ions) exacts les renseignements qui y sont contenus.

J'ai pris connaissance des règles générales de construction prévues par le chapitre premier du titre premier et par les chapitres II et III du titre II du livre premier du code de la construction et de l'habitation et notamment celles concernant l'accessibilité et la sécurité incendie et m'engage à respecter les règles du code de la construction et de l'habitation relatives à la solidité et à la sécurité des personnes.

à

Le :

SAS LES PETITES CANAILLES .
Solutions et services petite enfance
36 rue Pierret
92200 Neuilly sur Seine
RCS Nanterre B 520 223 546
www.lespetitescanailles.fr

Signature du (des) demandeur(s)

Si vous souhaitez vous opposer à ce que les informations nominatives comprises dans ce formulaire soient utilisées à des fins commerciales, cochez la case ci-contre : ☐

Si vous êtes un particulier : La loi n° 78 -17 du 6 janvier 1978 relative à l'informatique, aux fichiers et aux libertés, s'applique aux réponses contenues dans ce formulaire pour les personnes physiques. Elle garantit un droit d'accès aux données nominatives les concernant lorsqu'ils ne portent pas atteinte à la recherche d'infractions fiscales et la possibilité de rectification sous réserve des procédures prévues au code général des impôts et au Livre des procédures fiscales. Ces droits peuvent être exercés à la mairie. Les données recueillies seront transmises aux services compétents pour l'instruction de votre demande.



Bordereau de dépôt des pièces jointes à une demande d'autorisation de construire, d'aménager ou de modifier un établissement recevant du public

Veuillez cocher les cases correspondant aux pièces jointes à votre demande et reporter le numéro correspondant sur la pièce jointe.

L'attention du pétitionnaire est attirée sur le fait que la commission de sécurité et/ou d'accessibilité pourra lui demander des pièces complémentaires si la compréhension du projet le nécessite.

Pièces	Numéro de la pièce	Nombre d'exemplaires à fournir
☐ Imprimé de demande d'autorisation de construire, d'aménager ou de modifier un établissement recevant du public	1	4
☐ Plan de situation	2	3

1 - Dossier destiné à la vérification de la conformité aux règles de sécurité incendie (Art. R. 123-22 du code de la construction et de l'habitation)


Pièces	Numéro de la pièce	Nombre d'exemplaires à fournir
☐ Une notice récapitulant les dispositions prises pour satisfaire aux mesures prévues par le règlement de sécurité et notamment : • les matériaux utilisés pour le gros œuvre, la décoration et les aménagements intérieurs • la ou les solutions retenues pour l'évacuation des personnes de chaque niveau de la construction en tenant compte des différentes situations de handicap	3	3
☐ Un plan de situation, des plans de masse et de façades des constructions projetées faisant ressortir : • les conditions d'accessibilité des engins de secours • les largeurs des voies et les emplacements des baies d'intervention pompiers • la présence de tout bâtiment ou local occupé par des tiers	4	3
☐ Des plans de coupe et des plans de niveaux, ainsi qu'éventuellement ceux des planchers intermédiaires aménagés dans la hauteur comprise entre deux niveaux ou entre le dernier plancher et la toiture du bâtiment, faisant apparaître notamment : • les largeurs des passages affectés à la circulation du public tels que les dégagements, escaliers, sorties • la ou les solutions retenues pour l'évacuation des personnes de chaque niveau de la construction en tenant compte des différentes situations de handicap • les caractéristiques des éventuels espaces d'attente sécurisés	5	3
☐ La ou les demande(s) de dérogation(s) éventuelle(s), la ou les fiche(s) explicative(s) et tous les documents utiles à leur justification	6	3

N. B : les documents de détail intéressant les installations techniques doivent pouvoir être fournis par le constructeur ou l'exploitant avant le début des travaux portant sur ces installations ; ils sont alors communiqués à la commission de sécurité

2 - Dossier destiné à la vérification de la conformité aux règles d'accessibilité (Arrêté du 8 décembre 2014 ETLL1413935A et arrêté du 20 avril 2017 LHAL1704269A) (PC39 ou PA 50)

Pièces	Numéro de la pièce	Nombre d'exemplaires à fournir
☐ Plan côté dans les trois dimensions (longueur, largeur, hauteur), à une échelle adaptée, précisant : • les cheminements extérieurs (fonctions, largeurs, pentes, dévers, éclairage, solutions techniques pour assurer le guidage, le repérage, ...) • les raccordements (voirie/parties extérieures de l'établissement ; parties extérieures/parties intérieures du ou des bâtiments constituant l'établissement) • les circuits destinés aux piétons et aux véhicules (liaison accès au terrain/voie interne/places de stationnement adaptées/circulations piétonnes/entrée de l'établissement) • les espaces de manœuvre, de retournement et de repos extérieurs • les pentes des plans inclinés et les dévers de cheminement	7	3

☐ Plan côté dans les trois dimensions (longueur, largeur, hauteur), à une échelle adaptée, pour chaque niveau et pour chaque bâtiment précisant : • Les circulations intérieures horizontales et verticales (fonctions, largeurs, pentes, dévers ...) • Les aires de stationnement • Les locaux sanitaires destinés au public • Le sens d'ouverture des portes et leur espace de débattement • Les espaces d'usage, de manœuvre, de retournement et de repos intérieurs • L'emplacement des appareils sanitaires et leurs accessoires obligatoires • Les places de stationnements adaptées et réservées aux personnes handicapées et la mention du taux de ces places • Cas particuliers des ERP de 5^{ème} catégorie situés dans un cadre bâti existant et des IOP existantes : Délimitation de la partie de bâtiment accessible aux personnes handicapées et indications permettant de s'assurer que les prestations sont accessibles dans cette partie.	8	3
☐ Plans avant travaux s'il s'agit d'un bâtiment existant	9	3
☐ Notice descriptive présentant les points suivants pour expliquer comment le projet prend en compte l'accessibilité (Art. R. 111-19-19 CCH) : • Dimensions des locaux ouverts aux usagers de l'établissement • Caractéristiques fonctionnelles et dimensionnelles des équipements techniques et des dispositifs de commande utilisables par le public • Nature et couleur des matériaux et revêtements de sols, murs et plafonds • Traitement acoustique des espaces • Dispositif d'éclairage des parties communes et, le cas échéant, niveaux d'éclairement et moyens éventuels d'extinction progressive des luminaires S'il s'agit d'un établissement ou d'une installation recevant du public assis : • Emplacements accessibles aux personnes en fauteuil roulant : nombre, taux par rapport au nombre total de places assises, localisation, cheminements permettant d'y accéder depuis l'entrée de l'établissement • Dans le cas d'un établissement recevant du public assis de plus de 1 000 places, l'arrêté municipal fixant le nombre d'emplacements accessibles S'il s'agit d'un établissement disposant de locaux d'hébergement destinés au public • Nombre et caractéristiques des chambres, salles d'eau et cabinets d'aisance accessibles aux personnes handicapées : taux de ces chambres et locaux par rapport au nombre total de chambres, localisation, répartition par catégorie, le cas échéant S'il s'agit d'un établissement ou d'une installation comportant des cabines d'essayage, d'habillage ou de déshabillage ou des douches : • Nombre et caractéristiques des cabines et douches accessibles aux personnes handicapées S'il s'agit d'un établissement ou d'une installation comportant des caisses de paiement disposées en batterie • Nombre de caisses aménagées pour être accessibles aux personnes handicapées et leur localisation	10	3
☐ Dans le cas d'un parking de plus de 500 places, couvert ou non, dépendant d'un établissement recevant du public ou d'une installation ouverte au public : Arrêté municipal prévu à l'article 3 de l'arrêté du 1 ^{er} août 2006 (NOR : SOCU0611478A) fixant le nombre de places de stationnement automobile adaptées et réservées	11	3
☐ La ou les demande(s) de dérogation(s) éventuelle(s), la ou les fiche(s) explicative(s) et tous les documents utiles à leur justification	12	3

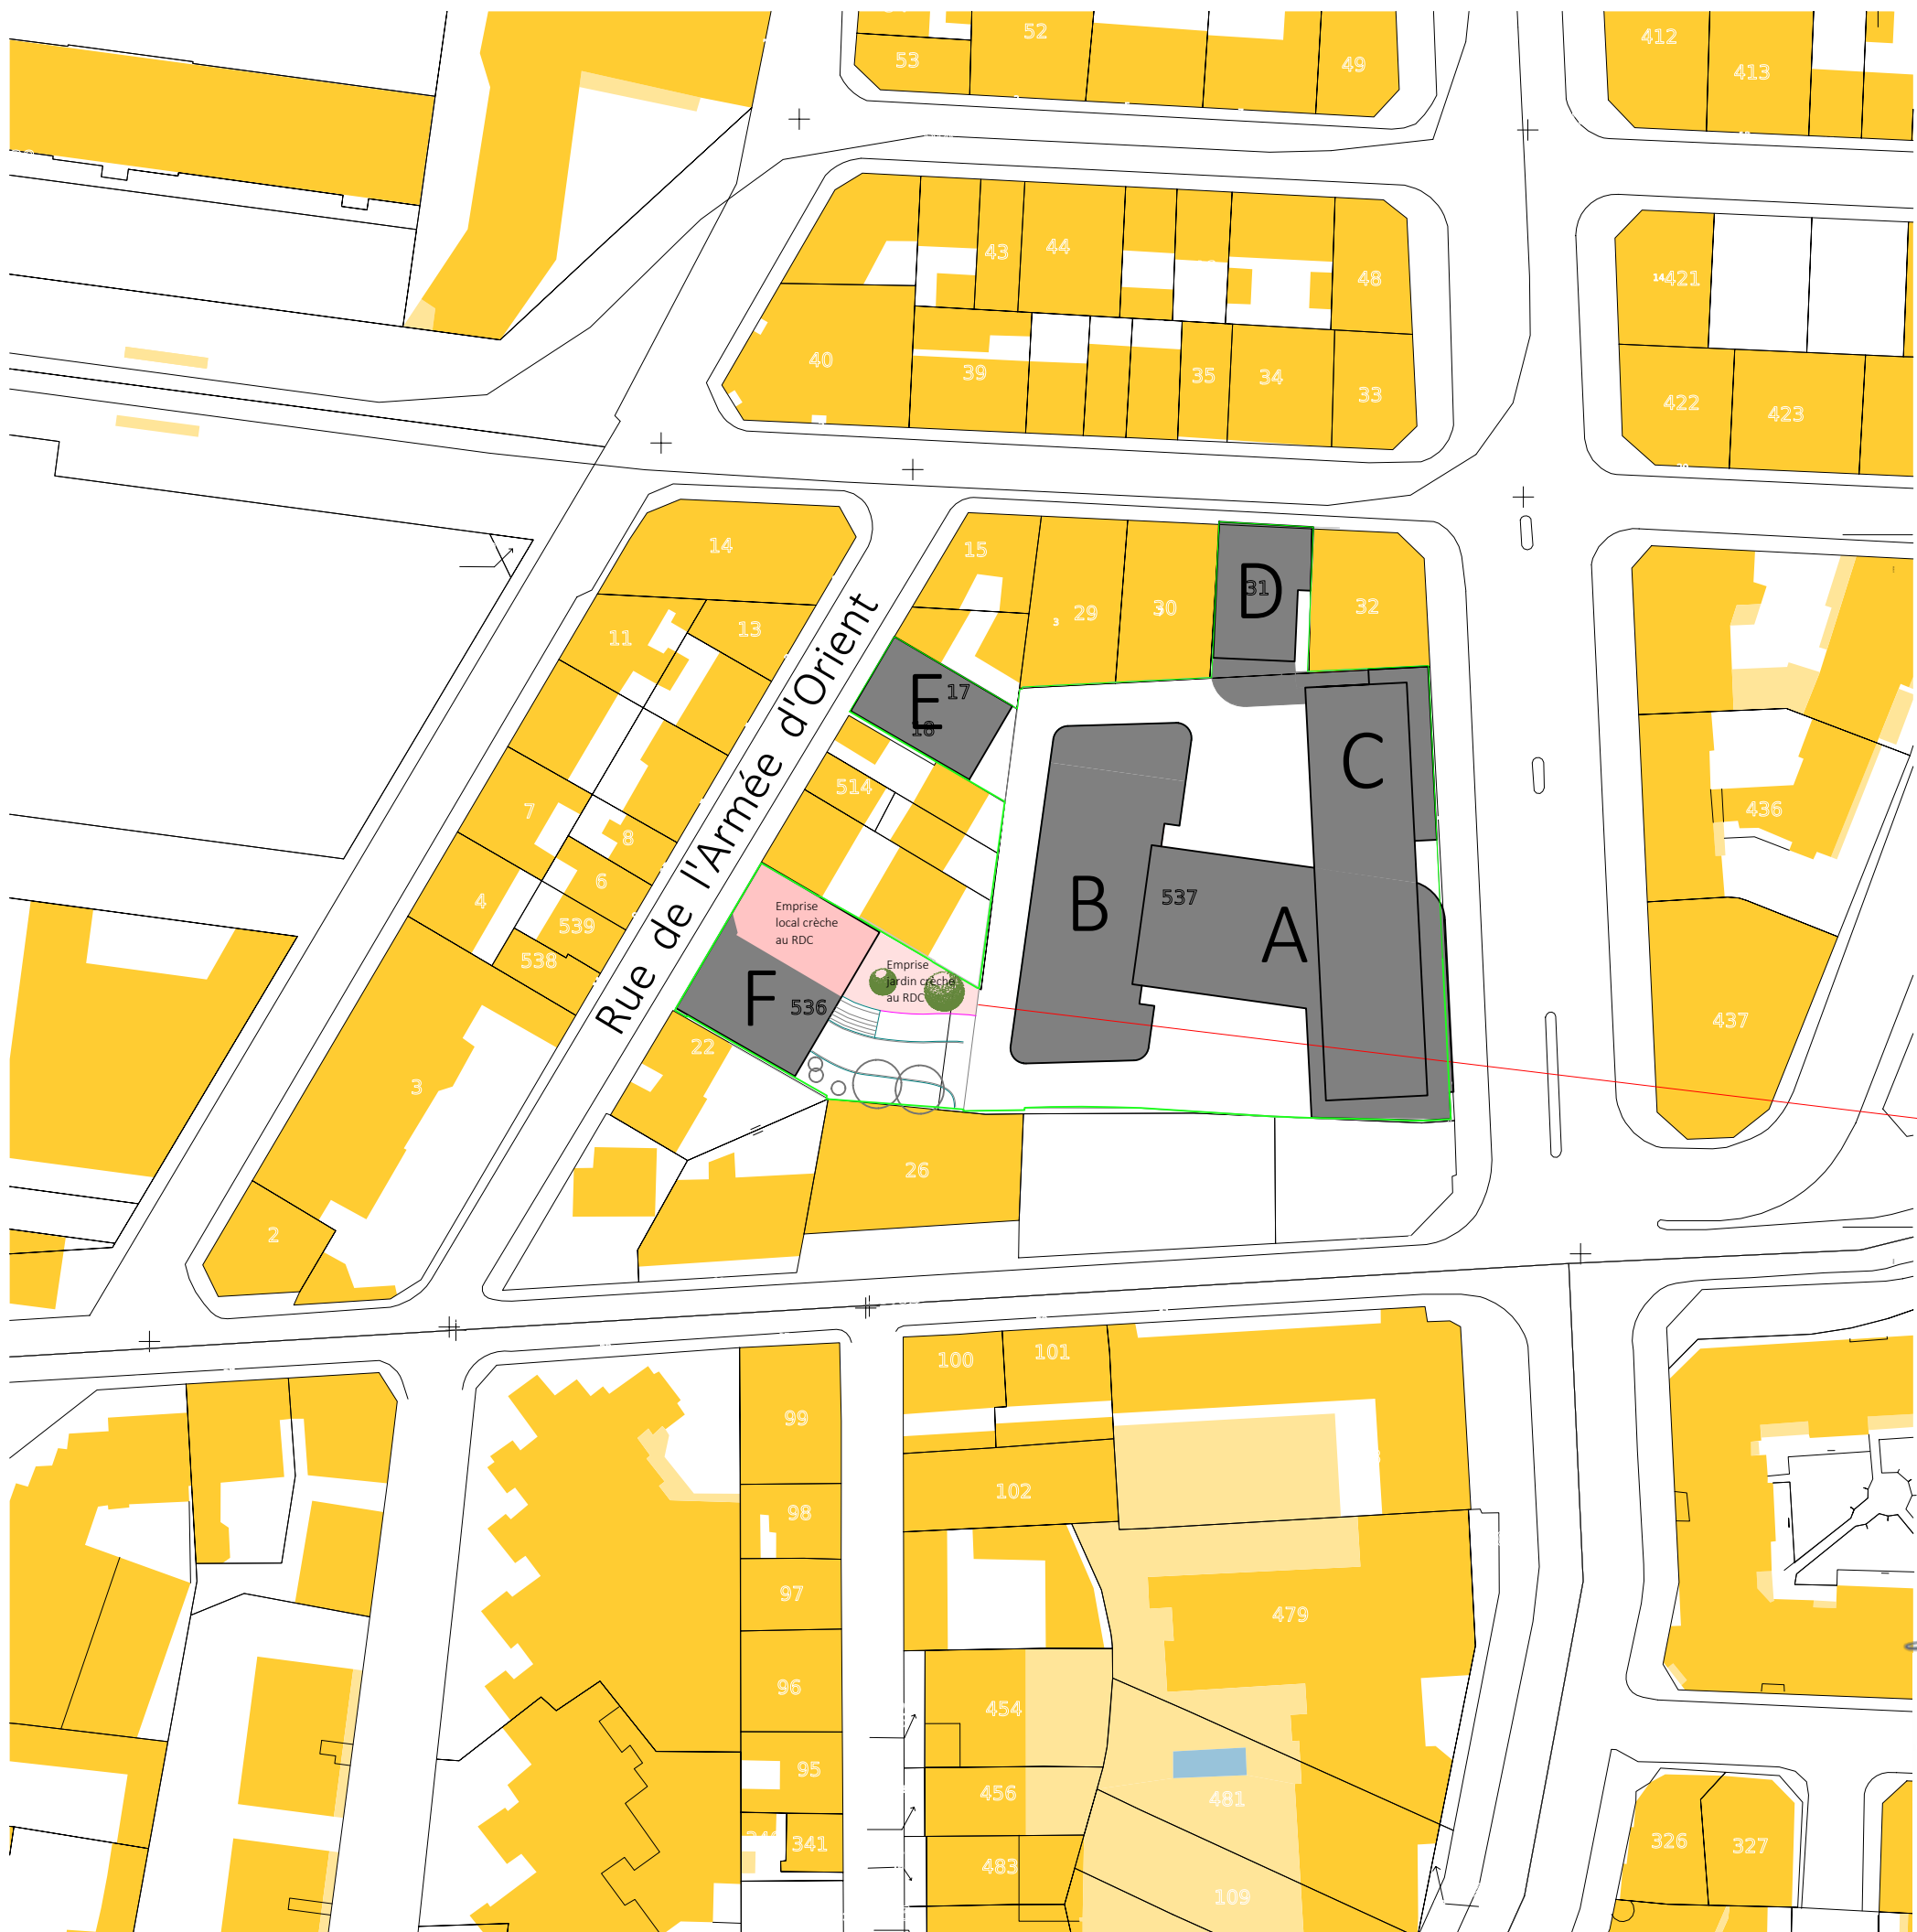

LOCALISATION
DU PROJET DE CRECHE
SITUÉ AU RDC

SAS LES PETITES CANAILLES
Solutions et services petite enfance
36 rue du Pierret
92200 Neuilly sur Seine
RCS Nanterre B 520 223 546
www.lespetitescanailles.fr

MARIN ARCHITECTES
Le Phare - 455 Pde des Anglais
06200 NICE - 04 22 53 34 24
accueil@marin-architectes.fr
sarl au capital de 100000 APE 7112
SIRET 497 900 17 00021
Ordre des architectes PRO 501 354

MAITRISE D'OUVRAGE

Les petites Canailles
36 Rue du Pierret
92200 NEUILLY SUR SEINE



MAITRISE D'OEUVRE

ARCHITECTES

MARIN ARCHITECTES
Le Phare
455 Promenade des Anglais -
06299 NICE CEDEX
T : 04 22 53 34 24



ECONOMIE DE LA CONSTRUCTION

SARL EXECO
196 Chemin du Terron
06200 NICE
sarl.execo@sfr.fr



BUREAU DE CONTROLE

APAVE
AGENCE NICE
22-26 Av. Edouard Grinda, 06200 Nice
T : 04 92 29 40 50



Les petites Canailles
8 Rue Armée de l'Orient
06300 NICE


PROJET
D'AMENAGEMENT
D'UNE CRECHE

Demande
d'autorisation
d'aménager
un ERP

n° pièce : 02

Plan de situation

ECHELLE	1/1000
DATE :	MAI 2022

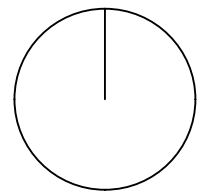

Rue Albert Voisin

Rue de l'Armée d'Orient

Boulevard St Roch

Avenue des Diablos Bleus



MARIN ARCHITECTES
le phare, 455 Pde des Anglais
06200 NICE - 04 22 53 34 24
accueil@marin-architectes.fr
sarl execo SARL APE 7112Z
SIRET 492 900 17 00021
ordre des architectes PRO 601 361

MAITRISE D'OUVRAGE

Les petites Canailles
36 Rue du Pierret
92200 NEUILLY SUR SEINE



Les Petites Canailles
Crèches et Écoles Montessori Bilingues

MAITRISE D'OEUVRE

ARCHITECTES

MARIN ARCHITECTES
Le Phare
455 Promenade des Anglais -
06299 NICE CEDEX
T : 04 22 53 34 24



ECONOMIE DE LA CONSTRUCTION

SARL EXECO
196 Chemin du Terron
06200 NICE
sarl.execo@sfr.fr



BUREAU DE CONTROLE

APAVE
AGENCE NICE
22-26 Av. Edouard Grinda, 06200 Nice
T : 04 92 29 40 50



Les petites Canailles
8 Rue Armée de l'Orient
06300 NICE

PROJET
D'AMENAGEMENT
D'UNE CRECHE


Demande
d'autorisation
d'aménager
un ERP

n° pièce : 04

Plan de masse
Existant

ECHELLE 1/500

DATE : MAI 2022

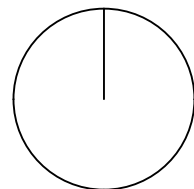


Rue Albert Voisin

Rue de l'Armée d'Orient

Boulevard St Roch

Avenue des Diablos Bleus

MARIN ARCHITECTES
Le Phare - 455 Pde des Anglais
06200 NICE - 04 22 53 34 24
accueil@marin-architectes.fr
sarl.execo@ncc.fr APE 7111Z
SIRET 492 900 137 00021
ordre des architectes PRO 501 354

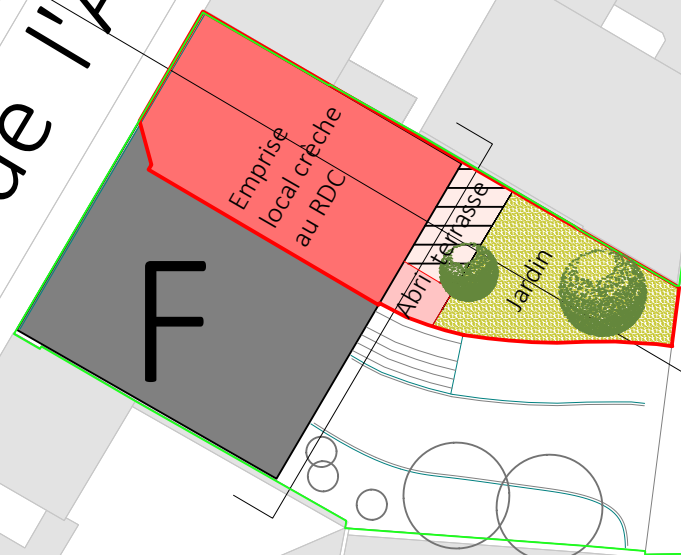

MAITRISE D'OUVRAGE

Les petites Canailles
36 Rue du Pierret
92200 NEUILLY SUR SEINE



Les petites Canailles
Crèches et Écoles Montessori Bilingues

MAITRISE D'OEUVRE

ARCHITECTES

MARIN ARCHITECTES
Le Phare
455 Promenade des Anglais -
06299 NICE CEDEX
T : 04 22 53 34 24



ECONOMIE DE LA CONSTRUCTION

SARL EXECO
196 Chemin du Terron
06200 NICE
sarl.execo@sfr.fr



BUREAU DE CONTROLE

APAVE
AGENCE NICE
22-26 Av. Edouard Grinda, 06200 Nice
T : 04 92 29 40 50



Les petites Canailles
8 Rue Armée de l'Orient
06300 NICE

PROJET
D'AMENAGEMENT
D'UNE CRECHE

Demande
d'autorisation
d'aménager
un ERP

n° pièce : 04

Plan de masse
Projet


ECHELLE 1/500

DATE : MAI 2022



FACADE OUEST SUR RUE DE L'ARMEE D'ORIENT - BAT F

Façade modifiée pour le changement de destination d'un local artisanal en crèche de 20 places

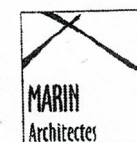

MARIN ARCHITECTES
Le Phare, 455 Pde des Anglais
06200 NICE - 04 22 53 34 24
accueil@marin-architectes.fr
sarl.aucapital.0000 APE 7112
SIRET 492 900 117 00021
ordre des architectes PRO 601 364

MAITRISE D'OUVRAGE

Les petites Canailles
36 Rue du Pierret
92200 NEUILLY SUR SEINE



Les petites Canailles
Crèches et Écoles Montessori Bilingues

MAITRISE D'OEUVRE

ARCHITECTES

MARIN ARCHITECTES
Le Phare
455 Promenade des Anglais -
06299 NICE CEDEX
T : 04 22 53 34 24



ECONOMIE DE LA CONSTRUCTION

SARL EXECO
196 Chemin du Terron
06200 NICE
sarl.execo@sfr.fr



BUREAU DE CONTROLE

APAVE
AGENCE NICE
22-26 Av. Edouard Grinda, 06200 Nice
T : 04 92 29 40 50



Les petites Canailles
8 Rue Armée de l'Orient
06300 NICE

PROJET
D'AMENAGEMENT
D'UNE CRECHE

Demande
d'autorisation
d'aménager
un ERP

n° pièce : 05


Elévation sur rue

ECHELLE 1/100

DATE : MAI 2022

LIMITE DE PROPRIETE

LIMITE DE PROPRIETE

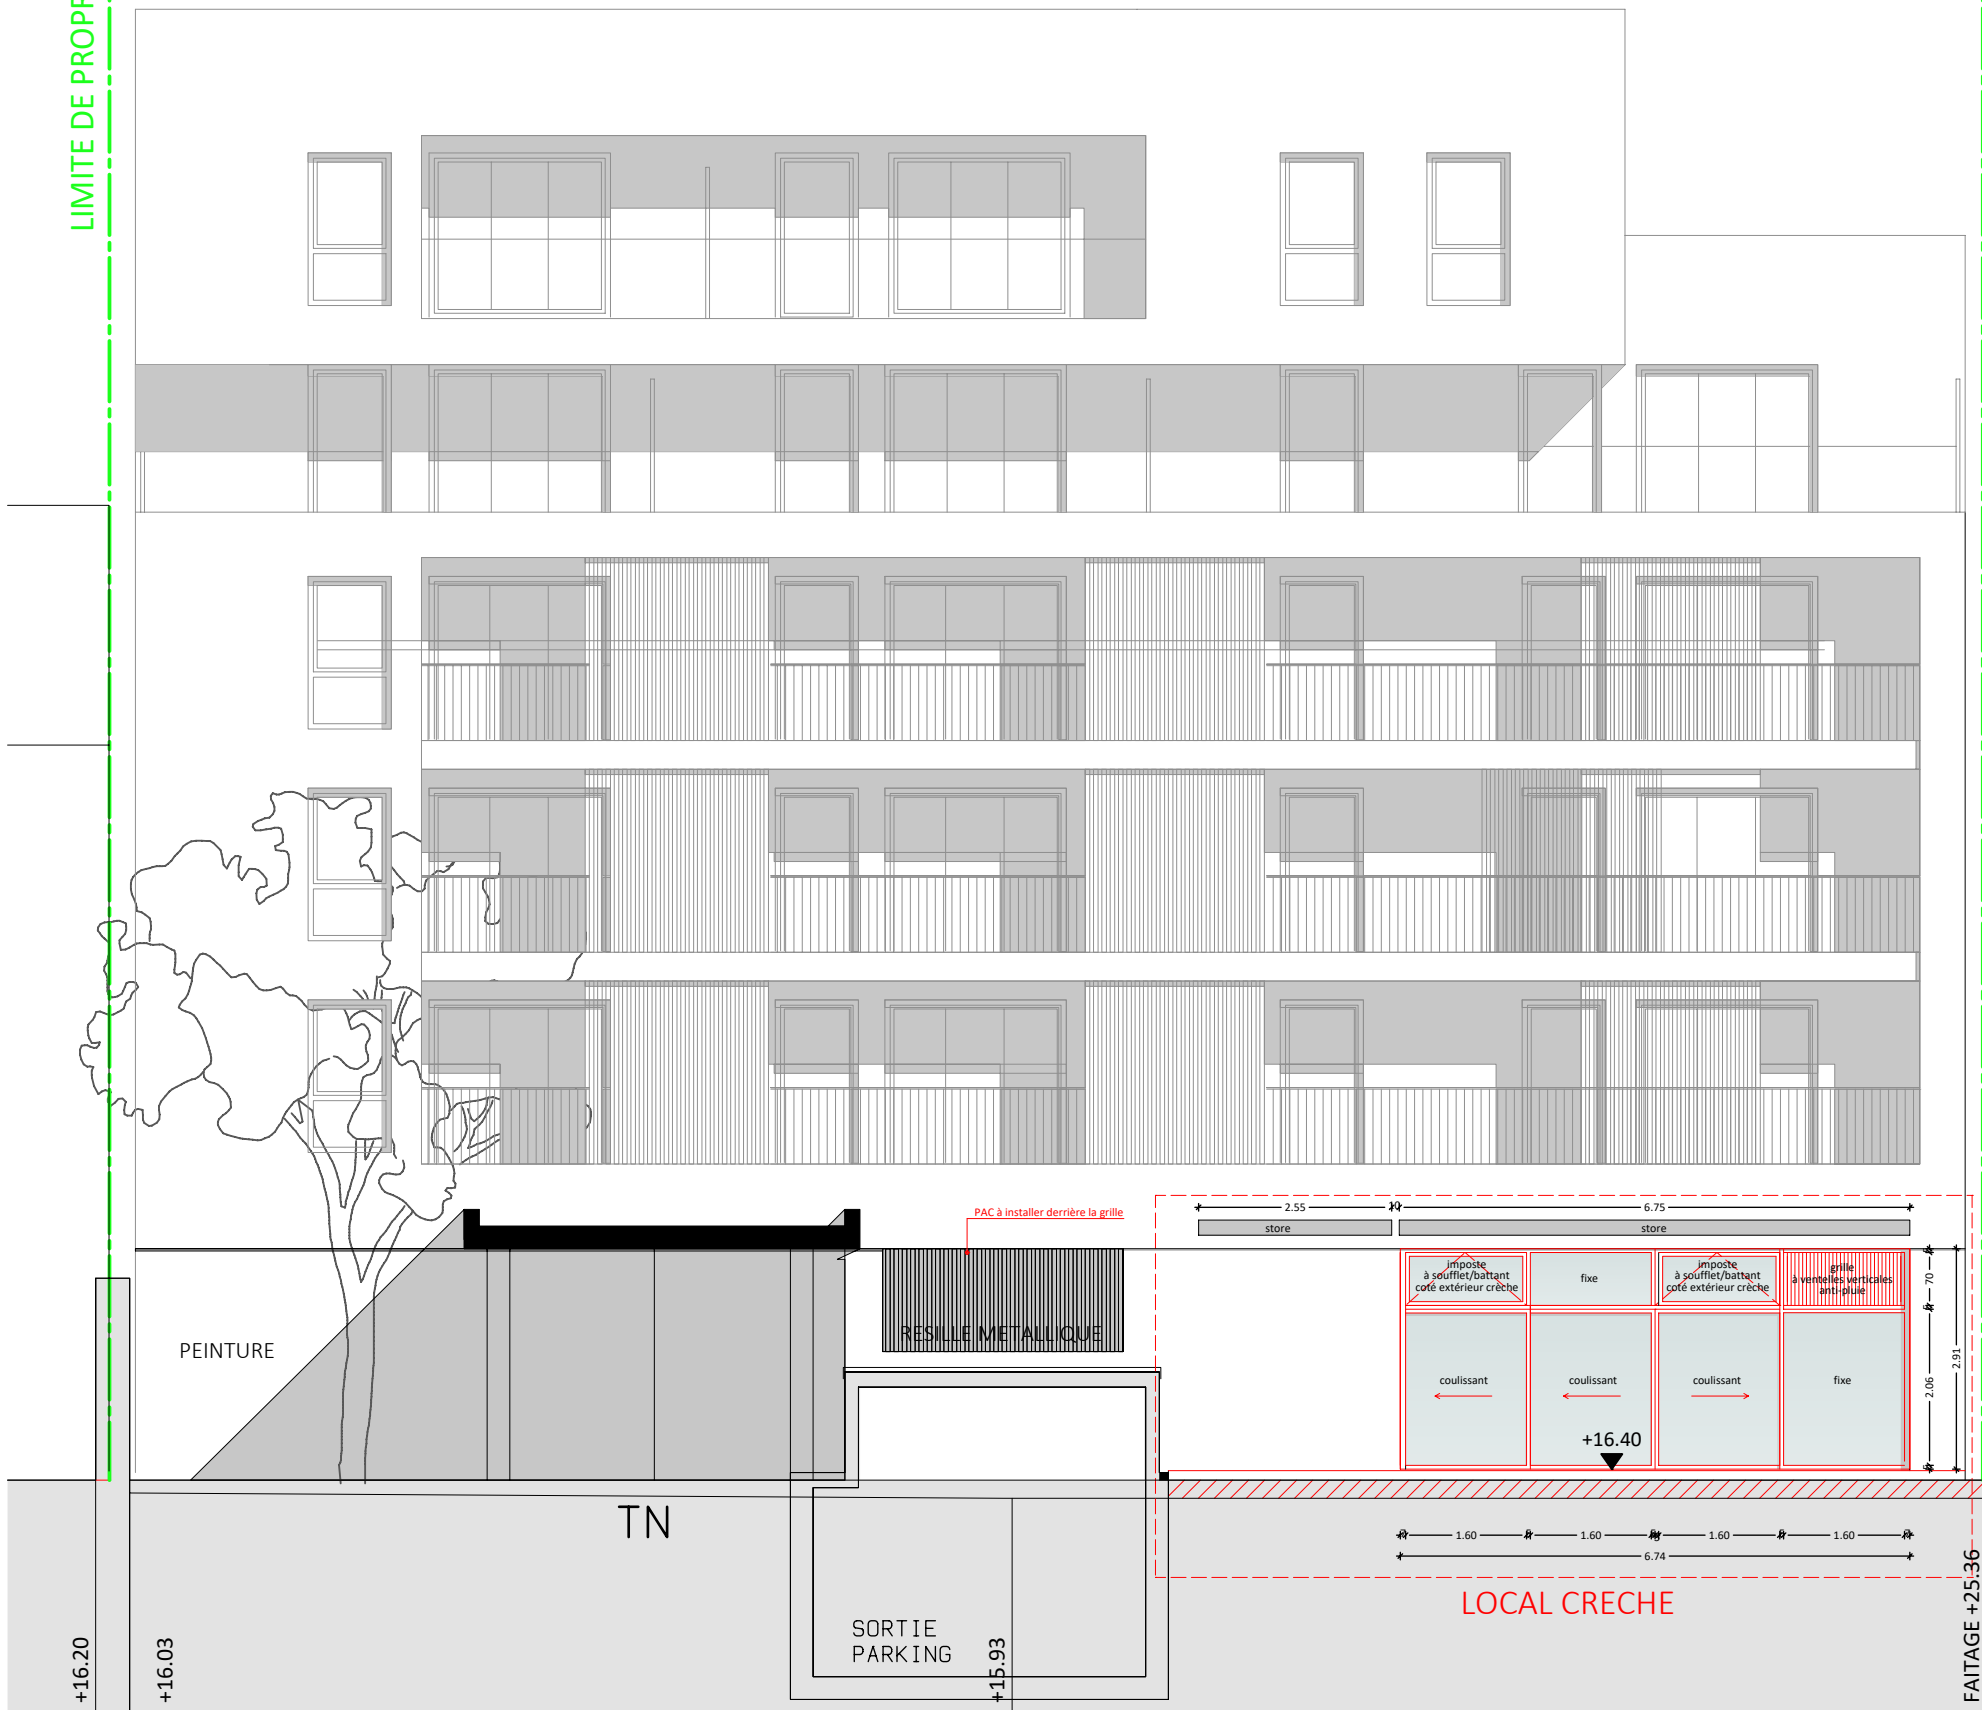

+34.34
Egout

+31.50
R+5

+28.70
R+4

+25.90
R+3

+23.10
R+2


+20.30
R+1

RDC

FAITAGE +25.36

FACADE INTERIEURE EST - BAT F

Façade modifiée pour le changement de destination d'un local artisanal en crèche de 20 places

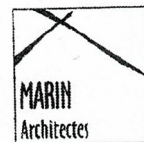

MARIN ARCHITECTES
le Phare - 455 Pde des Anglais
06200 NICE - 04 22 53 34 24
accueil@marin-architectes.fr
sarl au capital de 5000€ APE 7112
SIRET 492 900 137 00021
ordre des architectes PRO 501 354

MAITRISE D'OUVRAGE

Les petites Canailles
36 Rue du Pierret
92200 NEUILLY SUR SEINE



Les Petites Canailles
Crèches et Écoles Montessori Bilingues

MAITRISE D'OEUVRE

ARCHITECTES

MARIN ARCHITECTES
Le Phare
455 Promenade des Anglais -
06299 NICE CEDEX
T : 04 22 53 34 24



ECONOMIE DE LA CONSTRUCTION

SARL EXECO
196 Chemin du Terron
06200 NICE
sarl.execo@sfr.fr



BUREAU DE CONTROLE

APAVE
AGENCE NICE
22-26 Av. Edouard Grinda, 06200 Nice
T : 04 92 29 40 50



Les petites Canailles
8 Rue Armée de l'Orient
06300 NICE

PROJET
D'AMENAGEMENT
D'UNE CRECHE


Demande
d'autorisation
d'aménager
un ERP

n° pièce : 05

Elevation jardin

ECHELLE 1/100

DATE : MAI 2022

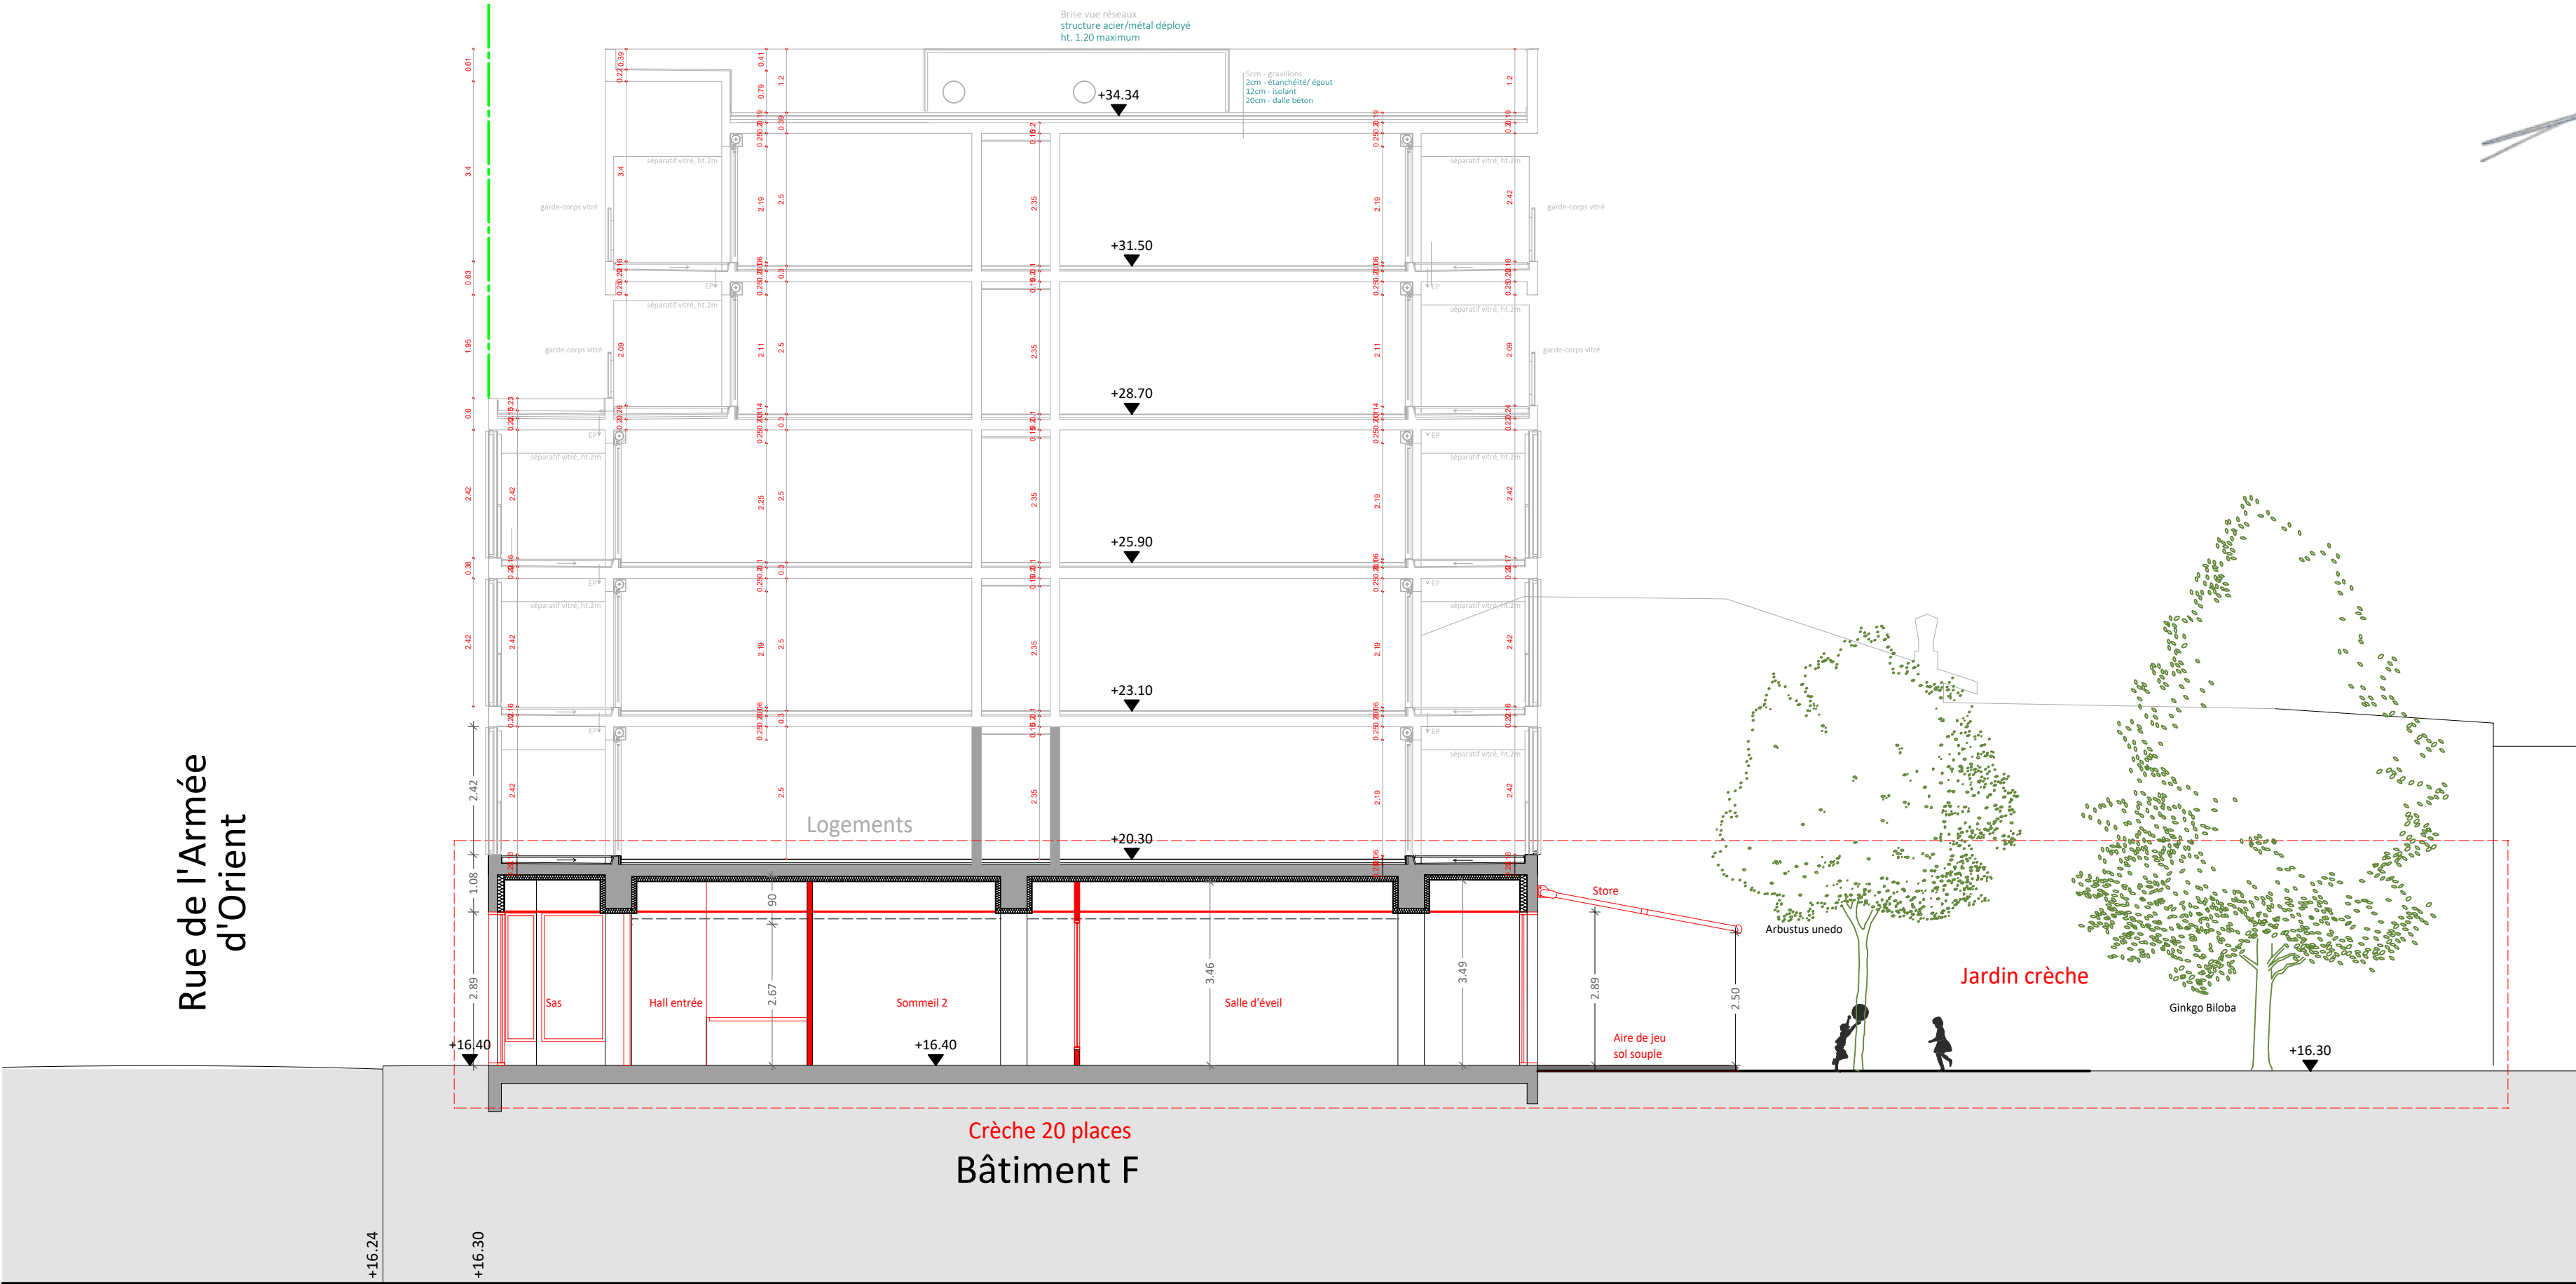

COUPE LONGITUDINALE - BAT F
Coupe modifiée pour le changement de destination d'un local artisanal en crèche de 20 places

A modifier



MARIN ARCHITECTES
Le Phare, 455 Pde des Anglais
06200 NICE - France - 04 22 53 34 24
acc@marin-architectes.fr
sarl@marin-architectes.fr
SIRET 492 900 17 000 21
ordre des architectes PRO 991 354

MAITRISE D'OUVRAGE

Les petites Canailles
36 Rue du Pierret
92200 NEUILLY SUR SEINE



Les Petites Canailles
Crèches et Écoles Montessori Bilingues

MAITRISE D'OEUVRE

ARCHITECTES

MARIN ARCHITECTES
Le Phare
455 Promenade des Anglais -
06299 NICE CEDEX
T : 04 22 53 34 24



ECONOMIE DE LA CONSTRUCTION

SARL EXECO
196 Chemin du Terron
06200 NICE
sarl.execo@sfr.fr



BUREAU DE CONTROLE

APAVE
AGENCE NICE
22-26 Av. Edouard Grinda, 06200 Nice
T : 04 92 29 40 50



Les petites Canailles
8 Rue Armée de l'Orient
06300 NICE

PROJET
D'AMENAGEMENT
D'UNE CRECHE

Demande
d'autorisation
d'aménager
un ERP

n° pièce : 05


Coupe longitudinale

ECHELLE 1/100

DATE : MAI 2022

Rue de l'Armée d'Orient

1

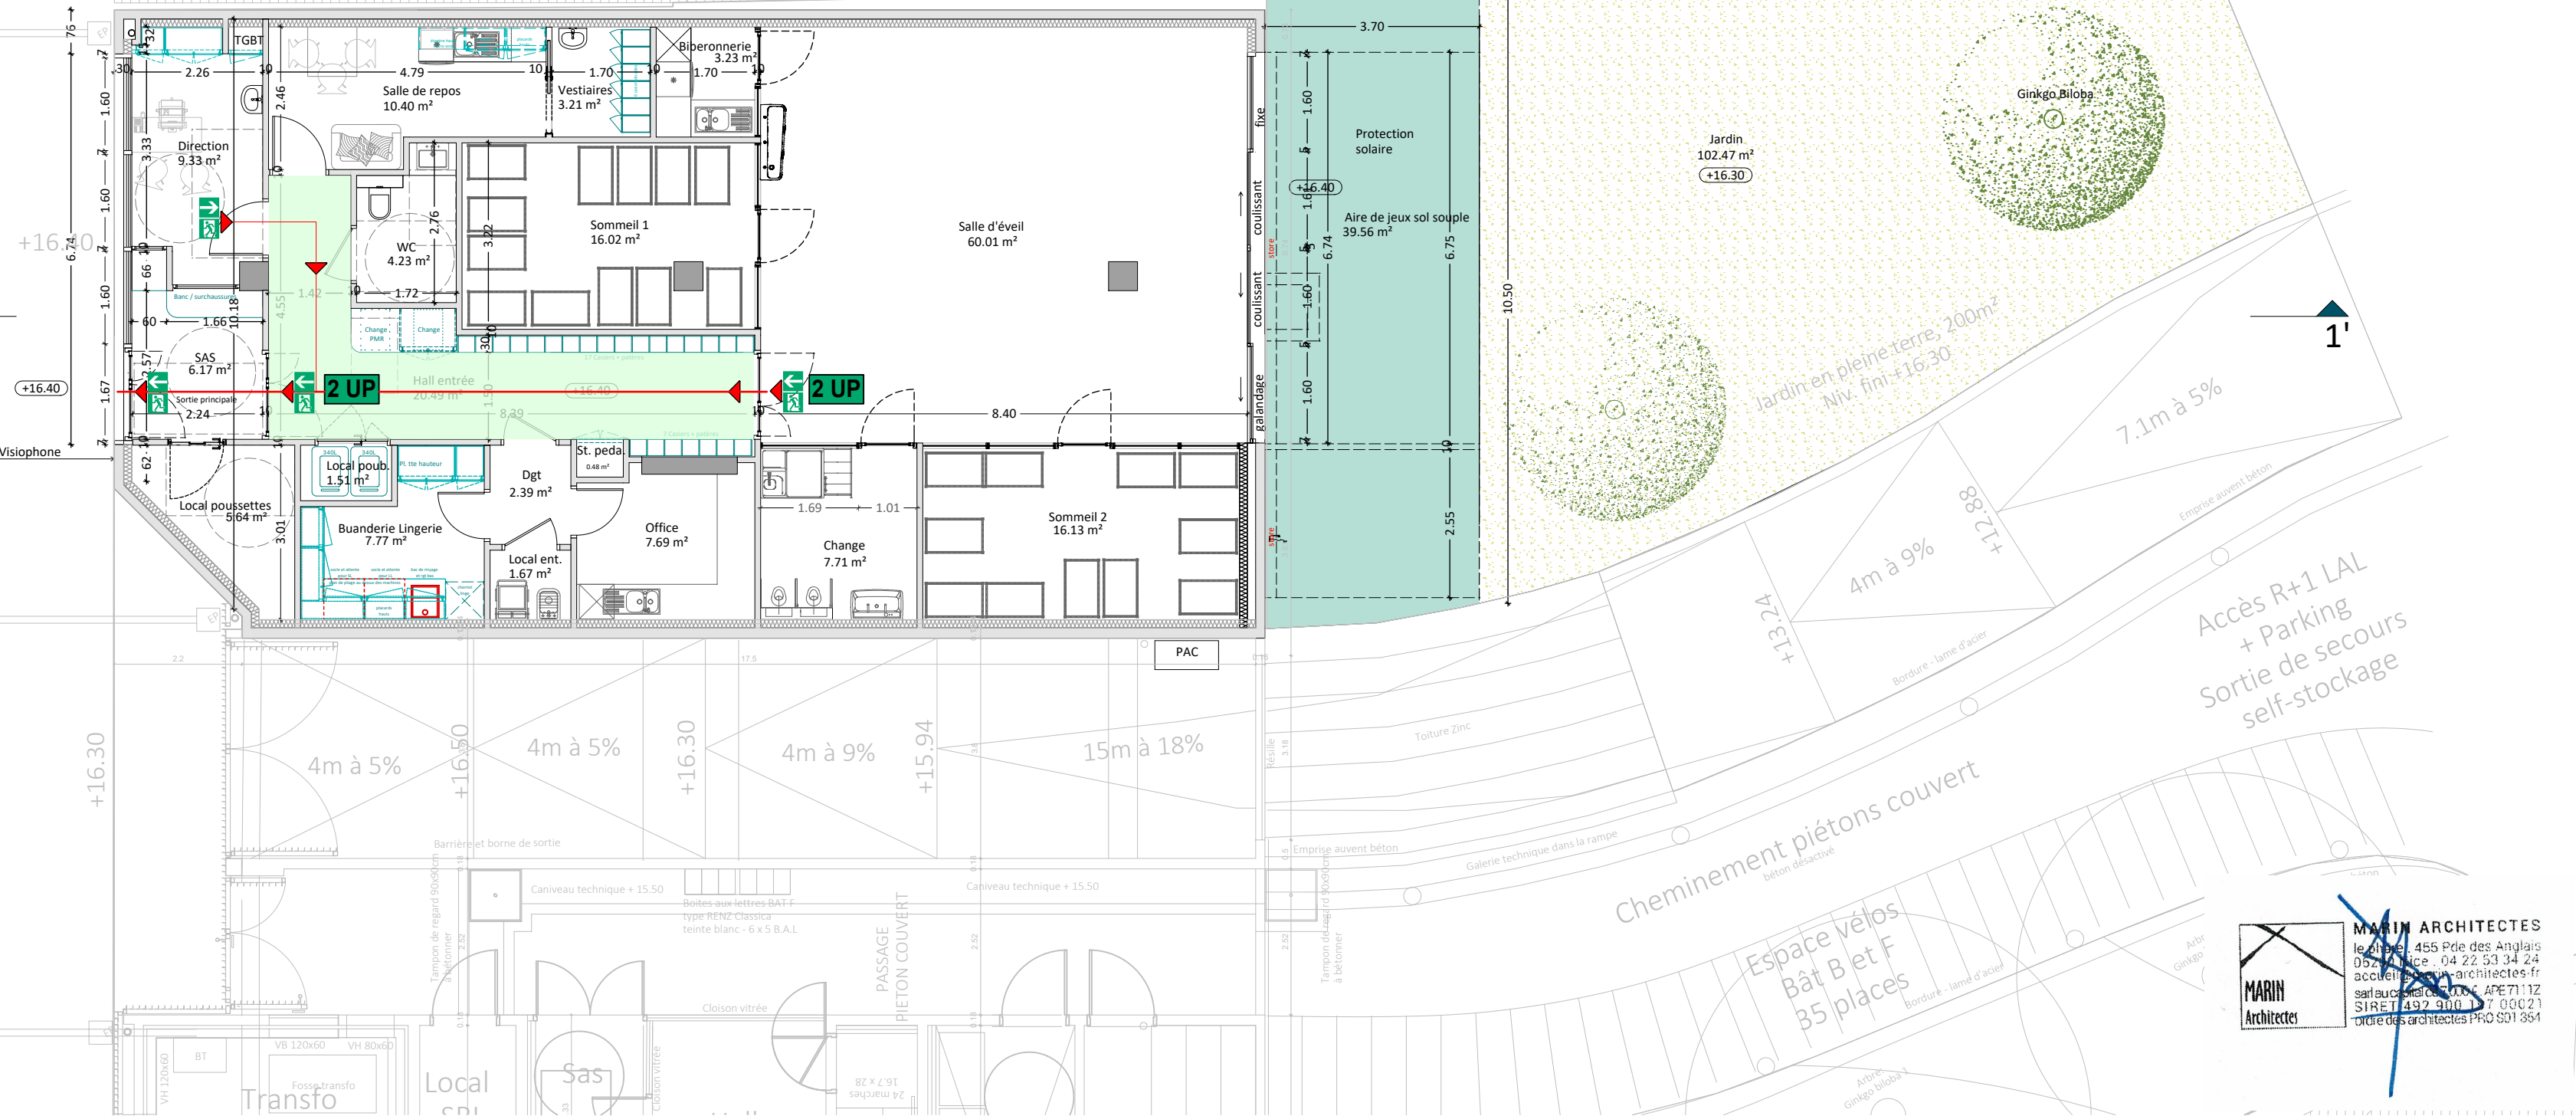

LEGENDE

PLAN DE SECURITE

- NOMBRE D'UNITE DE PASSAGE
- CIRCULATION
- ESPACE D'ATTENTE SECURISE
- CHEMIN ET SENS D'EVACUATION

MAITRISE D'OUVRAGE

Les petites Canailles
36 Rue du Pierret
92200 NEUILLY SUR SEINE

Crèches et Écoles Montessori Bilingues

MAITRISE D'OEUVRE

ARCHITECTES

MARIN ARCHITECTES
Le Phare
455 Promenade des Anglais -
06299 NICE CEDEX
T : 04 22 53 34 24

ECONOMIE DE LA CONSTRUCTION

SARL EXECO
196 Chemin du Terron
06200 NICE
sarl.execo@sfr.fr

BUREAU DE CONTROLE

APAVE
AGENCE NICE
22-26 Av. Edouard Grinda, 06200 Nice
T : 04 92 29 40 50

Les petites Canailles
8 Rue Armée de l'Orient
06300 NICE

PROJET
D'AMENAGEMENT
D'UNE CRECHE


Demande
d'autorisation
d'aménager
un ERP

n° pièce : 05

Plan de niveau
sécurité incendie

ECHELLE	1/100
DATE :	MAI 2022

MARIN ARCHITECTES
Le Phare, 455 Pde des Anglais
06299 NICE - 04 22 53 34 24
accueil@sfr.fr - marin-architectes.fr
sarl aux csi 0004 APE 7112
SIRET 492 900 137 00021
Ordre des architectes PRO S01351

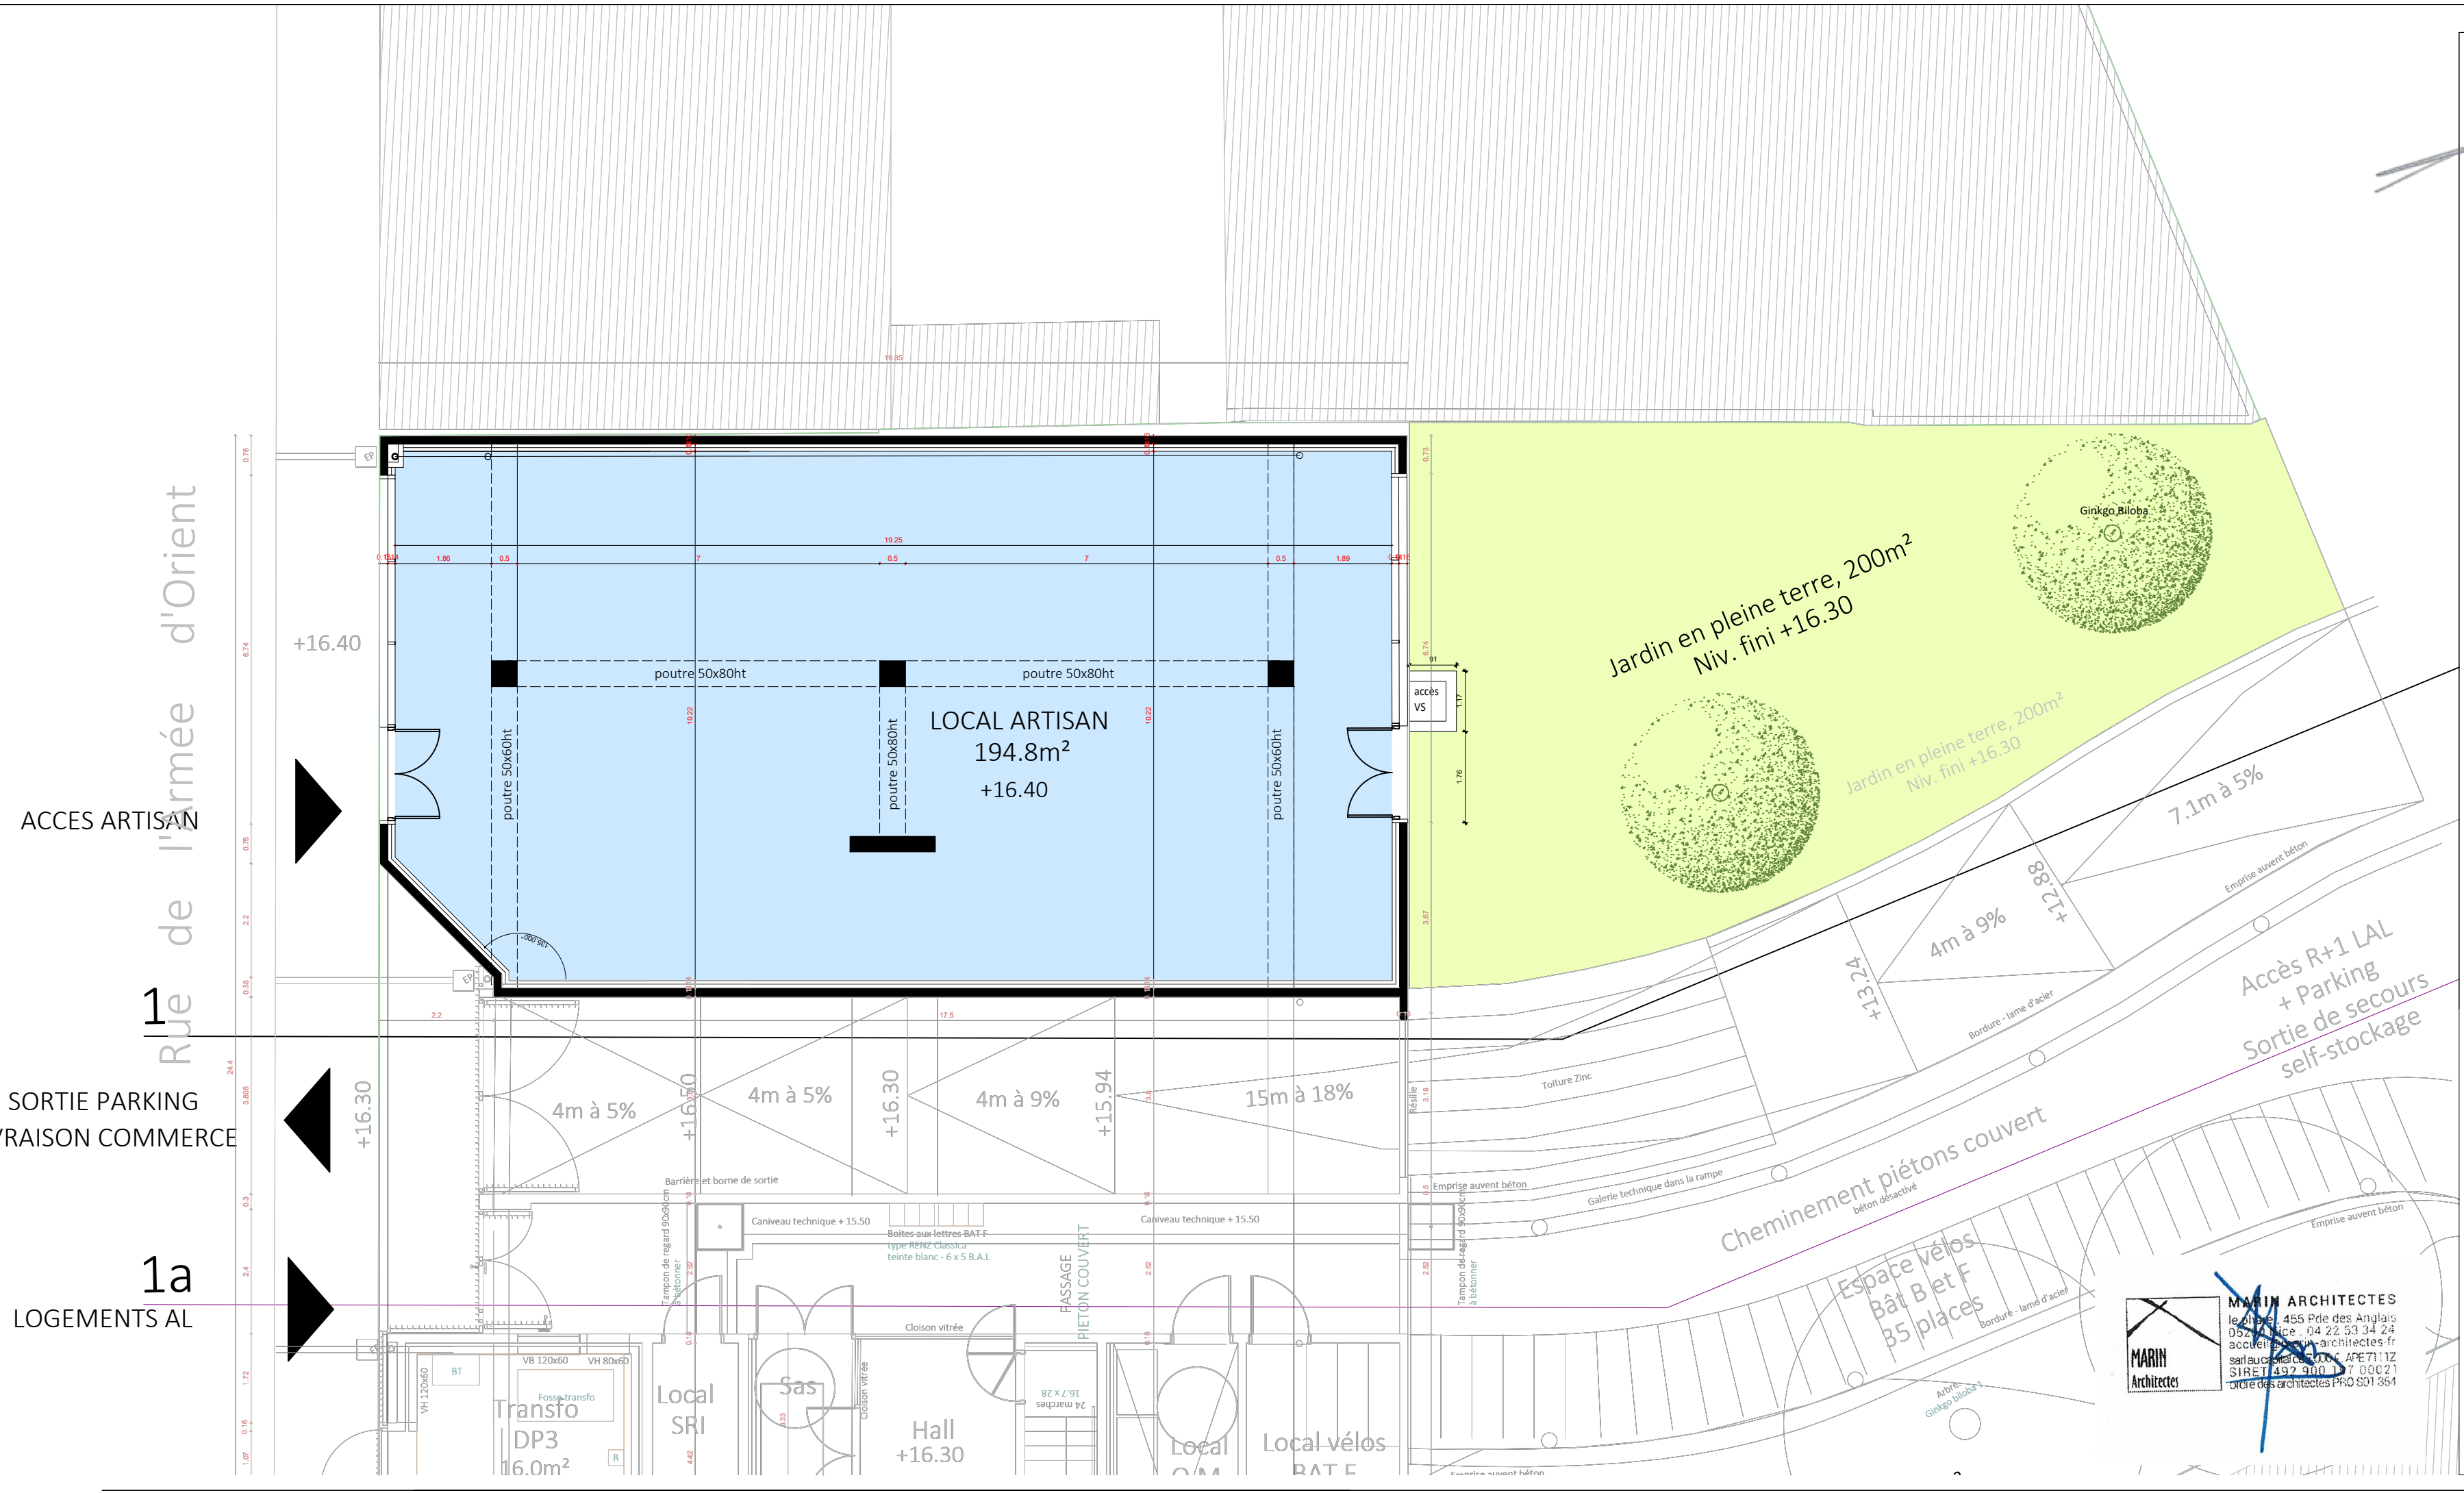

MAITRISE D'OUVRAGE

Les petites Canailles
36 Rue du Pierret
92200 NEUILLY SUR SEINE



MAITRISE D'OEUVRE

ARCHITECTES
MARIN ARCHITECTES
Le Phare
455 Promenade des Anglais -
06299 NICE CEDEX
T : 04 22 53 34 24



ECONOMIE DE LA CONSTRUCTION

SARL EXECO
196 Chemin du Terron
06200 NICE
sarl.execo@sfr.fr



BUREAU DE CONTROLE

APAVE
AGENCE NICE
22-26 Av. Edouard Grinda, 06200 Nice
T : 04 92 29 40 50



Les petites Canailles
8 Rue Armée de l'Orient
06300 NICE

PROJET
D'AMENAGEMENT
D'UNE CRECHE


Demande
d'autorisation
d'aménager
un ERP

n° pièce : 09

Plan état des lieux

ECHELLE 1/100

DATE : MAI 2022

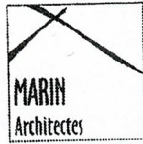


MARIN ARCHITECTES
Le Phare, 455 Pde des Anglais
06299 NICE - 04 22 53 34 24
accueil@marin-architectes.fr
sarlaucn062000112
SIRET 492 900 17 00021
ordre des architectes PRO 501 354

Rue de l'Armée d'Orient



1

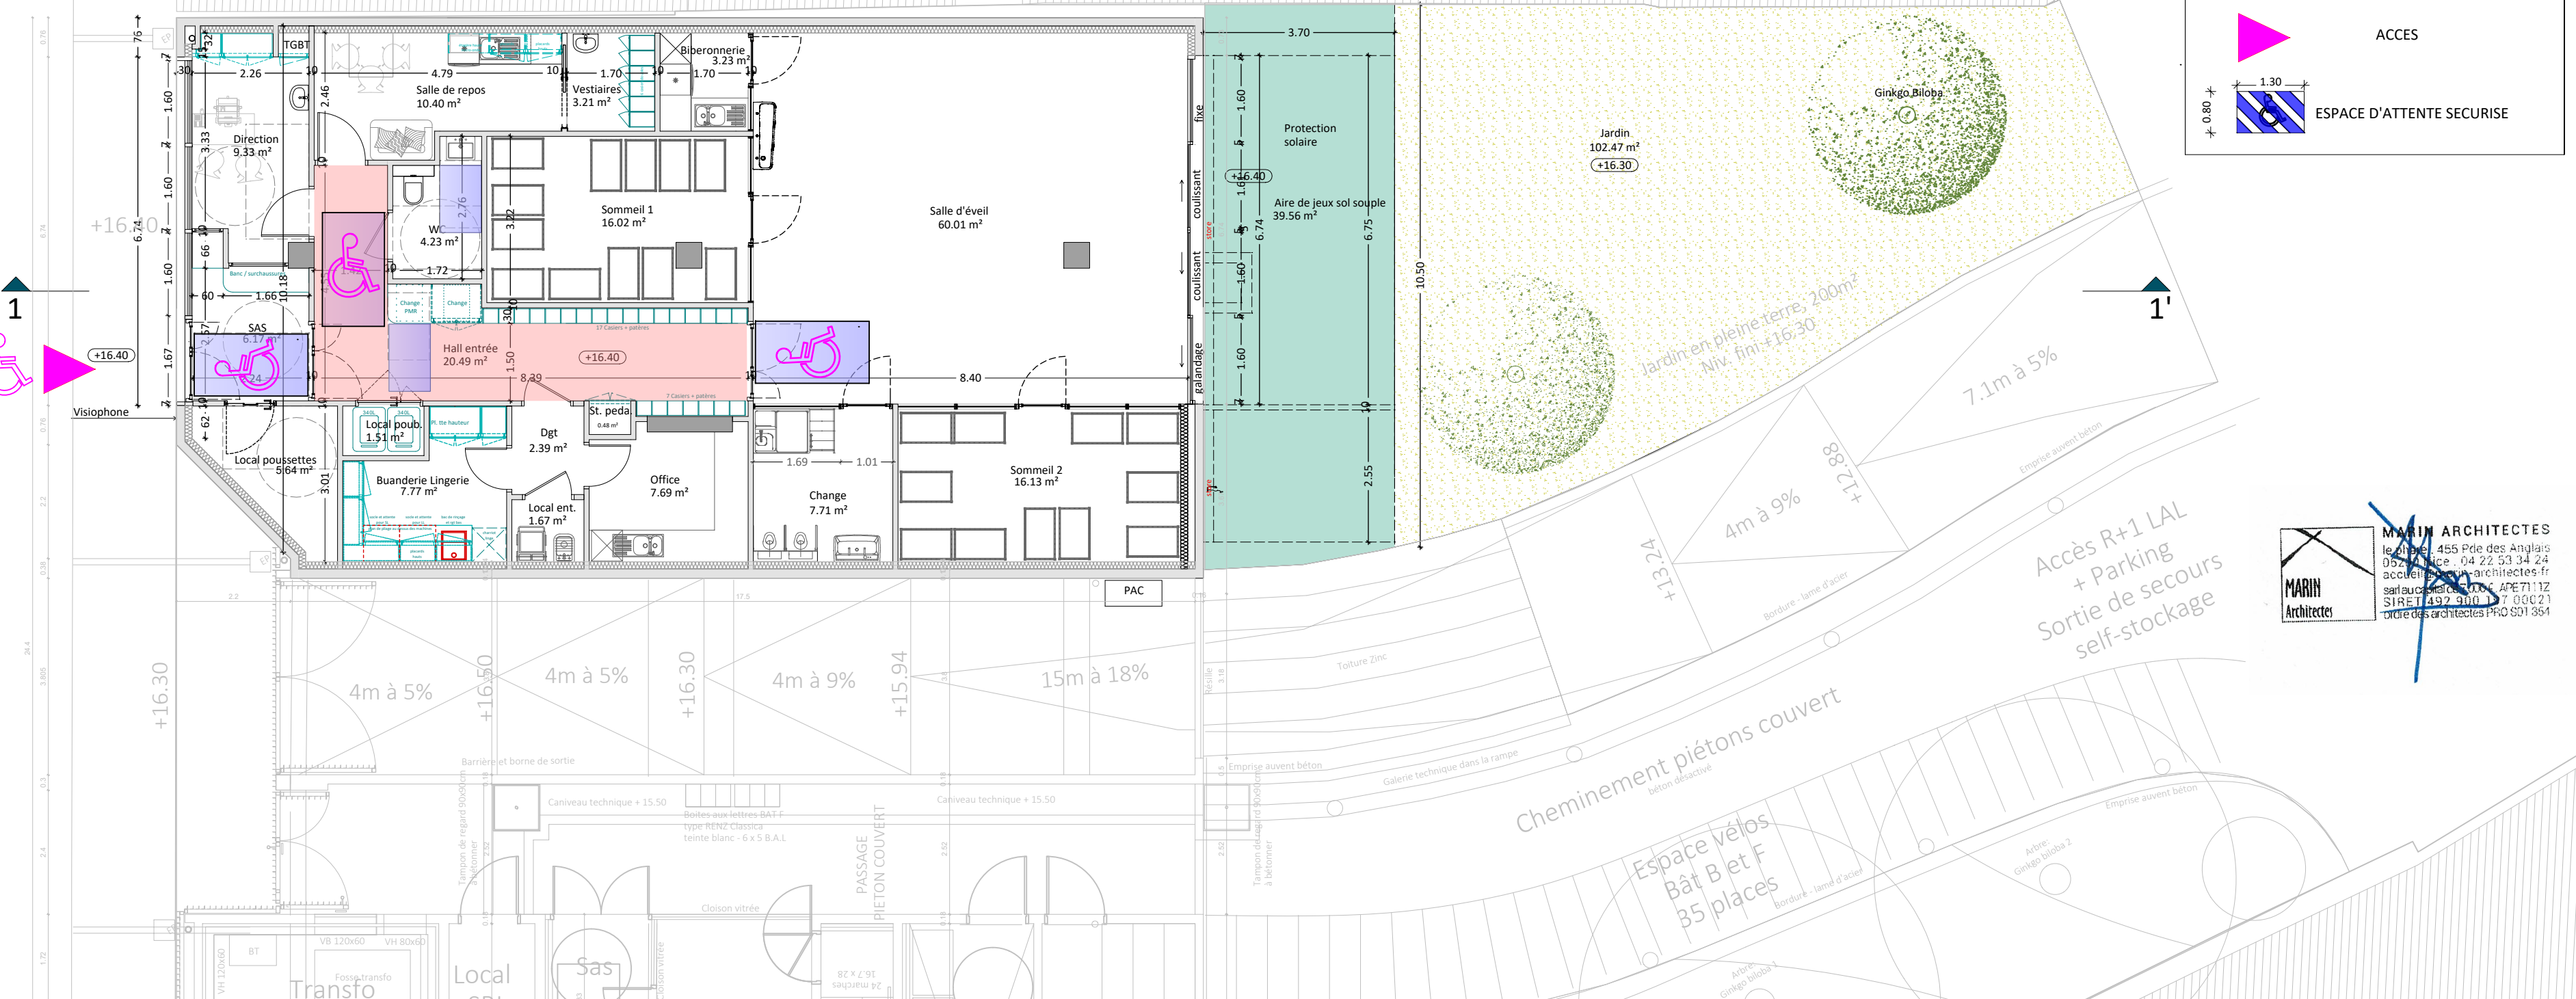

LEGENDE

ESPACES ACCESSIBLES P.M.R.

EMPLACEMENT

ESPACE DE MANOEUVRE PORTE EN TIRANT

CIRCULATION et DEGAGEMENT

ACCES

ESPACE D'ATTENTE SECURISE

MAITRISE D'OUVRAGE

Les petites Canailles
36 Rue du Piérret
92200 NEUILLY SUR SEINE



MAITRISE D'OEUVRE

ARCHITECTES
MARIN ARCHITECTES
Le Phare
455 Promenade des Anglais -
06299 NICE CEDEX
T : 04 22 53 34 24

ECONOMIE DE LA CONSTRUCTION

SARL EXECO
196 Chemin du Terron
06200 NICE
sarlexeco@sfr.fr

BUREAU DE CONTROLE

APAVE
AGENCE NICE
22-26 Av. Edouard Grinda, 06200 Nice
T : 04 92 29 40 50



Les petites Canailles
8 Rue Armée de l'Orient
06300 NICE

PROJET
D'AMENAGEMENT
D'UNE CRECHE

Demande
d'autorisation
d'aménager
un ERP

n° pièce : 07/08

Plan de niveau
accessibilité PMR
extérieur
intérieur

ECHELLE 1/100

DATE : MAI 2022

MARIN ARCHITECTES
le phare, 455 Pde des Anglais
06299 NICE - 04 22 53 34 24
accueil@marin-architectes.fr
sarlexeco@sfr.fr
SIRET 492 900 127 00021
ordre des architectes PNO 501 351

MAITRISE D'OUVRAGE



LES PETITES CANAILLES

36 Rue du Pierret
92200 NEUILLY SUR SEINE

MAITRISE D'OEUVRE

CONCEPTION ARCHITECTURALE

MARIN ARCHITECTES

455 pde des Anglais
Le Phare - 06000 Nice
T : 04 22 53 34 24



ECONOMIE

SARL EXECO

196, Chemin de Terron
06200 NICE
T : 06 64 06 04 40
execo@betexeco.fr



BUREAU DE CONTROLE

APAVE SUDEUROPE SAS

Agence de Nice
AGENCE NICE
22-26 Av. Edouard Grinda,
06200 Nice
T : 04 92 29 40 50

OPERATION :

Demande d'aménager un ERP
À USAGE DE STRUCTURE
D'ACCUEIL DE JEUNES ENFANTS DE
TYPE CRÈCHE 20 BERCEAUX
8, rue de L'Armée d'Orient
06300 NICE

PHASE:

AT
ERP

N° DOC:

N° 10

DATE:

MAI 2022

Notice d'accessibilité aux personnes à mobilité réduite

MODIFICATIONS :

DATE : INDICE :

-		
-		
-		
-		

Objet de la notice :

Cette notice a pour objet de détailler les aménagements extérieurs et intérieur pour ce projet de crèche 30 enfants, en vue de la mise en accessibilité aux personnes à mobilité réduite.

Description du projet :

Le projet est localisé 8 rue de l'Armée d'ORIENT à Nice (06300), et prévoit l'aménagement d'un local à simple rez-de-chaussée recevant moins de 50 personnes pour un effectif de 30 enfants et 19 personnels.

1 Accès principal et cheminement extérieurs :

Le cheminement extérieur sur la voirie n'est pas traité par le projet. L'accessibilité depuis la rue de l'Armée d'Orient se fait au pied de la façade.

L'accès à l'établissement est en continuité avec la rue. L'entrée de l'établissement sera facilement repérable.

L'accès à la crèche se fait par un digicode avec code sur la façade extérieure (commandant la porte du local crèche). Cette commande est installée en façade à la hauteur réglementaire comprise entre 0.90m et 1.30m et décalée de tout angle rentrant.

Les dispositifs de contrôle d'accès sont conformes aux exigences définies à l'annexe 3 et ne sont pas situées dans des zones d'ombre.

Un signal sonore et visuel sera prévu dans le fonctionnement du dispositif d'accès ainsi qu'une mise en relation visuelle des personnes utilisant le dispositif avec le personnel de la crèche (visiophone).

Une issue de secours est installée en façade sur rue de l'établissement. L'accessibilité de cette sortie est assurée par des ressauts de moins de 2 cm.

2. Stationnement :

1 stationnement situé dans les parkings de la résidence Eden Roch Plaza sera dédié au personnel l'établissement. L'équipement ne dispose pas de stationnement pour le public.

L'équipement est situé dans le périmètre « normes de stationnement corridor transport en commun » du PLU Métropolitain.

Le site est desservi par les transports en commun (tramway et bus à proximité).

3. Circulations intérieures horizontales :

Les usagers handicapés pourront accéder à l'ensemble des locaux ouverts au public, les portes d'accès ainsi que les portes intérieurs réservées au public respectent les largeurs de passage de 0,90m.

La largeur minimale des circulations accessibles au public est de 1,40m.

L'ensemble de la crèche dispose d'une planéité de l'ensemble de ses sols.

4. Circulations intérieures verticales :

La crèche est à simple rez-de-chaussée.

5. Revêtements de sols, murs et plafond

Les éventuels tapis permettront la progression du fauteuil roulant.

L'aire d'absorption des revêtements des espaces réservés à l'accueil et à l'attente du public sera supérieure à 25% de la surface du sol.

6. Portes :

Caractéristiques dimensionnelles :

Cet établissement recevra moins de 50 personnes.

Les portes principales ont une largeur minimale de 0.90m.

Les espaces de manœuvre des portes en tirant et en poussant, sont conformes à l'annexe 2. Aucun Les poignées de portes sont utilisables « assis » comme « debout » y compris par une personne ayant des difficultés à saisir et à faire un geste de rotation.

L'extrémité des poignées est située à plus de 0.40m d'un angle rentrant des parois ou tout autre obstacle à l'approche d'un fauteuil roulant.

La porte principale de l'établissement est commandée par un digicode-vidéophone avec voyants lumineux et pictogrammes à l'extérieur et bouton poussoir asservi sur brise-glace verre en cas d'urgence à l'intérieure. Ce dispositif permet une mise en relation visuelle des personnes utilisant le dispositif avec le personnel du centre.

Toutes ces commandes sont situées entre 0.90m et 1.30m du sol fini.

L'effort nécessaire pour ouvrir les portes est inférieur à 50N, que les portes soient équipées ou non de dispositifs de fermeture automatique.

7. Locaux ouverts au public, équipement et dispositifs de commandes

Repérage :

Le mobilier et les équipements sont repérables par contraste visuel avec leur environnement.

Atteinte et usage :

Un espace d'usage conforme aux exigences de l'annexe 2 est prévu au droit de chaque équipement, mobilier, dispositif de commande et de service.

Les éléments de signalisation et d'information répondent aux exigences de l'annexe 3.

8. Hauteur des tables à langer

Les locaux de change sont dimensionnés conformément aux attentes de la PMI pour recevoir une table à langer.

L'espace de change attenant à la salle d'éveil dispose d'une hauteur de +d0.80m offrant une bonne stabilité et une bonne posture aux utilisateurs. La hauteur de la partie supérieure des coussins de change égalera la hauteur finie de +0.83m équivalent à la hauteur des coudes des utilisateurs en position debout. Le poste de change est orienté vers la salle d'activité afin de limiter les retournements pour intervenir sur le groupe et disposent de rebords afin de prévenir les chutes.

Ce poste de change est équipé d'un ensemble vasque/coussin de change comprenant une hauteur libre sous plan de 0.75m minimum et d'une profondeur de 0.65m minimum afin de favoriser l'accessibilité aux personnels à mobilité réduite de la crèche.

9. Sanitaire

Un sanitaire accessible est aménagé. Il présente un espace d'usage de 0.80x1.30m situé latéralement par rapport à la cuvette. Il comporte un espace de manœuvre avec possibilité de demi-tour d'un espace équivalent à un diamètre de 1.50m à l'intérieur et à l'extérieur.

Le sanitaire est équipé d'un ferme porte, il comprend un lave main dont le plan supérieur est situé à 0.85m et un vide en partie inférieure d'au moins 0.30m de profondeur, 0.60m de largeur et 0.70m de hauteur.

La surface d'assise de la cuvette est située à une hauteur comprise entre 0.45 et 0.50m du sol.

Une barre d'appui latérale est prévue à côté de la cuvette, elle est positionnée à une hauteur comprise entre 0.70m et 0.80m.

10. Eclairage

Les dispositifs d'éclairage artificiel répondent aux exigences suivantes :

- 20 lux en tout point du cheminement extérieur accessible
- 200 lux au droit du poste d'accueil
- 100 lux en tout point des circulations intérieures horizontales

Pour les éclairages temporisés, l'extinction est progressive. Pour un fonctionnement avec détection de présence, la détection couvrira l'ensemble de l'espace concerné et deux zones de détection successives chevaucheront. Les systèmes d'éclairage ne provoqueront aucun effet d'éblouissement direct des usagers « assis » comme « debout ».

Fait à Nice, Mai 2022,

Le maître d'ouvrage :

L'architecte :

SAS LES PETITES CANAILLES
Solutions et services petite enfance
36 rue Pierret
92200 Neuilly sur Seine
RCS Nanterre B 520 223 546
www.lespetitescanailles.fr



MARIN ARCHITECTES
le phare, 455 Pde des Anglais
06200 Nice - 04 22 53 34 24
accueil@marin-architectes.fr
sarl au capital de 1000€ APE 7111Z
SIRET 492 900 107 00021
ordre des architectes PRO S01 354

MAITRISE D'OUVRAGE



LES PETITES CANAILLES

36 Rue du Pierret
92200 NEUILLY SUR SEINE

MAITRISE D'OEUVRE

CONCEPTION ARCHITECTURALE

MARIN ARCHITECTES

455 pde des Anglais
Le Phare - 06000 Nice
T : 04 22 53 34 24



ECONOMIE

SARL EXECO

196, Chemin de Terron
06200 NICE
T : 06 64 06 04 40
execo@betexeco.fr



BUREAU DE CONTROLE

APAVE SUDEUROPE SAS

Agence de Nice
AGENCE NICE
22-26 Av. Edouard Grinda,
06200 Nice
T : 04 92 29 40 50

OPERATION :

Demande d'aménager un ERP
À USAGE DE STRUCTURE
D'ACCUEIL DE JEUNES ENFANTS DE
TYPE CRÈCHE 20 BERCEAUX
8, rue de L'Armée d'Orient
06300 NICE

PHASE:

AT
ERP

N° DOC:

N° 3

DATE:

MAI 2022

Notice de sécurité

MODIFICATIONS :

DATE : INDICE :

-
-
-
-

1. PRÉSENTATION ET CLASSEMENT :

Cette notice a pour objet de détailler les aménagements extérieurs et intérieur pour ce projet de crèche 30 places, en vue de la mise en accessibilité aux personnes à mobilité réduite.

Description du projet :

Le projet est localisé 8 rue de l'Armée d'Orient à Nice (06300), et prévoit l'aménagement d'un local à simple rez-de-chaussée d'un effectif total de 49 personnes pour un effectif de 30 enfants et 19 pour le personnel.

En application de l'article R2 de l'Arrêté du 25 juin 1980, l'effectif du public admis au sein de la crèche est déterminé par déclaration du maître d'ouvrage à 30 enfants au plus et à 19 personnels.

L'effectif total est de 49 personnes.

L'établissement est donc classé en type R de 4ème catégorie.

Les travaux sont donc soumis aux dispositions de l'Arrêté du 22 juin 1990 modifié et du code du travail.

2. DESSERTE ET ISOLEMENT :

Les planchers haut et bas, les parois verticales sont Coupe-Feu 1H (livrés tel quel).

La façade d'entrée de l'établissement donne sur la rue.

L'établissement est directement accessible de plain pied depuis cette voie.

Le Sas donne alors accès de plain pied au hall de la crèche par le biais d'une porte à deux vantaux tiercés (largeur totale de 1,40m dont un vantail de 0,90m minimum). Cette porte sera équipée d'une ouverture automatique en cas de coupure de courant ou de déclenchement du boîtier brise glace à proximité.

Une sortie secondaire côté jardin, permet d'accéder aux espaces extérieurs accessibles aux enfants.

Cet accès aux espaces extérieurs de la crèche permet également un dégagement en cas d'urgence.

3. CONSTRUCTION ET DÉGAGEMENT

Le bâtiment comprend les logements à l'étage, le plancher haut du Rez-de-chaussée est Coupe-Feu 1H minimum.

L'établissement n'a pas de cul-de-sac. Les portes de la salle de repos sont situées à moins de 10 mètres d'un choix entre deux sorties (principale ou secondaire).

La section ou salle d'éveil peut recevoir plus de 19 personnes et moins de 50. Elle dispose d'une sortie.

Les 2 salles de repos accueillent moins de 19 personnes chacune.

La porte extérieure de l'établissement ouvrent dans le sens de l'entrée.
La distance de tout point de l'établissement pour gagner une sortie est inférieure à 50mètres.

La porte secondaire ouvrant sur le jardin est un ouvrant coulissant.

Les locaux à risques particuliers suivants seront créés dans l'établissement :

- Local Déchets,
- Local Entretien,
- Cuisine (office de remise en température au sens de l'article PE 17),
- Buanderie/Lingerie,

Ils seront isolés des locaux et circulations accessibles au public au moyen de parois coupe-feu de degré 1 heure et blocs-portes Coupe-Feu de degré ½ heure dotés de ferme-portes, suivant l'article PE9. Ces portes disposeront de la mention « Porte Coupe-Feu à maintenir fermée »

4. AMÉNAGEMENTS INTÉRIEURS :

Les aménagements mis en œuvre au sein de l'établissement respecteront les prescriptions minimales suivantes visant leur réaction au feu :

- revêtements de sol des circulations horizontales : M4 et solidement fixés ;
- revêtements muraux des locaux et des circulations : M2 au moins ;
- isolants en contact direct avec l'air (non protégés par un écran thermique stable au feu ¼ heure) : M1 ;
- plafonds, faux-plafonds et isolants dans faux-plafonds : M1 ;
- gros mobilier : M3 ;

Il n'y aura pas de tentures, voilages ou rideaux en travers des dégagements.

5. DÉSENFUMAGE


En application de l'article PE14, en l'absence de locaux de plus de 300 m², aucun désenfumage n'est requis.

6. CHAUFFAGE ET VENTILATION :

Une centrale de traitement d'air double flux installée en plenum du local, permettra de souffler et d'extraire dans les salles de vie. La prise d'air neuf se fera à l'aide d'une grille en façade sur jardin. La gaine d'extraction cheminera en plafond du local et débouchera au niveau de la grille en façade, rejetant l'air à l'extérieur, coté rue à RDC.

Une seconde centrale simple flux spécifique permettra d'extraire le local déchets et les locaux lingerie et buanderie à l'aide d'une gaine. La gaine d'extraction cheminera en plafond du local et débouchera au niveau de la grille en façade, rejetant l'air à l'extérieur, coté rue à RDC.

Les locaux seront chauffés et rafraîchis par une PAC. Les moteurs de la PAC seront installés sur le voile béton situé entre le local de la crèche et la rampe de parking.

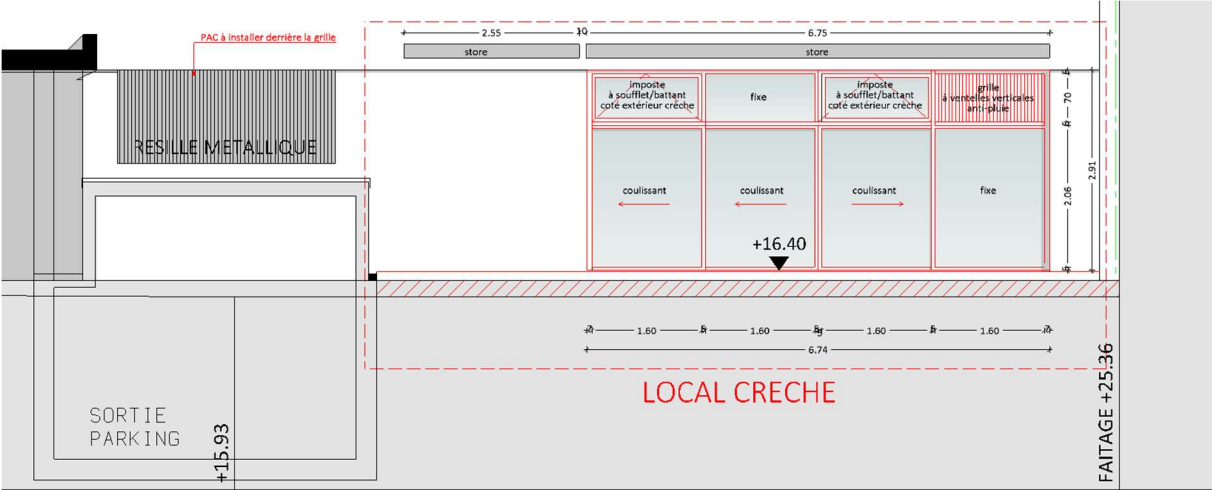

Extrait de la façade sur jardin

Position de la PAC dans la sortie de parking derrière la grille métallique



7. INSTALLATIONS ELECTRIQUES :

Les installations électriques seront conformes aux normes françaises les concernant. Il ne sera pas fait usage de canalisations propageant la flamme ni de douilles voleuses ou de fiches multiples.

Les installations ne comporteront que des canalisations fixes. Les canalisations mobiles éventuelles alimentant les appareils ne feront pas obstacle à la circulation du public.

L'éclairage de sécurité d'évacuation des dégagements conduisant le public vers l'extérieur sera assuré par blocs autonomes d'éclairage de sécurité.

Un dispositif de coupure générale des installations électriques de l'établissement sera mis en place. Il sera inaccessible au public et facile à atteindre en partant de la voie publique (bureau directrice).

Un dispositif assurant la coupure de l'alimentation électrique et de la ventilation sera prévu à proximité de l'entrée de l'établissement (bureau directrice).

7. MOYENS DE SECOURS ET D'ALERTE :

La défense intérieure contre l'incendie sera assurée par :

- des extincteurs à eau pulvérisée de 6 litres au moins, disposés tous les 200 m² de façon à avoir moins de 15 mètres à parcourir pour en atteindre un ;
- des extincteurs adaptés aux risques à proximité des risques particuliers (armoires électriques, office de réchauffage, etc.).

Un plan facilitant l'intervention des services de secours sera affiché à toutes les entrées de l'établissement (principale et secondaire). Il indiquera, en particulier, l'emplacement de toutes les coupures ayant une fonction de sécurité.

Il est prévu la mise en place d'un équipement d'alarme de type 4 semblable ou équivalent à un SSI E.

En application de la réglementation en vigueur (R13§2 et MS 60) un SSI de catégorie E associé à un équipement d'alarme de type 4 est apte à commander le déverrouillage des issues de secours.

Un flash lumineux sera installé dans le sanitaire PMR.

La liaison avec les sapeurs-pompiers sera assurée par la téléphonie sur fibre (téléphone par internet). La continuité de service en cas de coupure d'électricité sera assurée par un onduleur.

Fait à Nice, Mai 2022,

Le maître d'ouvrage :

L'architecte :

SAS LES PETITES CANAILLES .
Solutions et services petite enfance
36 rue Pierrat
92200 Neuilly sur Seine
RCS Nanterre B 520 223 546
www.lespetitescanailles.fr



MARIN ARCHITECTES
le phare . 455 Pde des Anglais
06200 Nice . 04 22 53 34 24
accueil@marin-architectes.fr
sarl au capital de 2000€ APE 7111Z
SIRET 492 900 137 00021
ordre des architectes PRC 501 354