


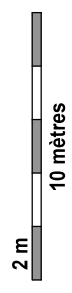

LÉGENDE

- Assiette foncière de la copropriété
- Parties communes générales
- Parties communes spéciales bâtiment DANUBE
- Parties communes spéciales bâtiment NIL
- Parties communes spéciales Bâtiment PARKING
- Parties communes spéciales lots cage DANUBE
- Parties communes spéciales lots cage NIL
- Parties communes spéciales lots d'appartement



Jocelyne FOREST & ASSOCIÉS
Géomètres Experts

Siège social Levallons-Perret :
88 rue du 19-23 octobre 1918
Agence de Clichy la Garenne : 1 rue de l'Éclair
Agence de Triel-sur-Seine : 184 rue Paul Doumer
Agence de Chateaufort-Malabry : 17 rue Jean Marthe
Agence de Pantin : 25 rue du 20 novembre 1918

Coordonnées : 01 47 39 32 68
Tél : 01 47 39 32 68
Fax : 01 47 39 32 68
Tél : 01 47 39 32 68
Fax : 01 47 39 32 68
Tél : 01 47 39 32 68
Fax : 01 47 39 32 68
Tél : 01 47 39 32 68
Fax : 01 47 39 32 68

REFERENCES TECHNIQUES

REDACTEUR	VERIFICATEUR	APPROBATEUR
CP	CP	J.L.

DOSSIER : 18028 ARCHIVES : 1006
DATE : 22 juin 2018 - V2
ECHELLE : 1/20ème

Nota :
Documents établis sur la base des plans
Phase DCE datés de décembre 2017 dressés par :
EURL ALAIN MANOILESCO Architecte
13 rue Chapot - 75003 PARIS

ALFORTVILLE

Val-de-Marne

Rue Etienne Dolet

Rue de Rome

Rue de Milan

Cadastre : Section AE n°185,186, 187, 190

PLAN DES INTÉRIEURS REZ-DE-CHAUSSÉE

MODIFICATIONS

INDICE	NATURE	AUTEUR	DATE
1	Édition du plan, (complément de côtes)	LM	06/05/2022

- Nota :
- Les relevés ont été effectués par le cabinet FOREST & Associés en janvier 2022.
 - Niveau de détail du relevé : 1/100.

RÉFÉRENCES TECHNIQUES		
DOSSIER :	212087	ARCHIVES : 16066
DATE :	05/01/2022	
ECHELLE :	1/100	
RÉDACTEUR	VÉRIFICATEUR	APPROBATEUR
BK	YK	AM

Légende :

Assiette foncière

Détail poutre

HSP=3,20m

Hauteur sous plafond


1

Numéro de lot


Emprise du lot n°1

Parties communes


Selon plan de copropriété en nos archives datant de juin 2018

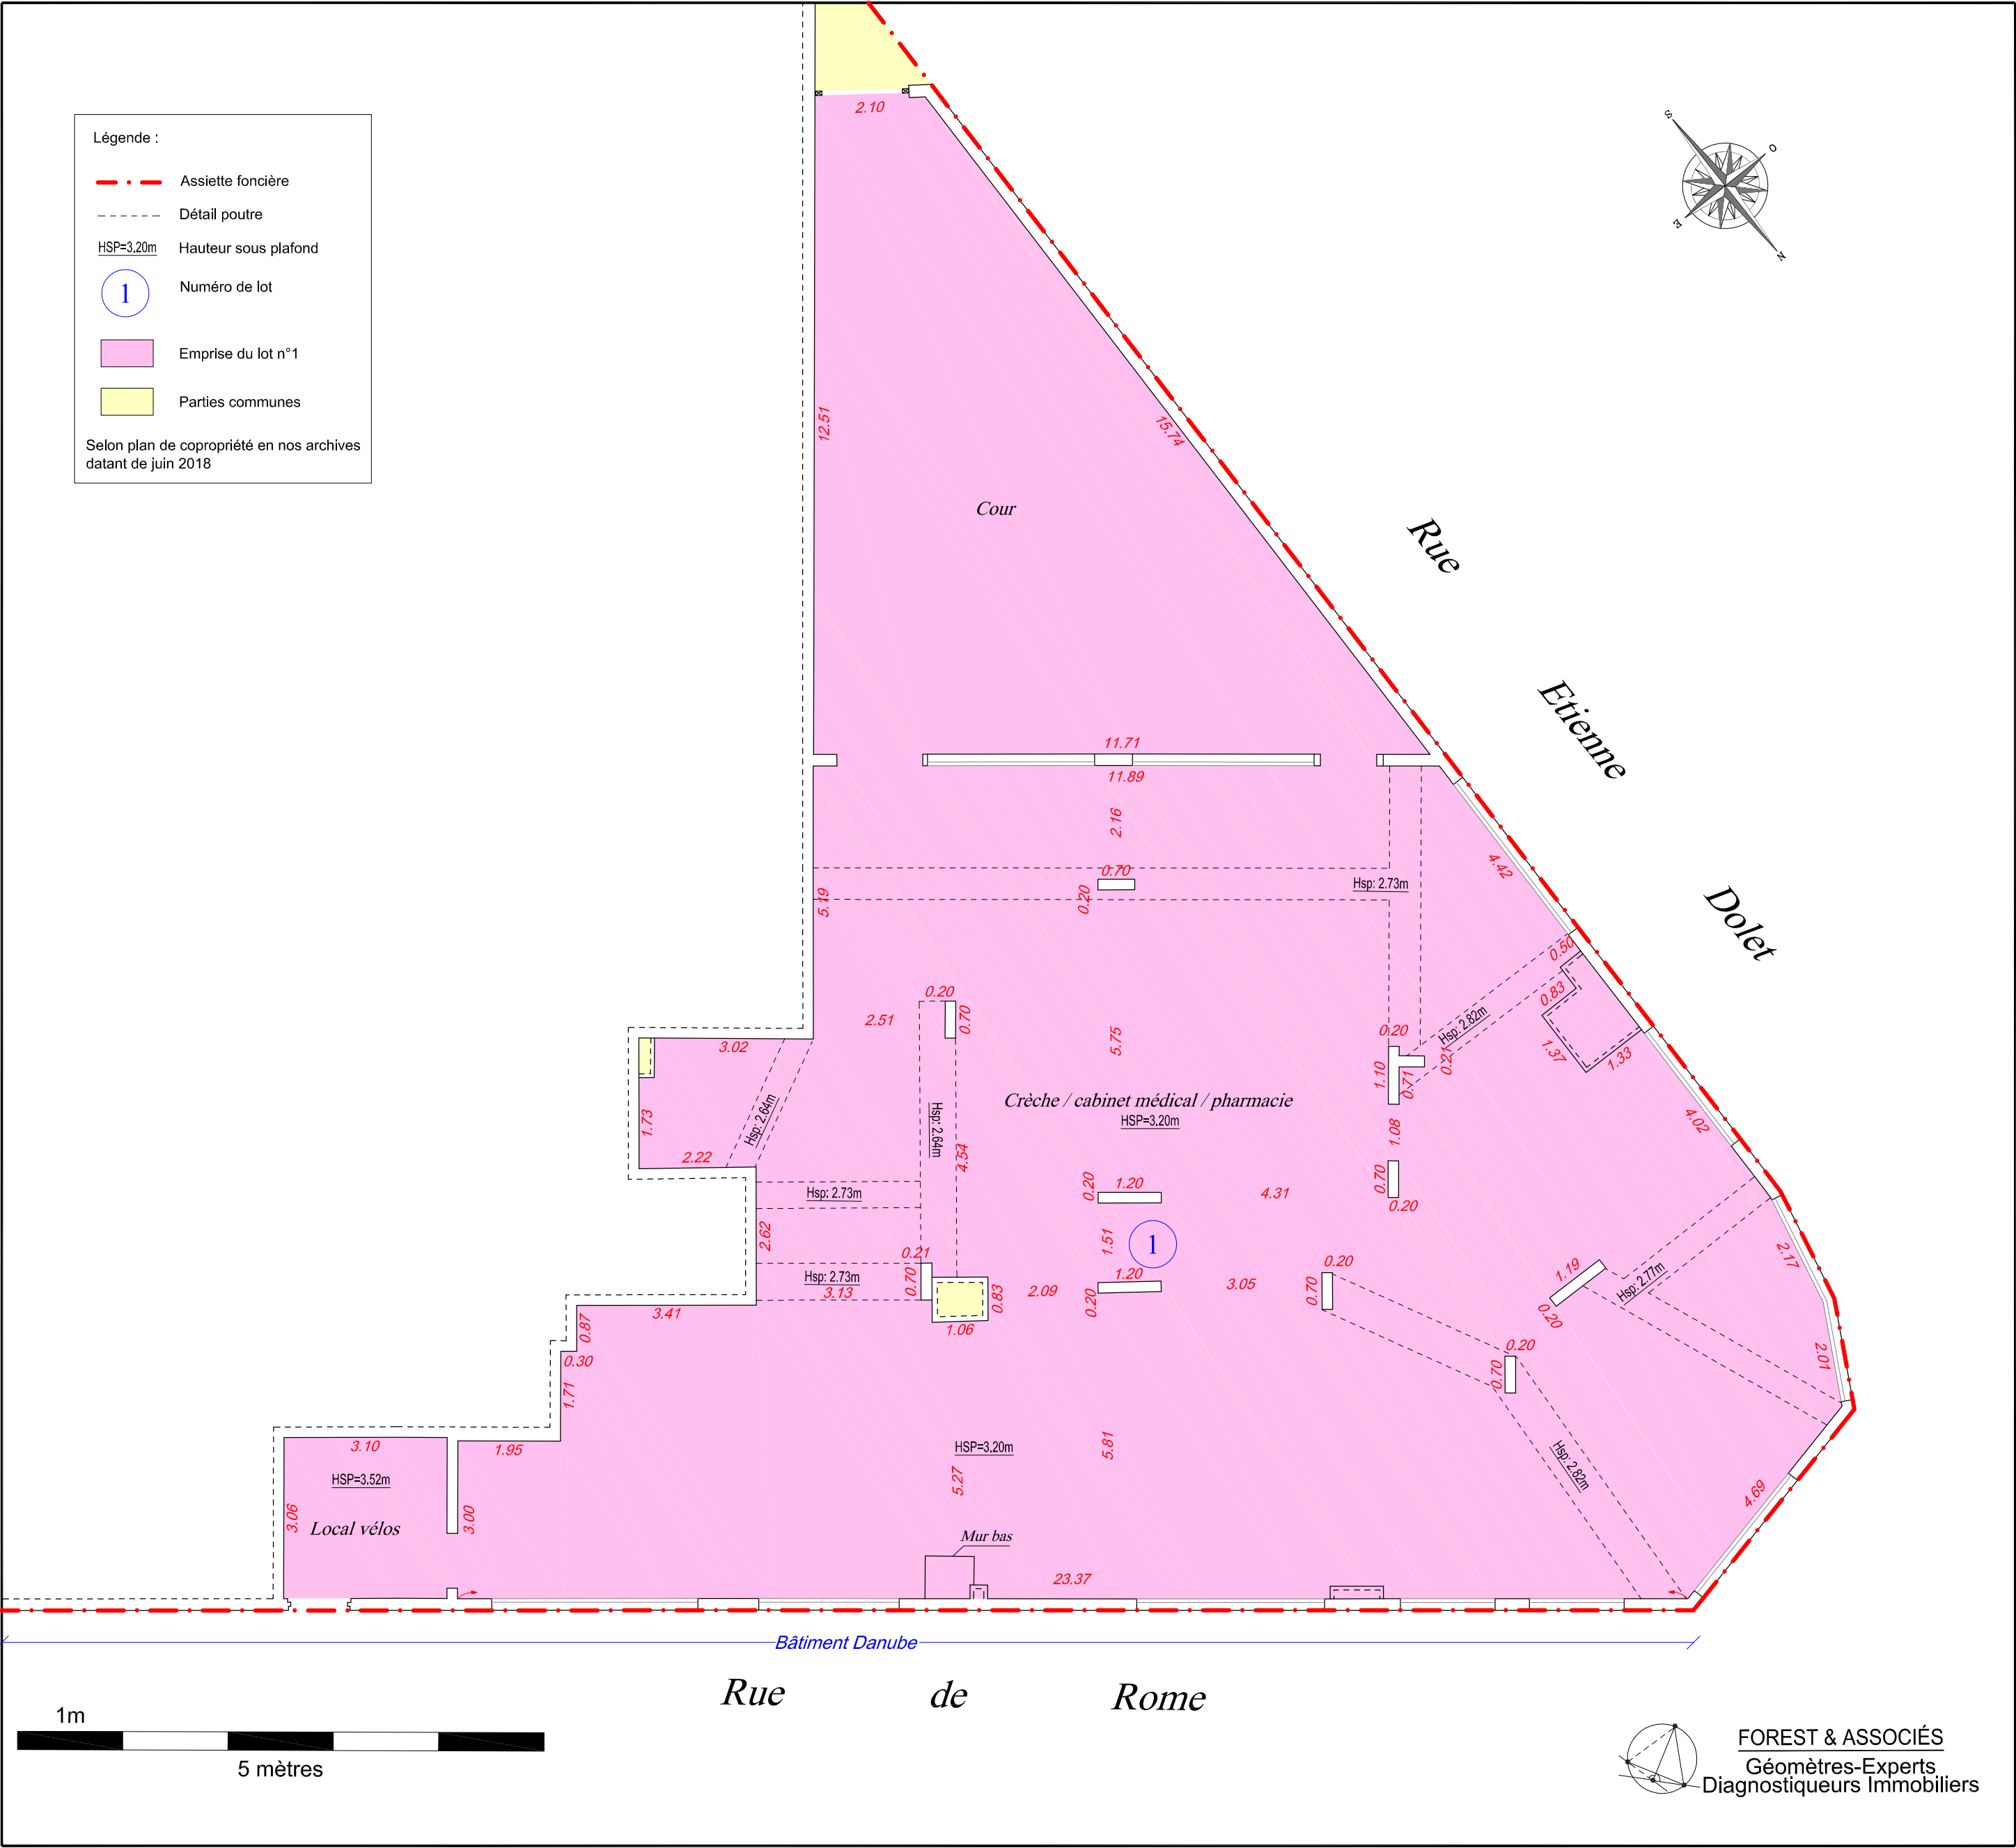

RUE DE ROME

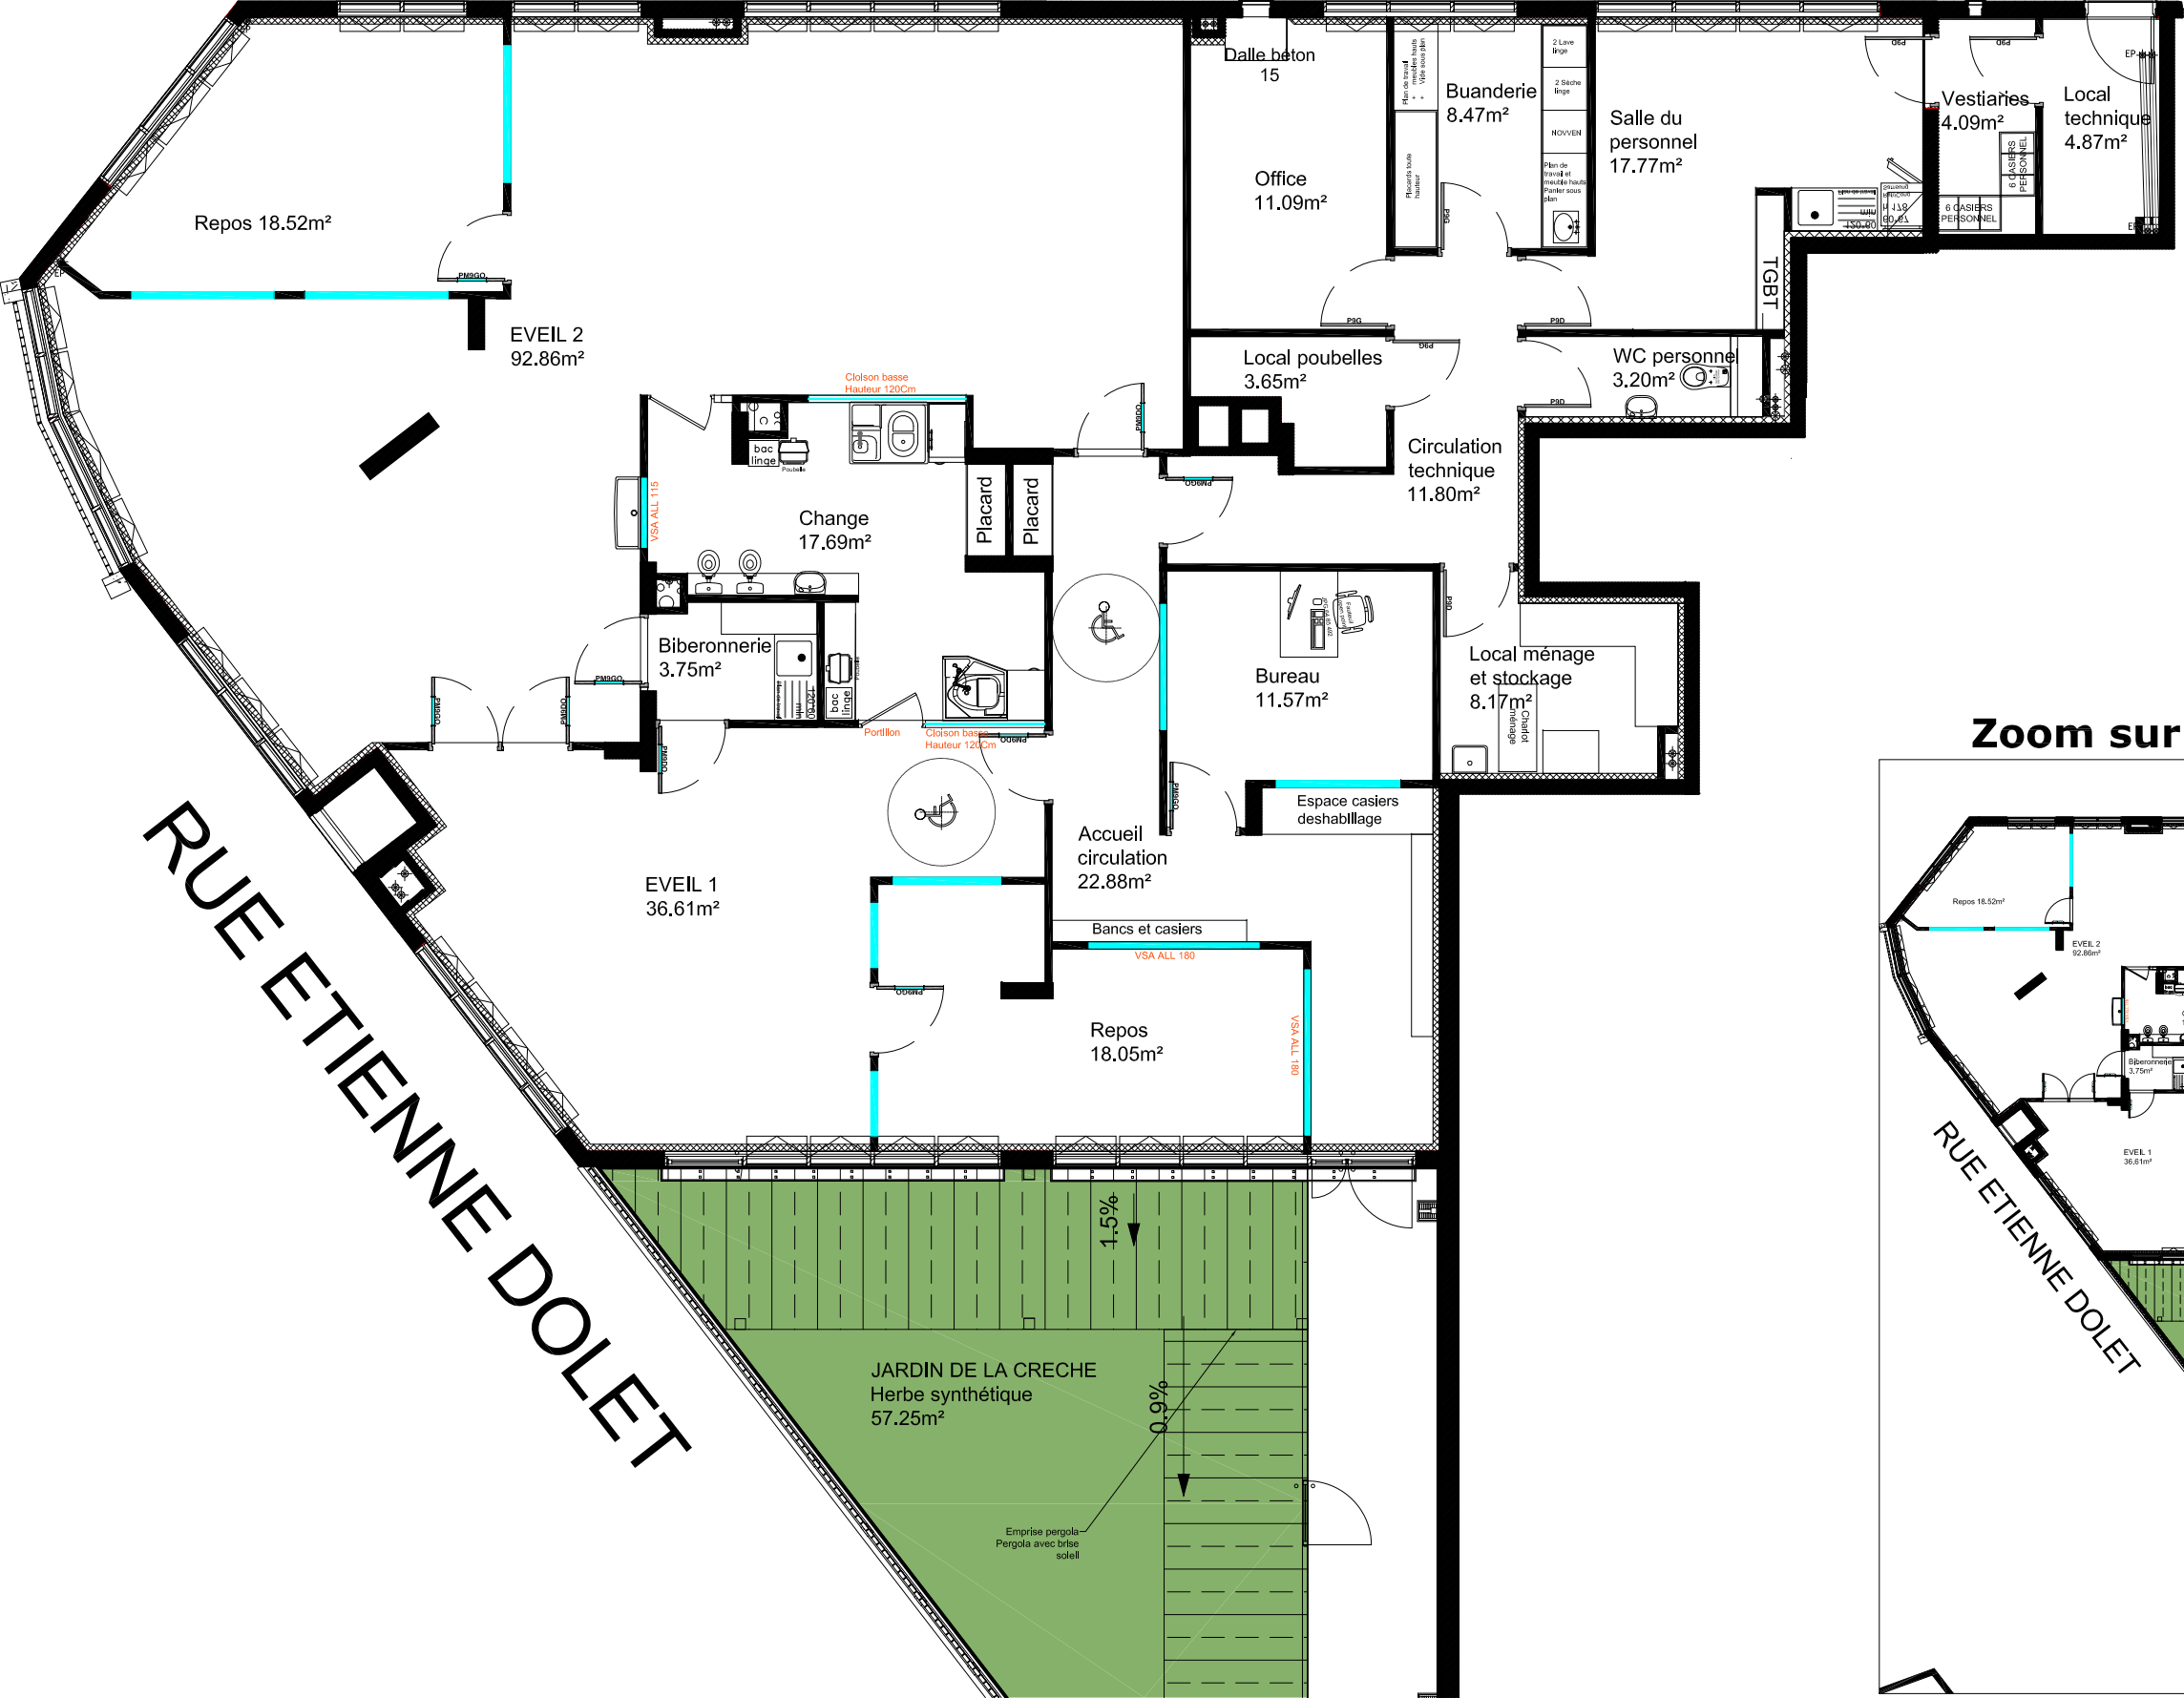

Zoom sur l'ensemble de la crèche

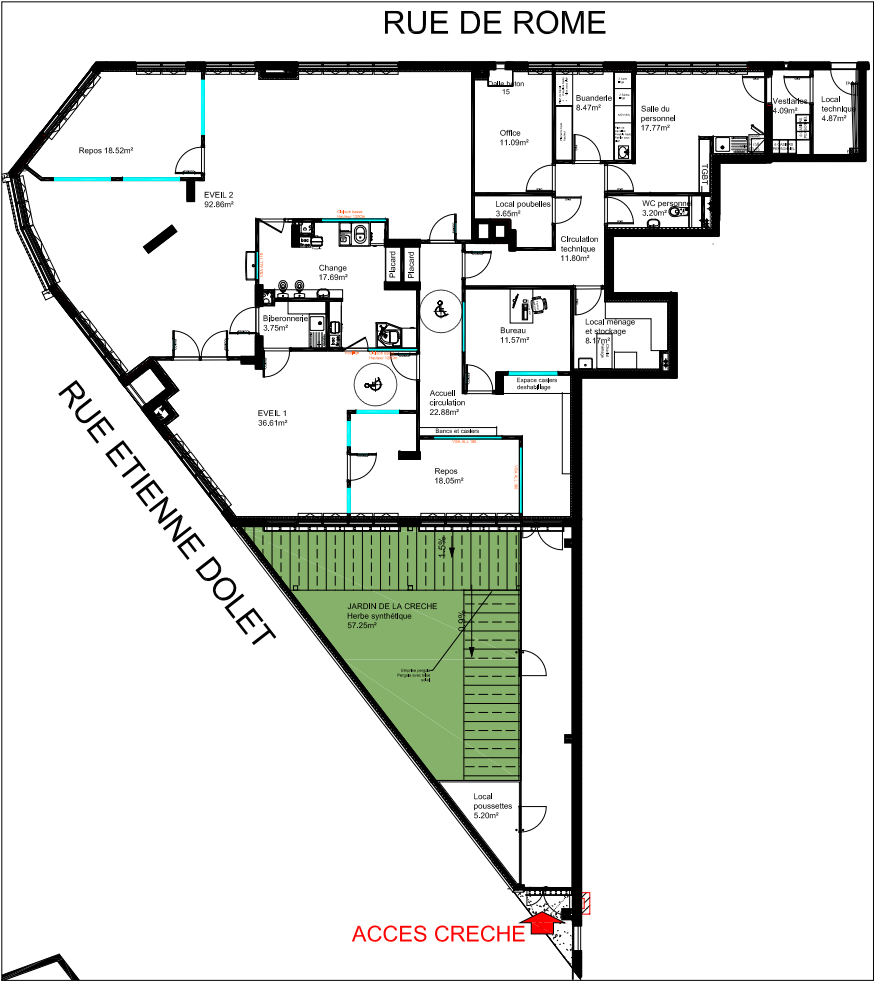

MAITRE D'OEUVRE	PHASE	NOM DU DOCUMENT	ECHELLE	PROJET	MAITRE D'OUVRAGE	DATE	
SARA HATTAB ARCHITECTURE 13 Rue du onze novembre 1918 94 310 Orly 06 33 80 48 43 Sh.architecture@outlook.fr	APD	PLAN RDC	1/100	Création d'un multi-accueil 105 Rue Etienne Dolet 94 140 ALFORTVILLE Les Petites Canailles Alfortville	LES PETITES CANAILLES 36 Rue Pierret 92 200 NEUILLY SUR SEINE	25/04/2023	 124

Plan de repérage


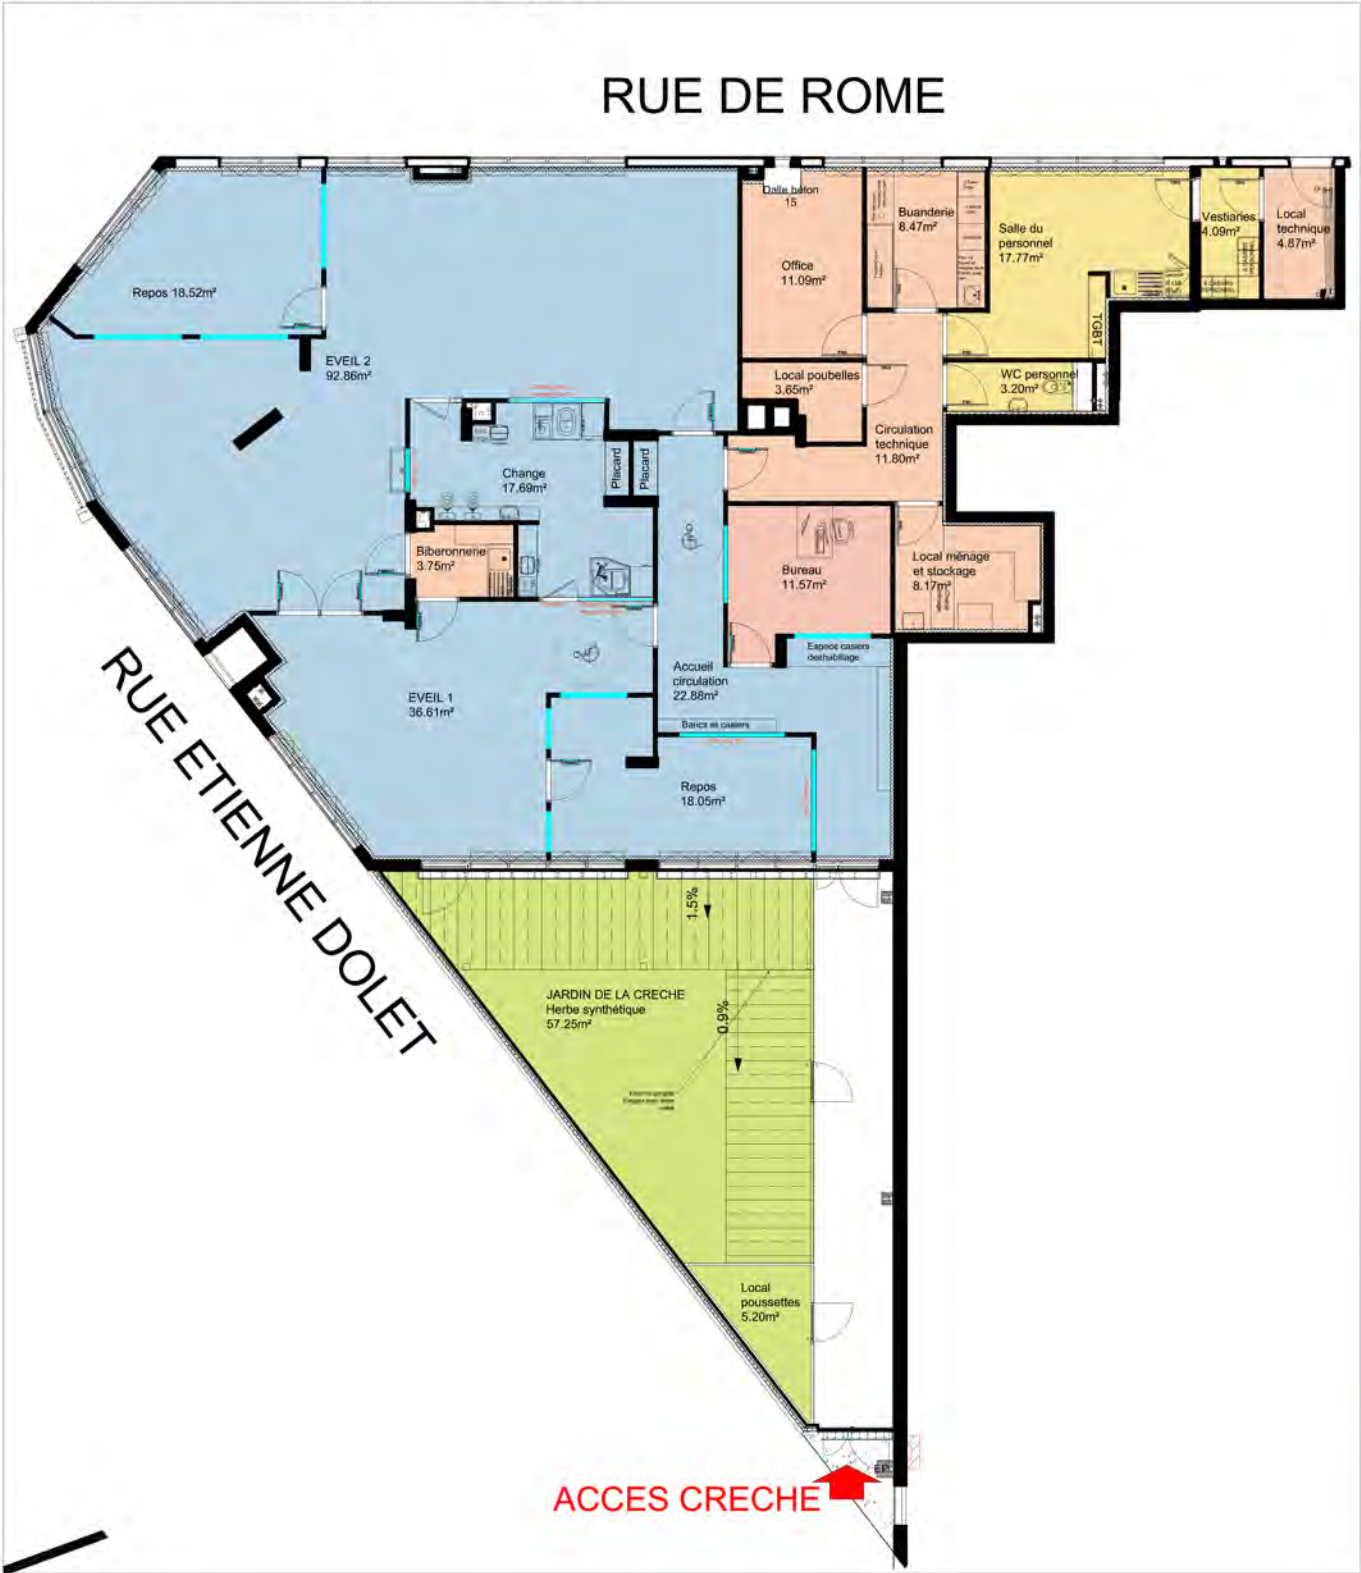


Tableau de surface

Type	locaux	Surface m²/ local	Surface m²/ type
PUBLIC	Bureau de la direction	11,57	11,57
ENFANTS	Entrée	22,88	206,62
	Repos 1	18,06	
	Repos 2	18,52	
	Salle de change	17,69	
	Salle d'éveil 1	36,61	
	Salle d'éveil 2	92,86	
Personnel	Salle du personnel	17,77	25,06
	Vestiaires	4,09	
	WC	3,2	
Zone technique	Office	11,09	51,8
	Buanderie et lingerie	8,47	
	Biberonnerie	3,75	
	Local ménage et stockage	8,17	
	Local poubelles	3,65	
	Local technique	4,87	
	Circulation technique	11,8	
TOTAL en m²(intérieur			295,05
Extérieur	Jardin	57,25	57,25
	Local poussette	5,2	5,2

Plan du jardin

Quelques références

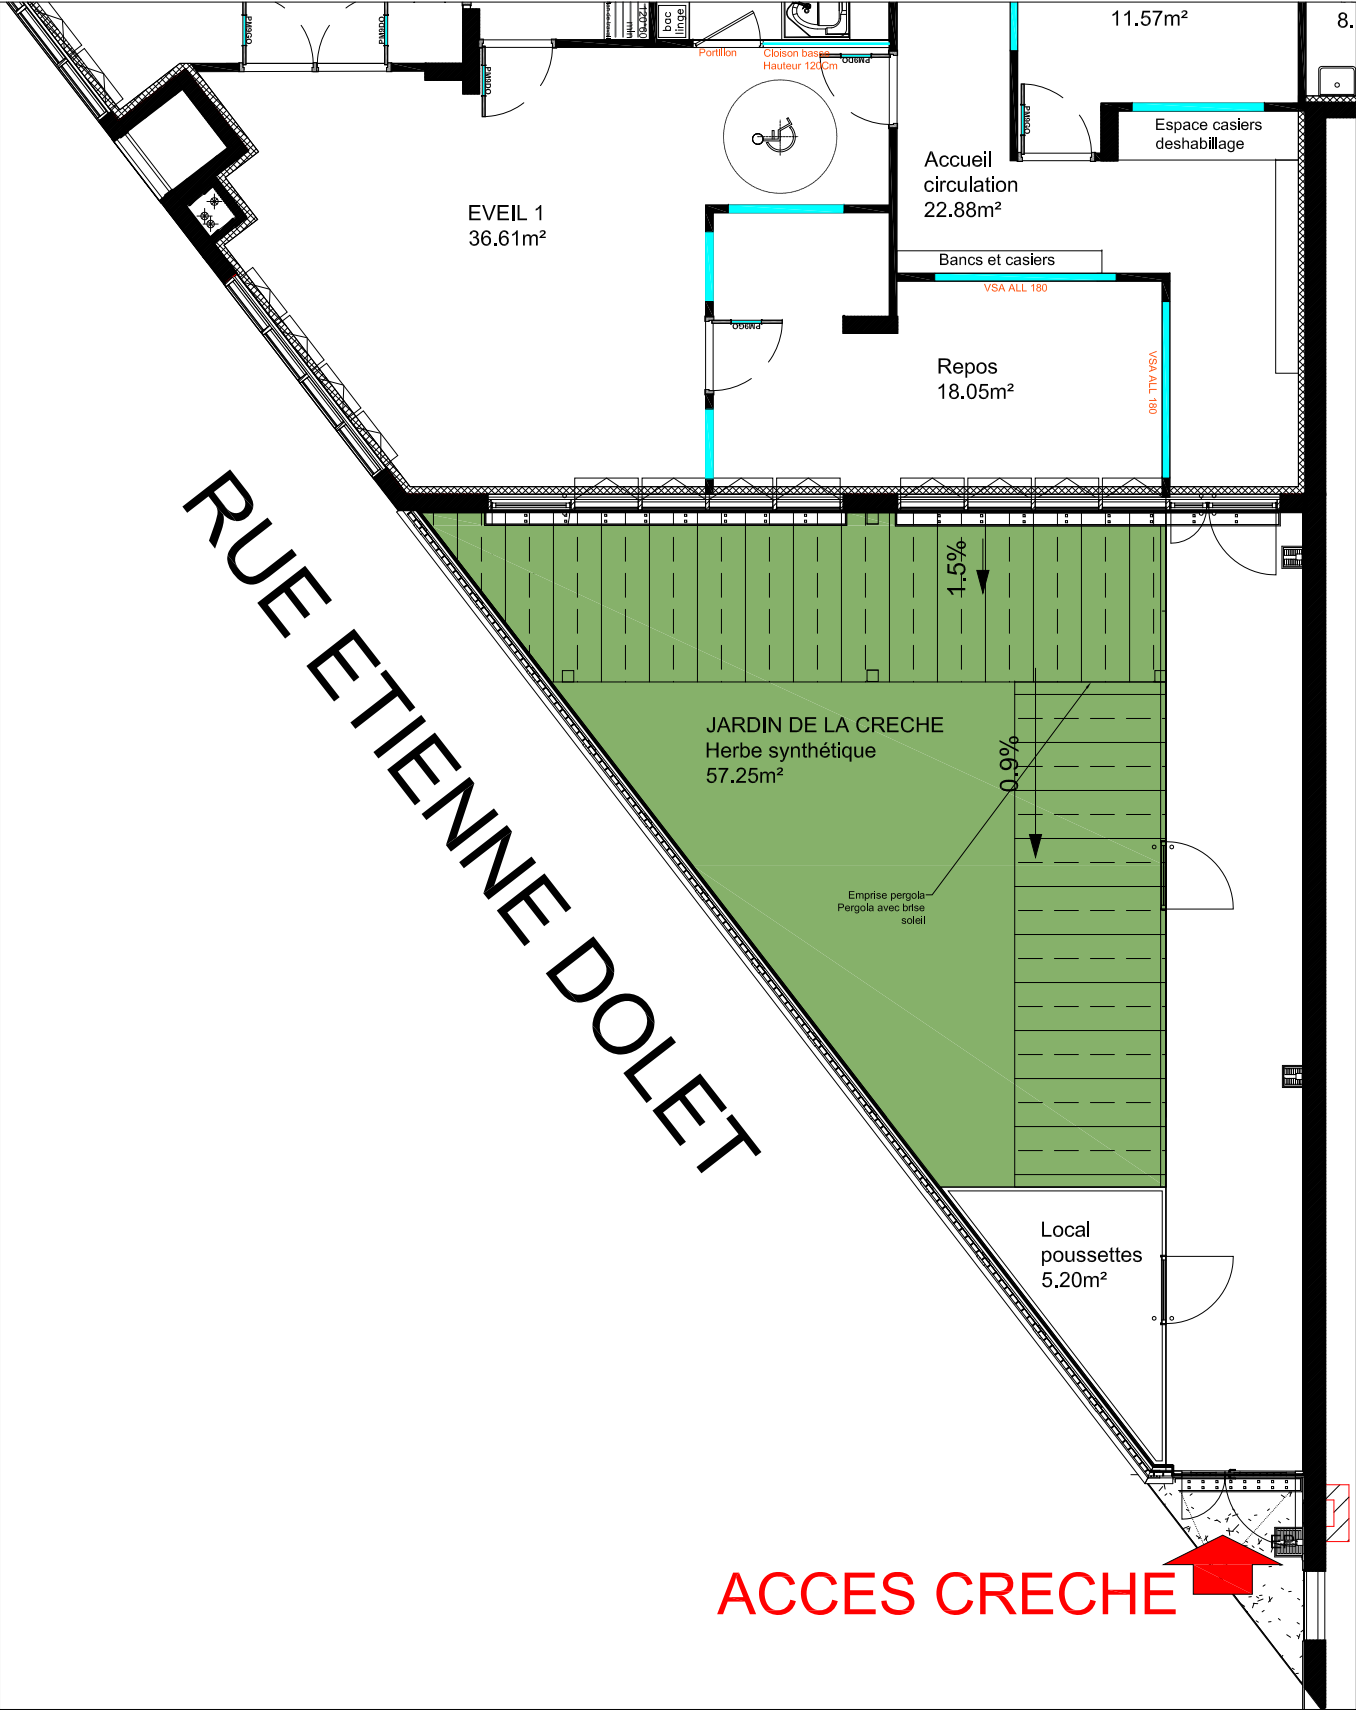

Pergola bois/métallique



Pergola métallique

MAITRE D'OEUVRE	PHASE	NOM DU DOCUMENT	ECHELLE	PROJET	MAITRE D'OUVRAGE	DATE	
SARA HATTAB ARCHITECTURE 13 Rue du onze novembre 1918 94 310 Orly 06 33 80 48 43 Sh.architecture@outlook.fr	APD	PLAN DU JARDIN	1/100	Création d'un multi-accueil 105 Rue Etienne Dolet 94 140 ALFORTVILLE Les Petites Canailles Alfortville	LES PETITES CANAILLES 36 Rue Pierret 92 200 NEUILLY SUR SEINE	25/04/2023	 125