



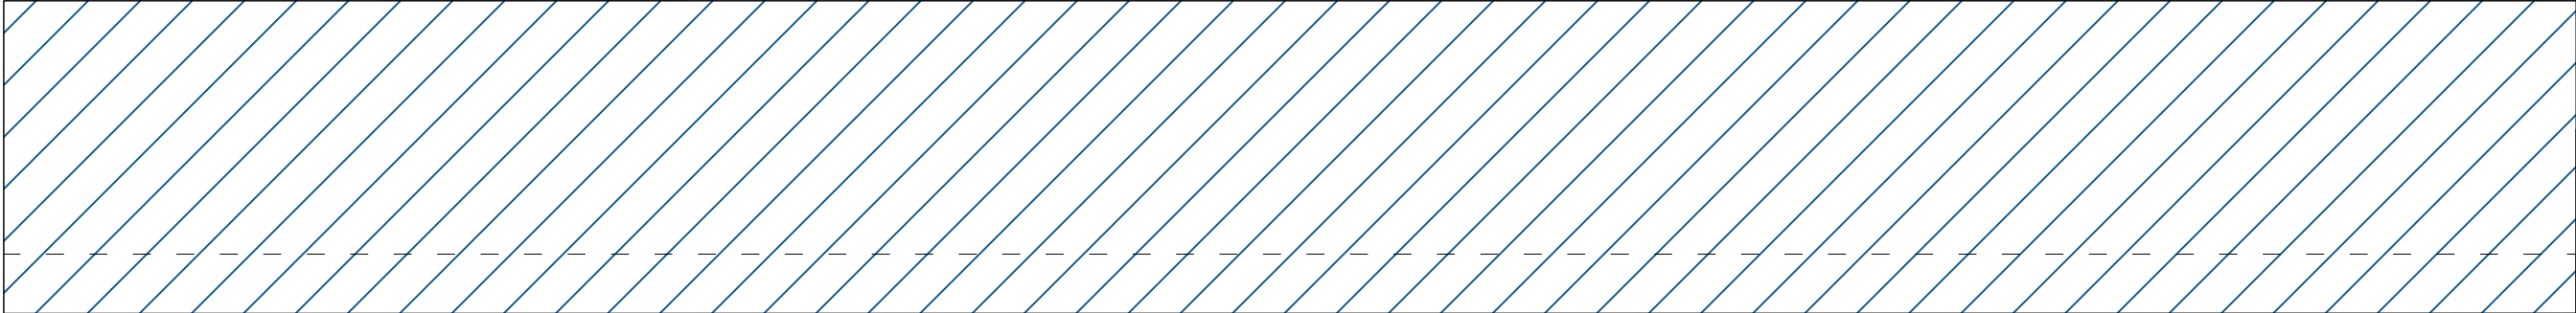

CREATION D'UN MULTI-ACCUEIL ET D'UNE MAISON MEDICALE 30 ter Avenue de Brimont 78400 CHATOU			
MOA	SARL LPC YVELINES 15 Rue de l'Orient78000 VERSAILLES		
MOE	NAHK ARCHITECTURE 24 Rue Yves Toudic, 75010 Paris		
NOM DU DOCUMENT			
COUPE AA'			
PHASE	PRO.DCE	ECH.	1/100
INDICE	1.1	DATE	29/06/2023
MODIFICATIONS			
INDICE DATE		OBJET	
1.1	29/06/2023	Diffusion initiale	
PLAN DE REPERAGE			




CREATION D'UN MULTI-ACCUEIL ET D'UNE MAISON MEDICALE 30 ter Avenue de Brimont 78400 CHATOU	
MOA	SARL LPC YVELINES 15 Rue de l'Orient78000 VERSAILLES
MOE	NAHK ARCHITECTURE 24 Rue Yves Toudic, 75010 Paris
NOM DU DOCUMENT	


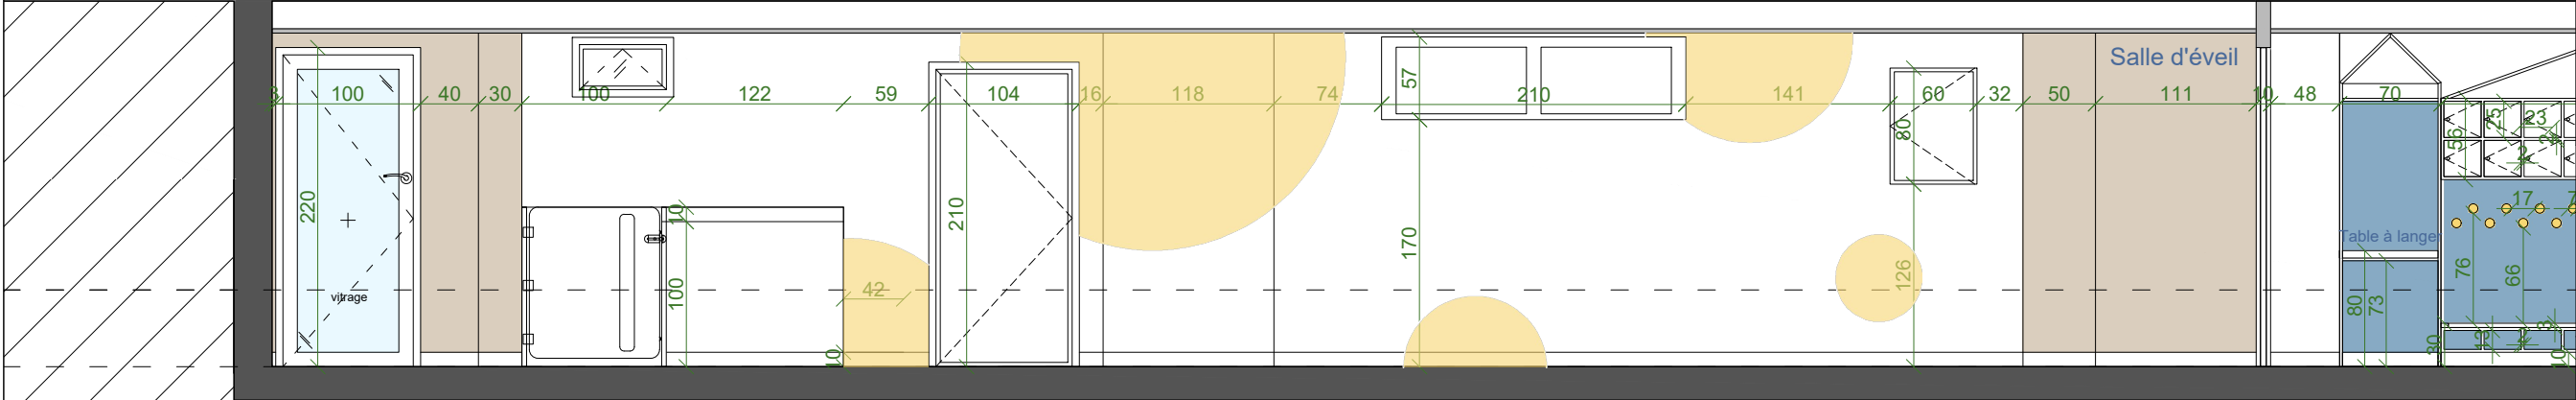



ZOOM COUPE AA'			
PHASE	PRO.DCE	ECH.	1/50
INDICE	1.1	DATE	29/06/2023

MODIFICATIONS			
INDICE	DATE	OBJET	
1.1	29/06/2023	Diffusion initiale	

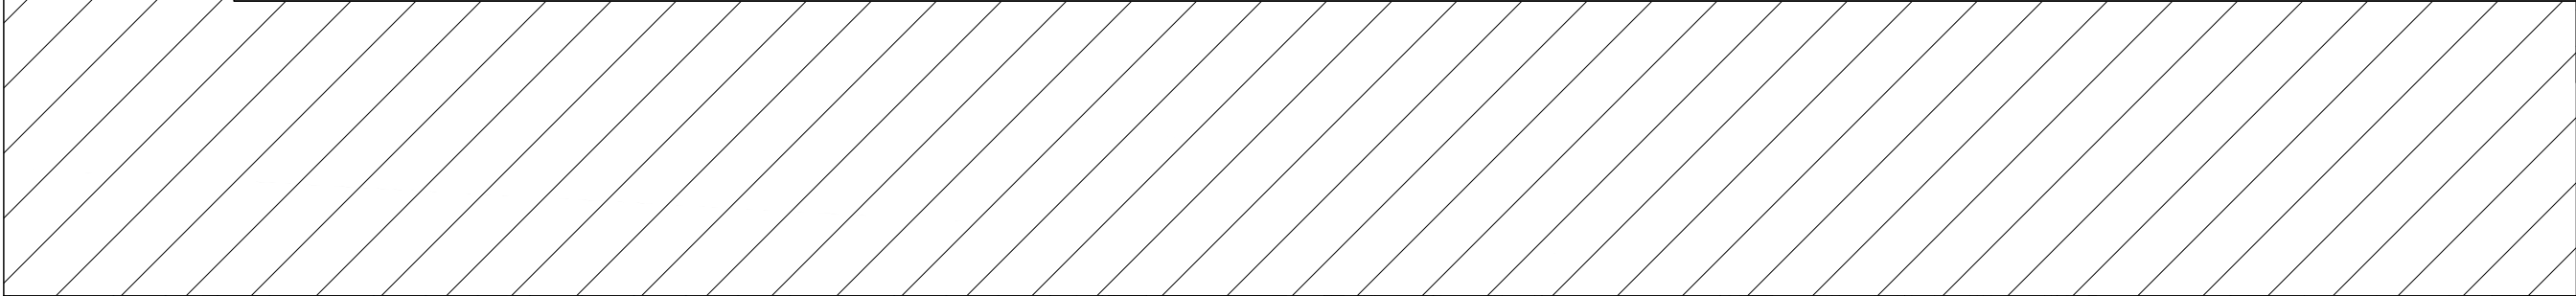

PLAN DE REPERAGE			
------------------	--	--	--

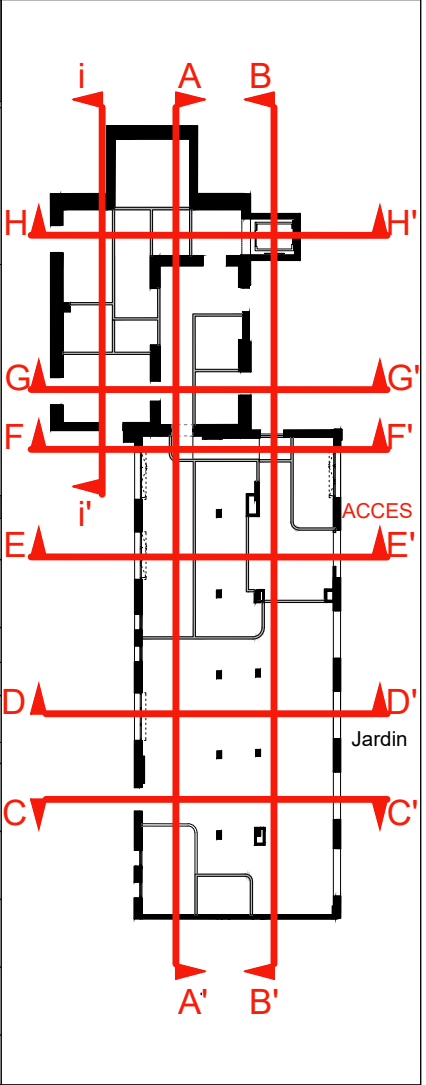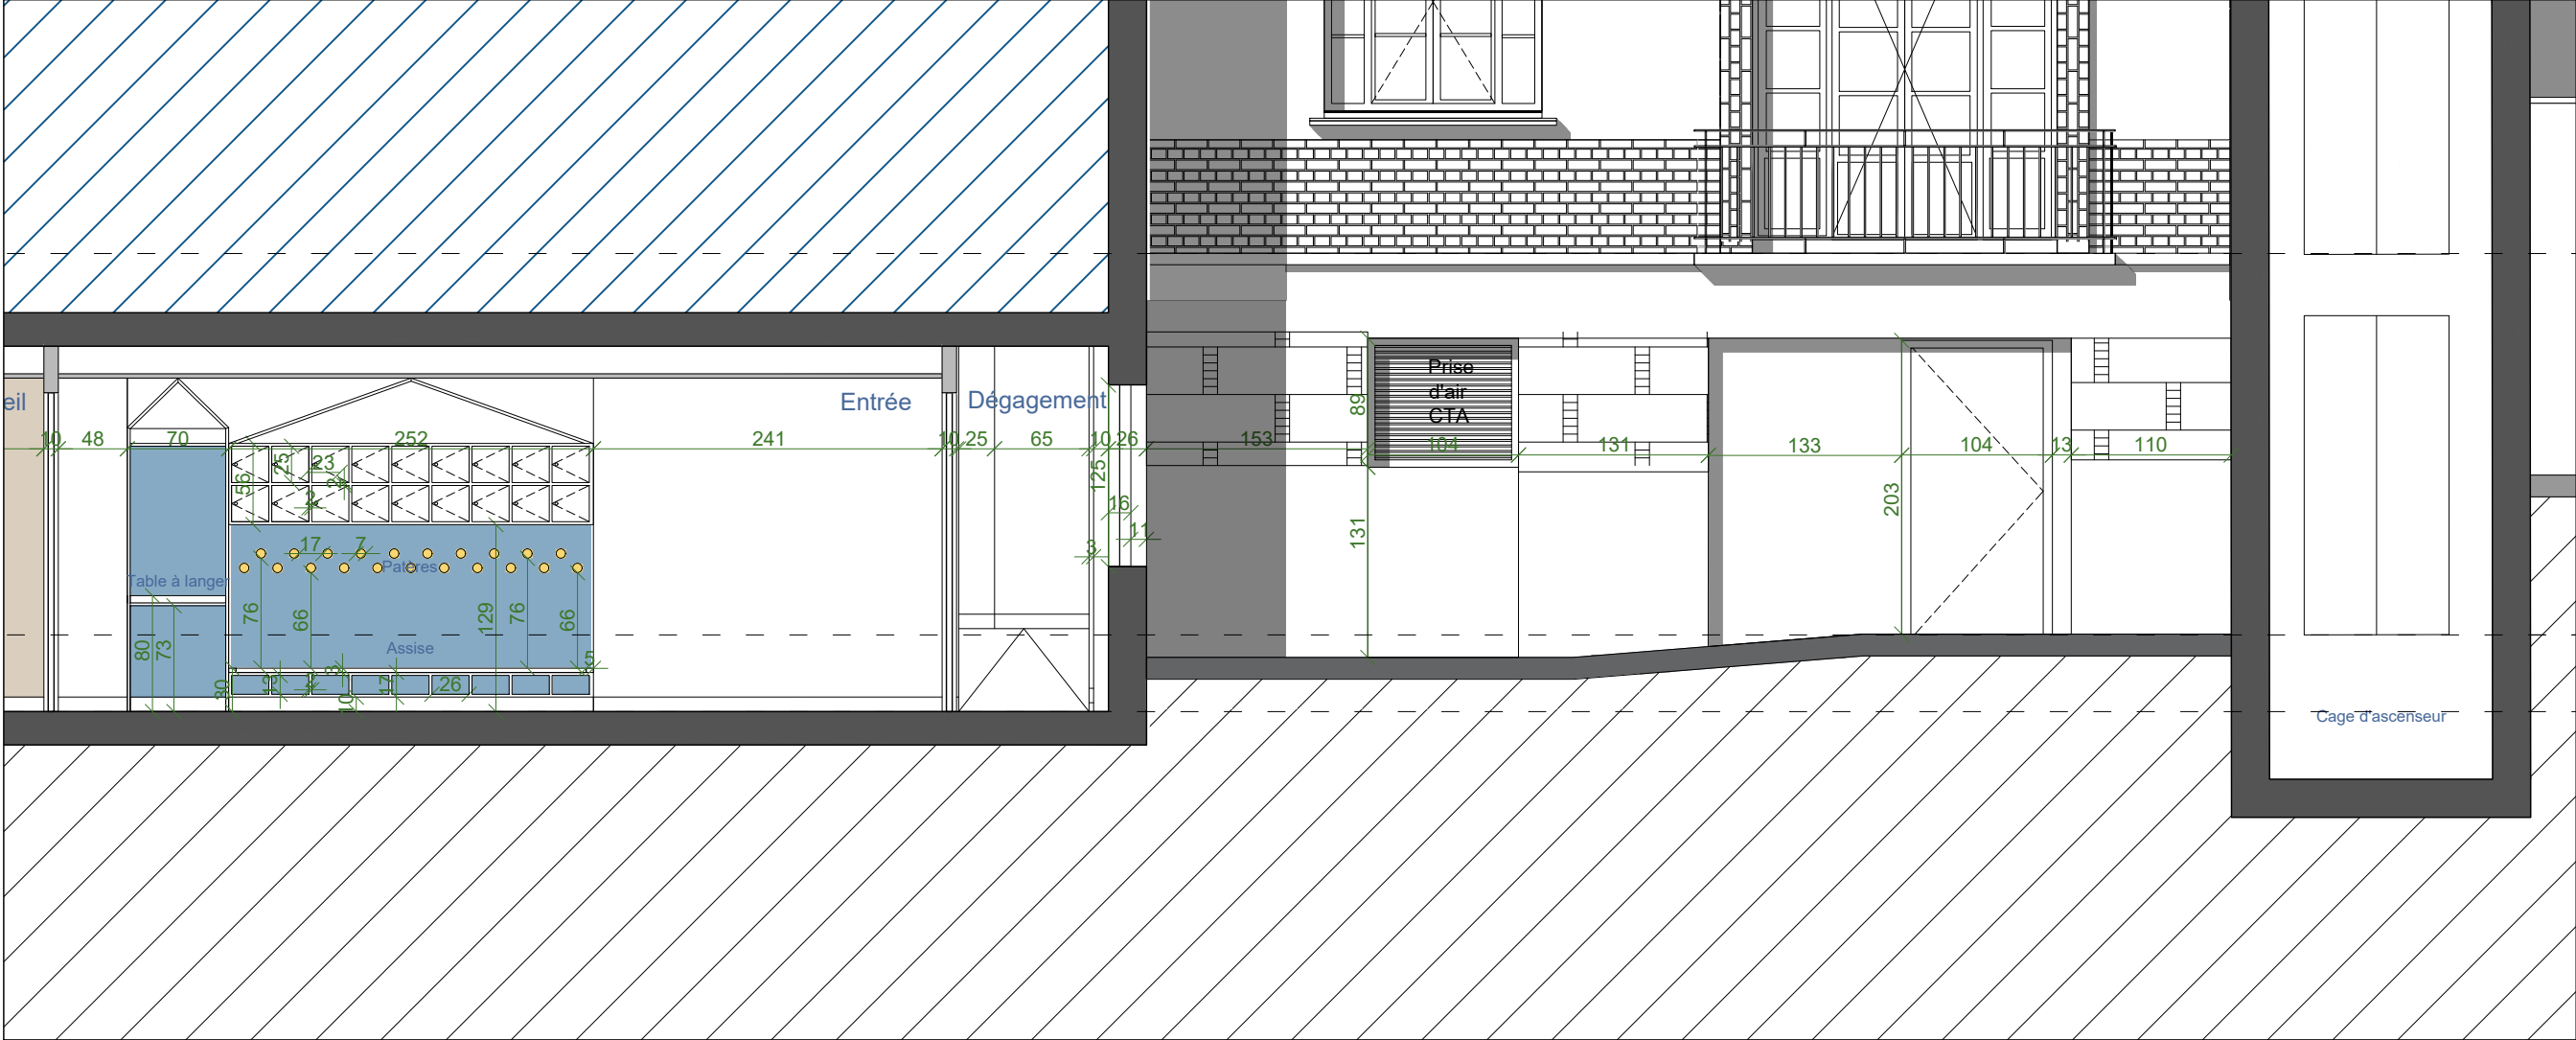

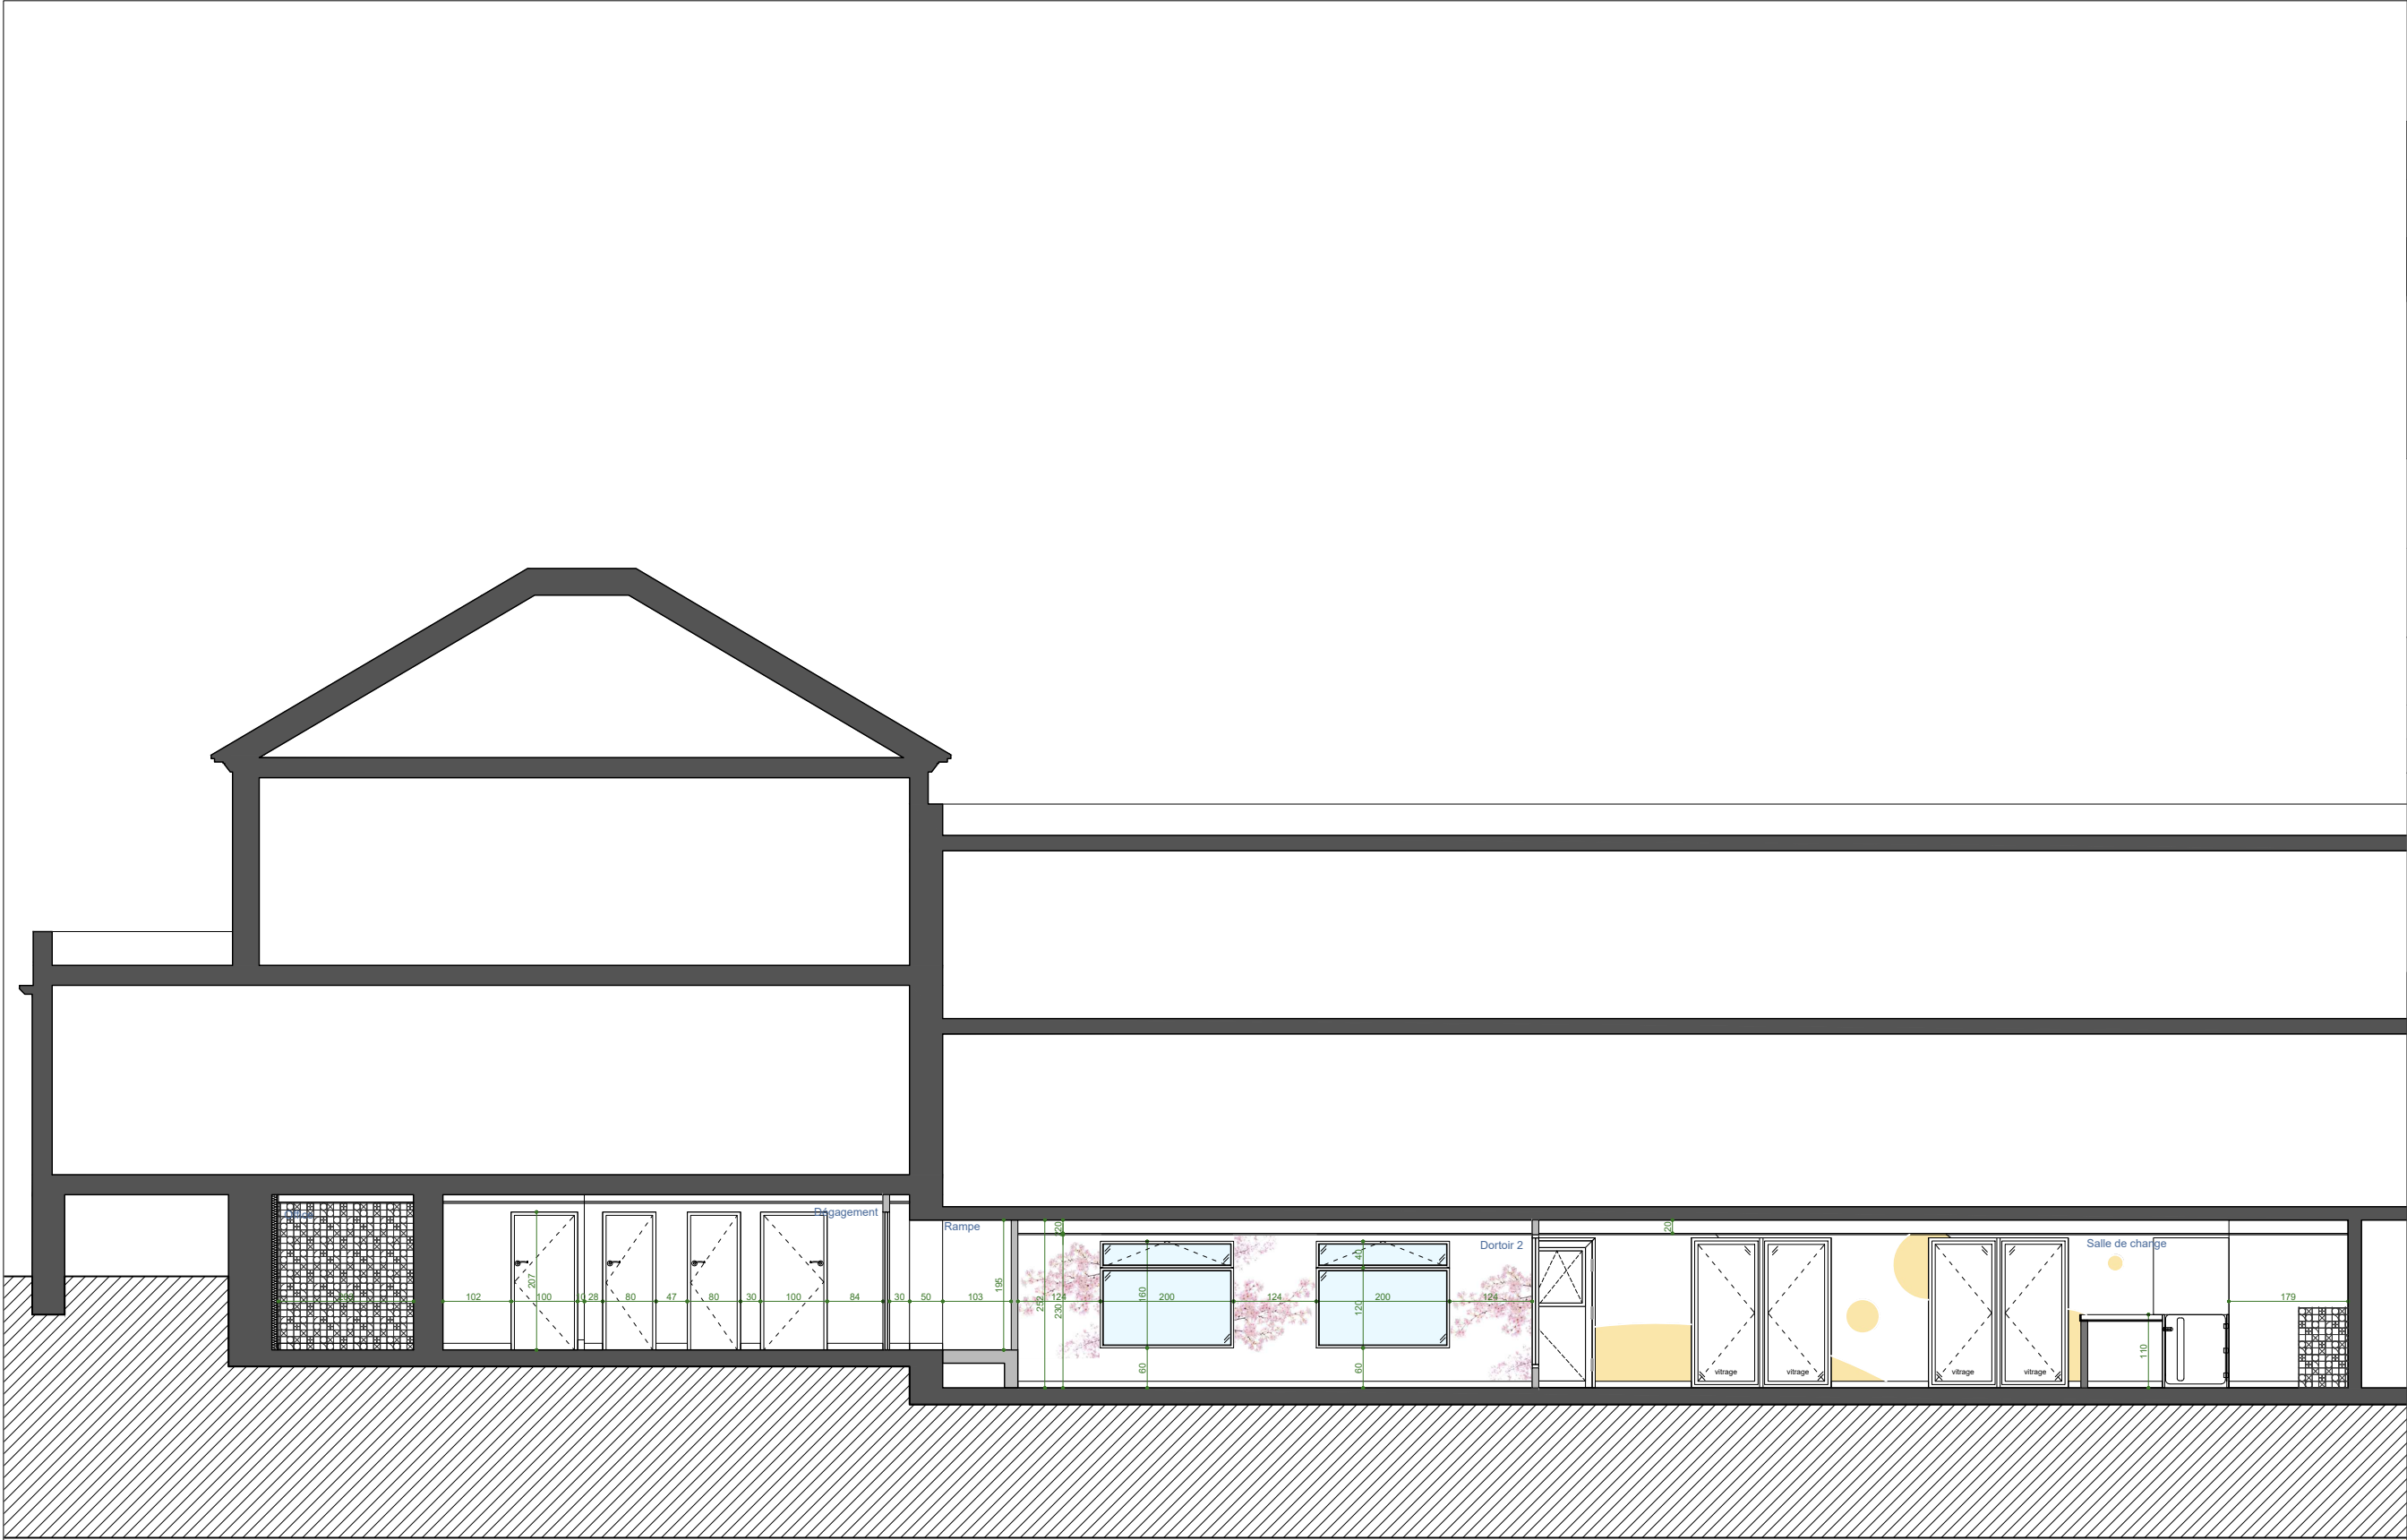

CREATION D'UN MULTI-ACCUEIL ET
D'UNE MAISON MEDICALE
30 ter Avenue de Brimont
78400 CHATOU

MOA

SARL LPC YVELINES
15 Rue de l'Orient78000 VERSAILLES

MOE

NAHK ARCHITECTURE
24 Rue Yves Toudic, 75010 Paris

NOM DU DOCUMENT

COUPE BB'

PHASE

PRO.DCE

ECH.

1/100

INDICE

1.1

DATE

29/06/2023

MODIFICATIONS

INDICE DATE OBJET

1.1 29/06/2023 Diffusion initiale

PLAN DE REPERAGE



CREATION D'UN MULTI-ACCUEIL ET D'UNE MAISON MEDICALE 30 ter Avenue de Brimont 78400 CHATOU			
MOA	SARL LPC YVELINES 15 Rue de l'Orient78000 VERSAILLES		
MOE	NAHK ARCHITECTURE 24 Rue Yves Toudic, 75010 Paris		
NOM DU DOCUMENT			
ZOOM COUPE BB'			
PHASE	PRO.DCE	ECH.	1/50
INDICE	1.1	DATE	29/06/2023
MODIFICATIONS			
INDICE DATE		OBJET	
1.1	29/06/2023	Diffusion initiale	

CREATION D'UN MULTI-ACCUEIL ET
D'UNE MAISON MEDICALE
30 ter Avenue de Brimont
78400 CHATOU

MOA	SARL LPC YVELINES 15 Rue de l'Orient 78000 VERSAILLES
-----	--

MOE	NAHK ARCHITECTURE 24 Rue Yves Toudic, 75010 Paris
-----	--

NOM DU DOCUMENT

COUPE CC'
COUPE DD'

PHASE	PRO.DCE	ECH.	1/50
-------	---------	------	------


INDICE	1.1	DATE	29/06/2023
--------	-----	------	------------


MODIFICATIONS

INDICE	DATE	OBJET
--------	------	-------



1.1	29/06/2023	Diffusion initiale
-----	------------	--------------------


PLAN DE REPERAGE

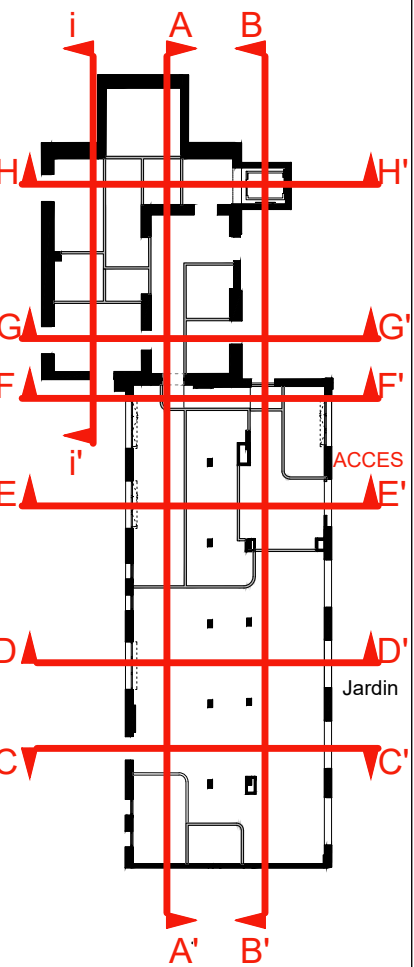


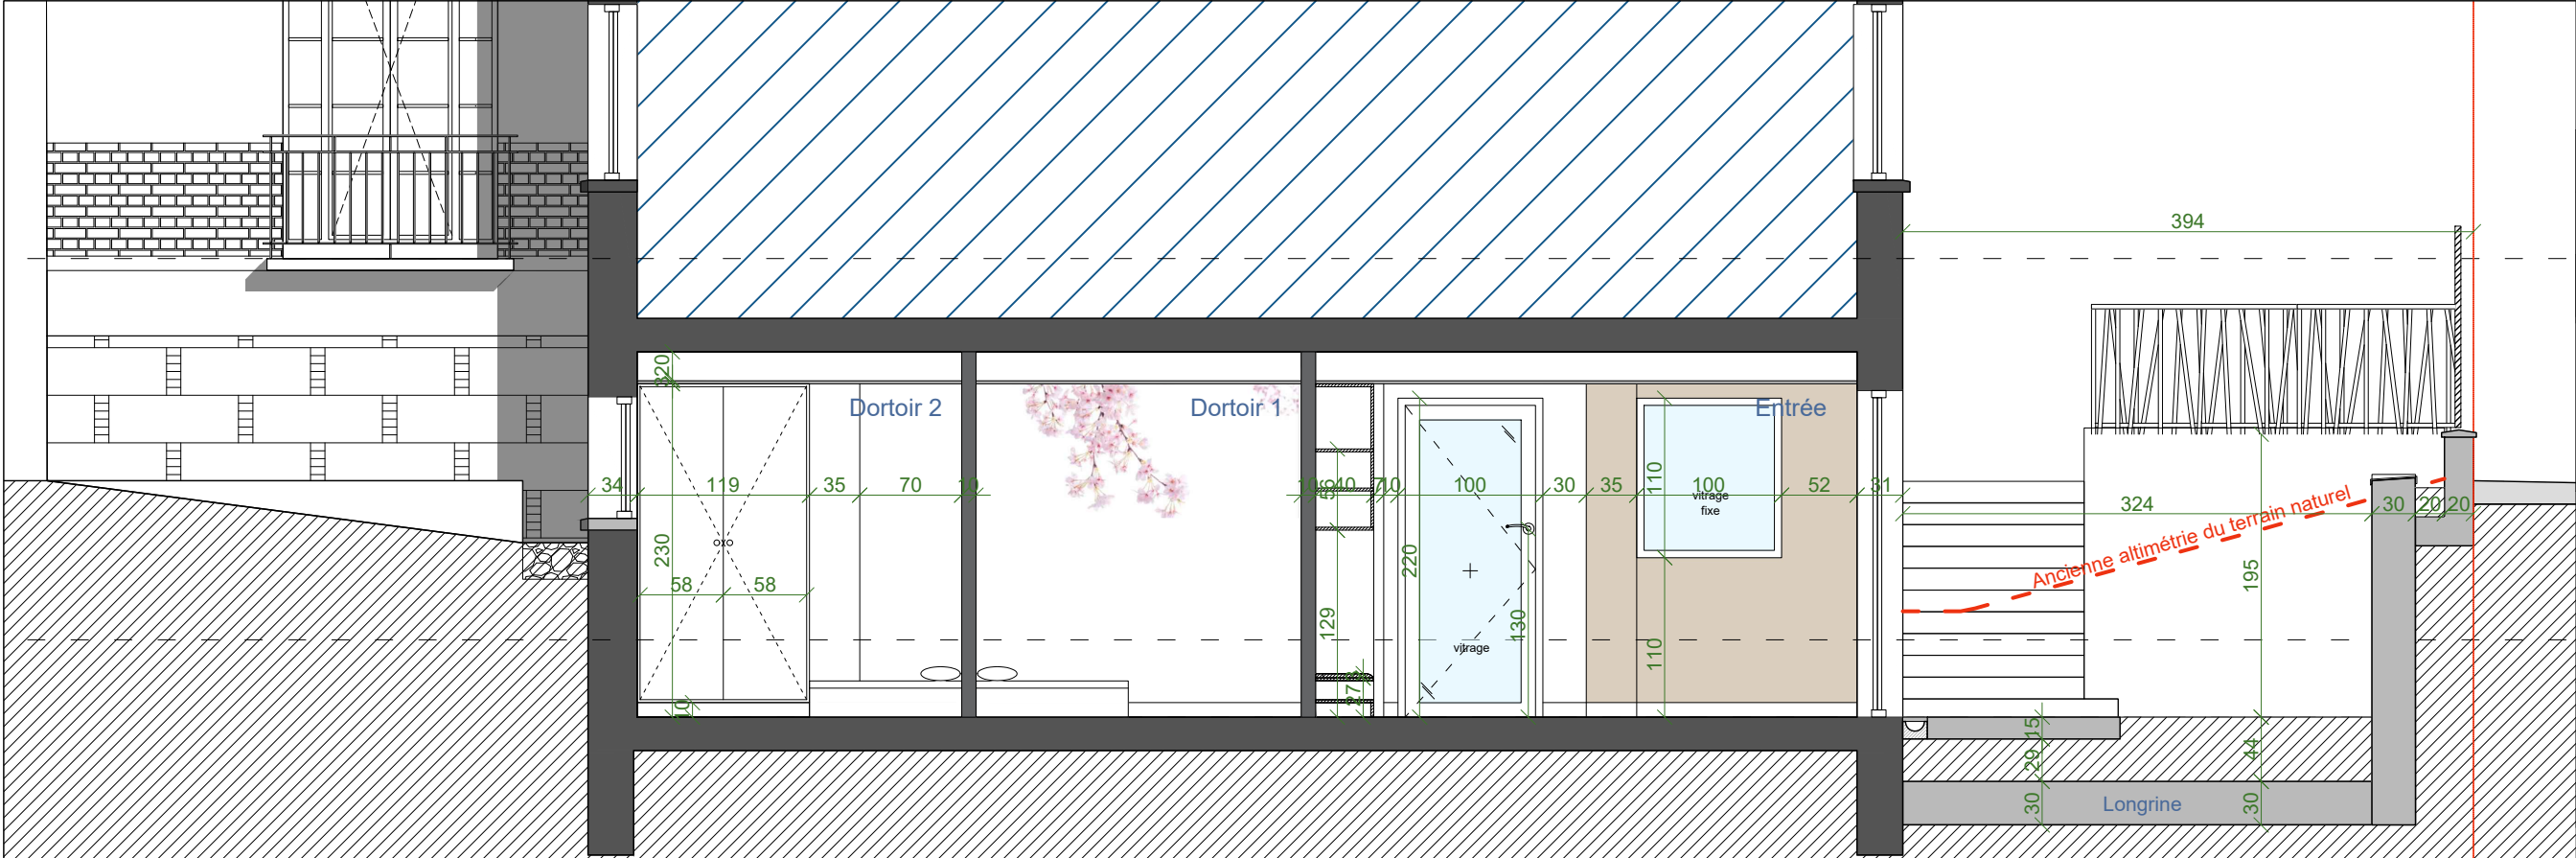



CREATION D'UN MULTI-ACCUEIL ET D'UNE MAISON MEDICALE 30 ter Avenue de Brimont 78400 CHATOU			
MOA	SARL LPC YVELINES 15 Rue de l'Orient78000 VERSAILLES		
MOE	NAHK ARCHITECTURE 24 Rue Yves Toudic, 75010 Paris		
NOM DU DOCUMENT			
COUPE EE' COUPE FF'			
PHASE	PRO.DCE	ECH.	1/50
INDICE	1.1	DATE	29/06/2023
MODIFICATIONS			
INDICE DATE		OBJET	
1.1	29/06/2023	Diffusion initiale	

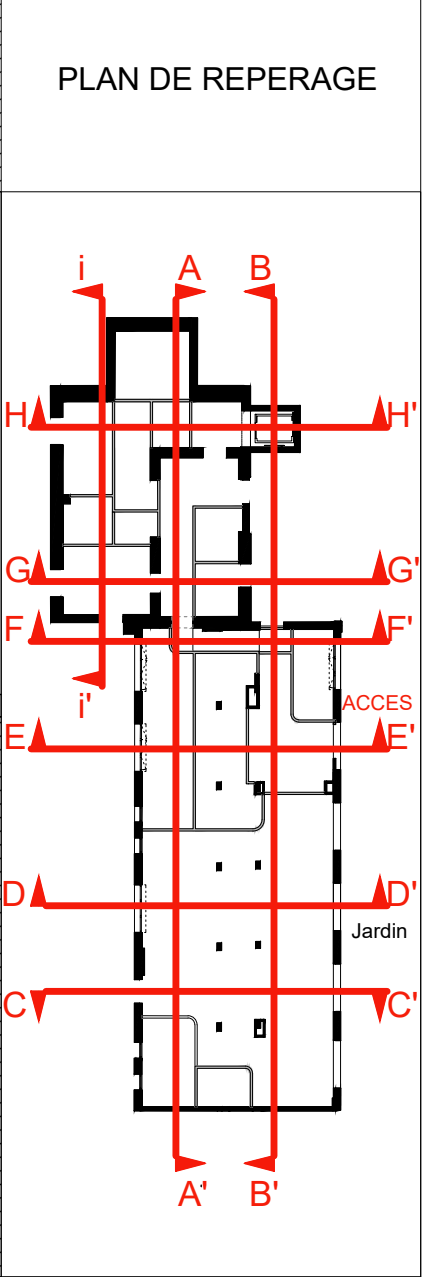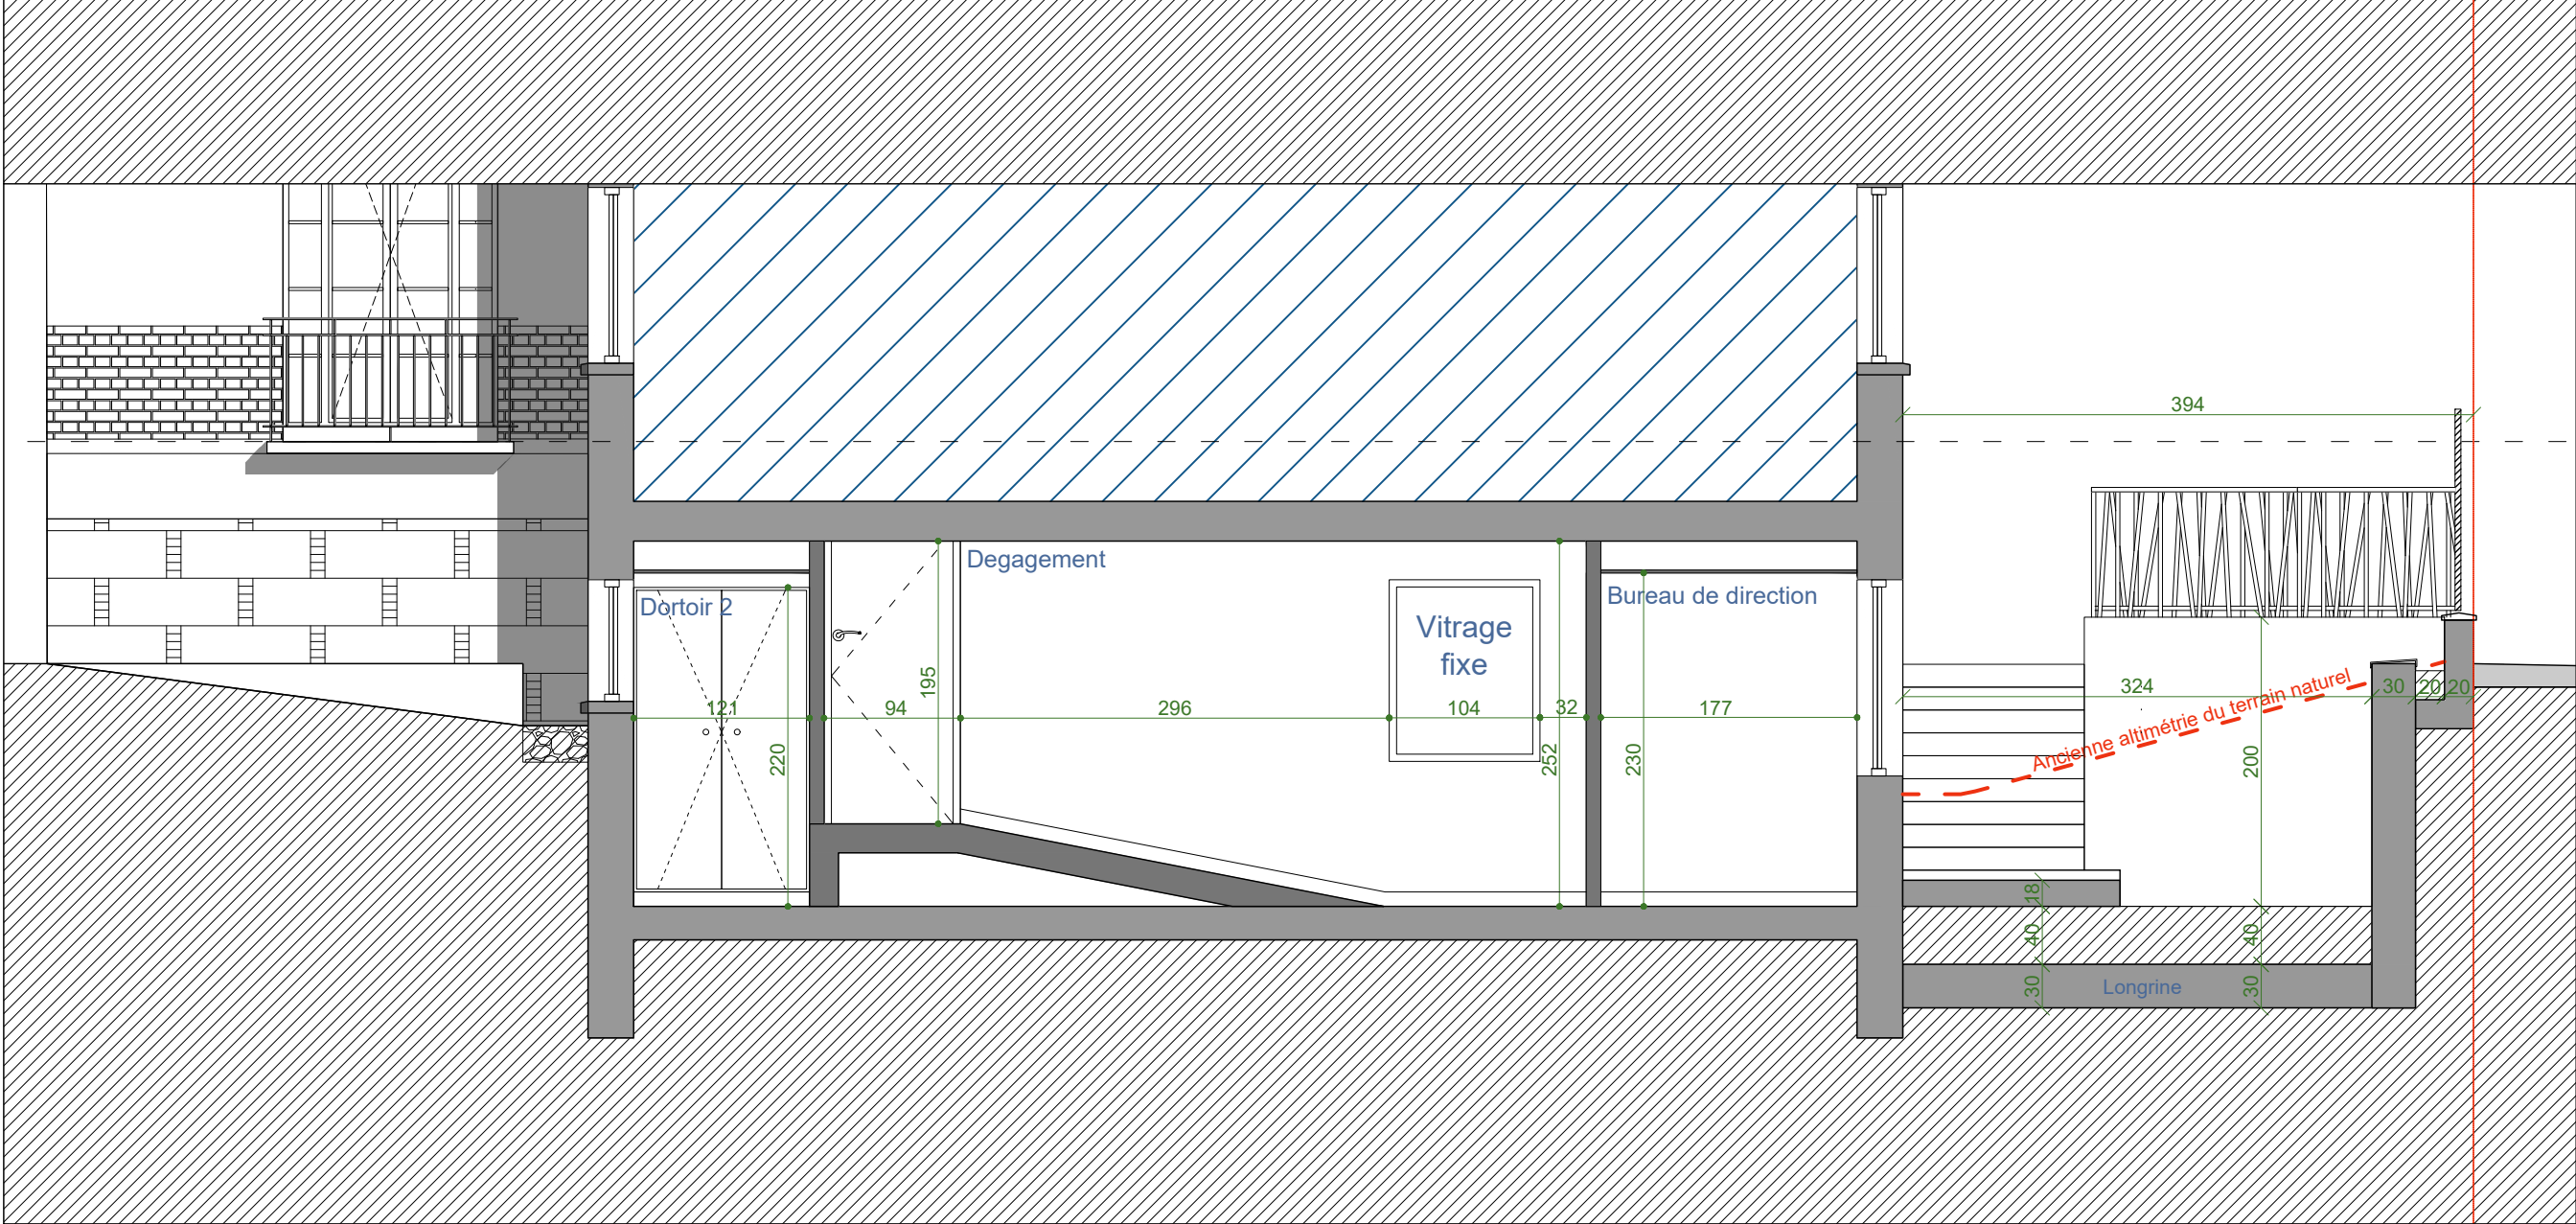

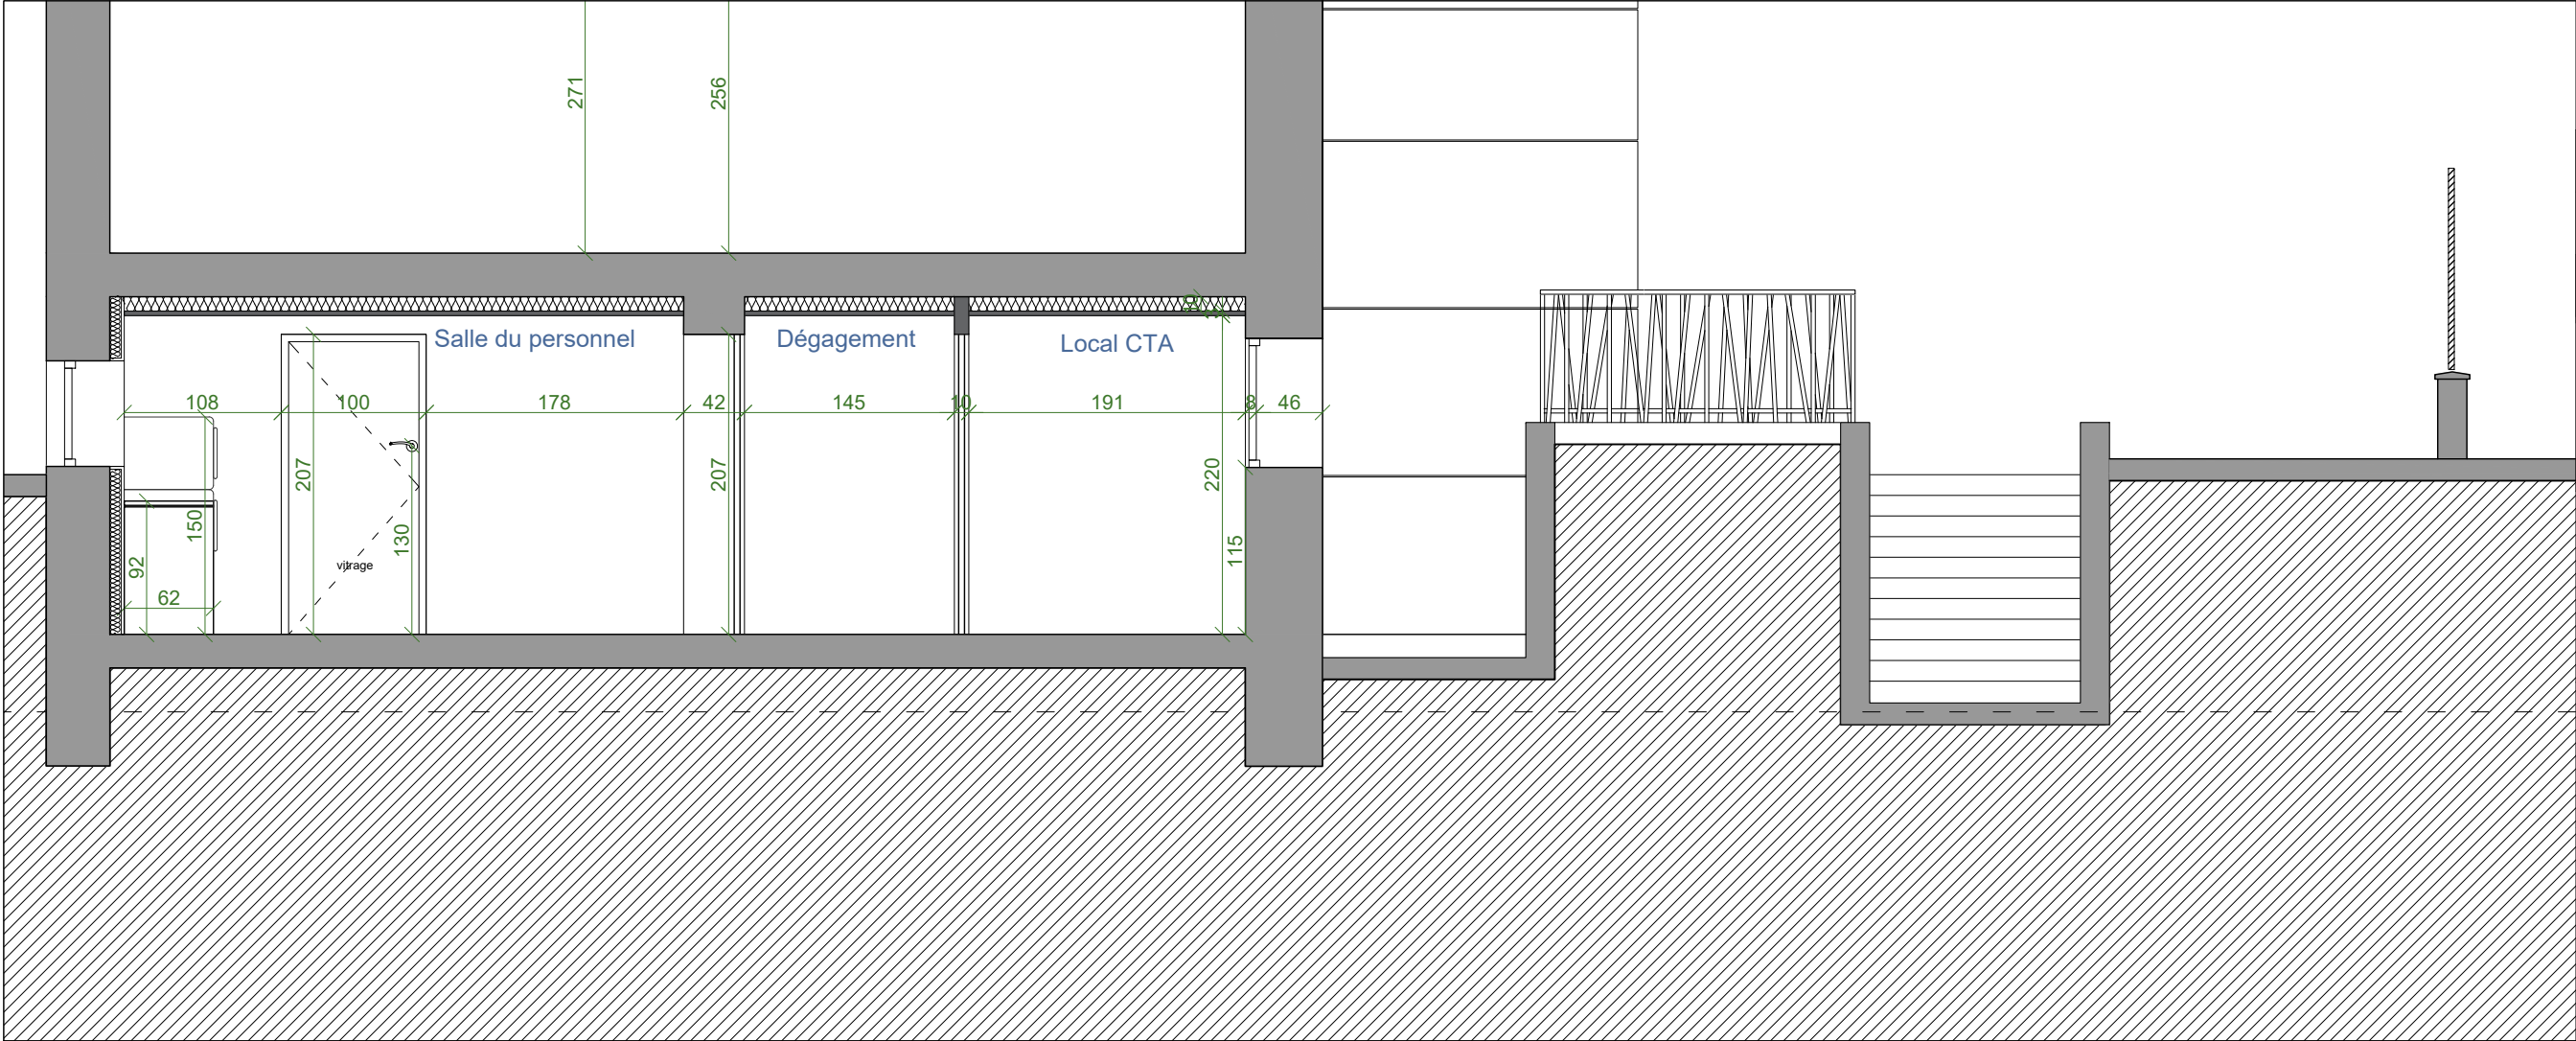

CREATION D'UN MULTI-ACCUEIL ET D'UNE MAISON MEDICALE 30 ter Avenue de Brimont 78400 CHATOU			
MOA	SARL LPC YVELINES 15 Rue de l'Orient78000 VERSAILLES		
MOE	NAHK ARCHITECTURE 24 Rue Yves Toudic, 75010 Paris		
NOM DU DOCUMENT			
COUPE GG' COUPE HH'			
PHASE	PRO.DCE	ECH.	1/50
INDICE	1.1	DATE	29/06/2023
MODIFICATIONS			
INDICE DATE		OBJET	
1.1	29/06/2023	Diffusion initiale	
PLAN DE REPERAGE			

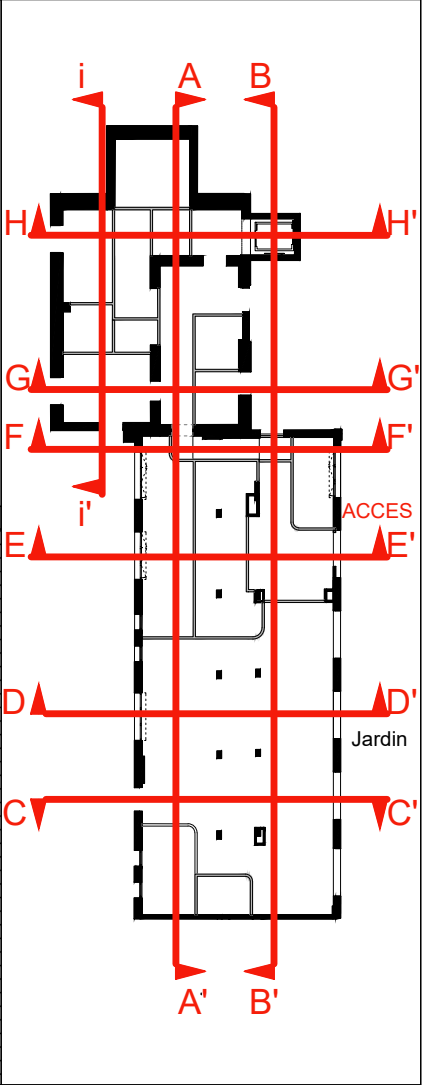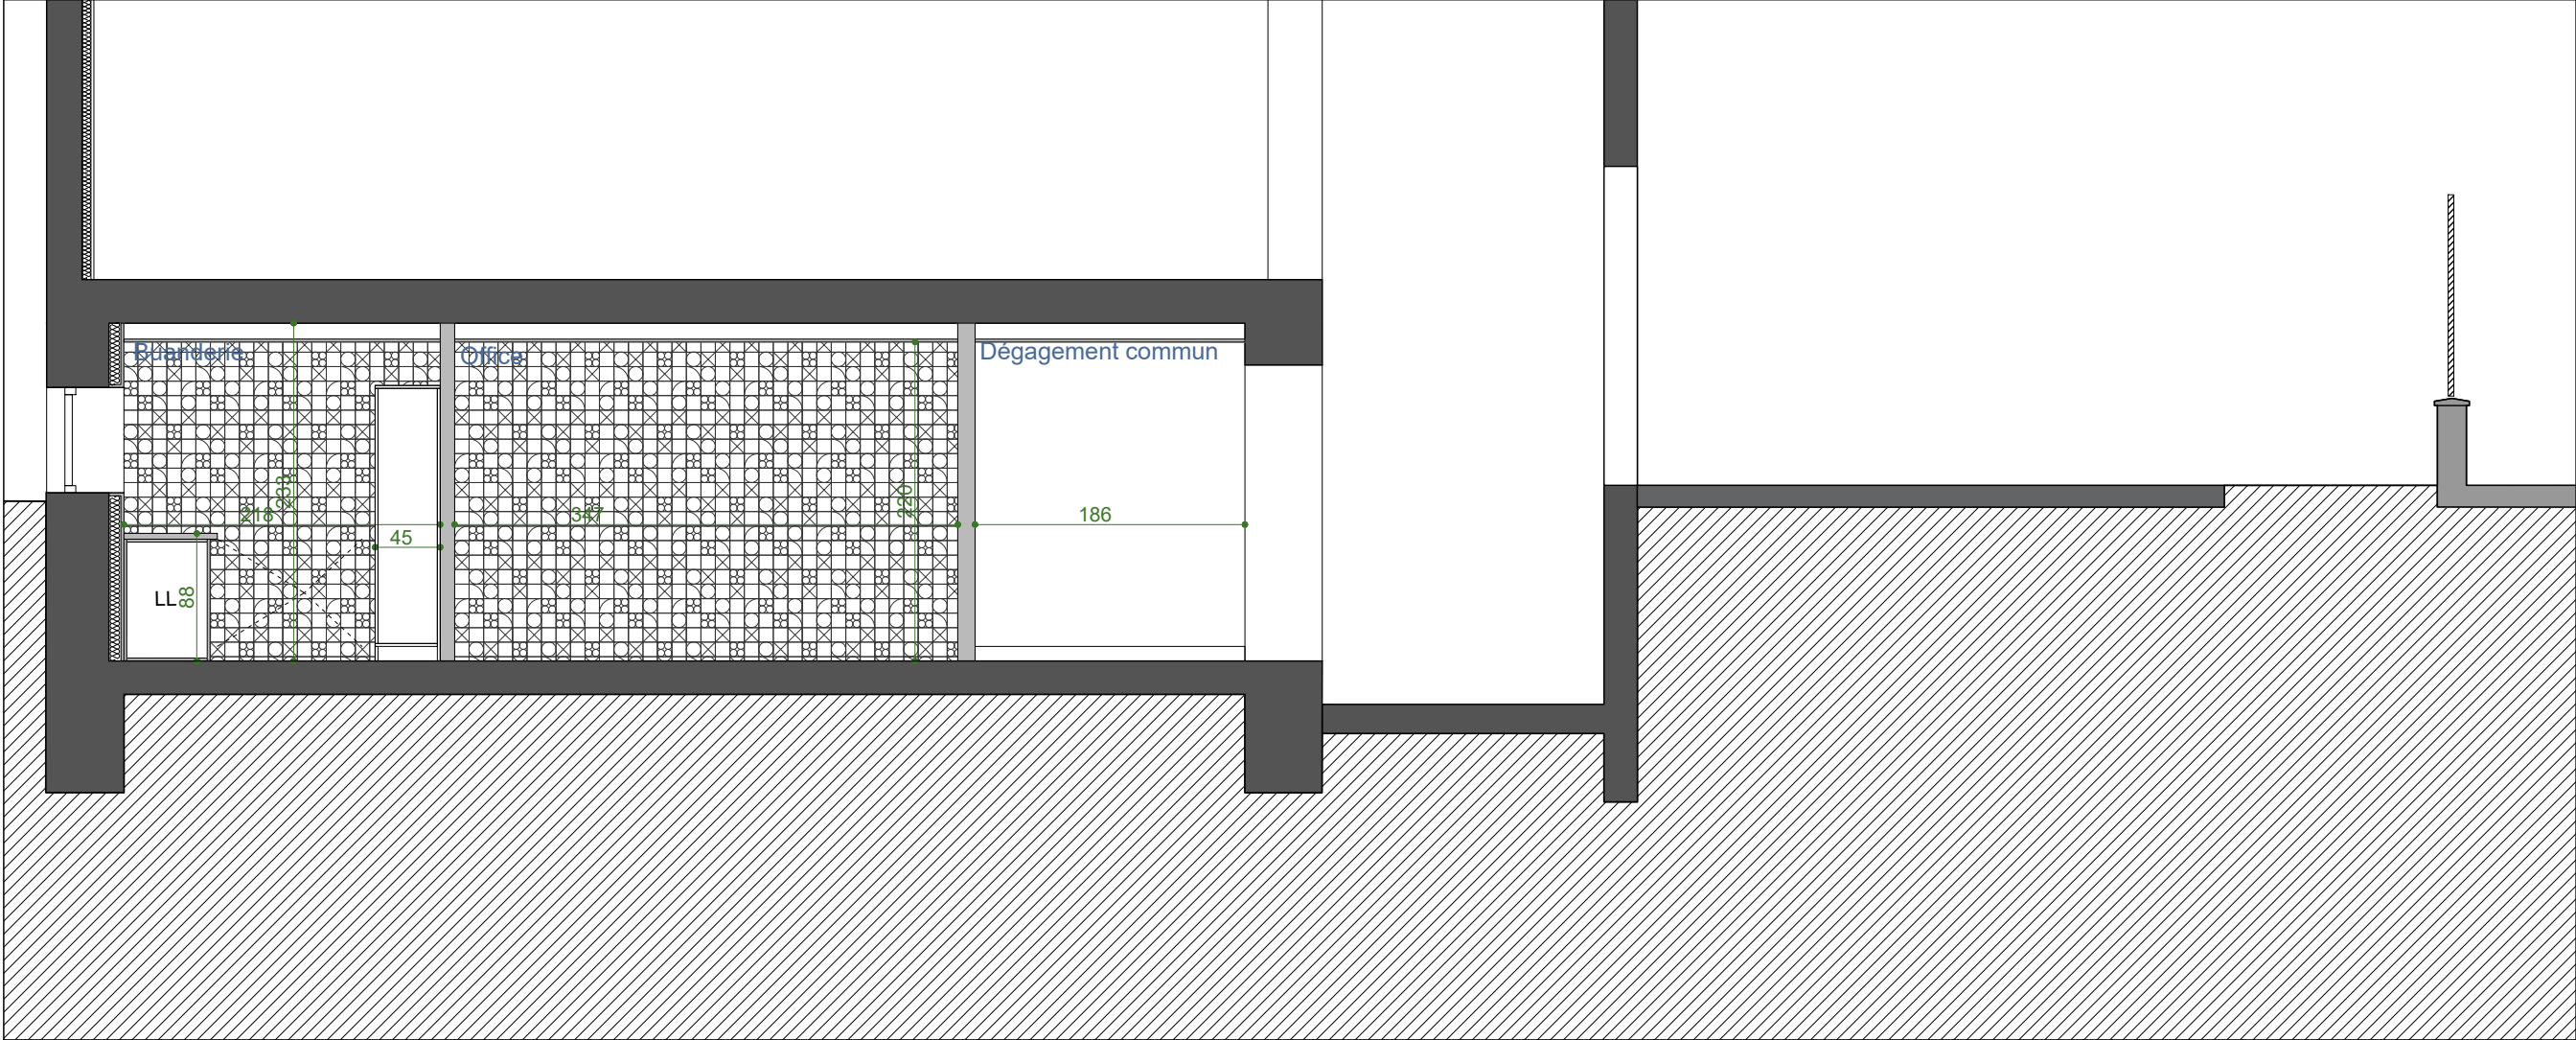

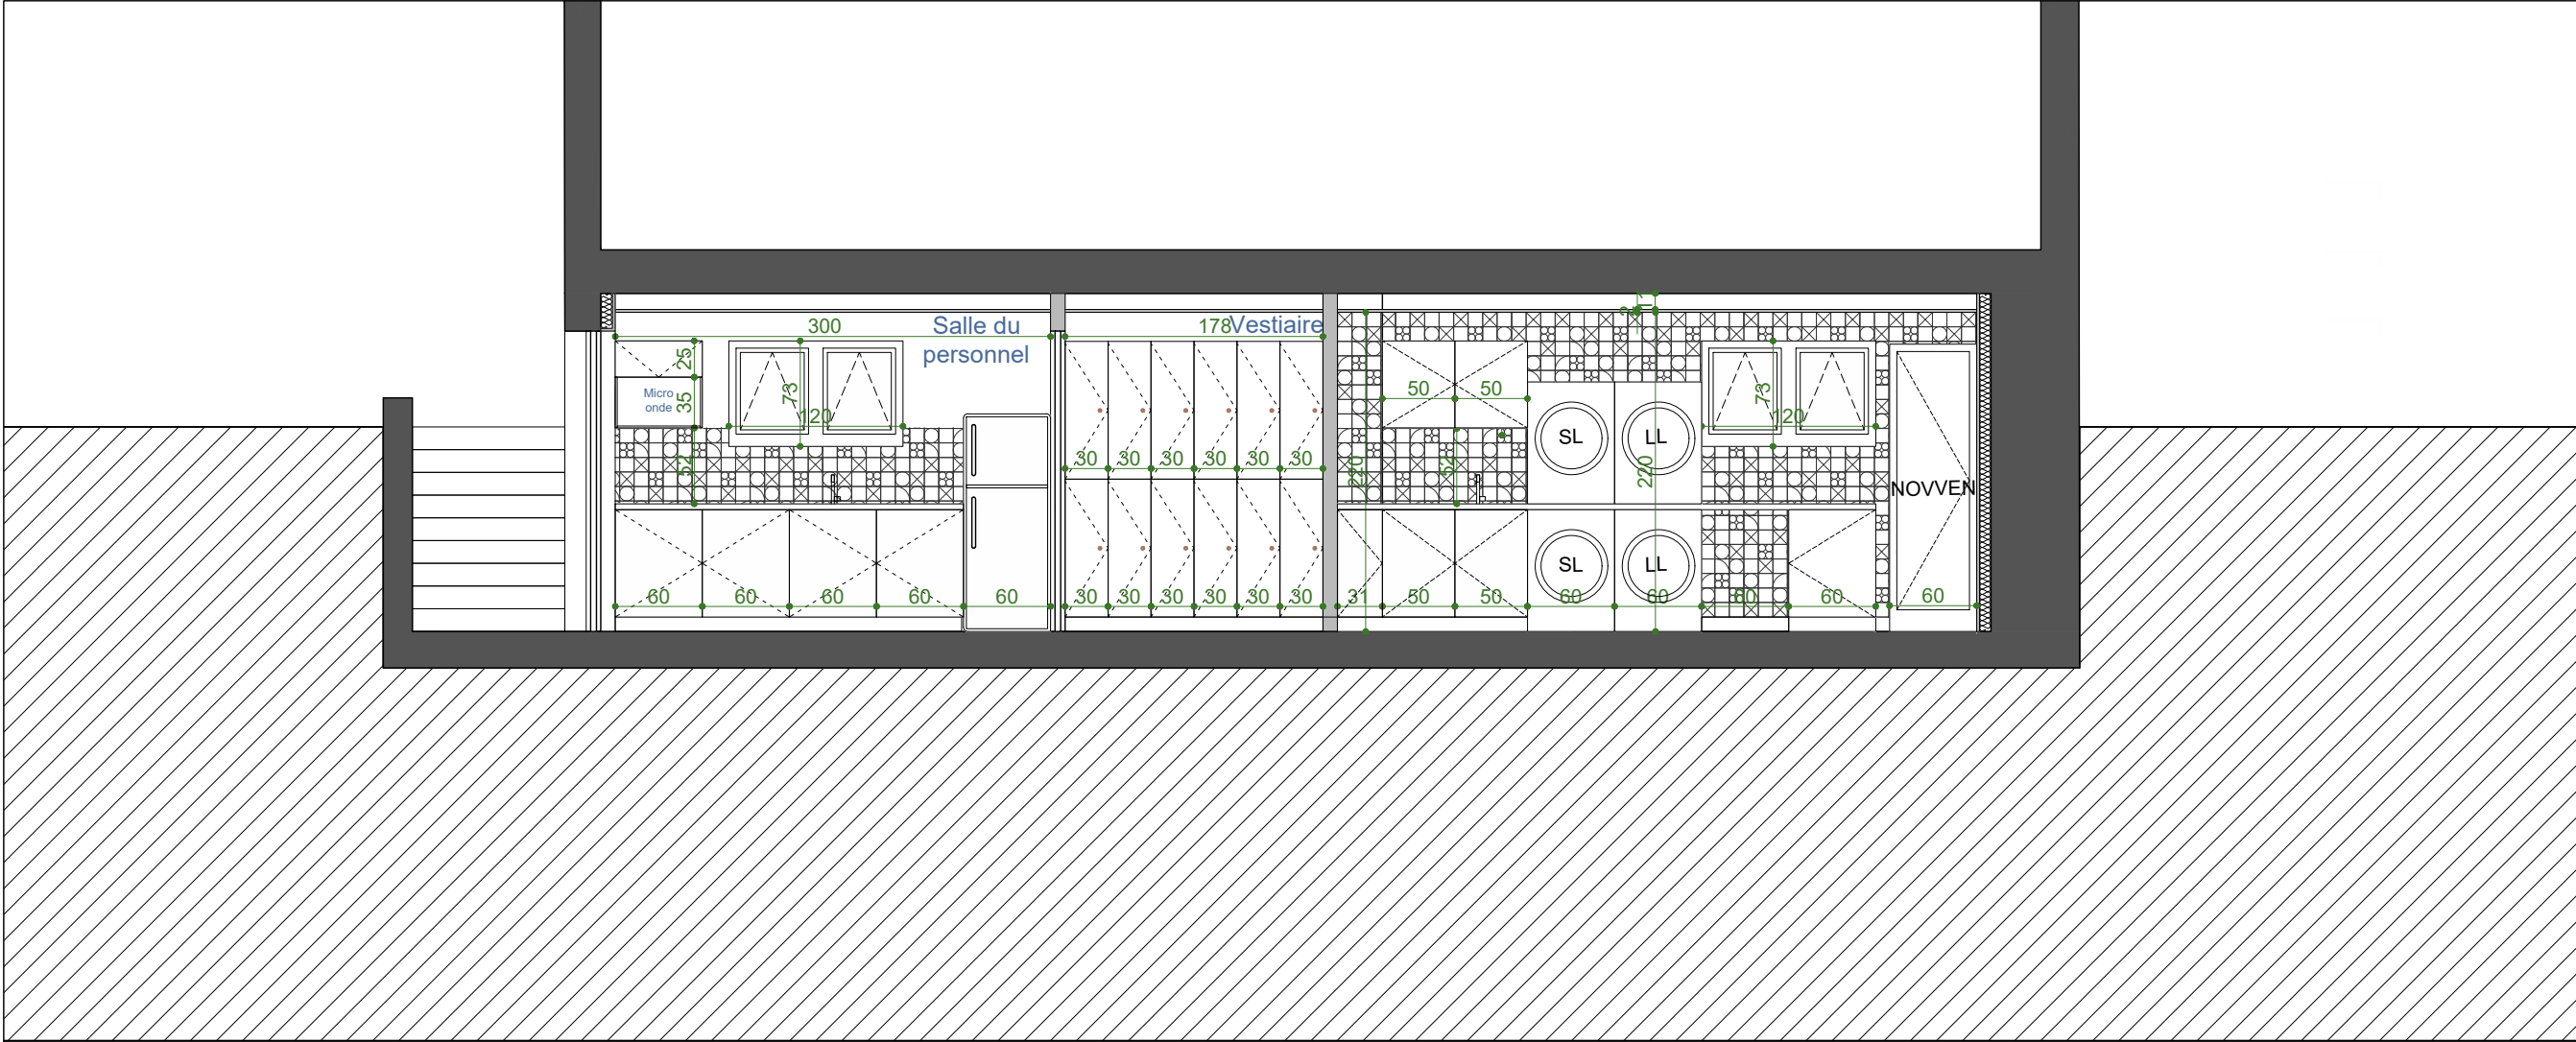

CREATION D'UN MULTI-ACCUEIL ET
D'UNE MAISON MEDICALE
30 ter Avenue de Brimont
78400 CHATOU

MOA

SARL LPC YVELINES
15 Rue de l'Orient78000 VERSAILLES

MOE

NAHK ARCHITECTURE
24 Rue Yves Toudic, 75010 Paris

NOM DU DOCUMENT

COUPE ii'

PHASE	PRO.DCE	ECH.	1/50
INDICE	1.1	DATE	29/06/2023

MODIFICATIONS

INDICE	DATE	OBJET
1.1	29/06/2023	Diffusion initiale

PLAN DE REPERAGE