



MOBILIER - ENTREE


Détails de principe

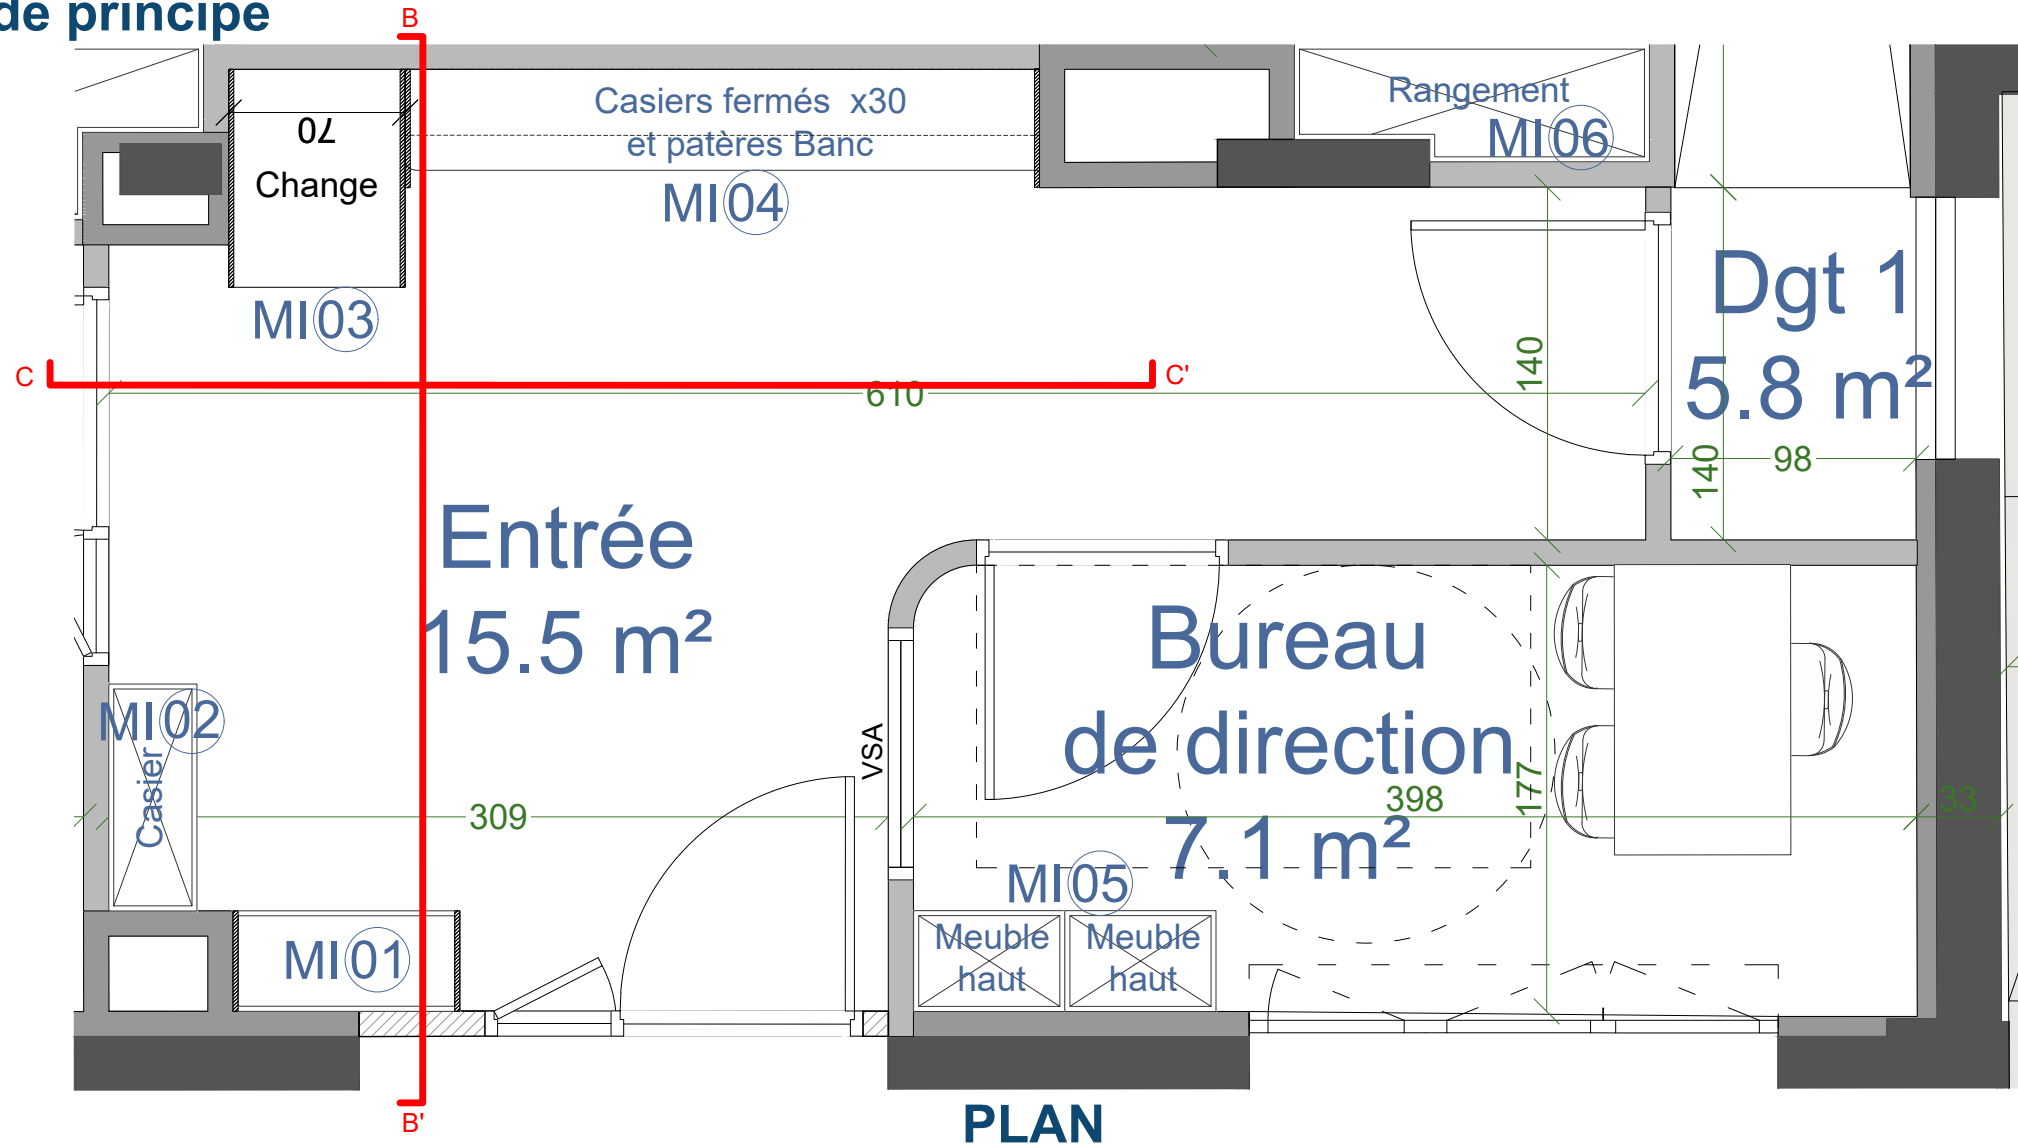

PLAN

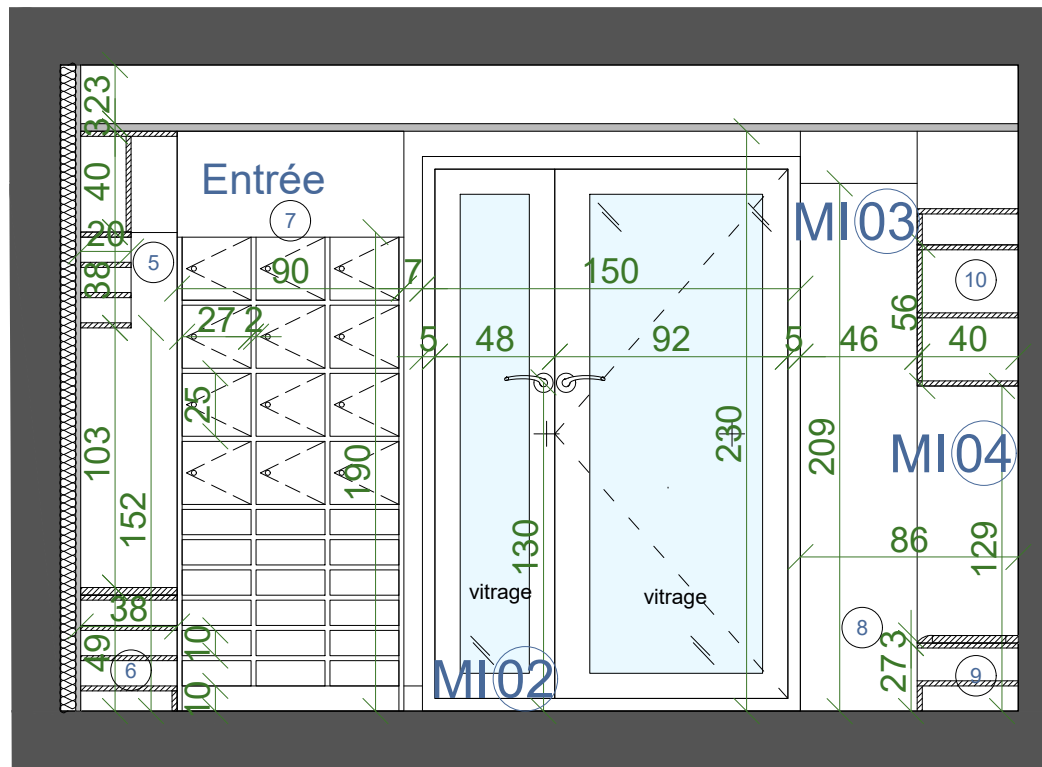

COUPE BB'

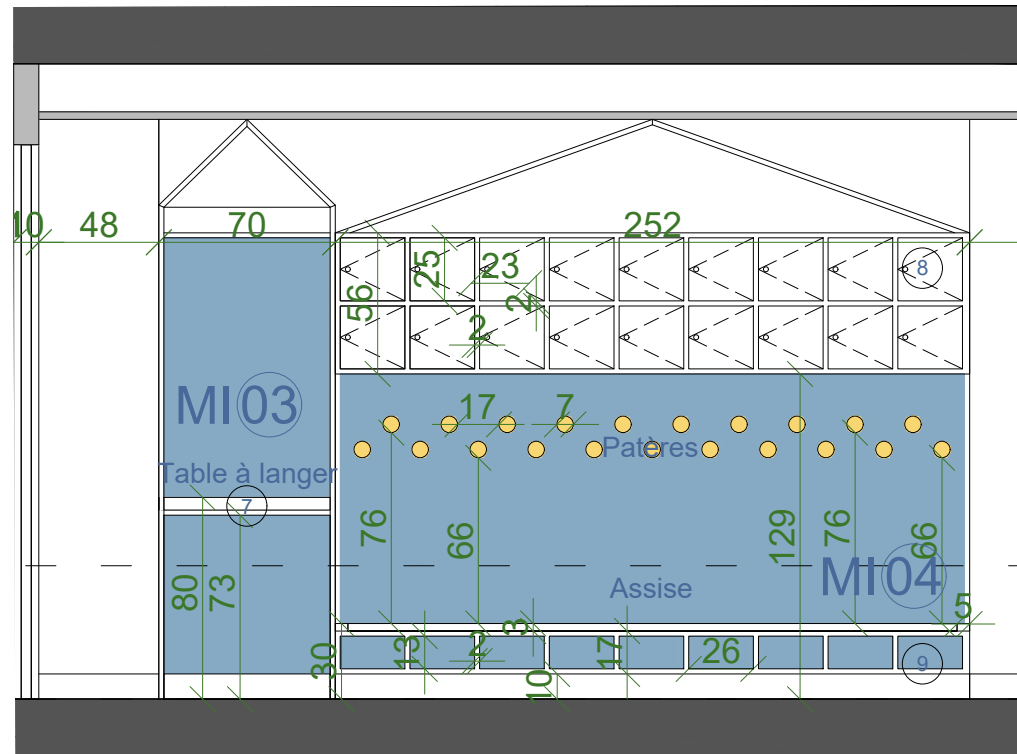


COUPE CC'


CREATION D'UN MULTI-ACCUEIL ET REAMENAGEMENT D'UNE MAISON MEDICALE 30 TER, AVENUE DE BRIMONT 78400 CHATOU			
MOA	LES PETITES CANAILLES 36 Rue Pierret, 92200 Neuilly-sur-Seine		
MOE	NAHK ARCHITECTURE 24 Rue Yves Toudic, 75010 Paris		
NOM DU DOCUMENT			
DETAIL MOBILIER ENTREE			
PHASE	PRO.DCE	ECH.	1/30
INDICE	1.1	DATE	09/06/2023
MODIFICATIONS			
INDICE	DATE	OBJET	
1.1	09/06/2023	Diffusion initiale	
1. Placard haut IKEA ENHET ref. 093.210.11			
2. Emplacement imprimante non encastré			
3. Placard bas IKEA METHOD ref. 494.698.78			
4. Placard			
5. Niches à sur-chaussures			
6. Meuble sur mesure à casiers sur-chaussures et niches à chaussures			
7. Table à langer sur mesure			
8. Meuble sur mesure à casiers fermés et casiers à chaussures			
9. Casiers à chaussures			
10. Casiers fermés			
ECHELLE GRAPHIQUE 30 CM 1.5 M			

MOBILIER - ENTREE ET BUREAU DE DIRECTION

Détails de principe

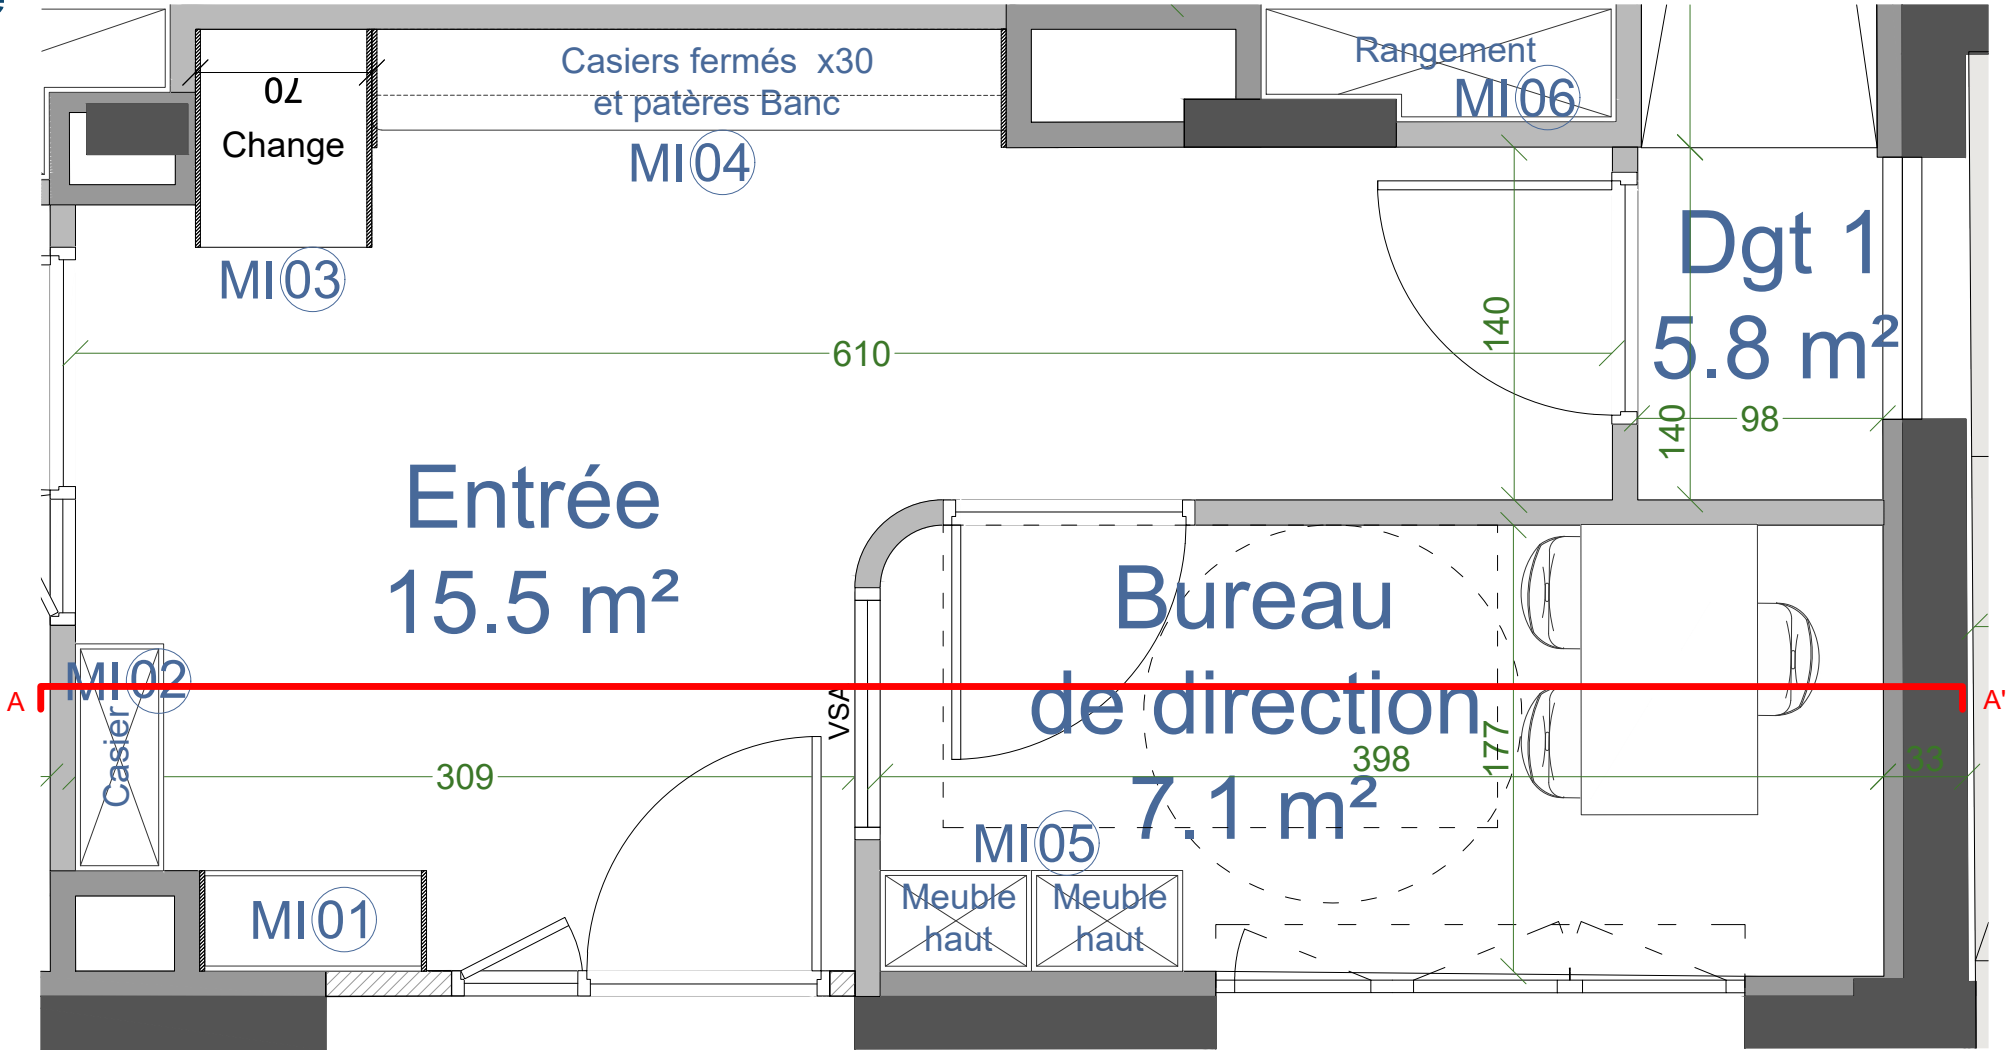

PLAN

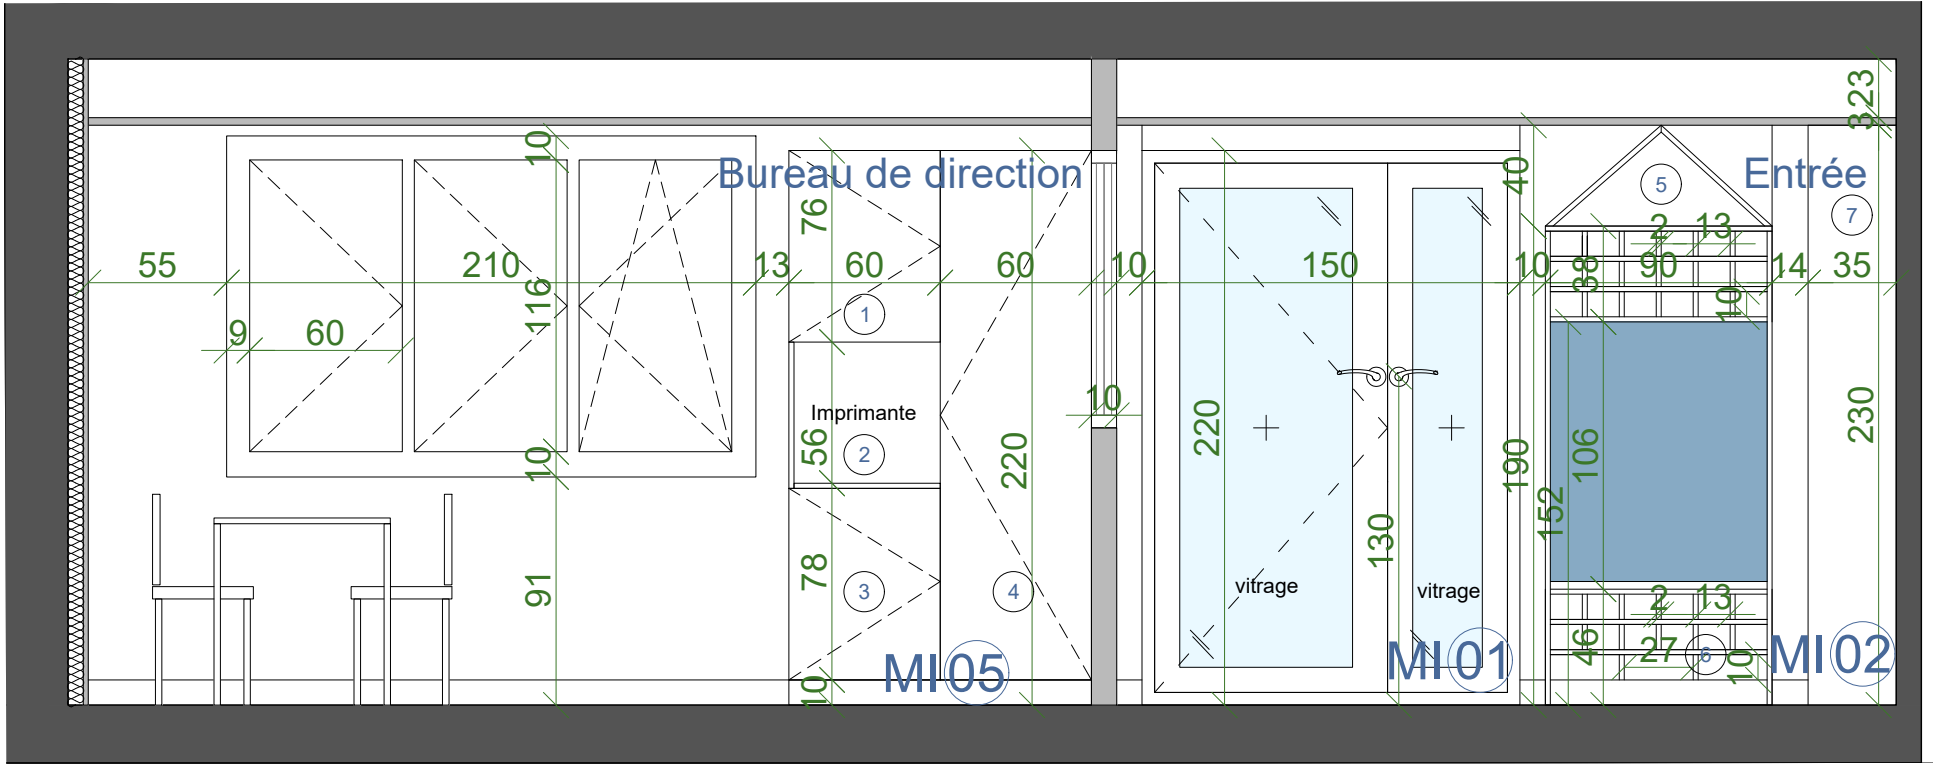


COUPE AA'


CREATION D'UN MULTI-ACCUEIL ET REAMENAGEMENT D'UNE MAISON MEDICALE			
30 TER, AVENUE DE BRIMONT 78400 CHATOU			
MOA	LES PETITES CANAILLES 36 Rue Pierret, 92200 Neuilly-sur-Seine		
MOE	NAHK ARCHITECTURE 24 Rue Yves Toudic, 75010 Paris		
NOM DU DOCUMENT			
DETAIL MOBILIER ENTREE ET BUREAU DE DIRECTION			
PHASE	PRO.DCE	ECH.	1/30
INDICE	1.1	DATE	09/06/2023
MODIFICATIONS			
INDICE	DATE	OBJET	
1.1	09/06/2023	Diffusion initiale	
1. Placard haut IKEA ENHET ref. 093.210.11			
2. Emplacement imprimante non encastré			
3. Placard bas IKEA METHOD ref. 494.698.78			
4. Placard			
5. Niches à sur-chaussures			
6. Meuble sur mesure à casiers sur-chaussures et niches à chaussures			
7. Table à langer sur mesure			
8. Meuble sur mesure à casiers fermés et casiers à chaussures			
9. Casiers à chaussures			
10. Casiers fermés			
ECHELLE GRAPHIQUE 30 CM 1.5 M			

MOBILIER - BIBERONNERIE


Détails de principe

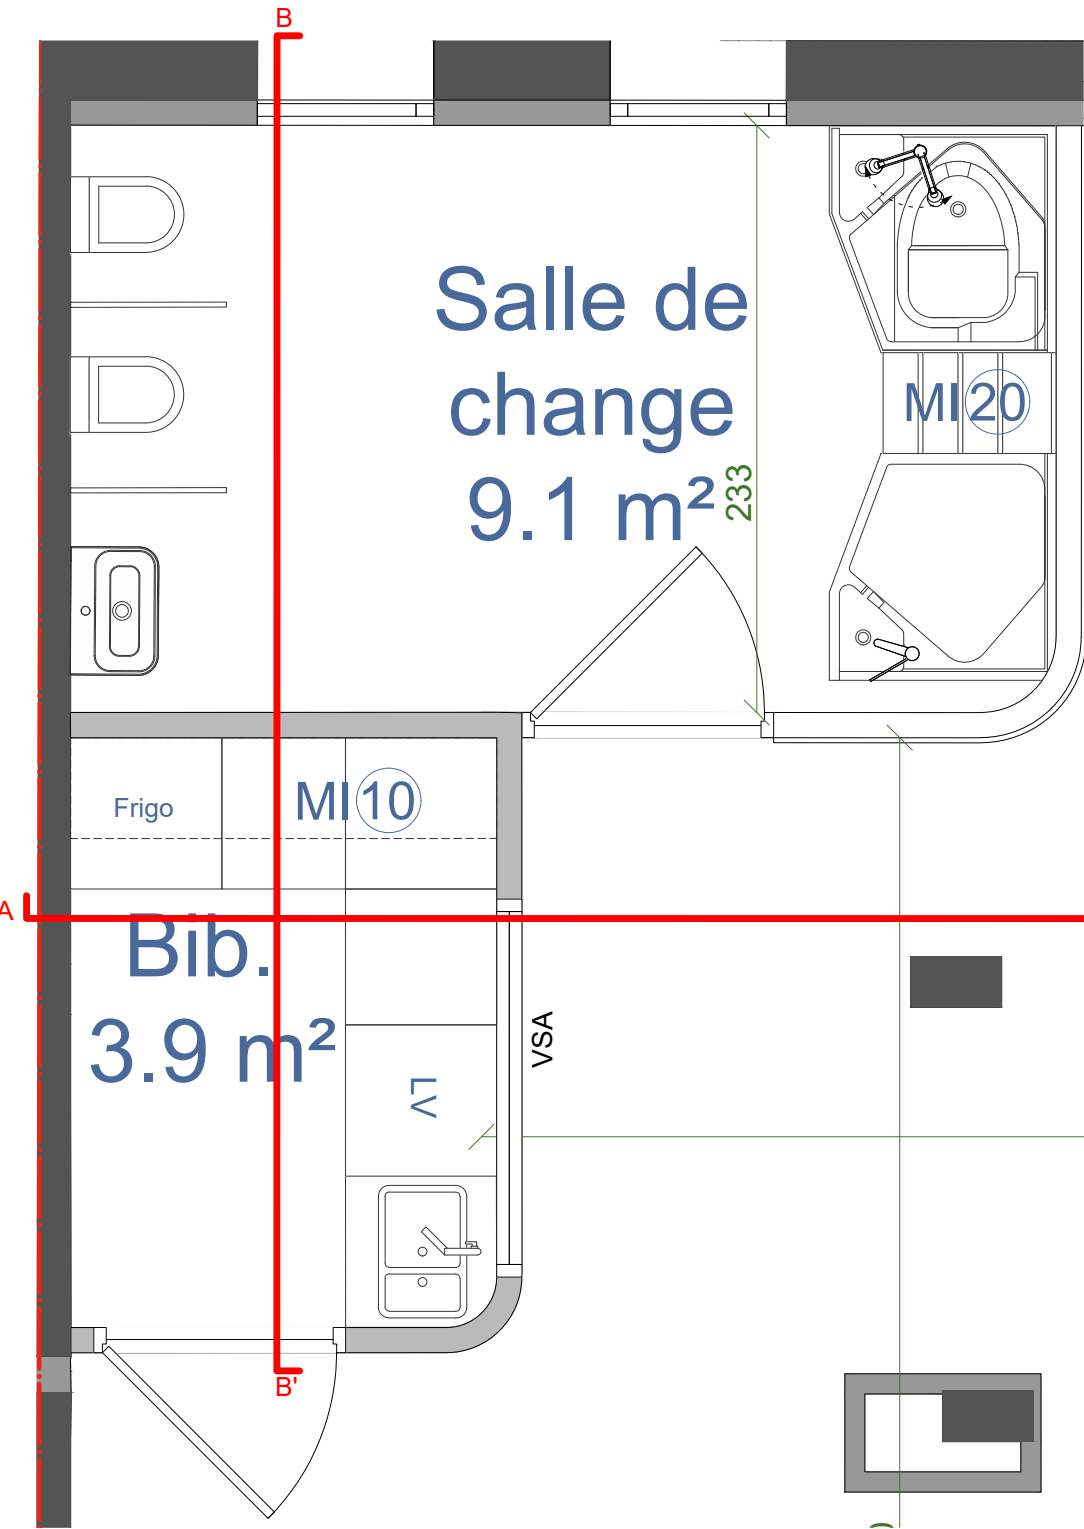

PLAN

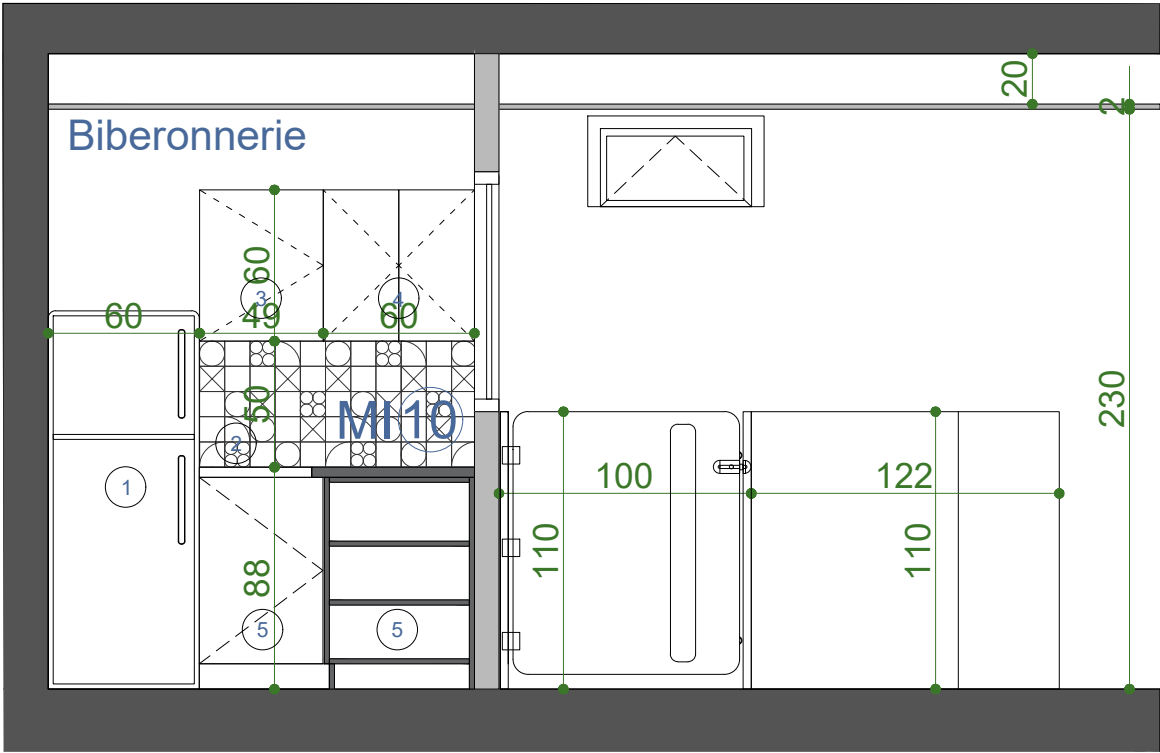

COUPE AA'

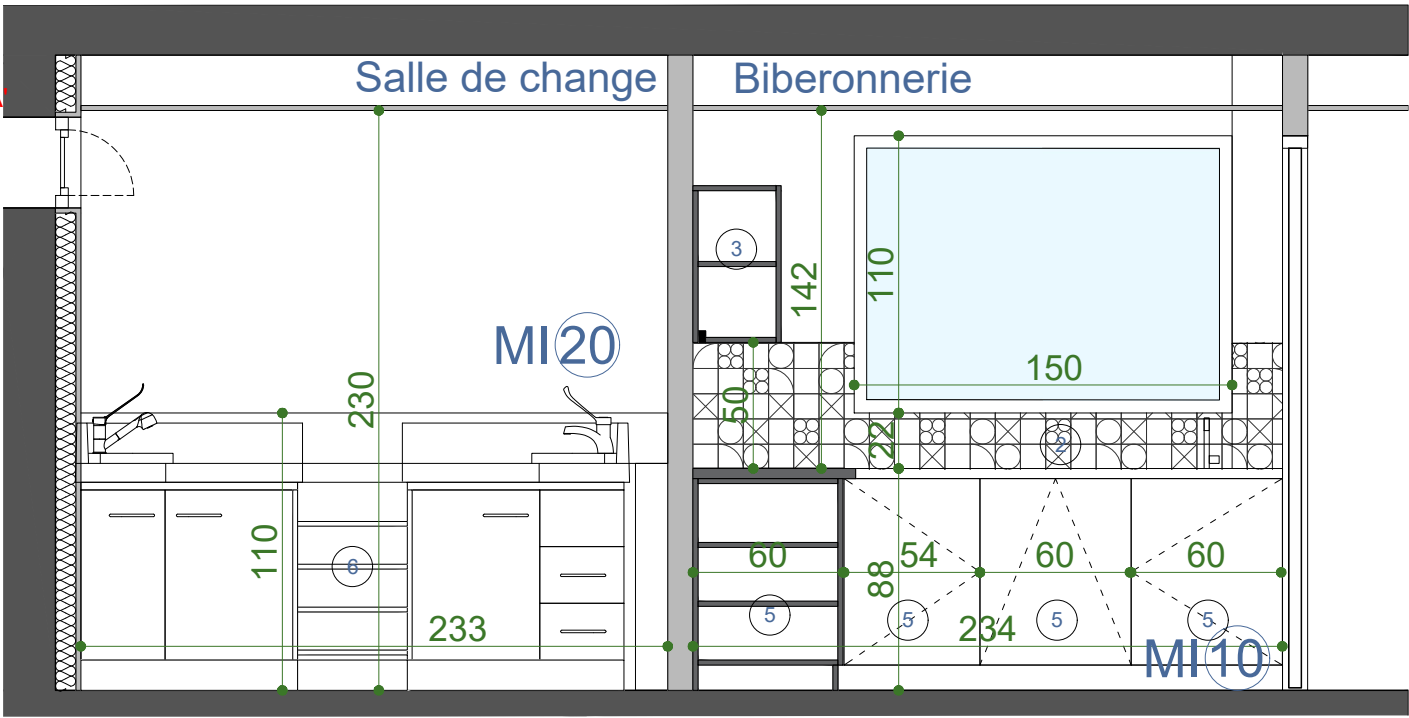

COUPE BB'

CREATION D'UN MULTI-ACCUEIL ET
REAMENAGEMENT D'UNE MAISON
MEDICALE
30 TER, AVENUE DE BRIMONT
78400 CHATOU

MOA LES PETITES CANAILLES
36 Rue Pierret, 92200 Neuilly-sur-Seine

MOE NAHK ARCHITECTURE
24 Rue Yves Toudic, 75010 Paris

NOM DU DOCUMENT

DETAIL MOBILIER
BIBERONNERIE

PHASE PRO.DCE ECH. 1/30

INDICE 1.1 DATE 09/06/2023


MODIFICATIONS
INDICE DATE OBJET

1.1 09/06/2023 Diffusion initiale


1. Emplacement frigo 150 cm
2. Plan de travail
3. Placard haut IKEA ENHET
ref. 093.210.11
4. Placard haut
5. Placard bas IKEA METHOD
ref. 494.698.78
6. Loxos ref. 2

ECHELLE GRAPHIQUE
30 CM 1.5 M

PEINTURE - DORTOIR 1

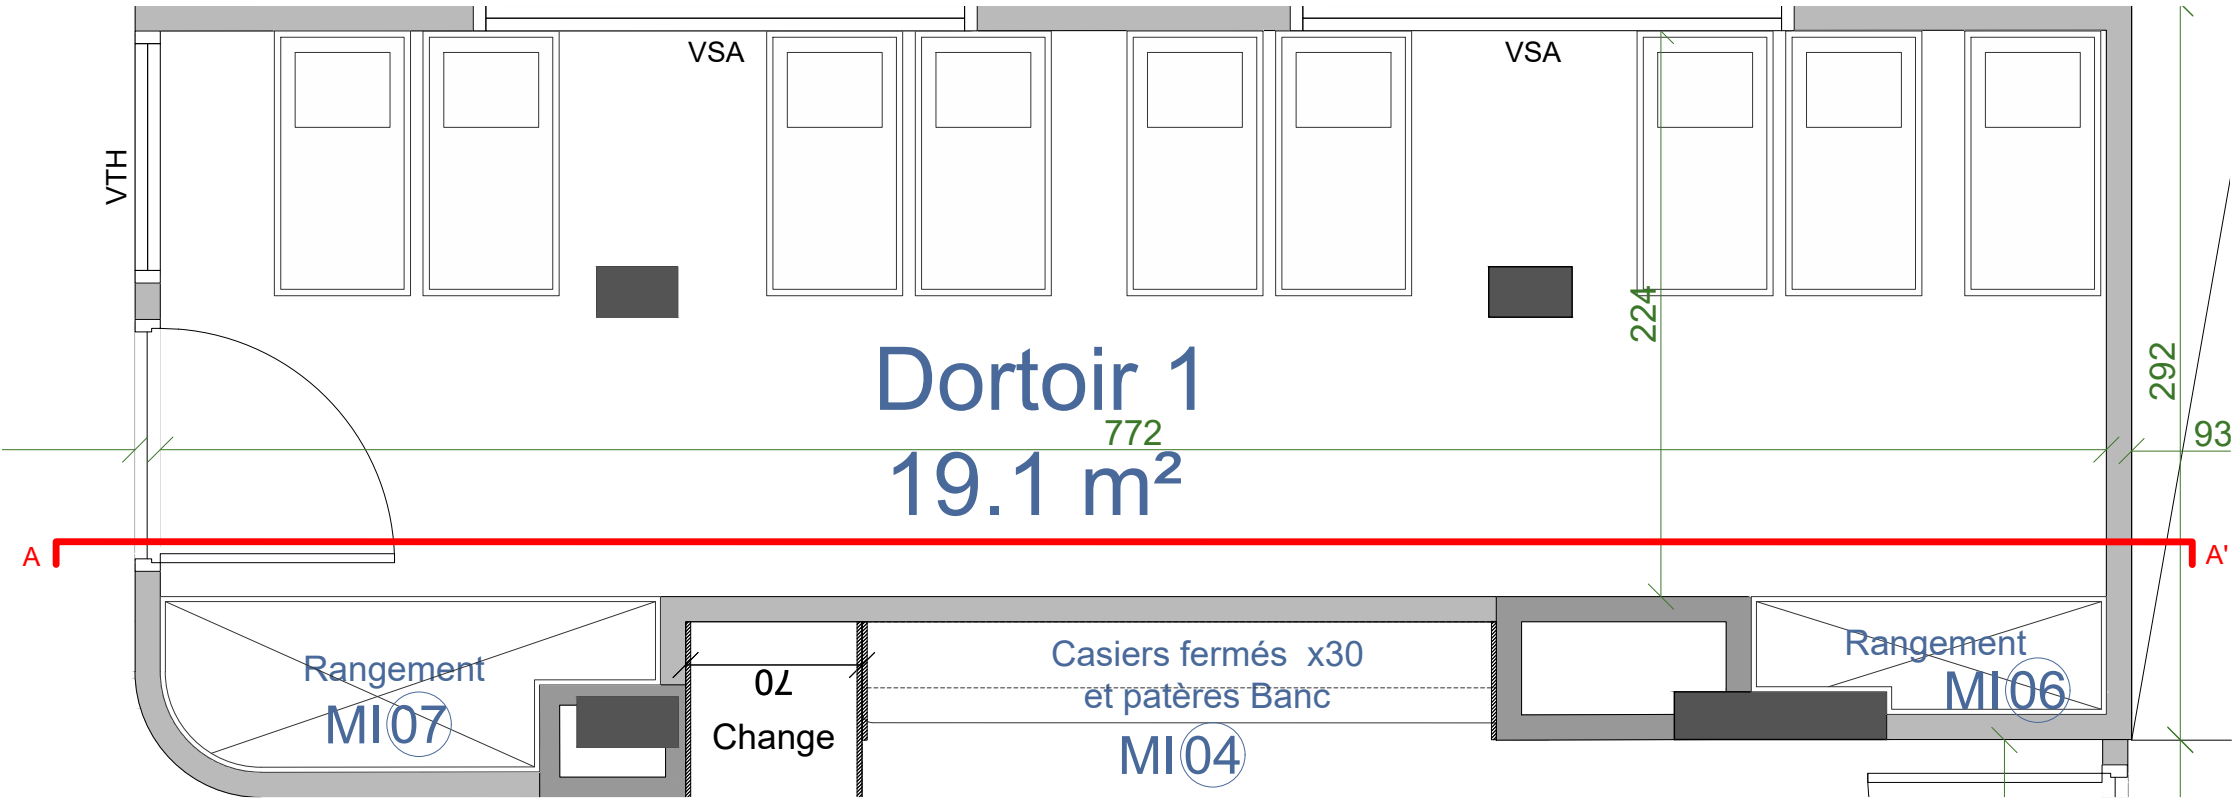

PLAN

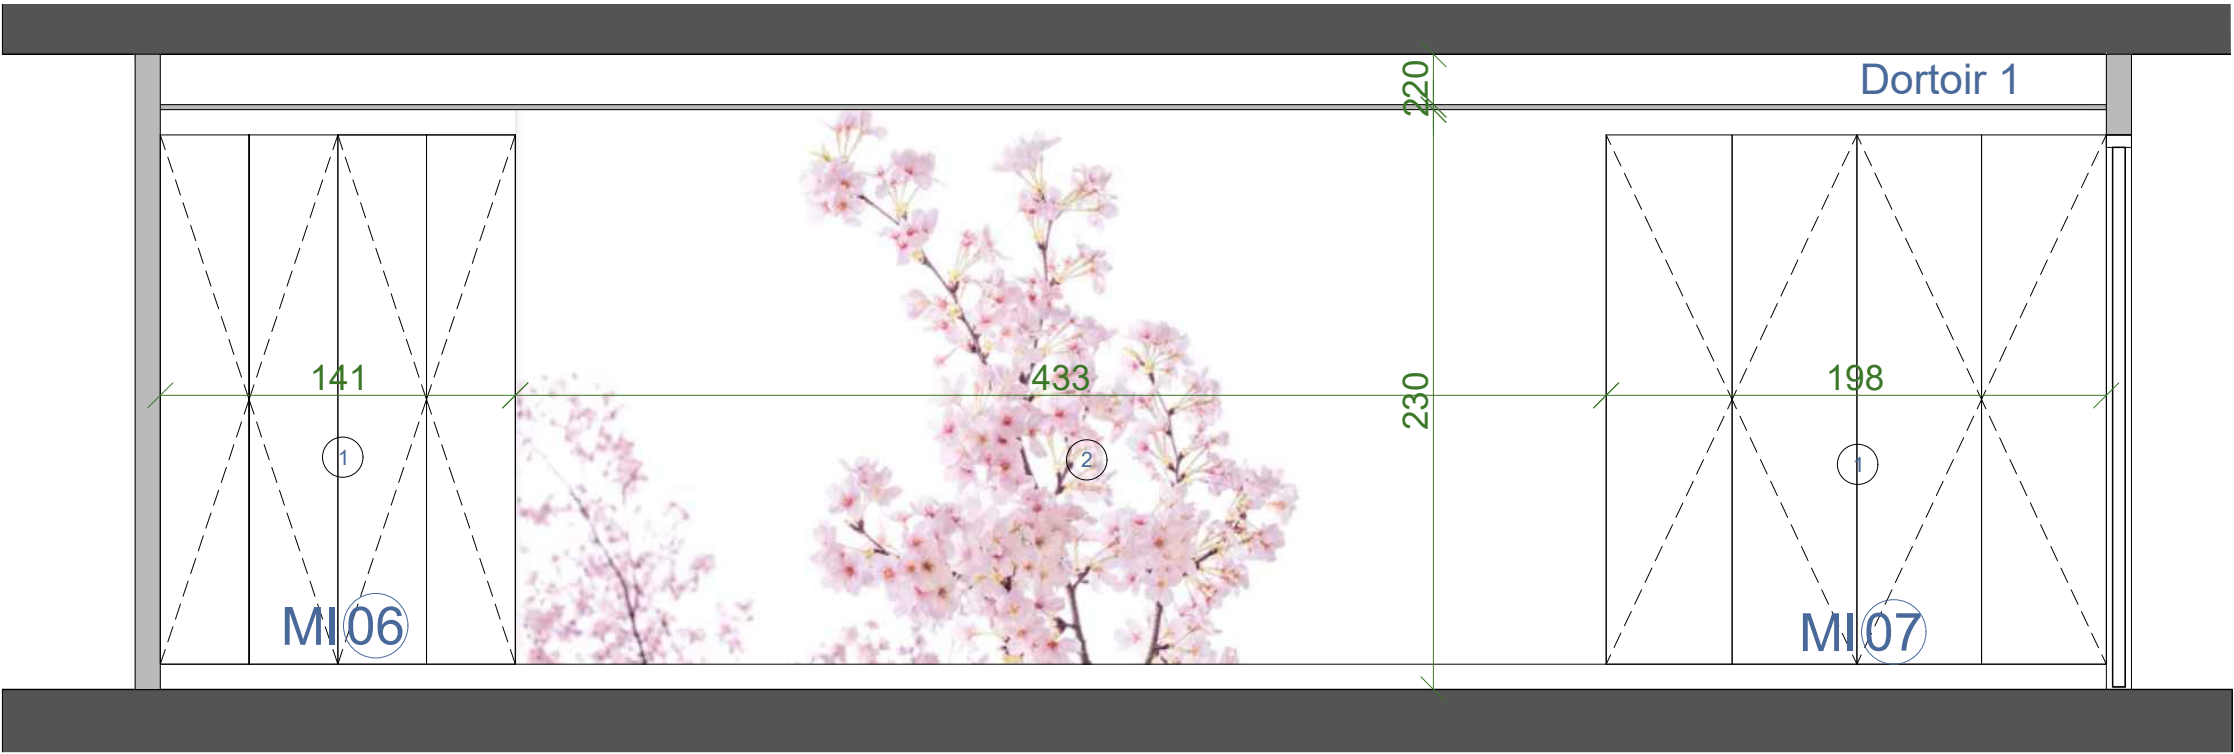

COUPE AA'

CREATION D'UN MULTI-ACCUEIL ET
REAMENAGEMENT D'UNE MAISON
MEDICALE
30 TER, AVENUE DE BRIMONT
78400 CHATOU

MOA LES PETITES CANAILLES
36 Rue Pierret, 92200 Neuilly-sur-Seine

MOE NAHK ARCHITECTURE
24 Rue Yves Toudic, 75010 Paris

NOM DU DOCUMENT

DETAIL MOBILIER
DORTOIR 1

PHASE	PRO.DCE	ECH.	1/30
-------	---------	------	------

INDICE	1.1	DATE	09/06/2023
--------	-----	------	------------


MODIFICATIONS
INDICE DATE OBJET

1.1	09/06/2023	Diffusion initiale
-----	------------	--------------------

- Meubles sur-mesure :
- Armoire haute
 - Papier peint ref. Divine Cherry Blossoms

ECHELLE GRAPHIQUE
30 CM 1.5 M

PEINTURE - DORTOIR 2

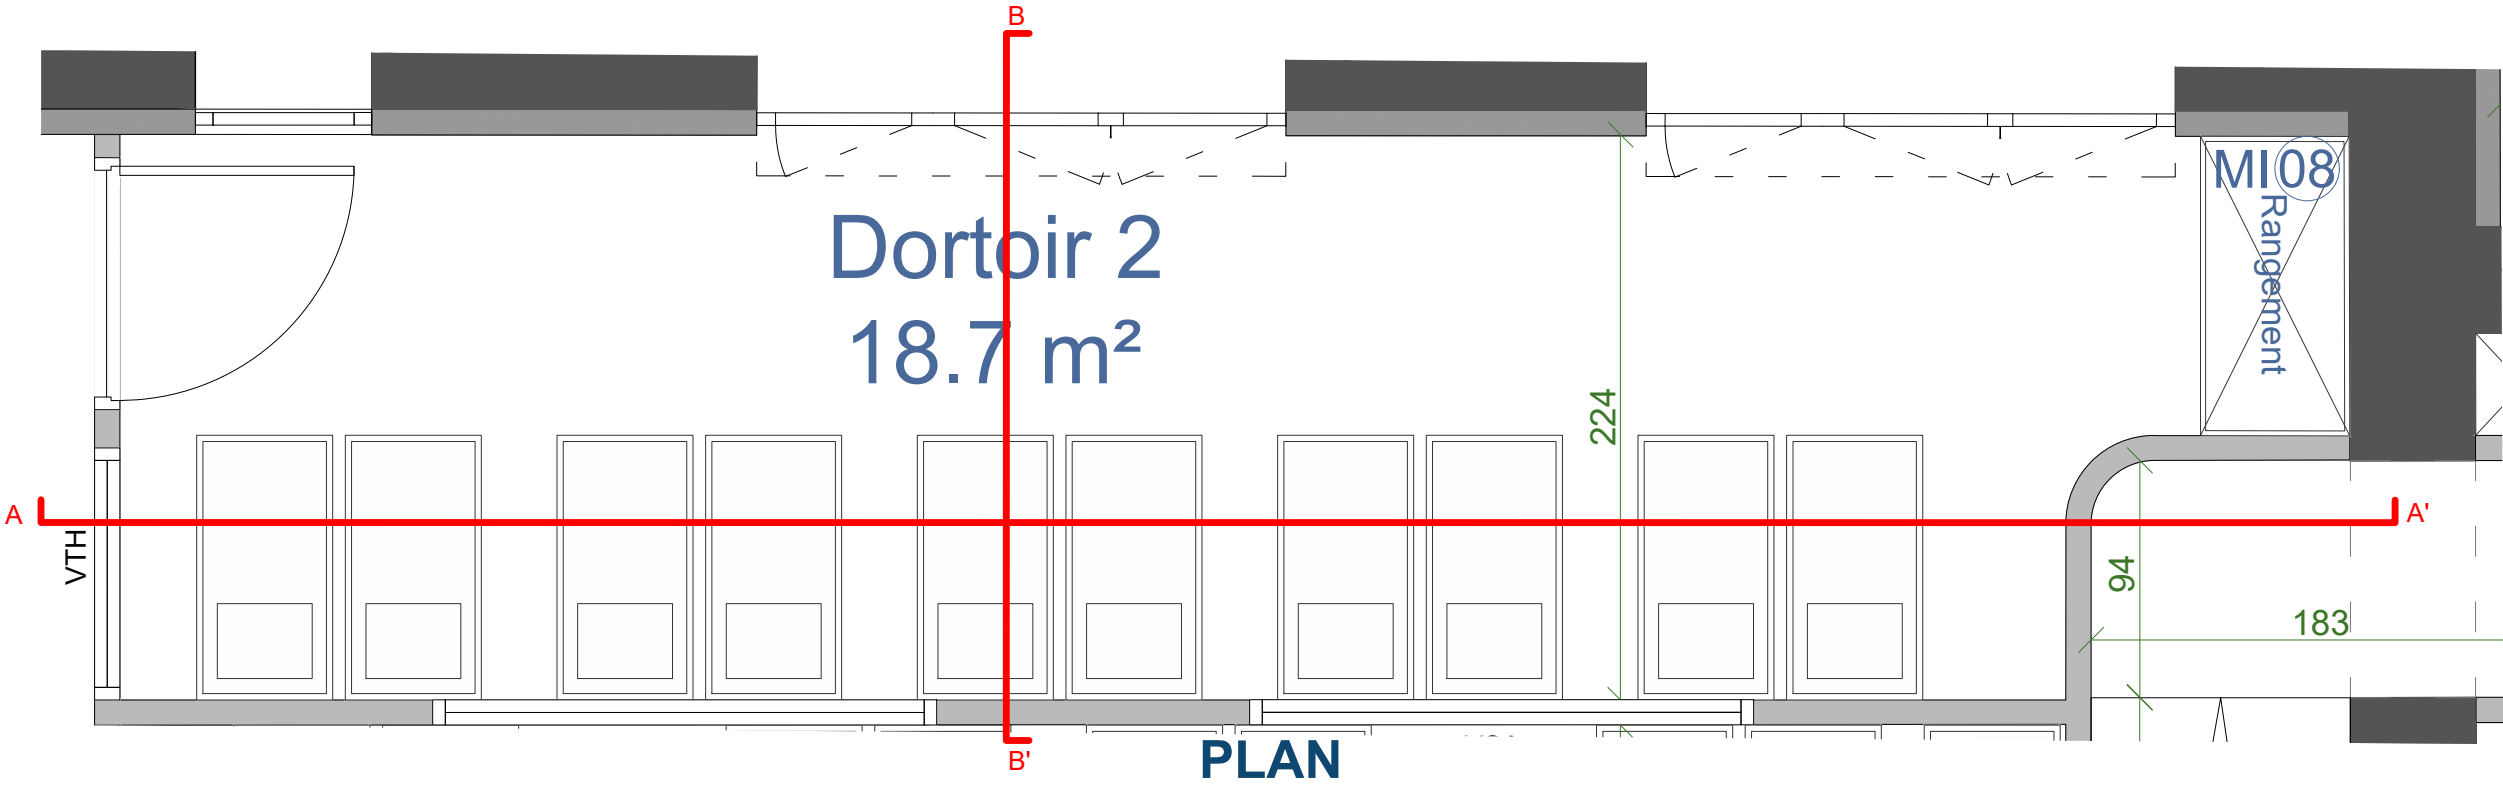

CREATION D'UN MULTI-ACCUEIL ET REAMENAGEMENT D'UNE MAISON MEDICALE
30 TER, AVENUE DE BRIMONT
78400 CHATOU

MOA

LES PETITES CANAILLES
36 Rue Pierret, 92200
Neuilly-sur-Seine

MOE

NAHK ARCHITECTURE
24 Rue Yves Toudic, 75010 Paris

NOM DU DOCUMENT

DETAIL MOBILIER
DORTOIR 2

PHASE	PRO.DCE	ECH.	ECHELLE
INDICE	1.1	DATE	09/06/2023


MODIFICATIONS
INDICE DATE OBJET

1.09/06/2023Diffusion initiale


Meuble sur-mesure :
1. Armoire haute

2. Papier peint ref. Divine Cherry Blossoms

ECHELLE GRAPHIQUE
30 CM 1.5 M

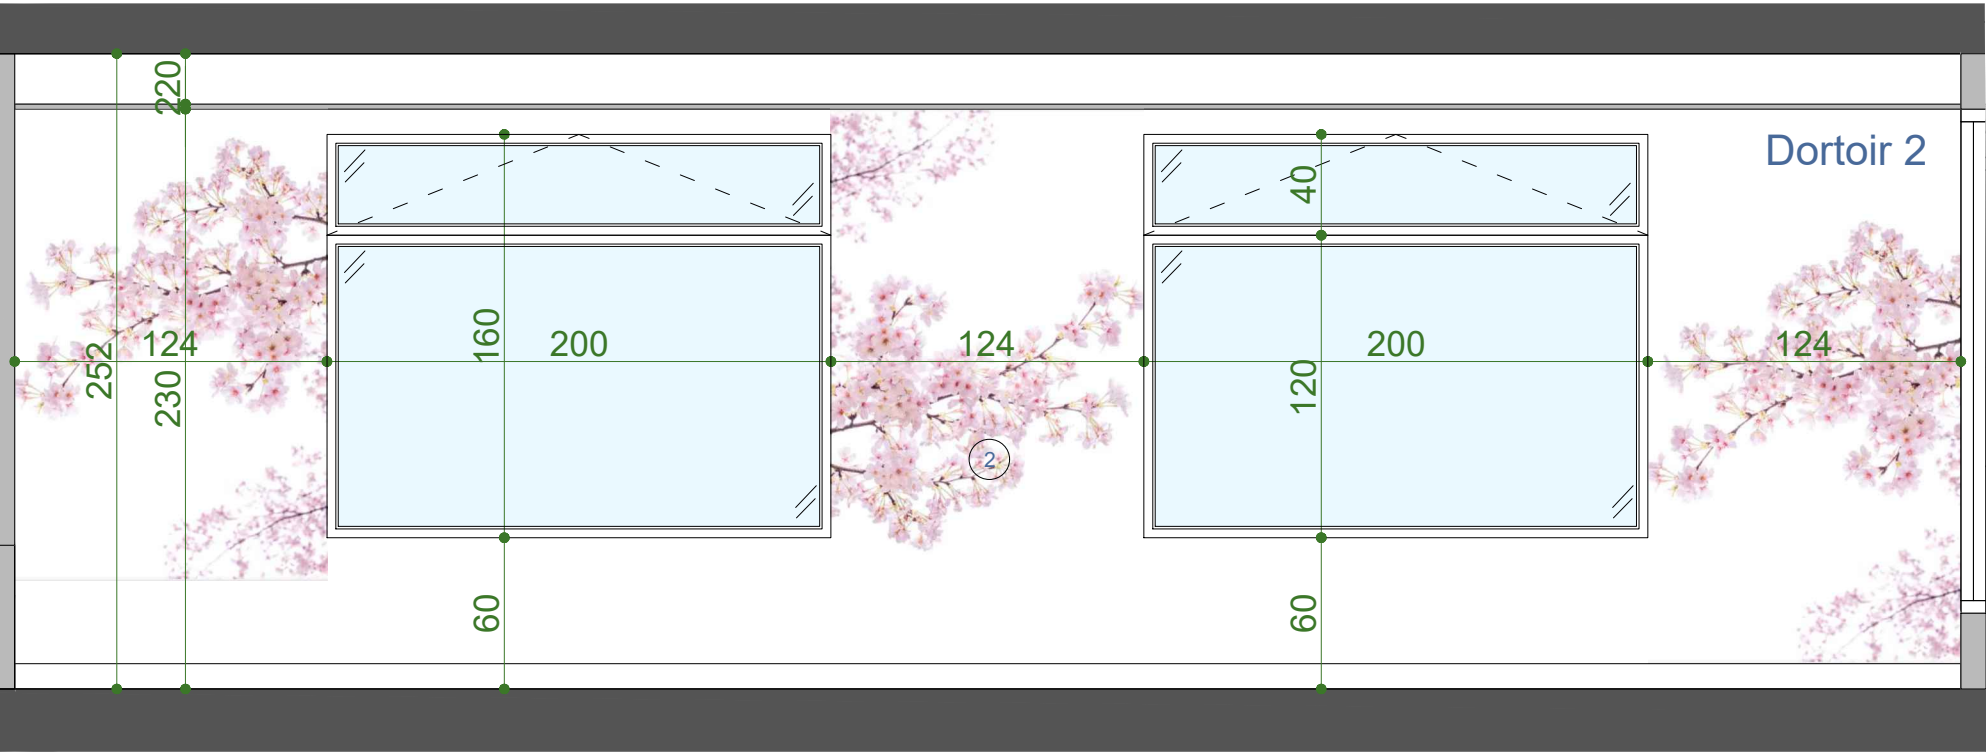


COUPE AA'

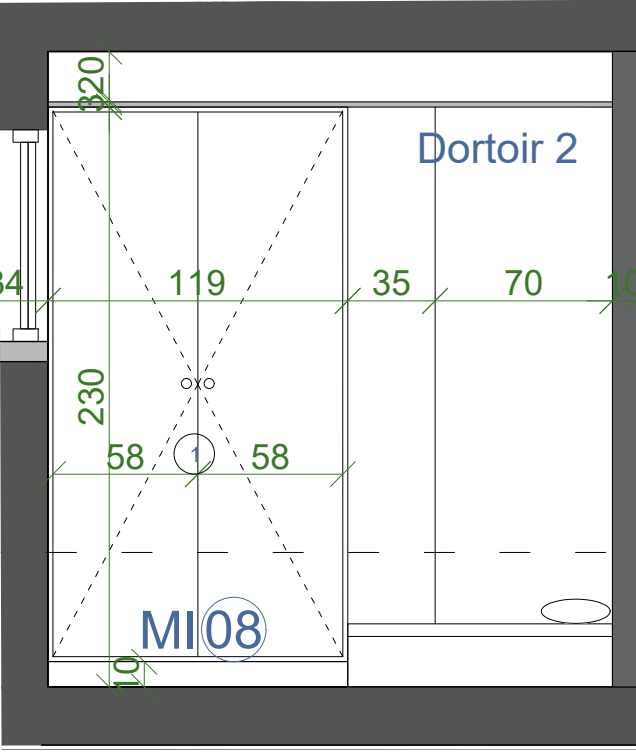


COUPE BB'

MOBILIER - BUANDERIE


Détails de principe

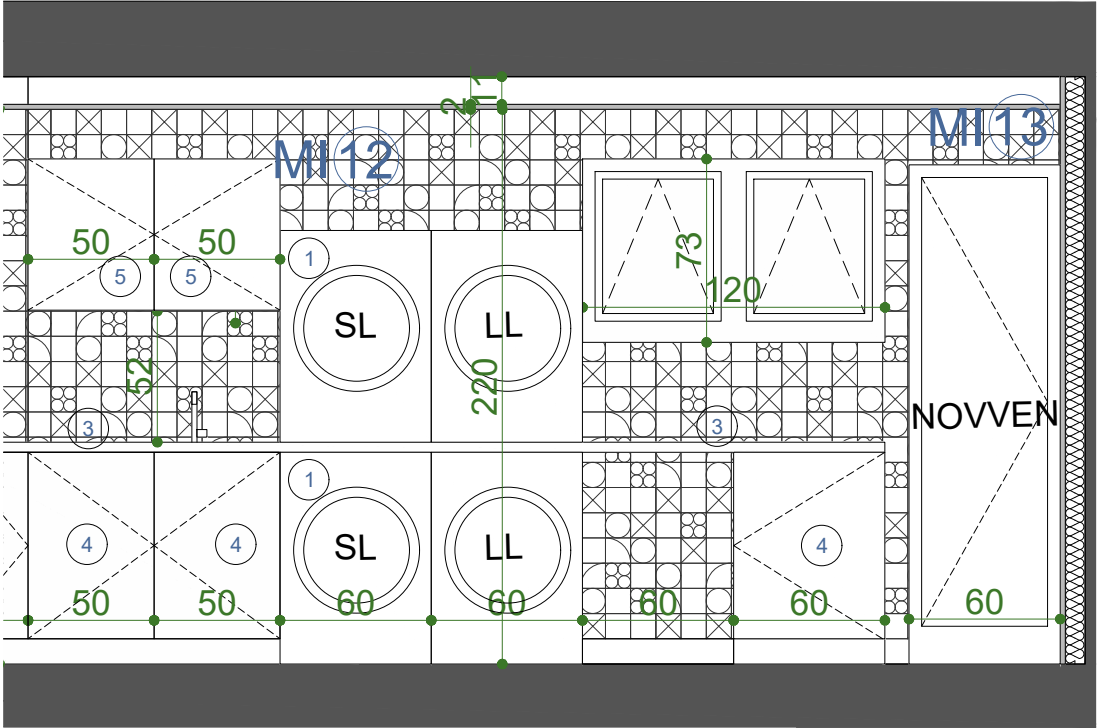


COUPE AA'

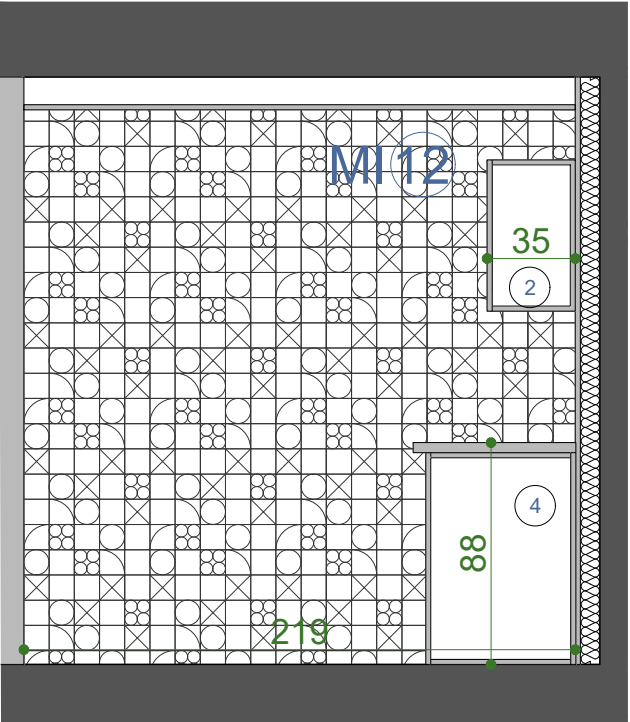

COUPE BB'

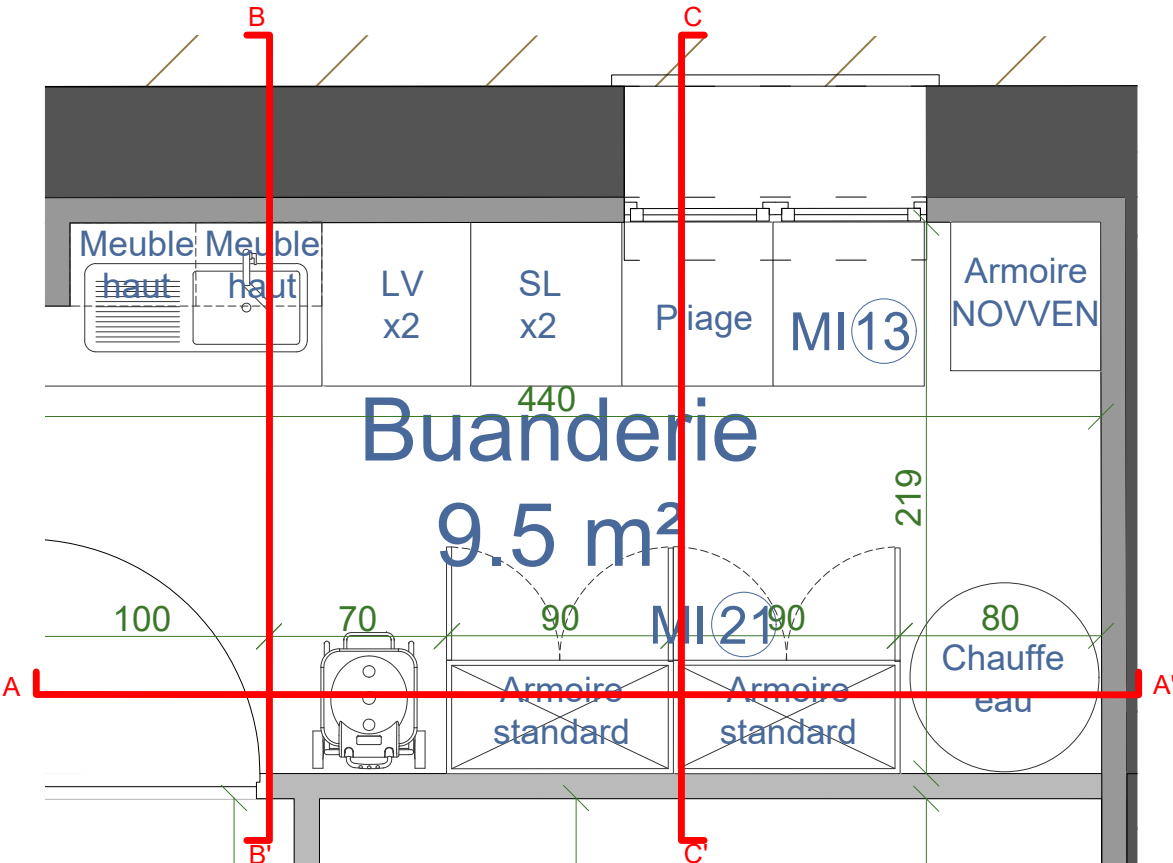

PLAN

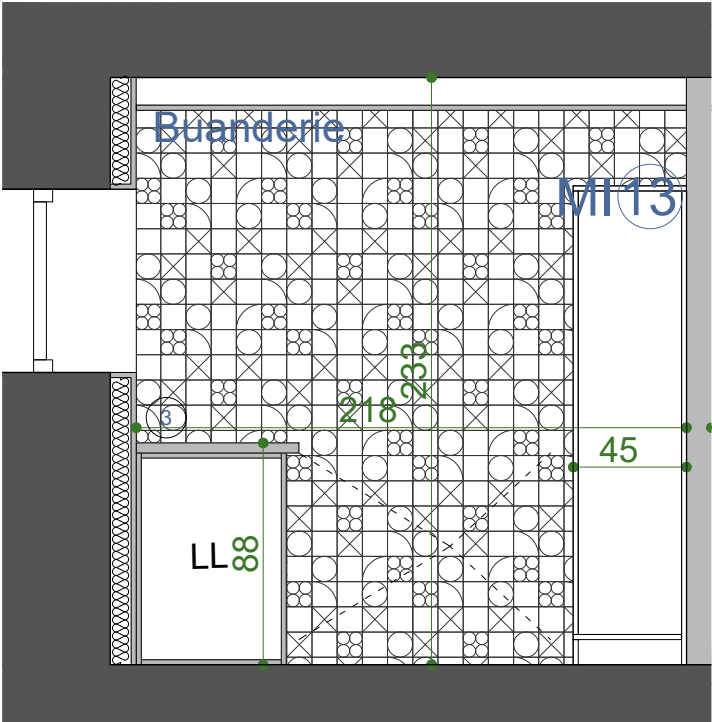


COUPE CC'


CREATION D'UN MULTI-ACCUEIL ET REAMENAGEMENT D'UNE MAISON MEDICALE 30 TER, AVENUE DE BRIMONT 78400 CHATOU			
MOA	LES PETITES CANAILLES 36 Rue Pierret, 92200 Neuilly-sur-Seine		
MOE	NAHK ARCHITECTURE 24 Rue Yves Toudic, 75010 Paris		
NOM DU DOCUMENT			
DETAIL MOBILIER BUANDERIE			
PHASE	PRO.DCE	ECH.	1/30
INDICE	1.1	DATE	09/06/2023
MODIFICATIONS			
INDICE	DATE	OBJET	
1.1	09/06/2023	Diffusion initiale	
1. Emplacement lave-linge et sèche-linge			
2. 2 étagères sur crémaillères			
3. Plan de travail			
4. Placard bas			
5. Placard haut			
6. Bandeau led			
ECHELLE GRAPHIQUE 30 CM 1.5 M			

MOBILIER - SALLE DU PERSONNEL

Détails de principe

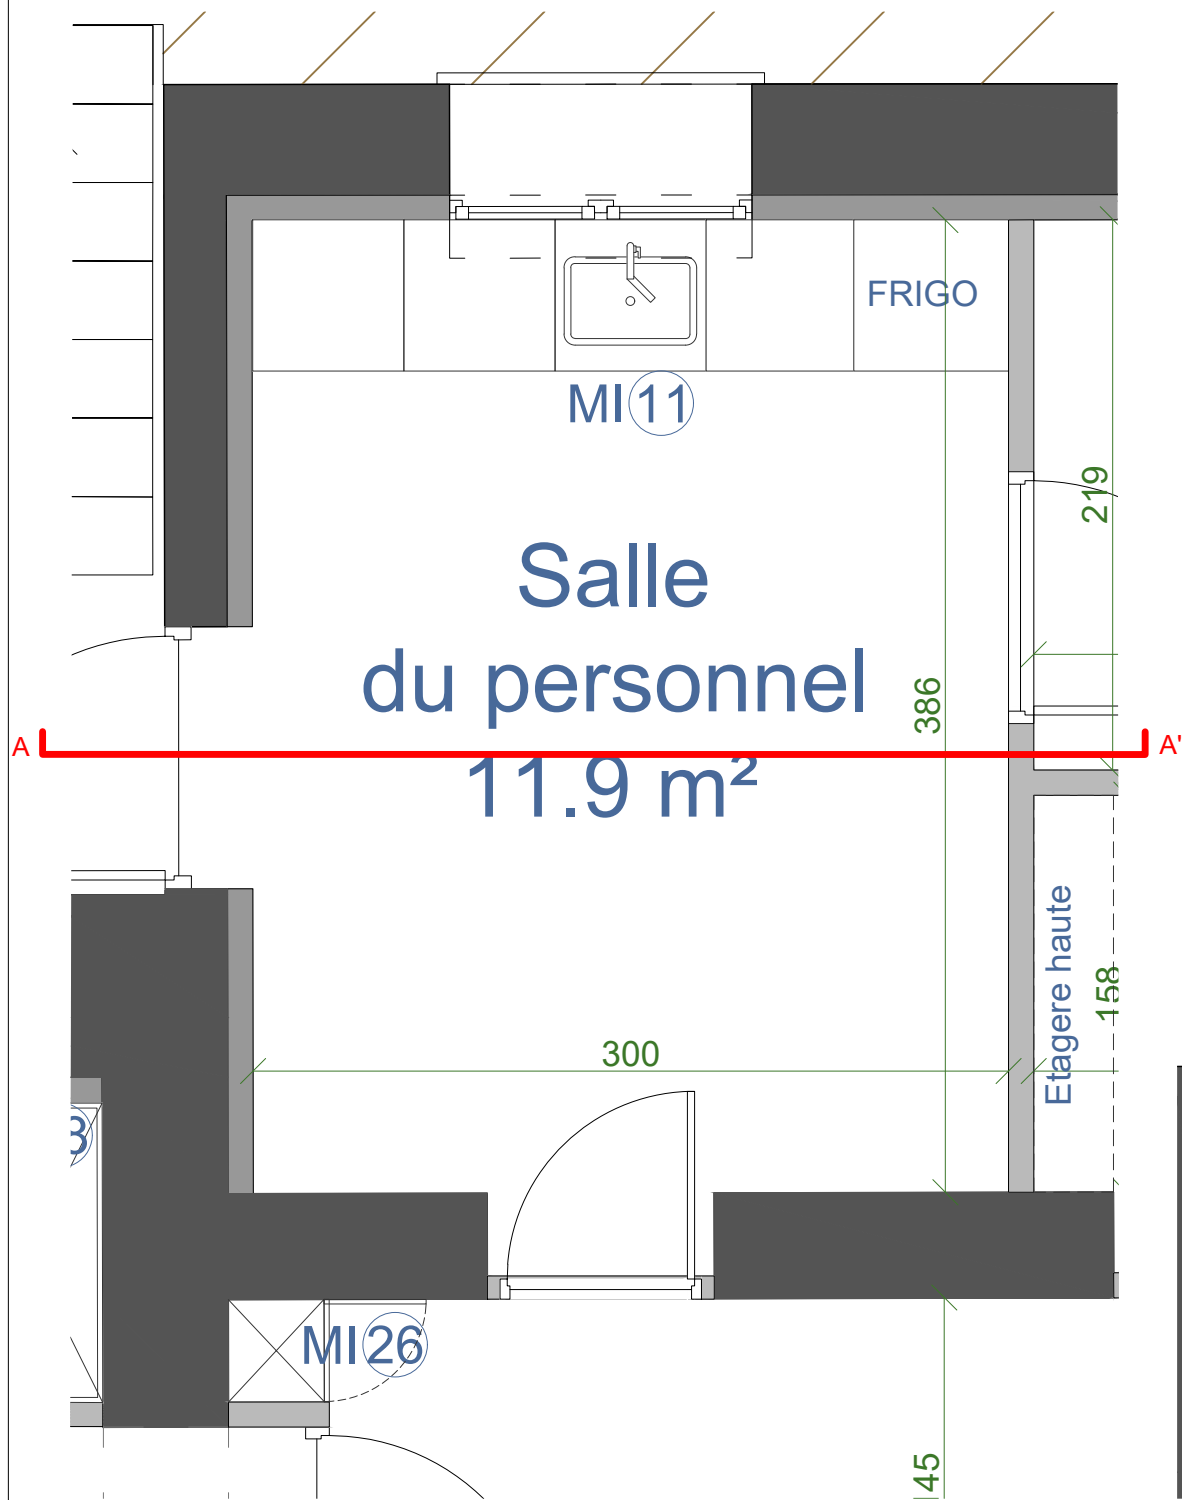

PLAN

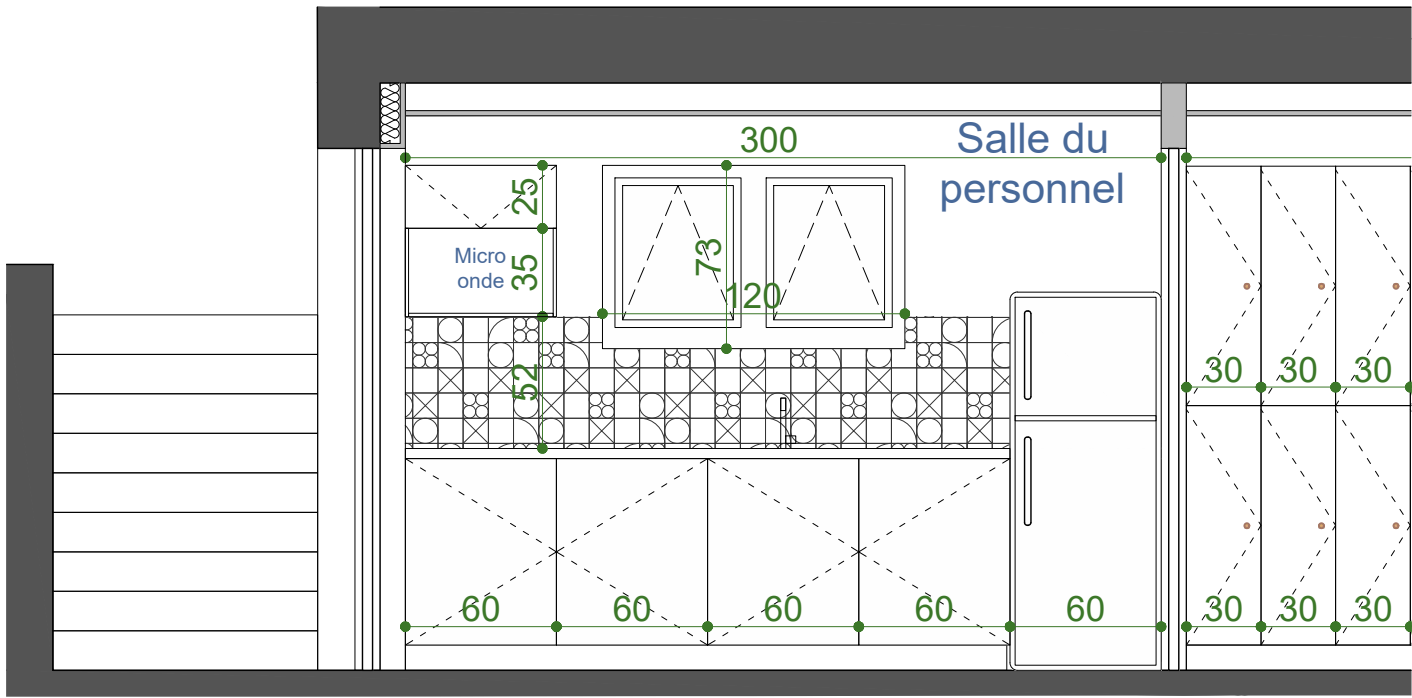

COUPE AA'

CREATION D'UN MULTI-ACCUEIL ET REAMENAGEMENT D'UNE MAISON MEDICALE			
30 TER, AVENUE DE BRIMONT 78400 CHATOU			
MOA	LES PETITES CANAILLES 36 Rue Pierret, 92200 Neuilly-sur-Seine		
MOE	NAHK ARCHITECTURE 24 Rue Yves Toudic, 75010 Paris		

NOM DU DOCUMENT			
-----------------	--	--	--

DETAIL MOBILIER SALLE DU PERSONNEL			
------------------------------------	--	--	--

PHASE	PRO.DCE	ECH.	1/30
INDICE	1.1	DATE	09/06/2023

MODIFICATIONS			
INDICE	DATE	OBJET	

1.1	09/06/2023	Diffusion initiale	
-----	------------	--------------------	--