
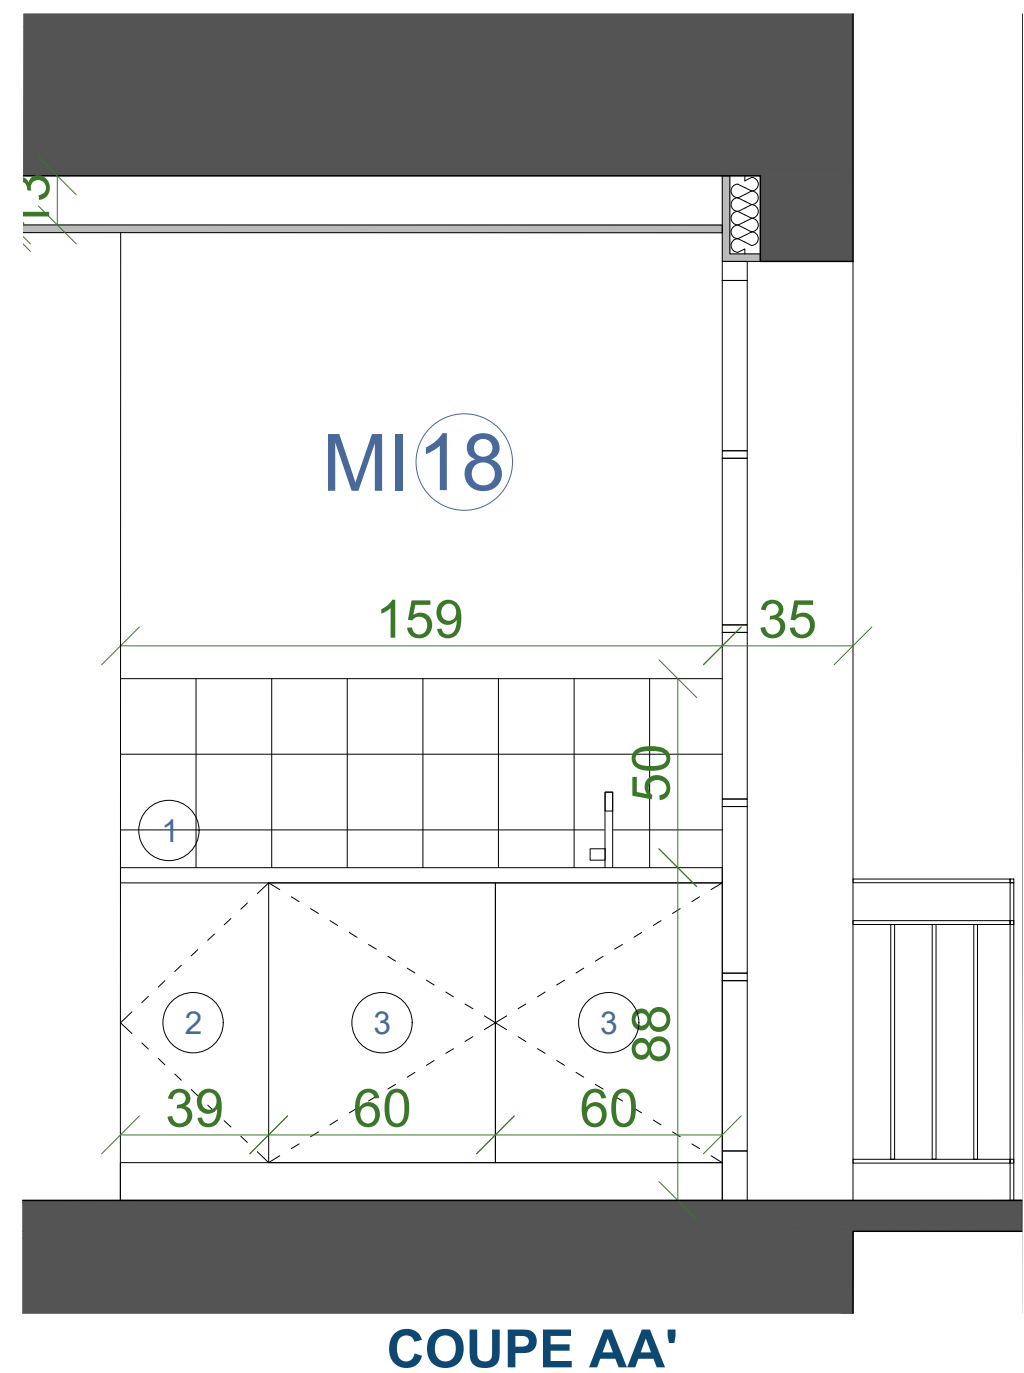


MOBILIER - SALLE 3

Détails de principe

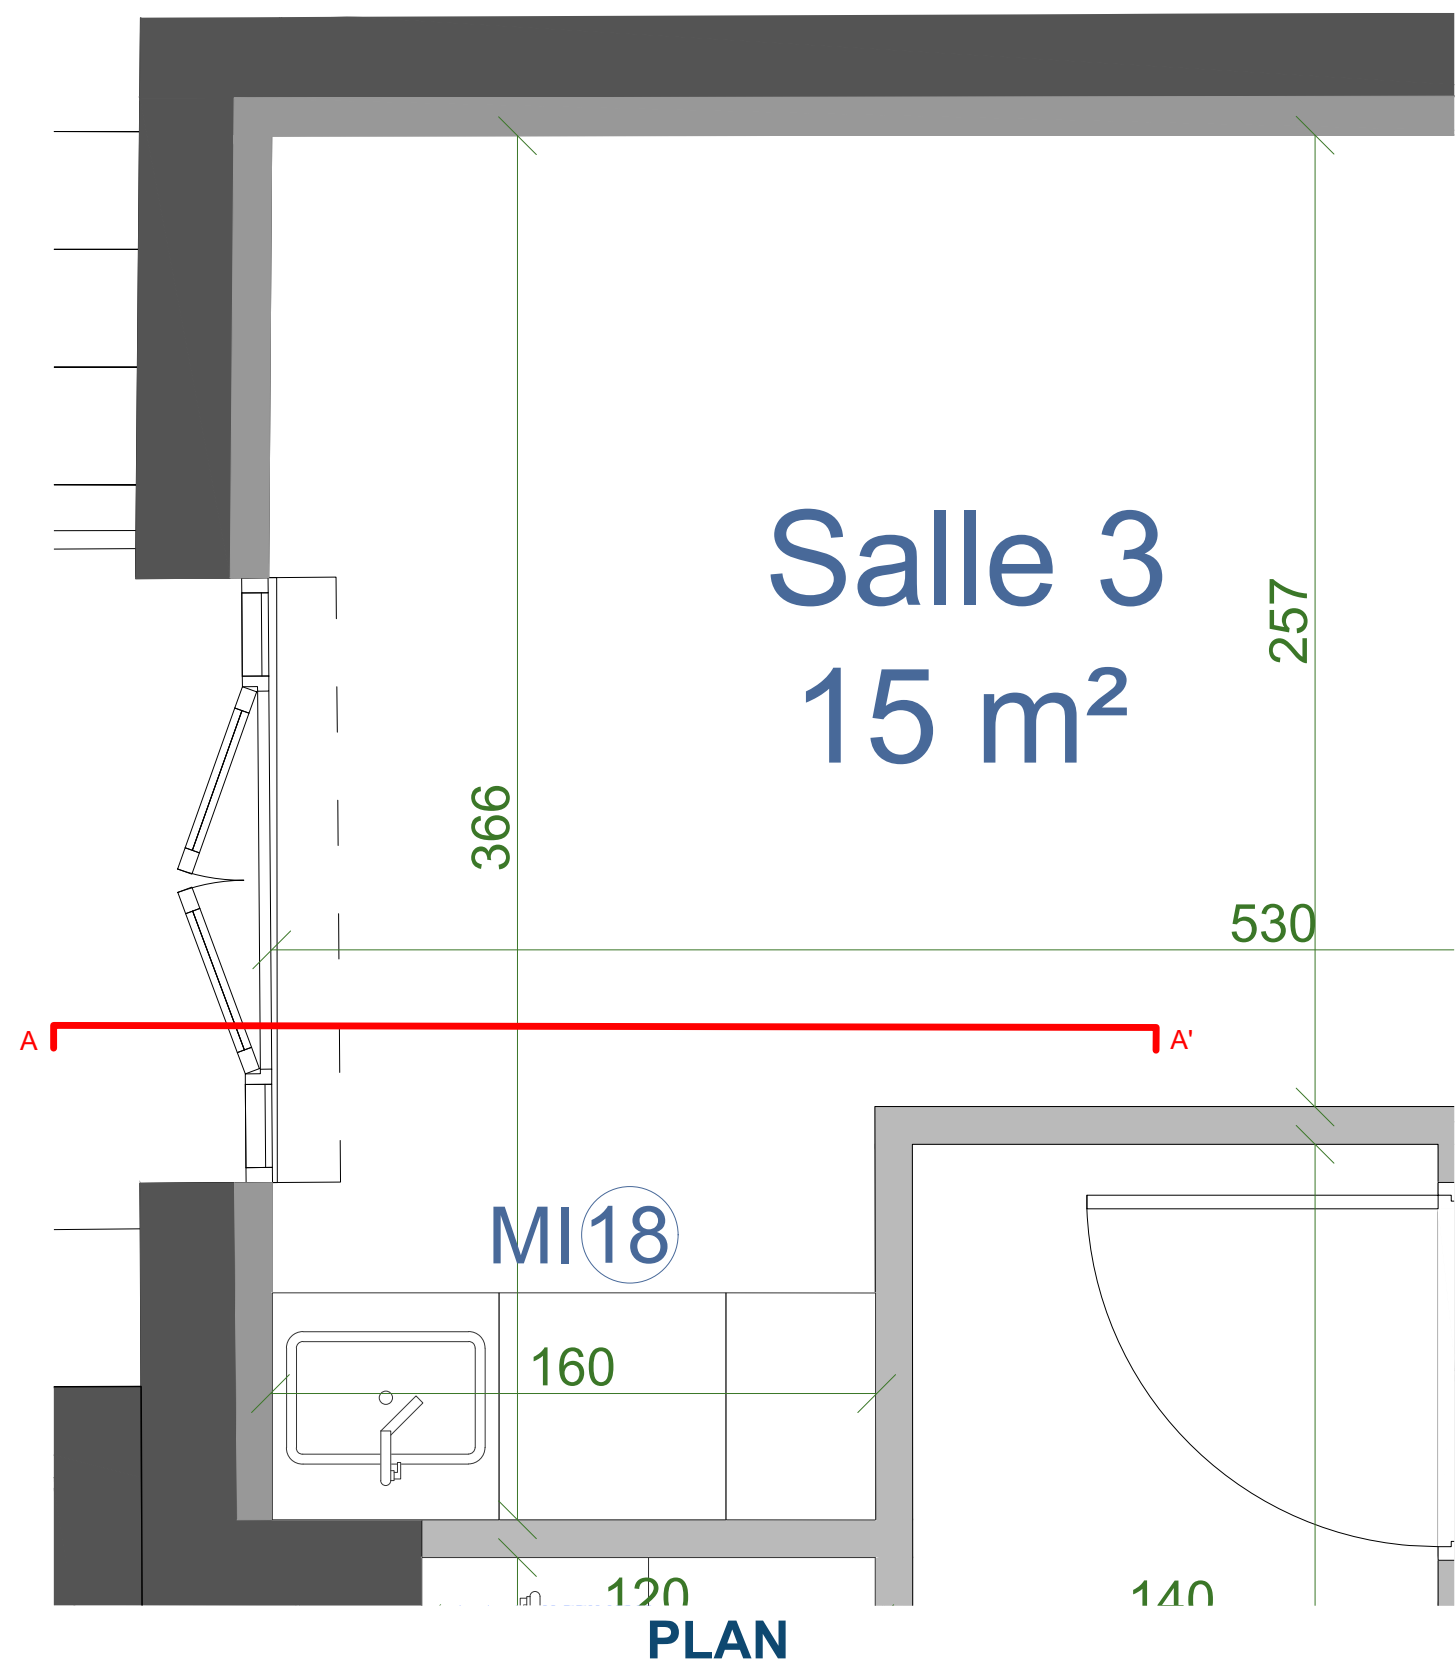

CREATION D'UN MULTI-ACCUEIL ET
D'UNE MAISON MEDICALE
30 ter Avenue de Brimont
78400 CHATOU

MOA SARL LPC YVELINES
15 Rue de l'Orient, 78000 Versailles

MOE NAHK ARCHITECTURE
24 Rue Yves Toudic, 75010 Paris

NOM DU DOCUMENT

DETAIL MOBILIER
SALLE 3

PHASE	PRO.DCE	ECH.	1/20
-------	---------	------	------

INDICE	1.1	DATE	07/06/2023
--------	-----	------	------------

MODIFICATIONS
INDICE DATE OBJET


1.0	07/06/2023	Diffusion initiale
-----	------------	--------------------

1. Plan de travail
2. Placard bas
3. Placard bas IKEA METOD
ref. 494.698.78

ECHELLE GRAPHIQUE
20 CM 1 M

MOBILIER - CUISINE

Détails de principe

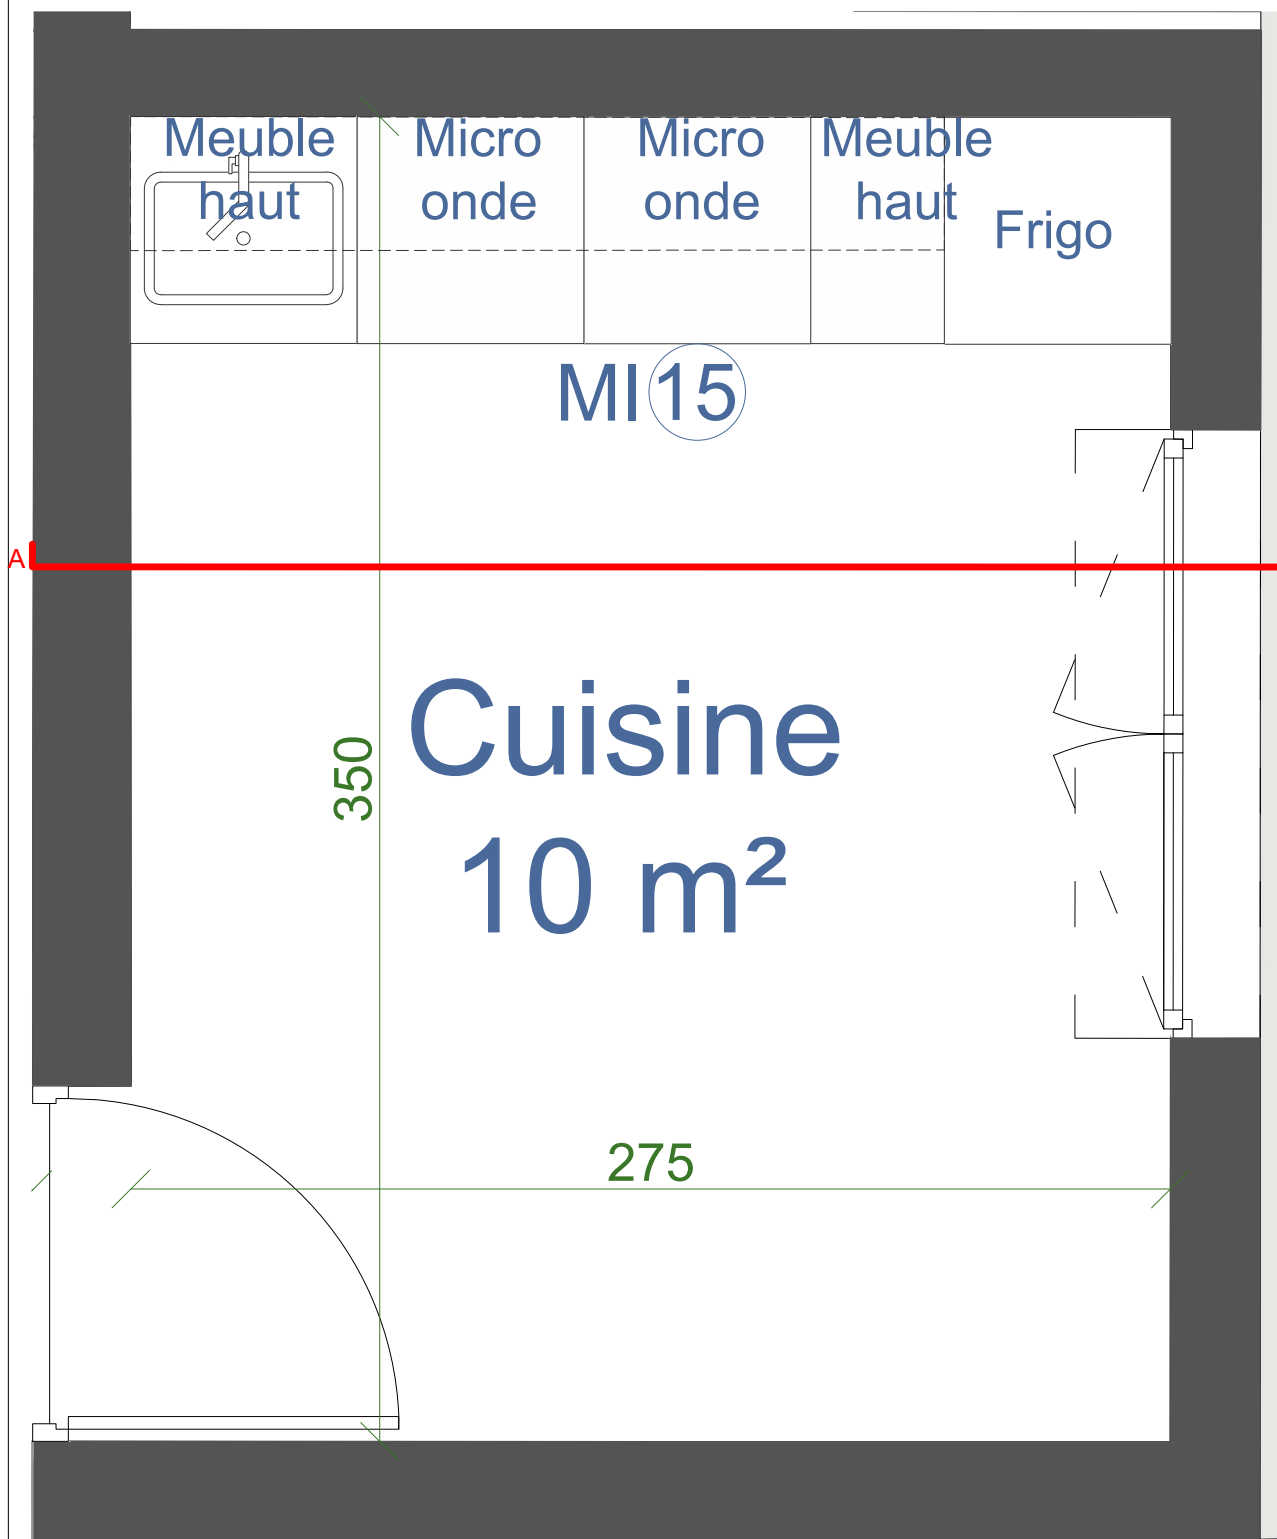

PLAN




COUPE AA'


CREATION D'UN MULTI-ACCUEIL ET D'UNE MAISON MEDICALE 30 ter Avenue de Brimont 78400 CHATOU			
MOA	SARL LPC YVELINES 15 Rue de l'Orient, 78000 Versailles		
MOE	NAHK ARCHITECTURE 24 Rue Yves Toudic, 75010 Paris		
NOM DU DOCUMENT			
DETAIL MOBILIER CUISINE			
PHASE	PRO.DCE	ECH.	1/20
INDICE	1.1	DATE	07/06/2023
MODIFICATIONS			
INDICE DATE OBJET			
1.0	07/06/2023	Diffusion initiale	
1. Placard haut IKEA ENHET ref. 093.210.11 2. Placard haut 3. Placard bas IKEA METHOD ref. 494.698.78 4. Placard bas 5. Emplacement frigo 150 cm 6. Bandeau LED 7. Plan de travail			
ECHELLE GRAPHIQUE 20 CM 1 M			

MOBILIER - SALLE 5

Détails de principe

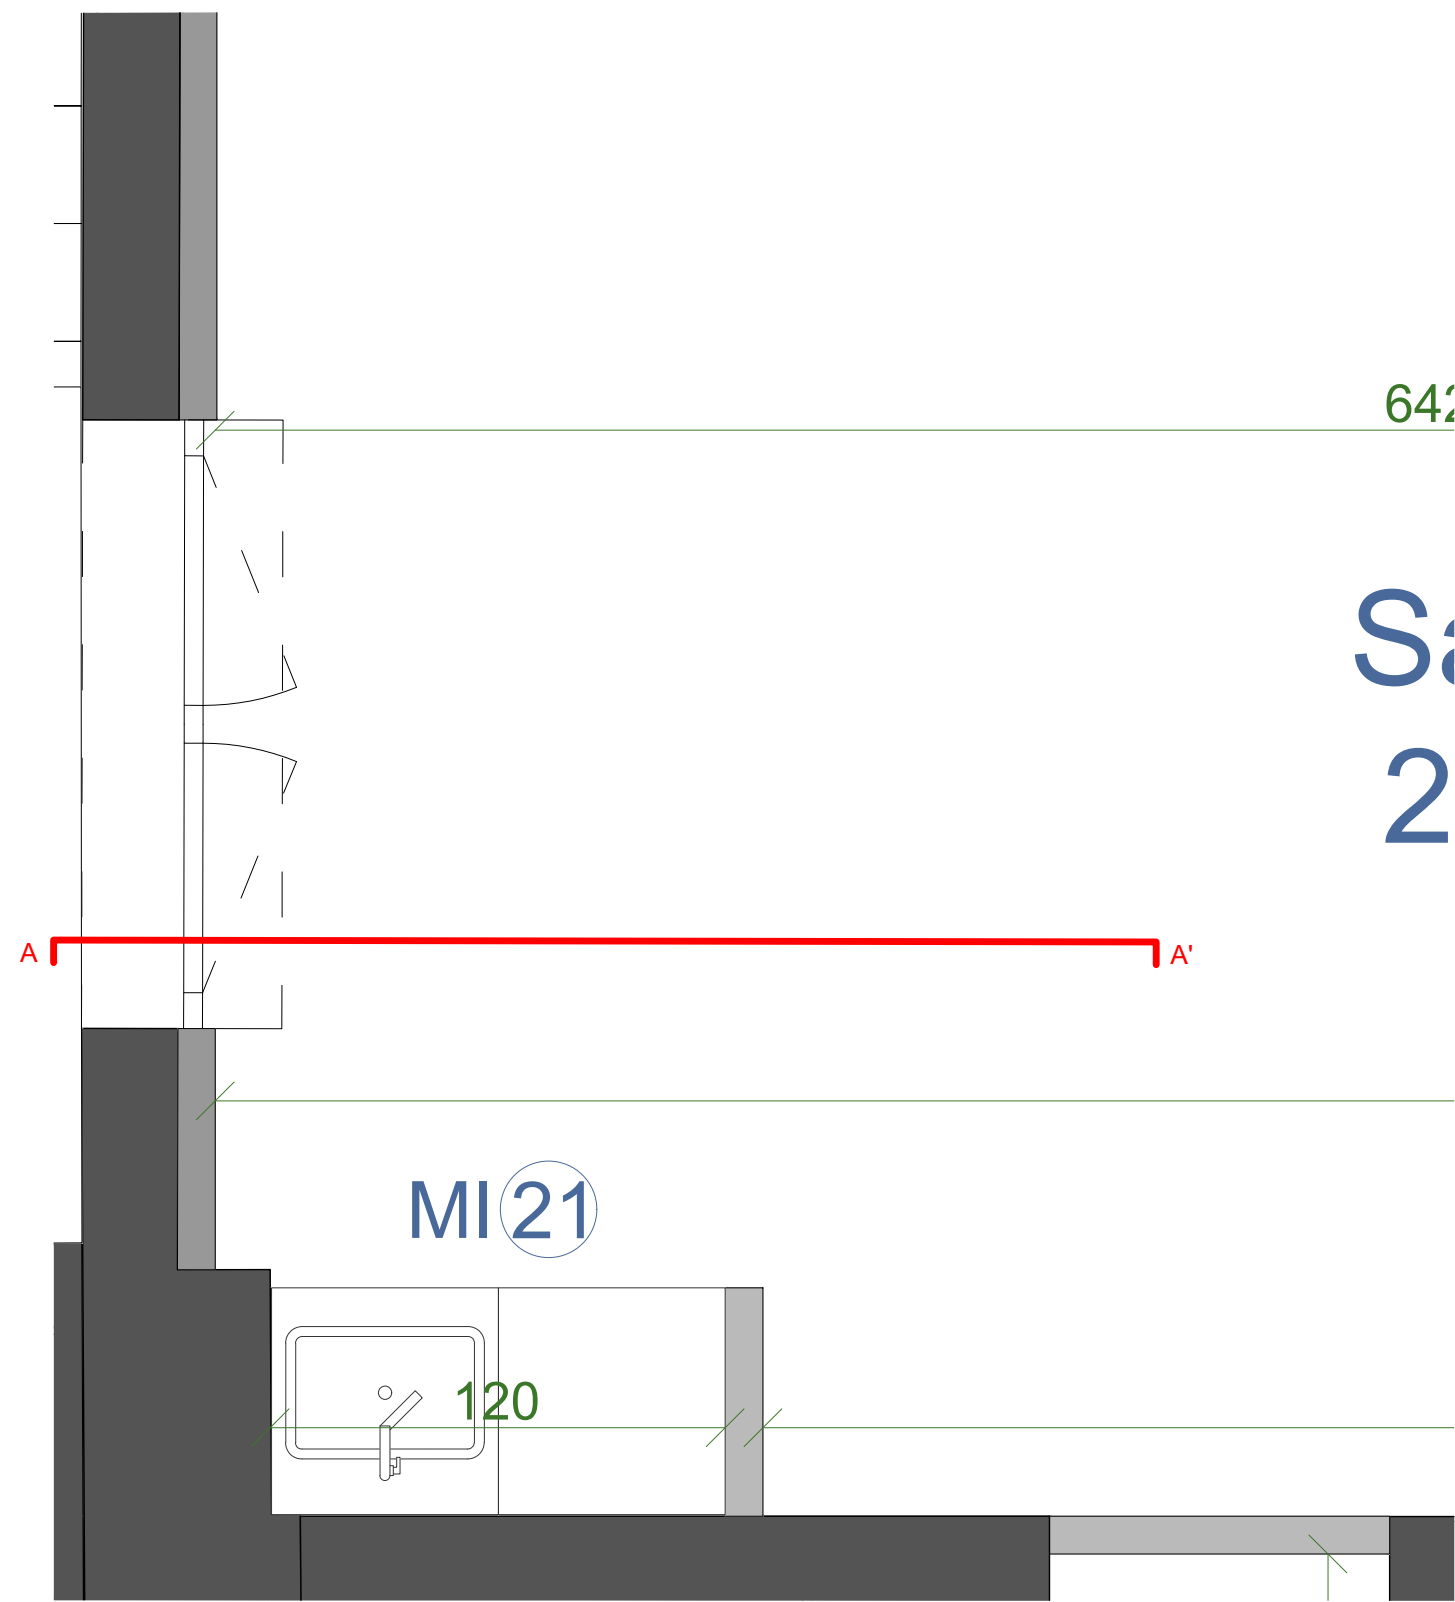

PLAN

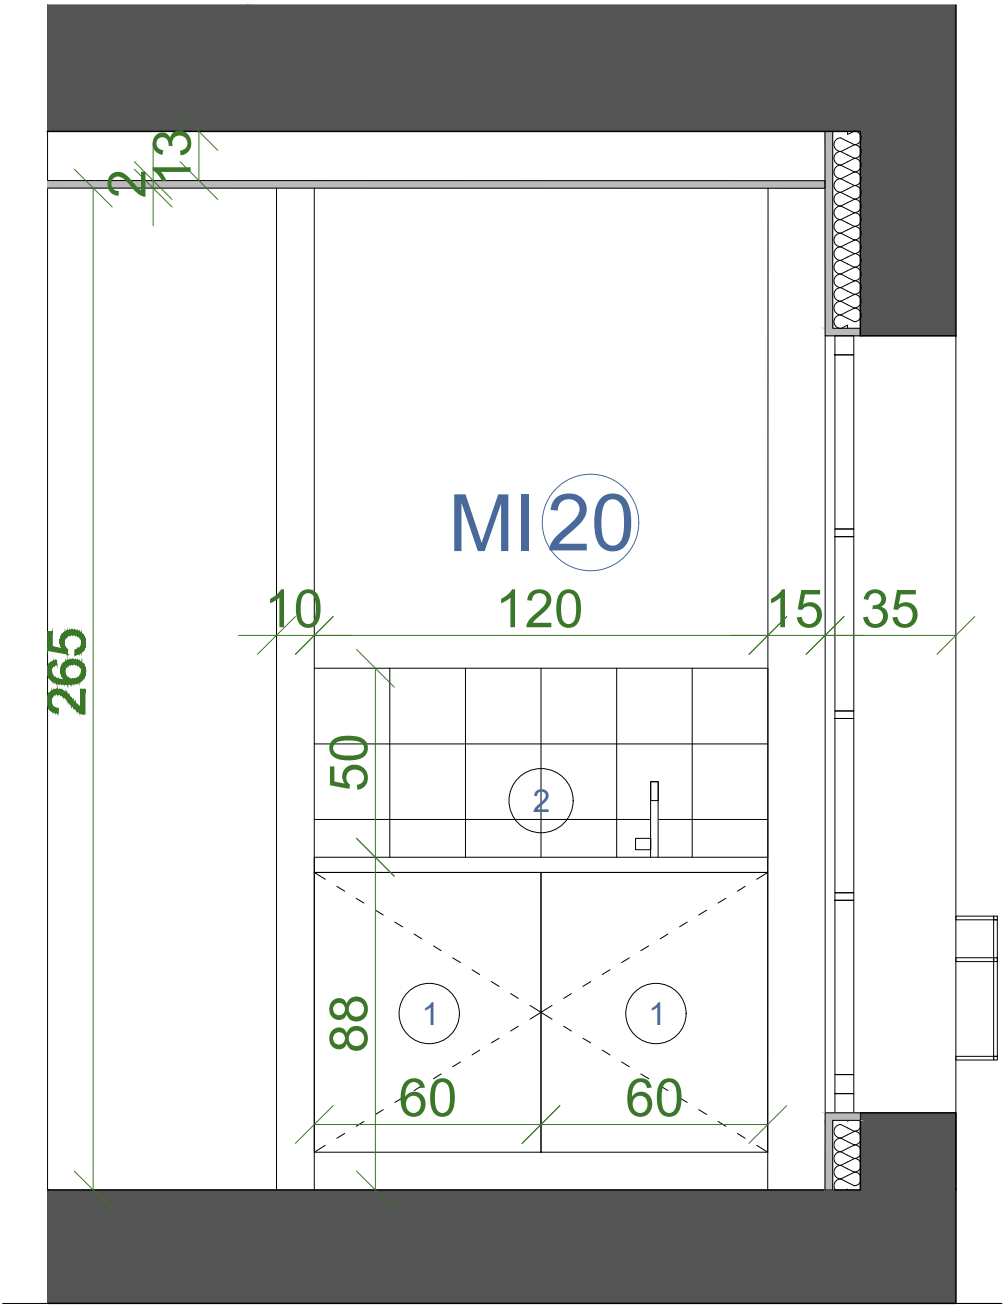

COUPE AA'

CREATION D'UN MULTI-ACCUEIL ET
D'UNE MAISON MEDICALE
30 ter Avenue de Brimont
78400 CHATOU

MOA SARL LPC YVELINES
15 Rue de l'Orient, 78000 Versailles

MOE NAHK ARCHITECTURE
24 Rue Yves Toudic, 75010 Paris

NOM DU DOCUMENT

DETAIL MOBILIER
SALLE 5

PHASE	PRO.DCE	ECH.	1/20
-------	---------	------	------

INDICE	1.1	DATE	07/06/2023
--------	-----	------	------------

MODIFICATIONS
INDICE DATE OBJET

1.0	07/06/2023	Diffusion initiale
-----	------------	--------------------

- Placard bas IKEA METOD
ref. 494.698.78
- Plan de travail

ECHELLE GRAPHIQUE
20 CM 1 M