

DOS-
SIER
DCE

AMENAGEMENTS EXTERIEURS


78 400 CHATOU

MOA : SARL LPC YVELINES
15 Rue de l'Orient 78000 VERSAILLES



Les Petites Canailles

MAITRE D'OEUVRE  NAHK ARCHITECTURE 24 rue Yves Toudic - 75010 PARIS	PHASE DCE	VERSION 01	DATE 07/06/2023	OPÉRATION CREATION D'UN MULTI ACCUEIL DE 30 BERCEAUX ET REAMENAGEMENT D'UNE MAISON MEDICALE 30 ter Avenue de Brimont 78400 CHATOU	MAITRE D'OUVRAGE SARL LPC YVELINES 15 Rue de l'Orient78000 VERSAILLES	N° DOC --	NOM DU DOCUMENT	ÉCHELLE --
--	---------------------------------	----------------------------------	---------------------------------------	---	--	---------------------------------	--	----------------------------------

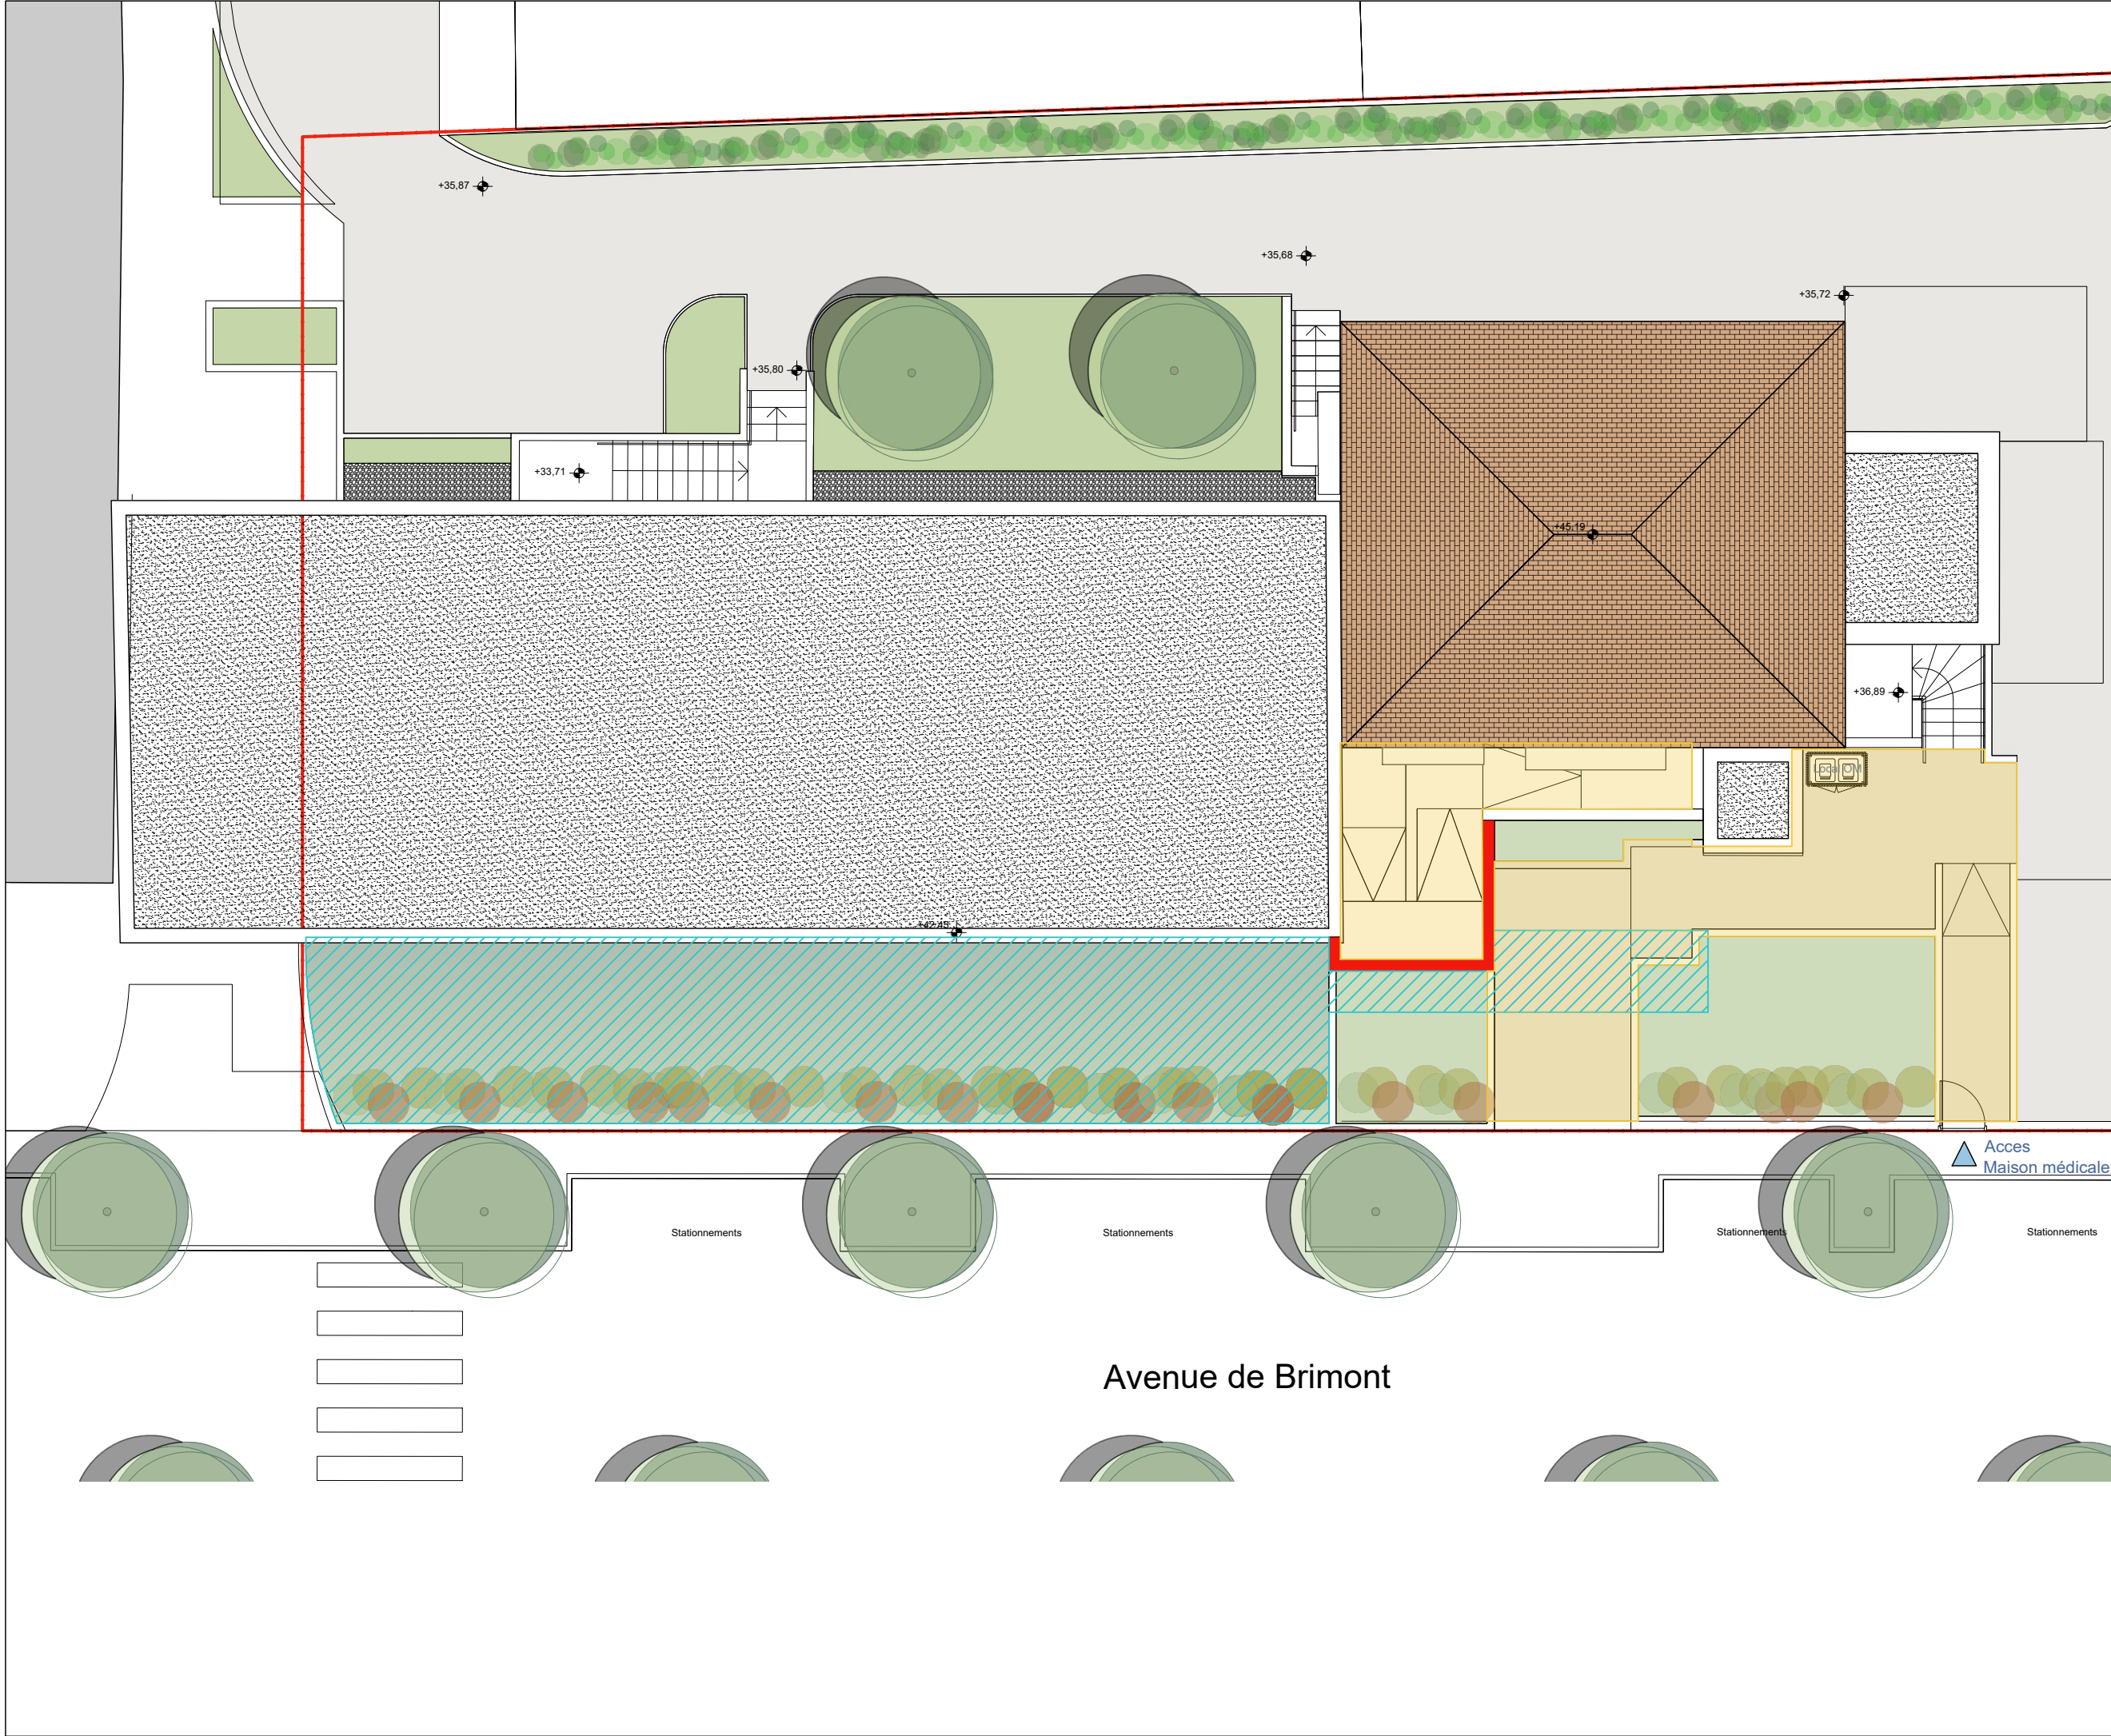

CREATION D'UN MULTI-ACCUEIL
49 RUE ARISTIDE BRIAND
94430 CHENNEVIERES-SUR-MARNE

MOA

SARL LPC YVELINES
15 Rue de l'Orient78000 VERSAILLES

MOE

NAHK ARCHITECTURE
24 Rue Yves Toudic, 75010 Paris

NOM DU DOCUMENT

PLAN DE LOCALISATION
DES DEMOLITIONS

PHASE	PRO.DCE	ECH.	1/100
INDICE	1.1	DATE	07/06/2023

MODIFICATIONS


INDICE	DATE	OBJET
1.1	07/06/2023	Diffusion initiale

DEMOLITION

• MUR DEMOLIE

• DALLE DEMOLIE

• SOL EXCAVE

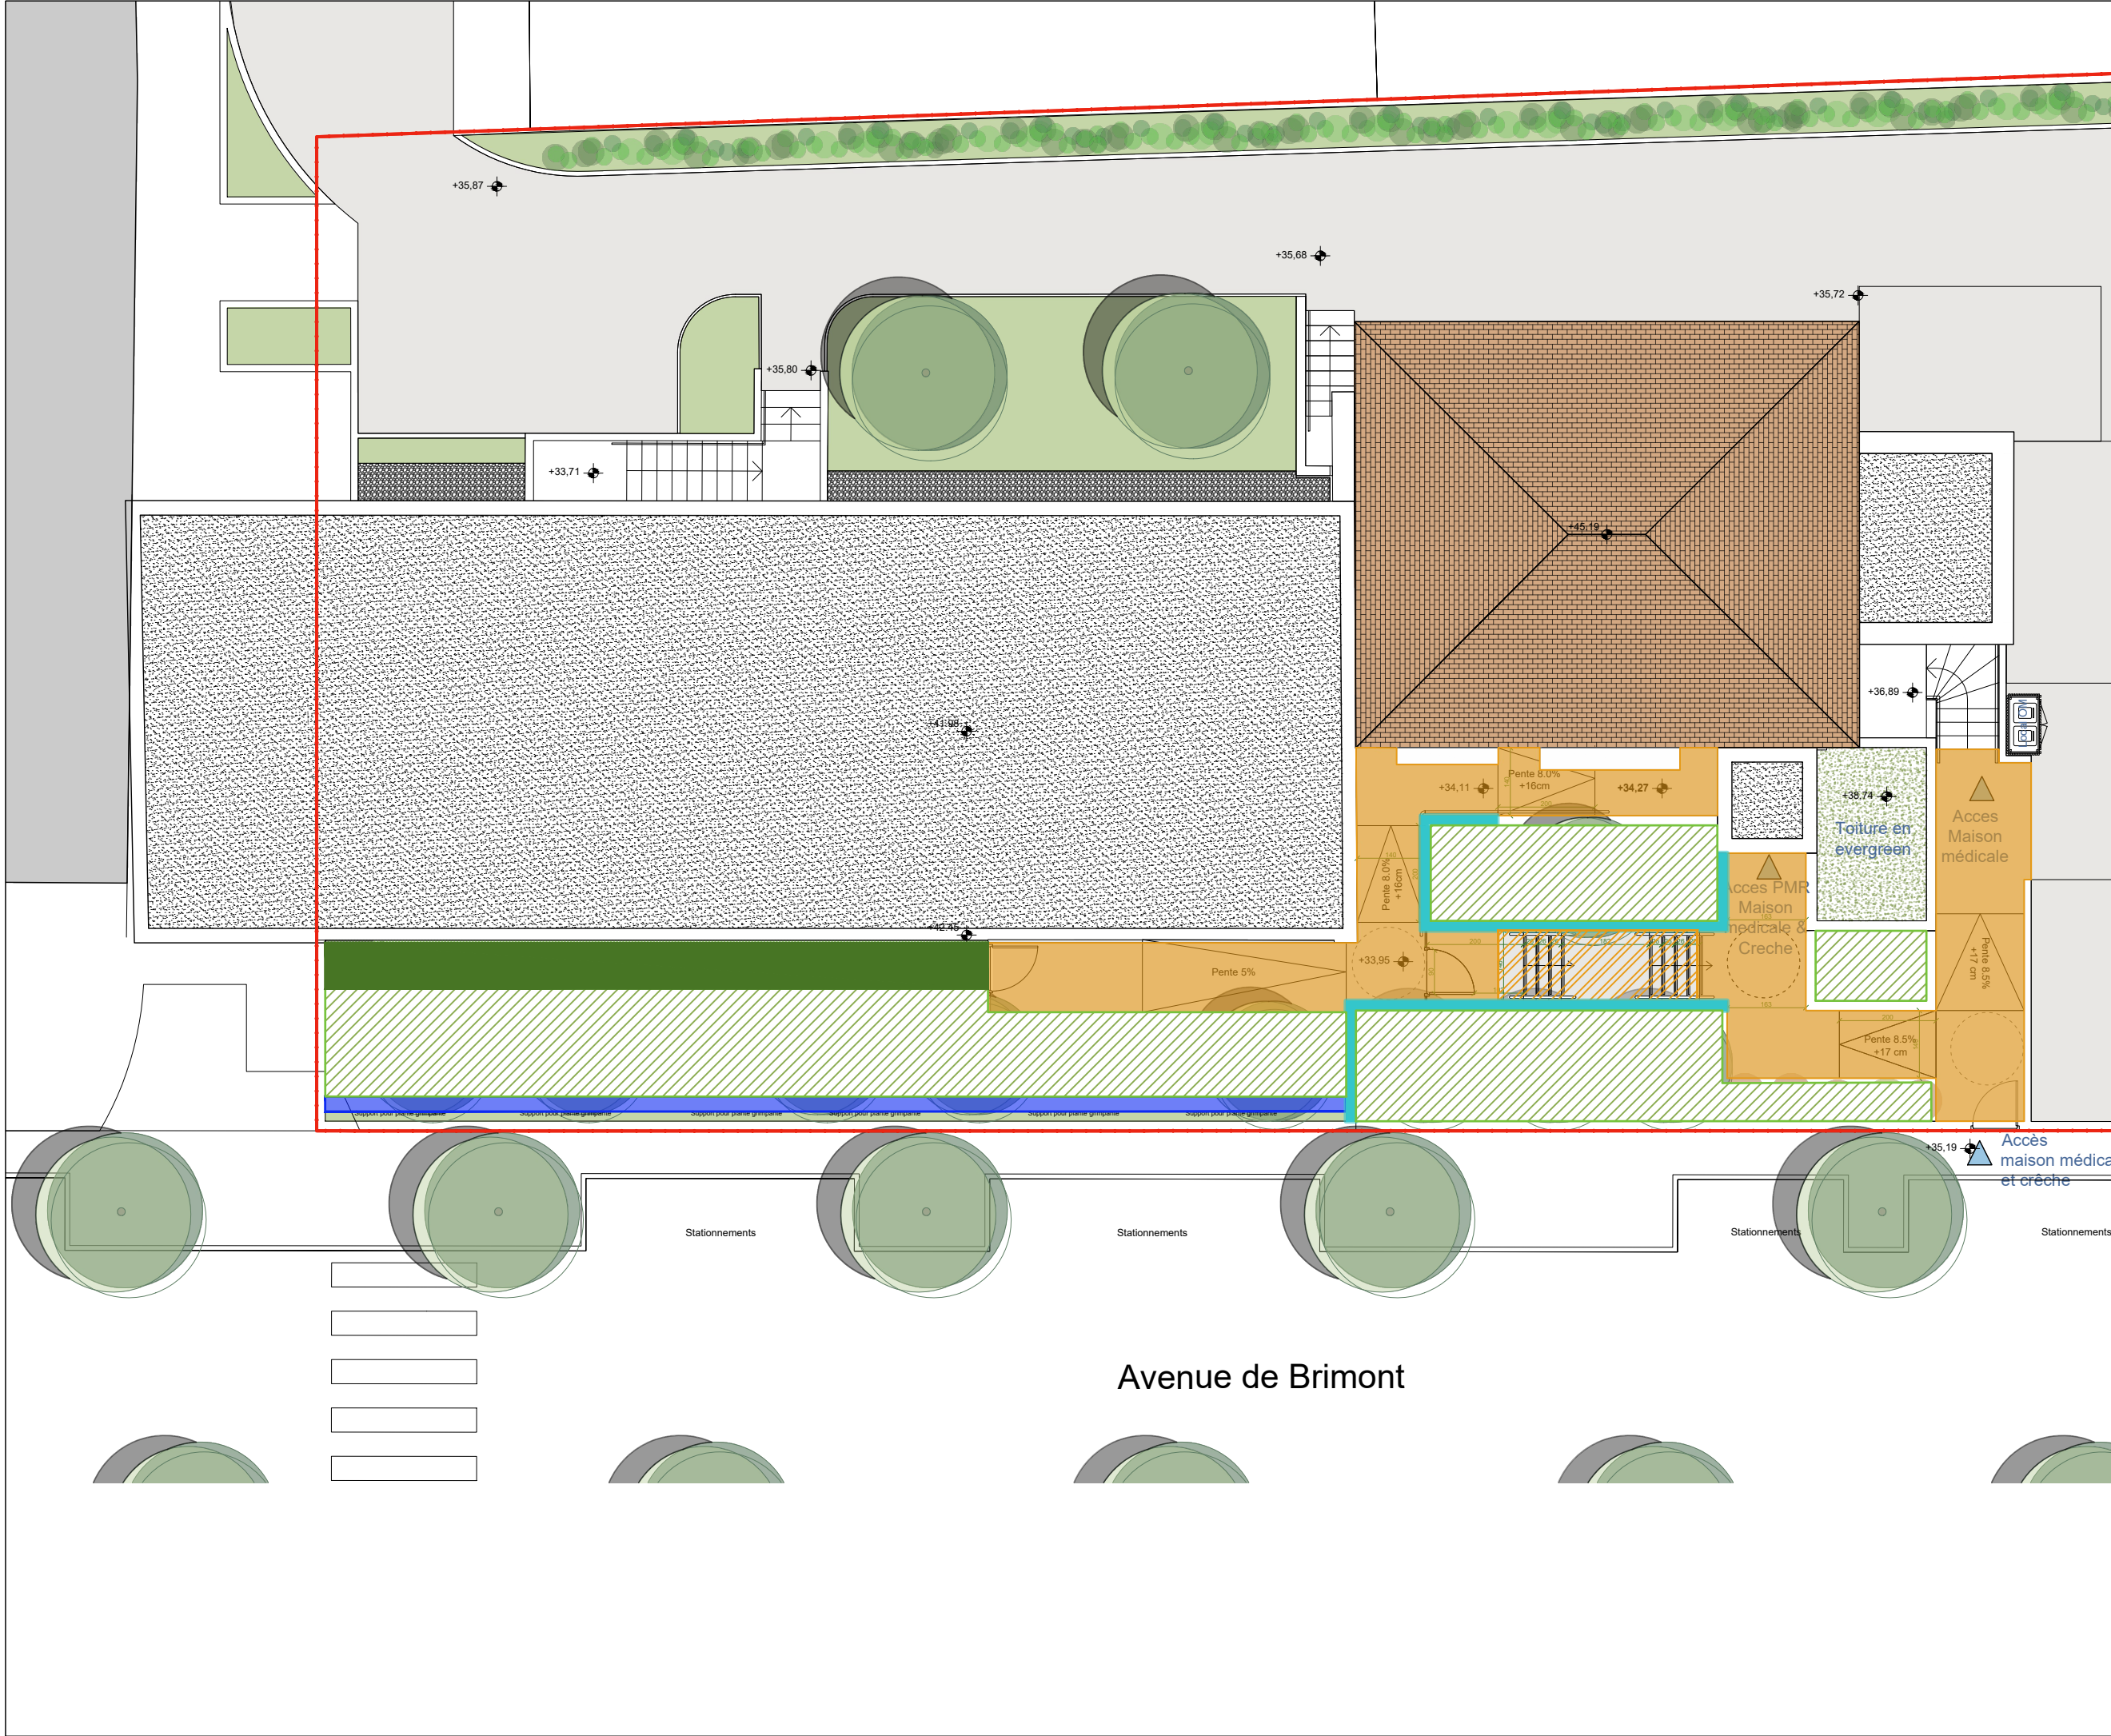

CREATION D'UN MULTI-ACCUEIL
49 RUE ARISTIDE BRIAND
94430 CHENNEVIERES-SUR-MARNE

MOA

SARL LPC YVELINES
15 Rue de l'Orient78000 VERSAILLES

MOE

NAHK ARCHITECTURE
24 Rue Yves Toudic, 75010 Paris

NOM DU DOCUMENT

PLAN DE LOCALISATION
DES DEMOLITIONS

PHASE

PRO.DCE

ECH.

1/100

INDICE

1.1

DATE

07/06/2023

MODIFICATIONS

INDICE DATE OBJET

1.1 07/06/2023 Diffusion initiale

DEMOLITION

• CREATION DE RAMPE
ET DE DALLE


• CREATION D'UN
ESCALIER

• CREATION DE MUR
MACONNE

• CREATION DE MUR DE
SOUTENEMENT

• HERBE SYNTHETIQUE

• CREATION D'ESPACE
VERT

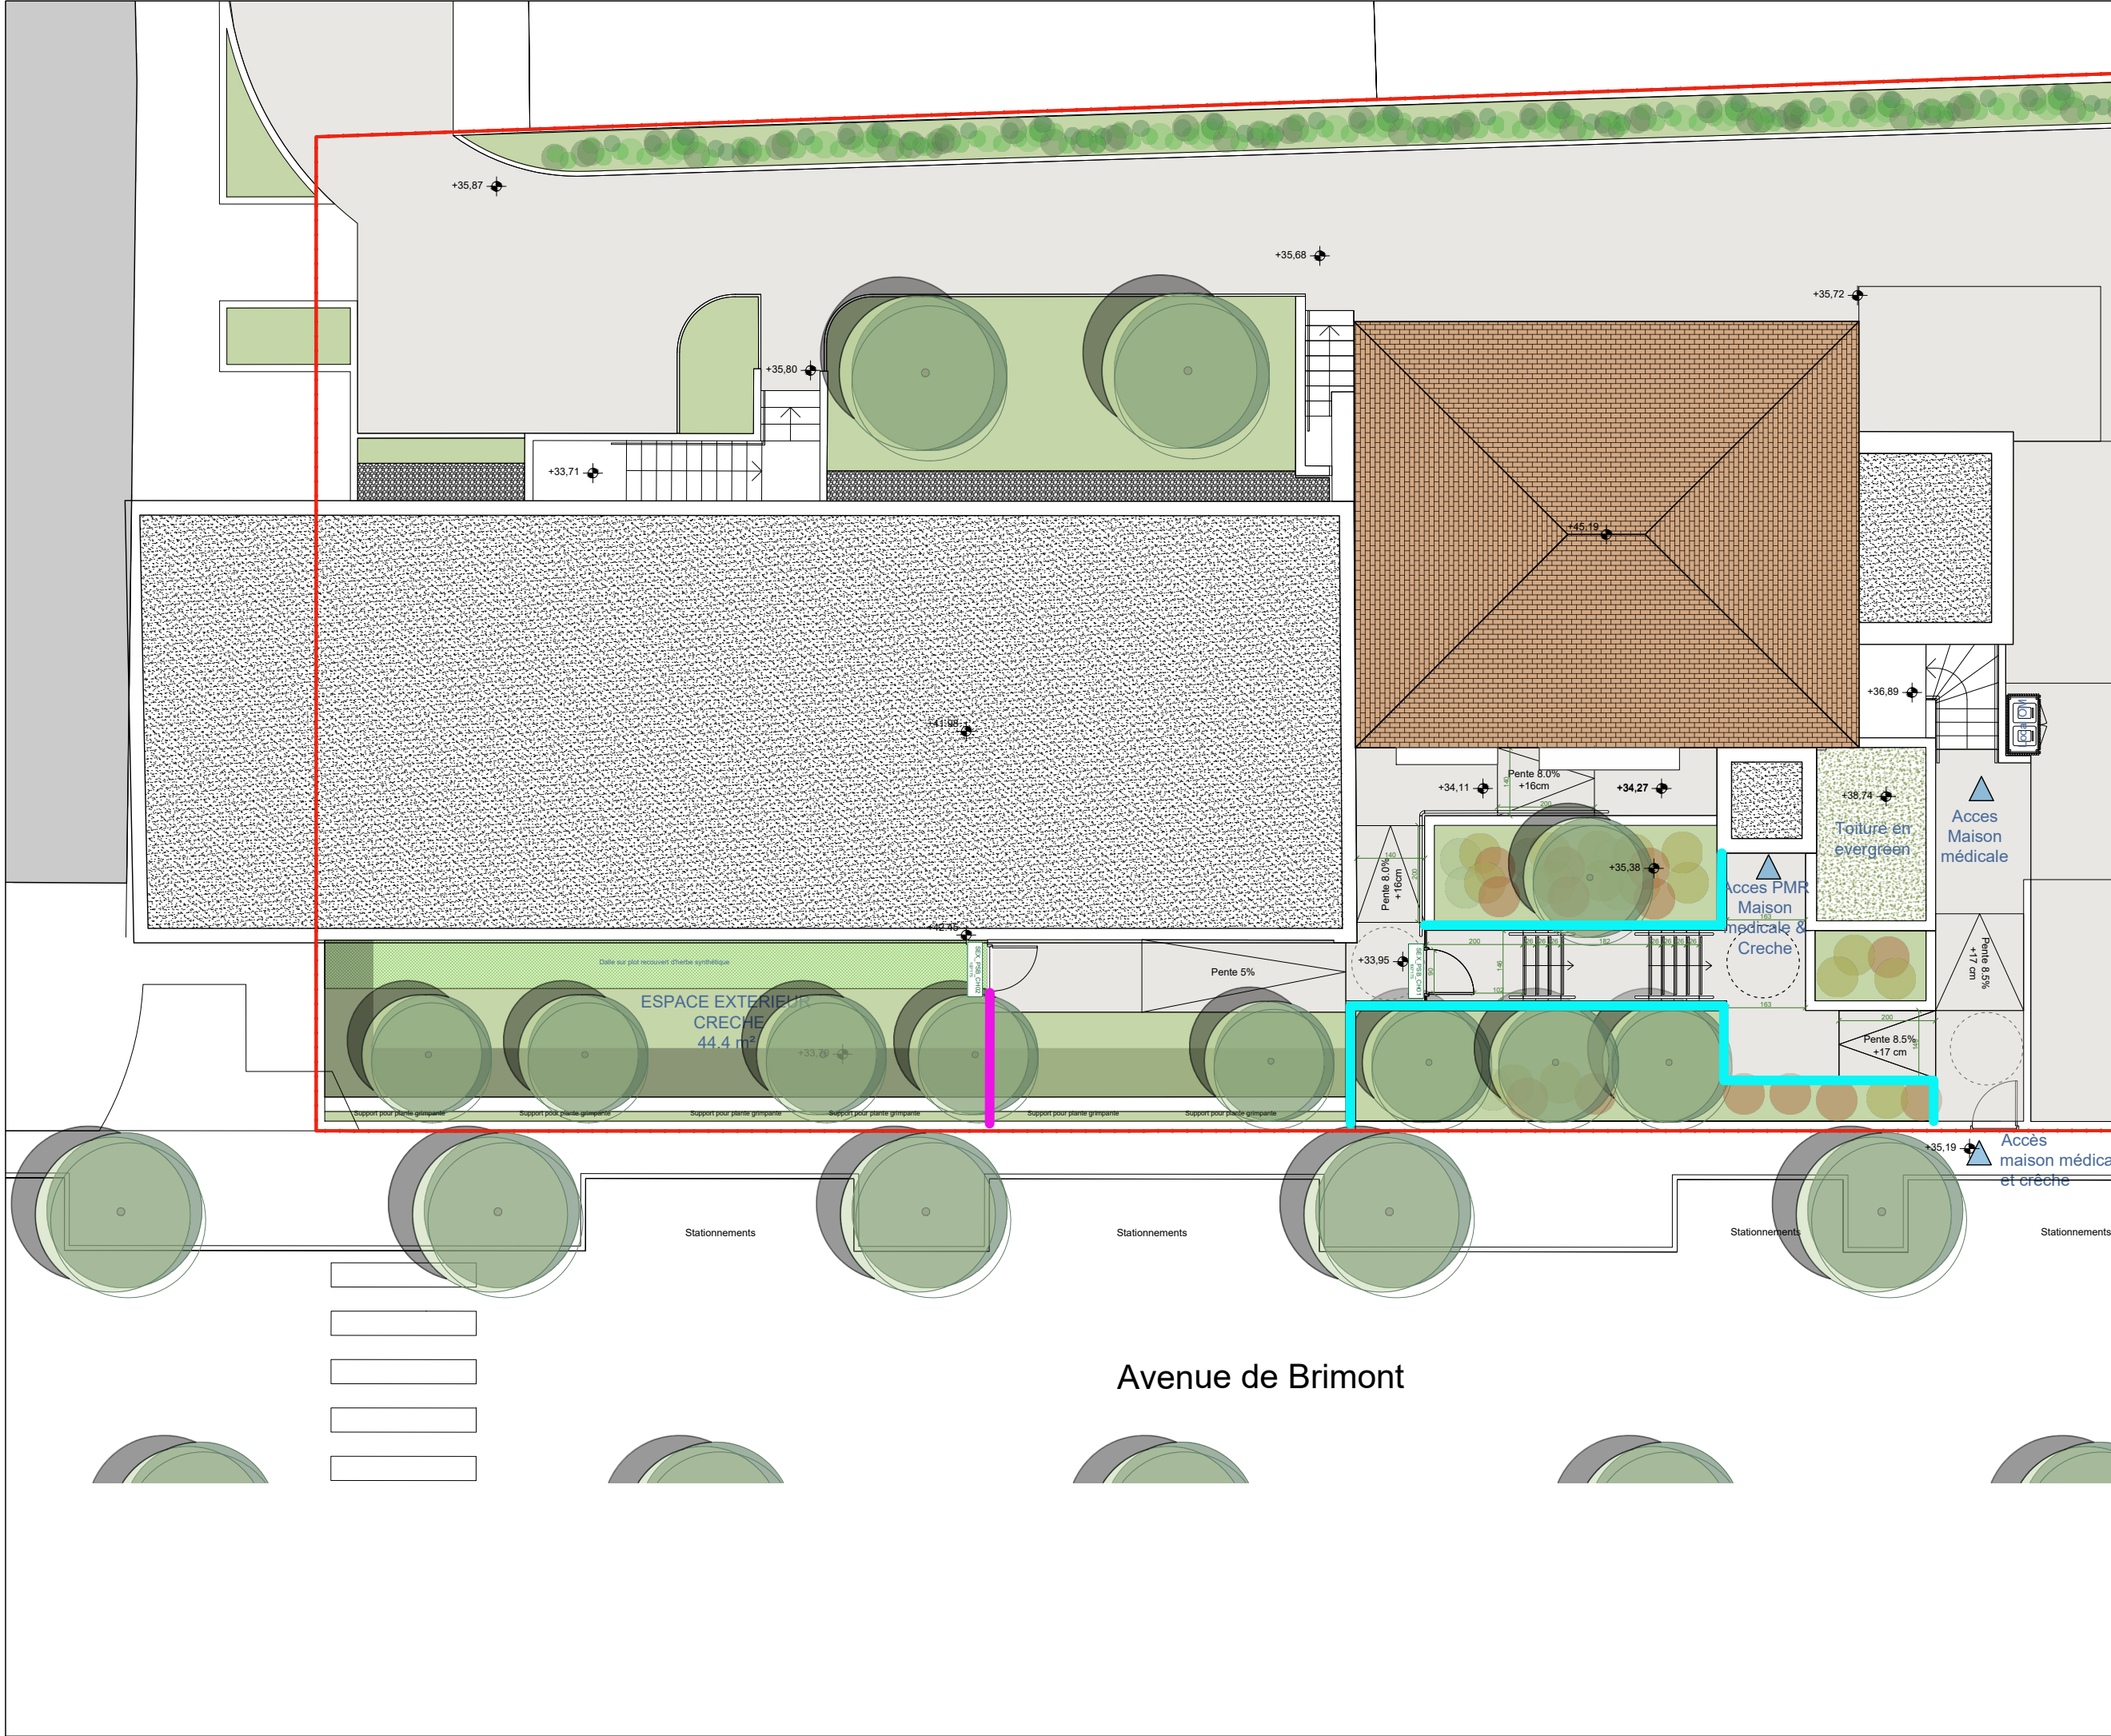

CREATION D'UN MULTI-ACCUEIL
49 RUE ARISTIDE BRIAND
94430 CHENNEVIERES-SUR-MARNE

MOA

SARL LPC YVELINES
15 Rue de l'Orient78000 VERSAILLES

MOE

NAHK ARCHITECTURE
24 Rue Yves Toudic, 75010 Paris

NOM DU DOCUMENT

PLAN DE LOCALISATION
DES SERRURERIES

PHASE

PRO.DCE

ECH.

1/100

INDICE

1.1

DATE

07/06/2023

MODIFICATIONS

INDICE

DATE

OBJET

1.1

07/06/2023

Diffusion initiale

SERRURERIE

• CLOTURE NOMACLO
OBAMBOO 1M

• CLOTURE NOMACLO
OBAMBOO 2M

SEX_PSB. Simple battant

Dimensions : 100 x 175cm

Quantité : 2

Battants : Simple à âme pleine

Localisation : Jardin creche, escalier


Remarques :

SEX_PSB_CH01
100*175

SEX_PSB_CH02
100*175

Vue en plan :

Élévation :

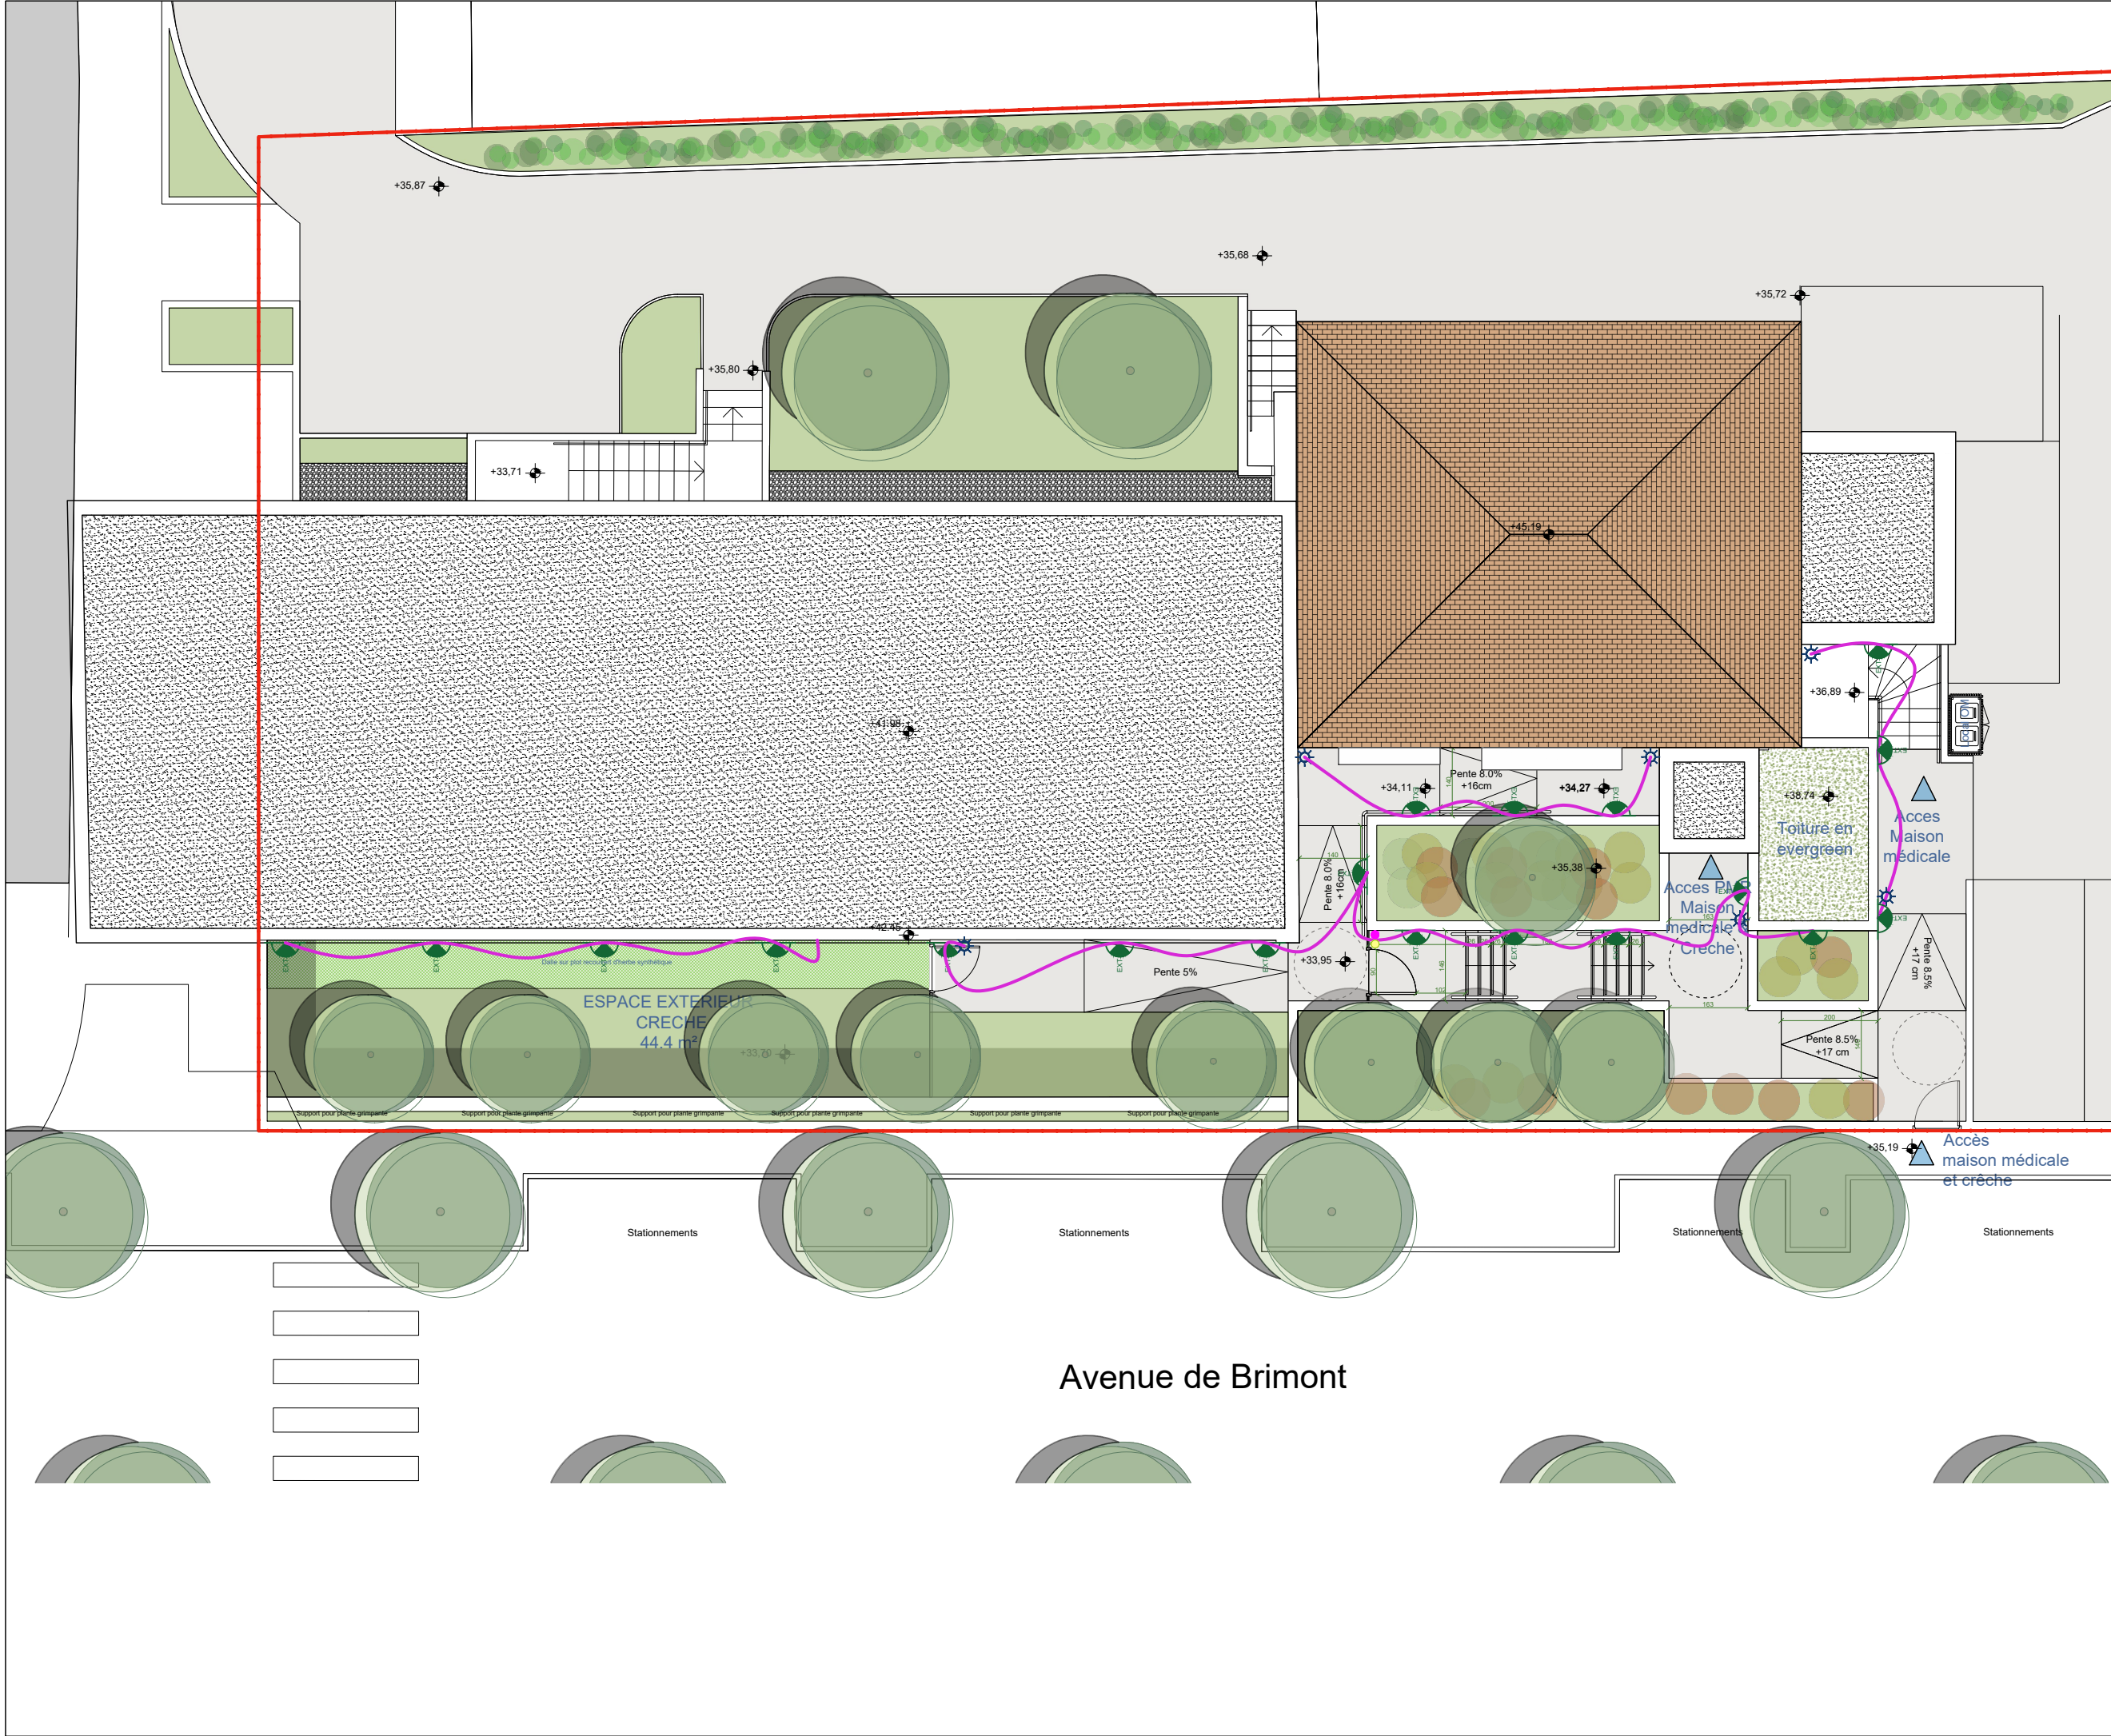

CREATION D'UN MULTI-ACCUEIL
49 RUE ARISTIDE BRIAND
94430 CHENNEVIERES-SUR-MARNE

MOA

SARL LPC YVELINES
15 Rue de l'Orient78000 VERSAILLES

MOE

NAHK ARCHITECTURE
24 Rue Yves Toudic, 75010 Paris

NOM DU DOCUMENT

AMENAGEMENT
EXTERIEUR
ELECTRICITE

PHASE

PRO.DCE

ECH.

1/100

INDICE

1.1

DATE

07/06/2023

MODIFICATIONS

INDICE	DATE	OBJET
1.1	07/06/2023	Diffusion initiale


ELECTRICITE

• TYPE 4 - APPLIQUE MURALE
DELTALIGHT TOPIX WW

• DETECTEUR DE PRESENCE
AVEC MINUTERIE

• VISIOPHONE AVEC VENTOUS

• DIGICODE

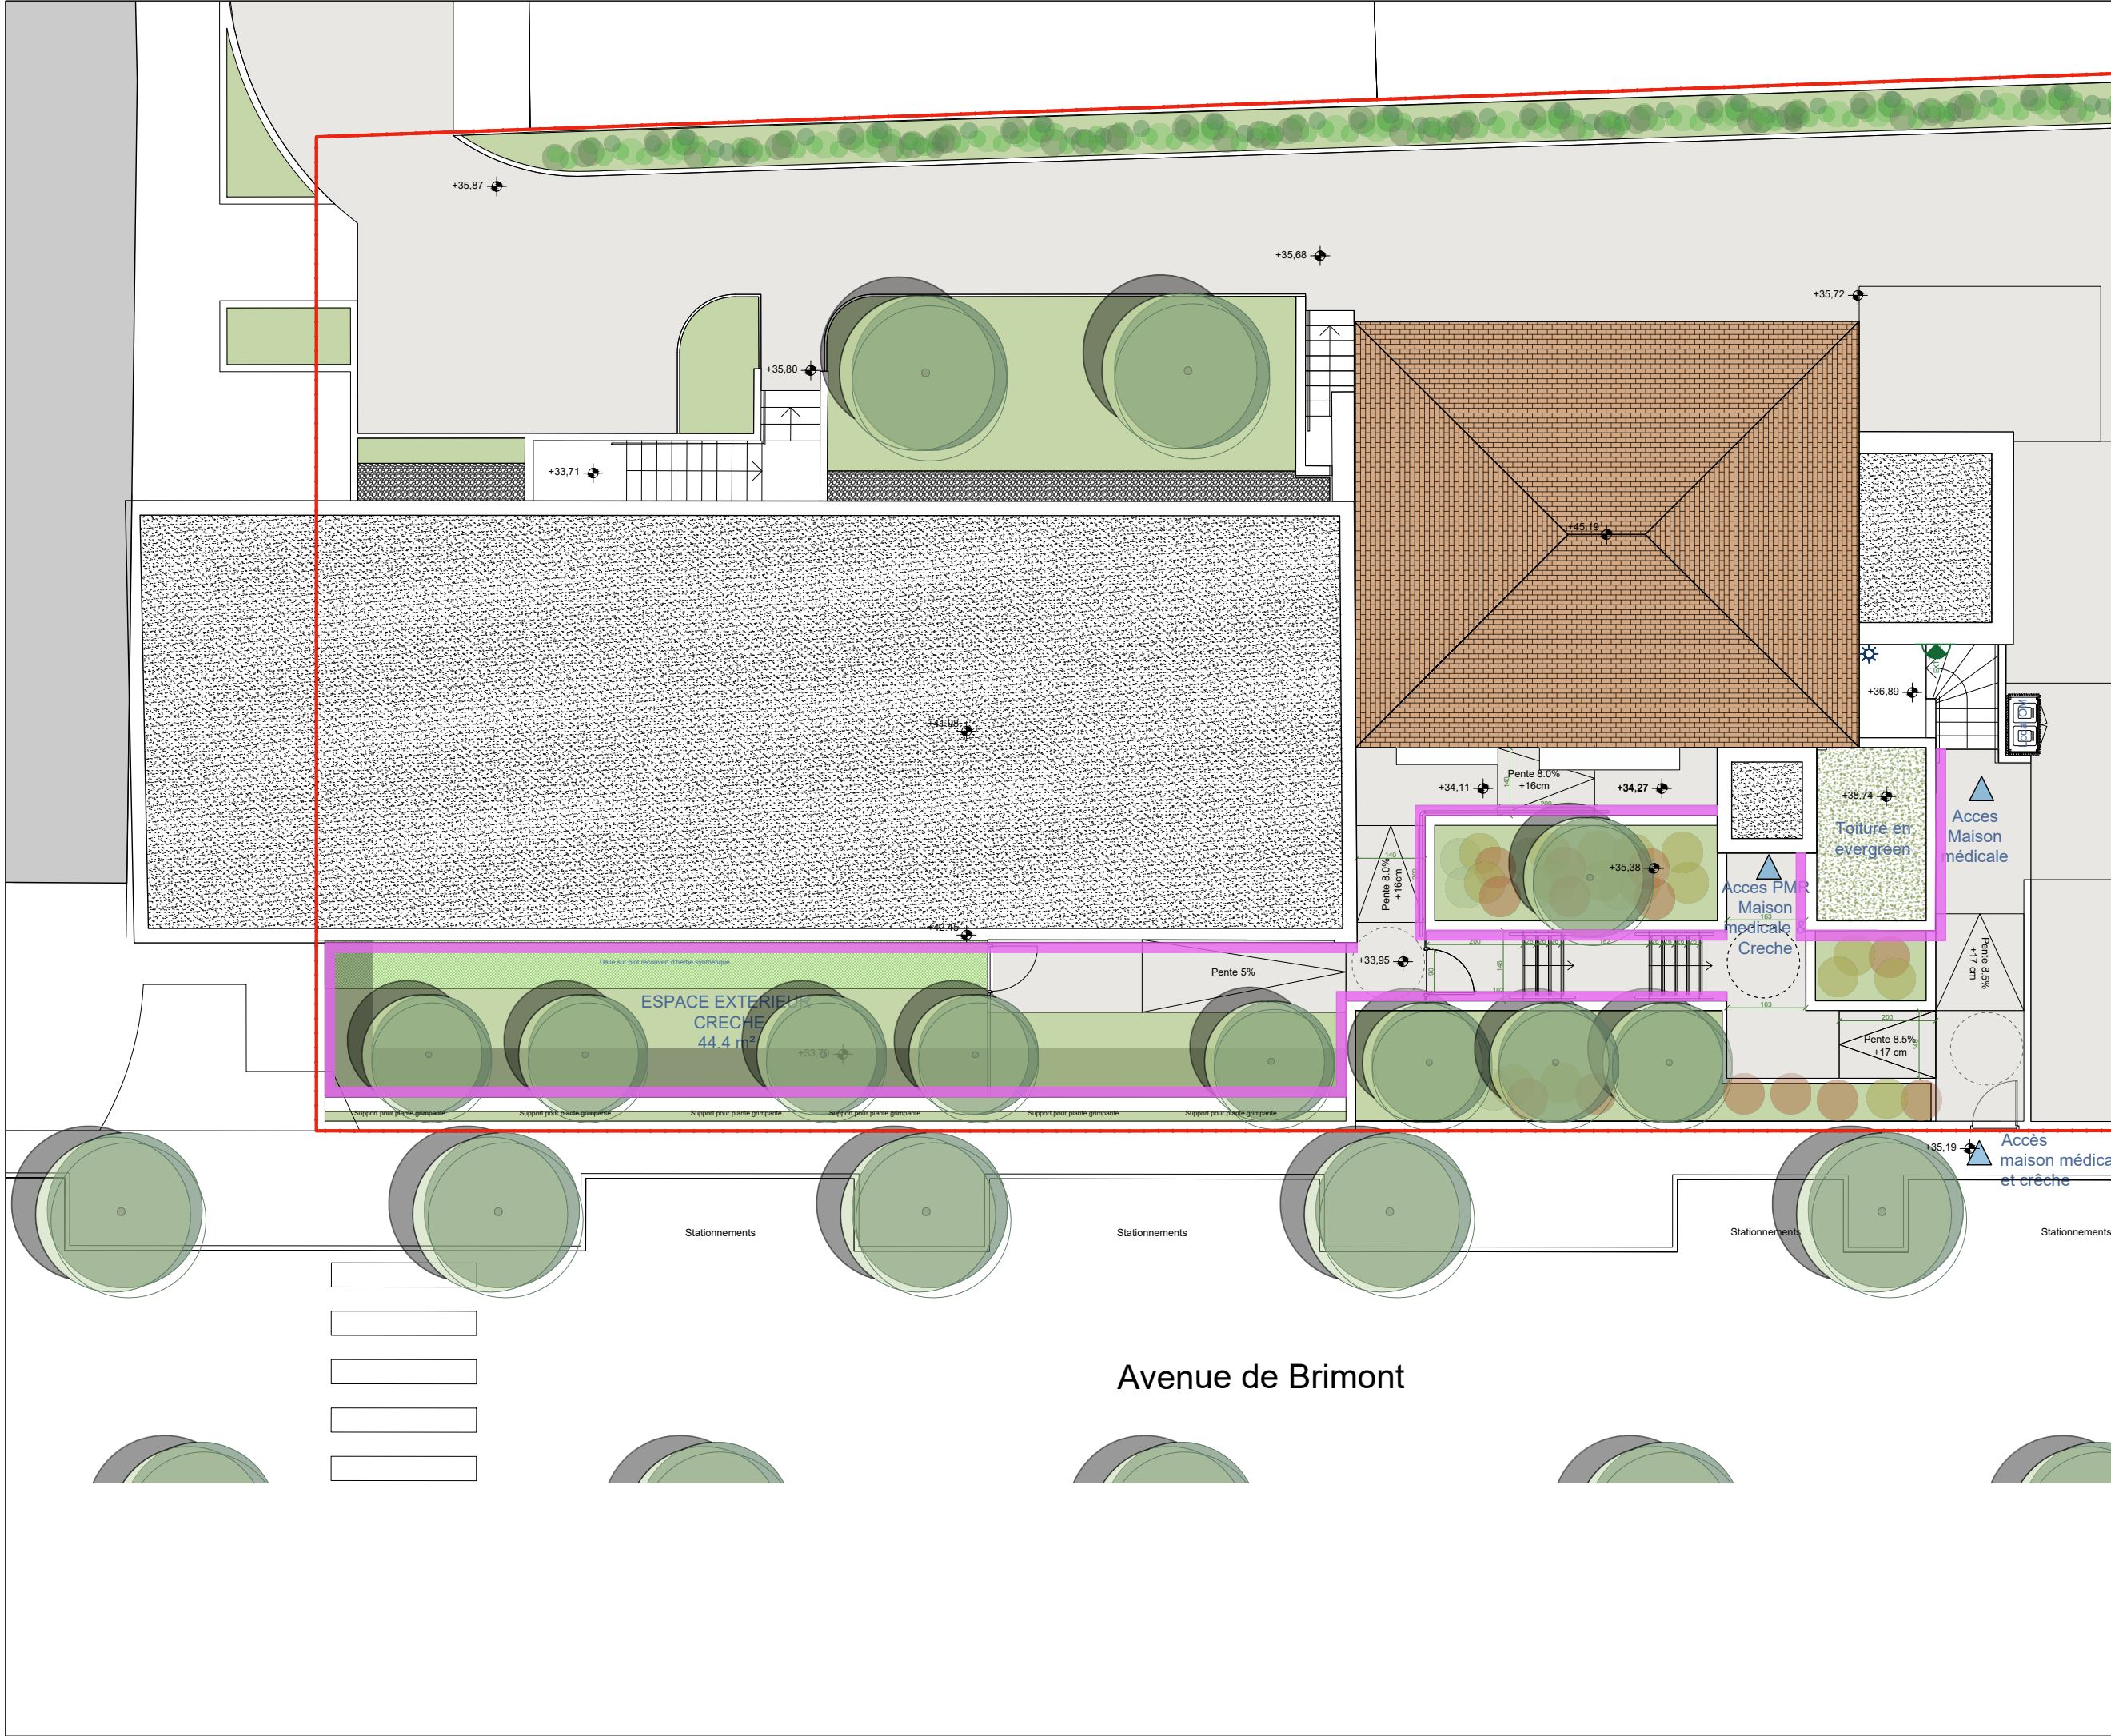

CREATION D'UN MULTI-ACCUEIL 49 RUE ARISTIDE BRIAND 94430 CHENNEVIERES-SUR-MARNE			
MOA	SARL LPC YVELINES 15 Rue de l'Orient78000 VERSAILLES		
MOE	NAHK ARCHITECTURE 24 Rue Yves Toudic, 75010 Paris		
NOM DU DOCUMENT			
AMENAGEMENT EXTERIEUR REVETEMENT MURAL			
PHASE	PRO.DCE	ECH.	1/100
INDICE	1.1	DATE	07/06/2023
MODIFICATIONS			
INDICE DATE		OBJET	
1.1	07/06/2023	Diffusion initiale	
REVETEMENT DE FACADE			
• Enduit minéral dito existant			




CREATION D'UN MULTI-ACCUEIL 49 RUE ARISTIDE BRIAND 94430 CHENNEVIERES-SUR-MARNE			
MOA	SARL LPC YVELINES 15 Rue de l'Orient78000 VERSAILLES		
MOE	NAHK ARCHITECTURE 24 Rue Yves Toudic, 75010 Paris		
NOM DU DOCUMENT			
COUPE DANS LE JARDIN			
PHASE	PRO.DCE	ECH.	1/100
INDICE	1.1	DATE	07/06/2023
MODIFICATIONS			
INDICE DATE		OBJET	
1.1	07/06/2023	Diffusion initiale	
SERRURERIE • CLOTURE NOMACLO OBAMBOO 2M			



CREATION D'UN MULTI-ACCUEIL 49 RUE ARISTIDE BRIAND 94430 CHENNEVIERES-SUR-MARNE			
MOA	SARL LPC YVELINES 15 Rue de l'Orient78000 VERSAILLES		
MOE	NAHK ARCHITECTURE 24 Rue Yves Toudic, 75010 Paris		
NOM DU DOCUMENT			
COUPE DANS LE JARDIN			
PHASE	PRO.DCE	ECH.	1/20
INDICE	1.1	DATE	07/06/2023
MODIFICATIONS			
INDICE DATE		OBJET	
1.1	07/06/2023	Diffusion initiale	

REVETEMENT DE FACADE

• Enduit minéral dito existant

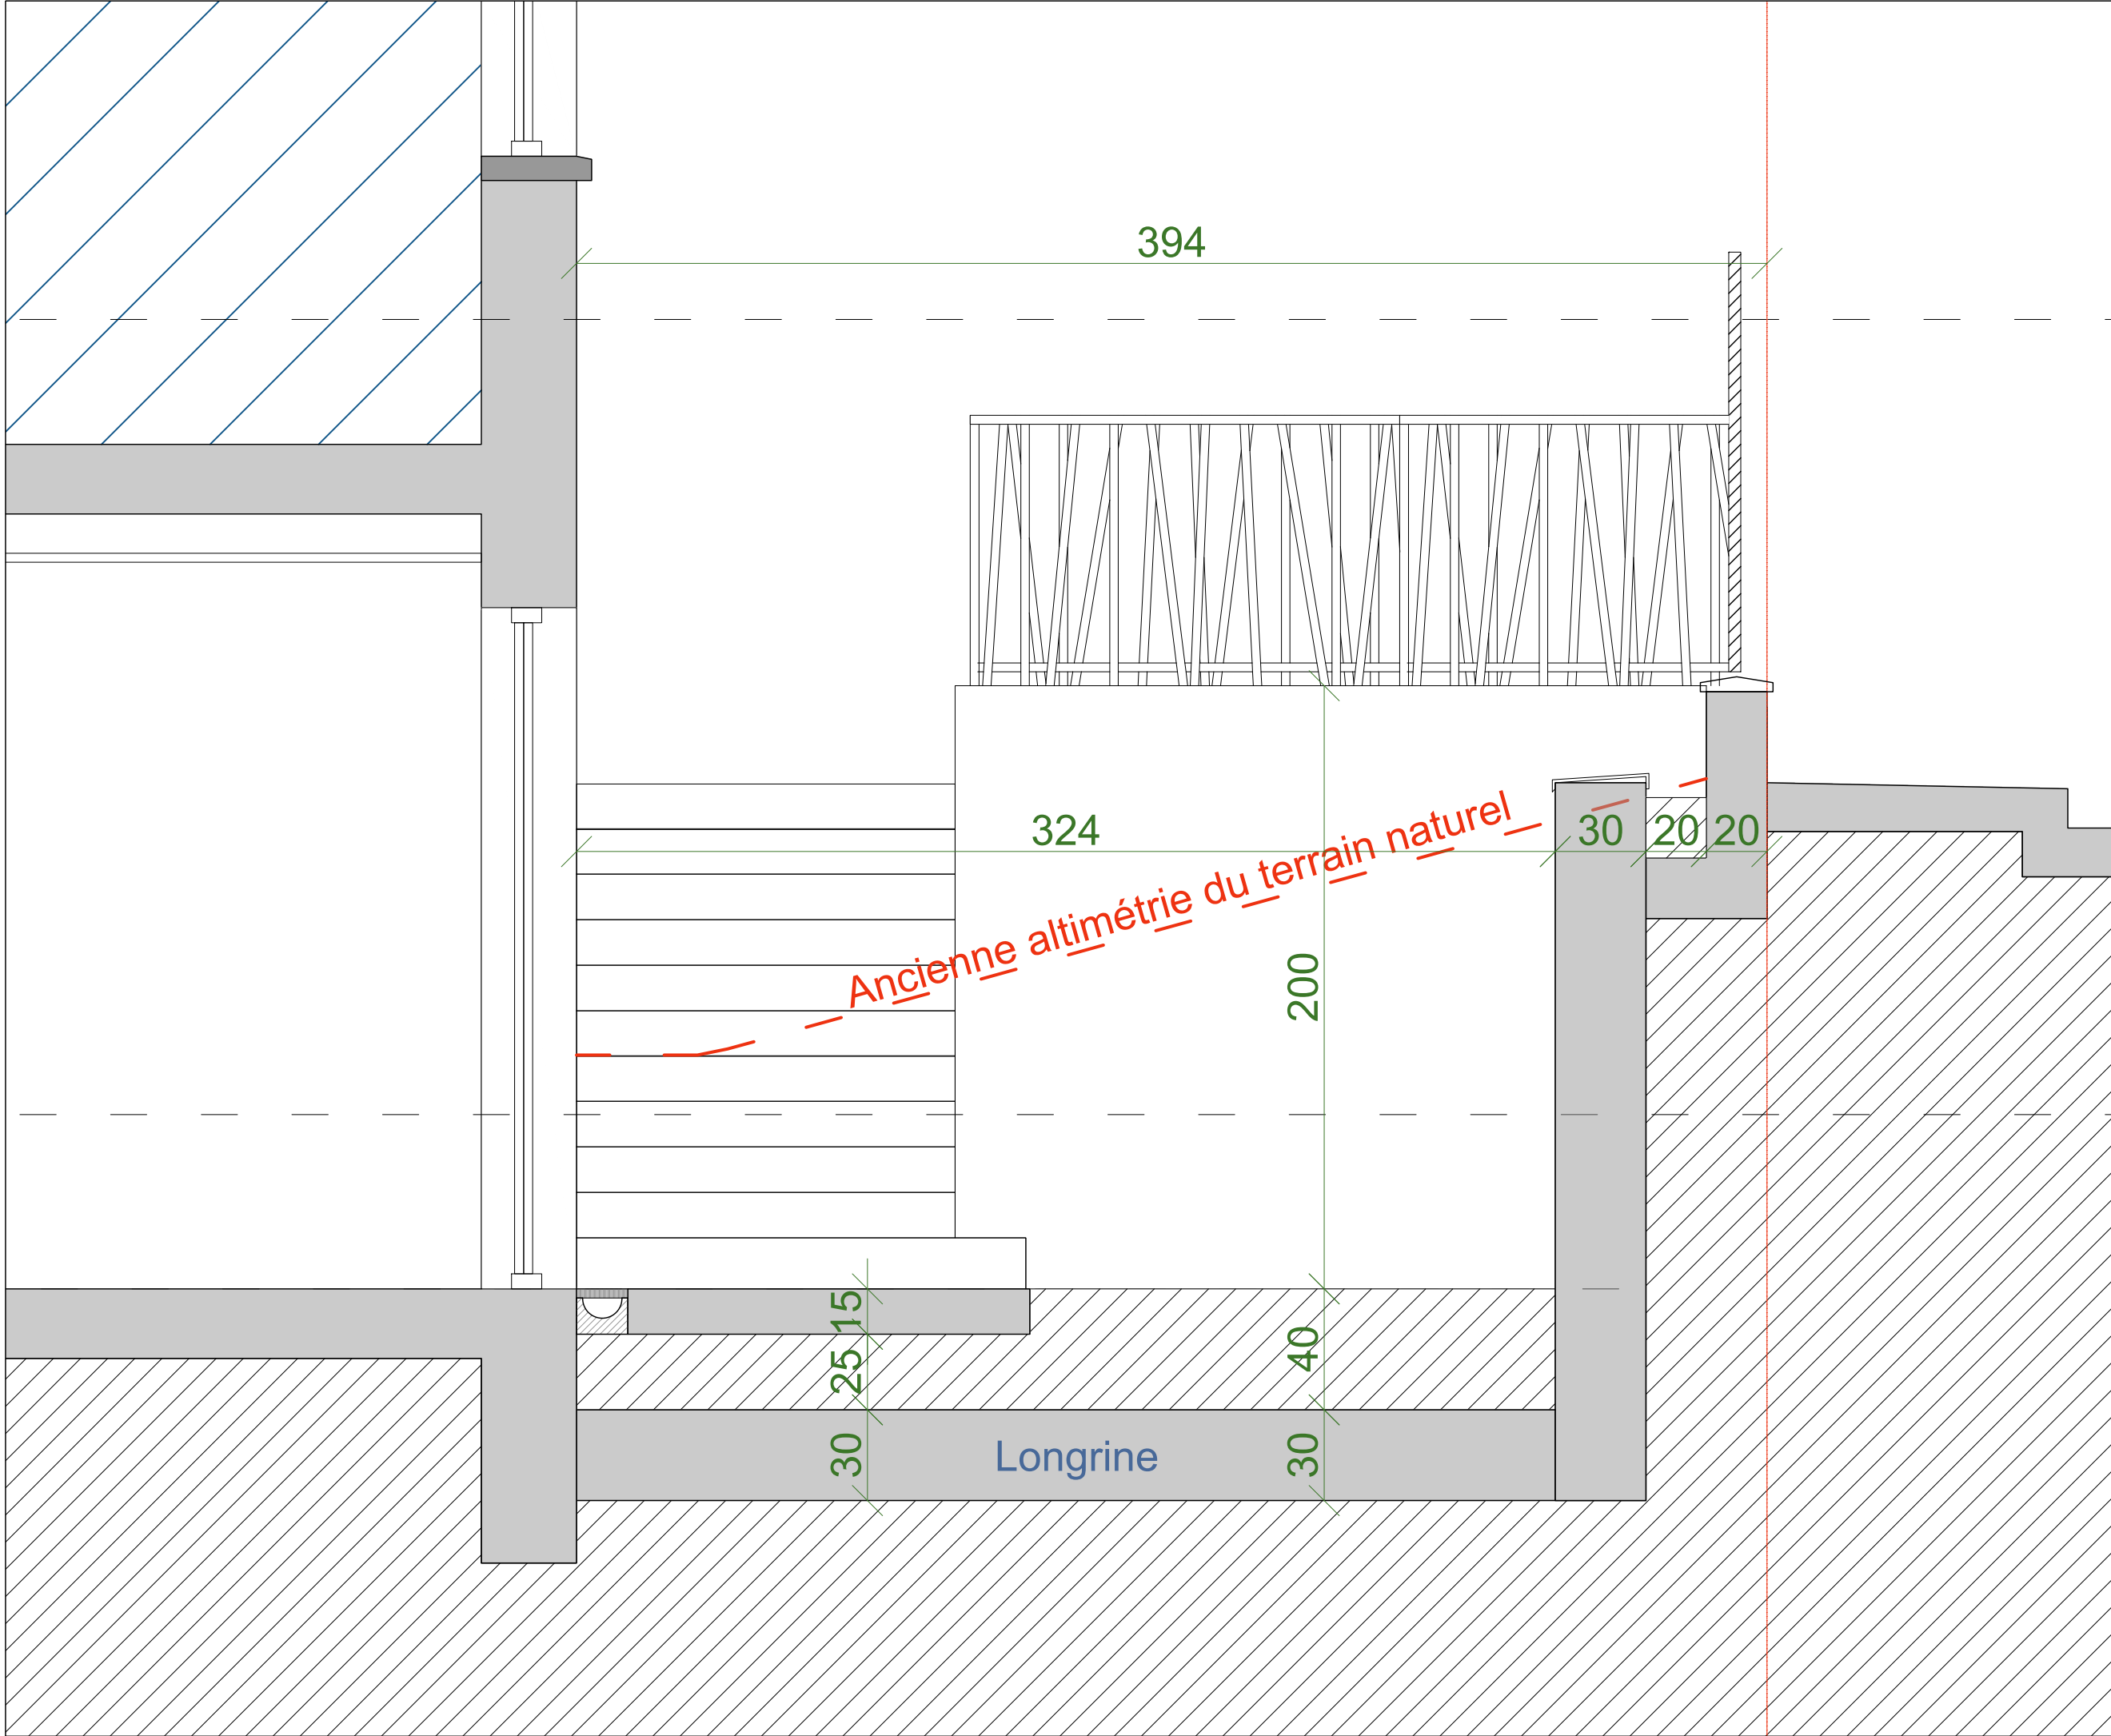

CREATION D'UN MULTI-ACCUEIL 49 RUE ARISTIDE BRIAND 94430 CHENNEVIERES-SUR-MARNE			
MOA	SARL LPC YVELINES 15 Rue de l'Orient78000 VERSAILLES		
MOE	NAHK ARCHITECTURE 24 Rue Yves Toudic, 75010 Paris		
NOM DU DOCUMENT			
DETAIL MUR DE SOUTÈNEMENT			
PHASE	PRO.DCE	ECH.	1/20
INDICE	1.1	DATE	07/06/2023
MODIFICATIONS			
INDICE DATE		OBJET	
1.1	07/06/2023	Diffusion initiale	