

DOS-
SIER
DCE

MAISON MEDICALE

78 400 CHATOU



MOA : SARL LPC YVELINES

15 Rue de l'Orient 78000 VERSAILLES



Les Petites Canailles


MAITRE D'OEUVRE  NAHK ARCHITECTURE 24 rue Yves Toudic - 75010 PARIS	PHASE DCE	VERSION 01	DATE 04/07/2023	OPÉRATION CREATION D'UN MULTI ACCUEIL DE 30 BERCEAUX ET REAMENAGEMENT D'UNE MAISON MEDICALE 30 ter Avenue de Brimont 78400 CHATOU	MAITRE D'OUVRAGE SARL LPC YVELINES 15 Rue de l'Orient78000 VERSAILLES	N° DOC --	NOM DU DOCUMENT	ÉCHELLE --
--	---------------------------------	----------------------------------	---------------------------------------	---	---	---------------------------------	--	----------------------------------

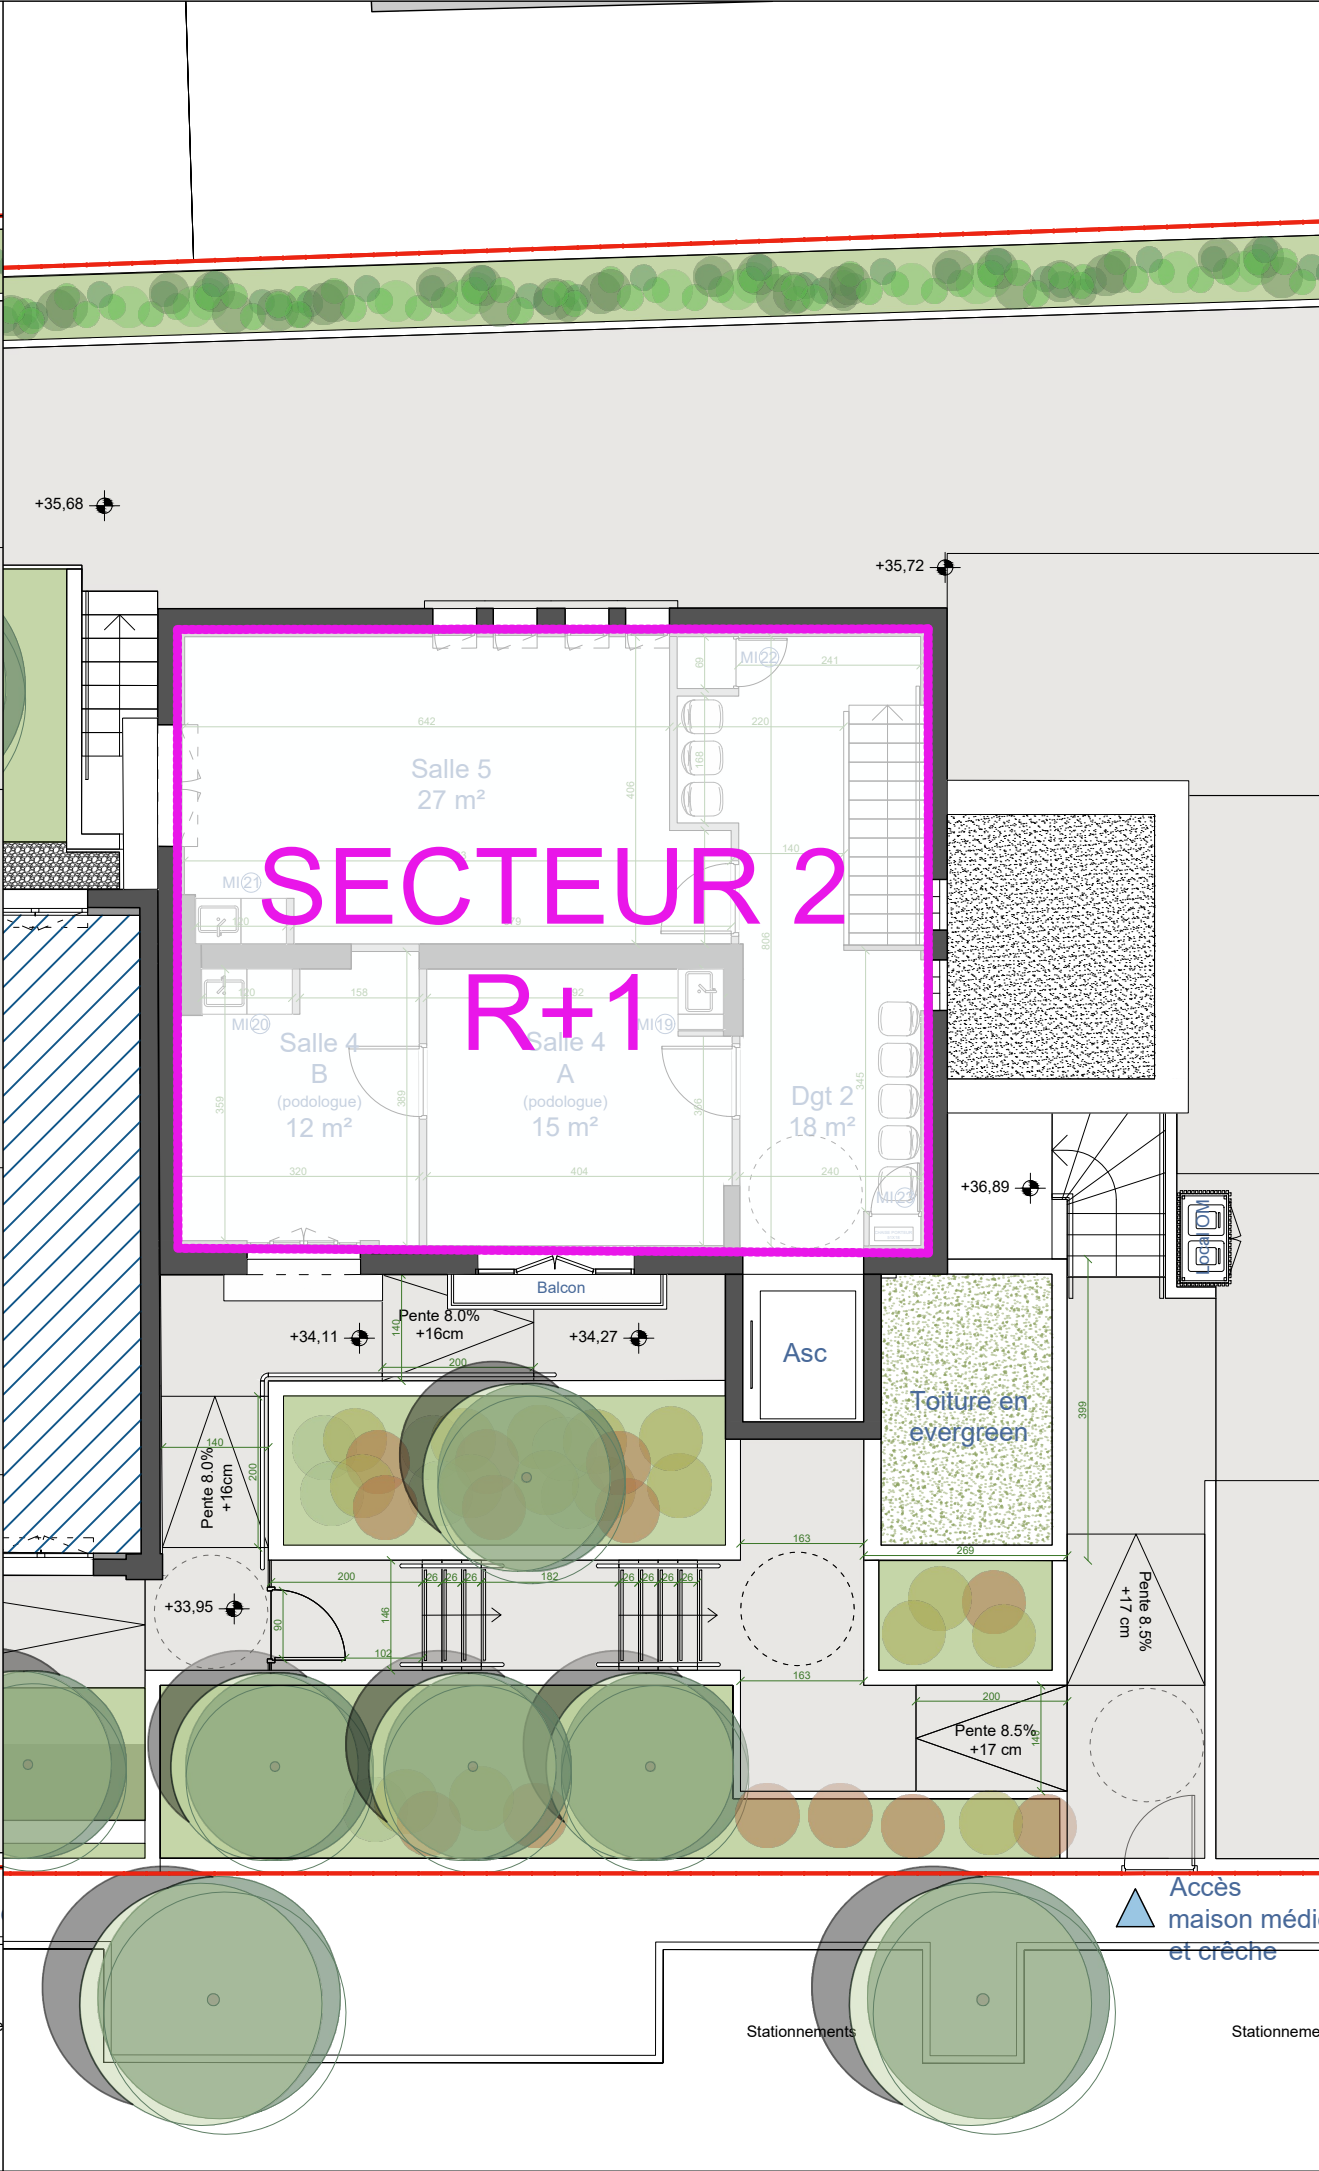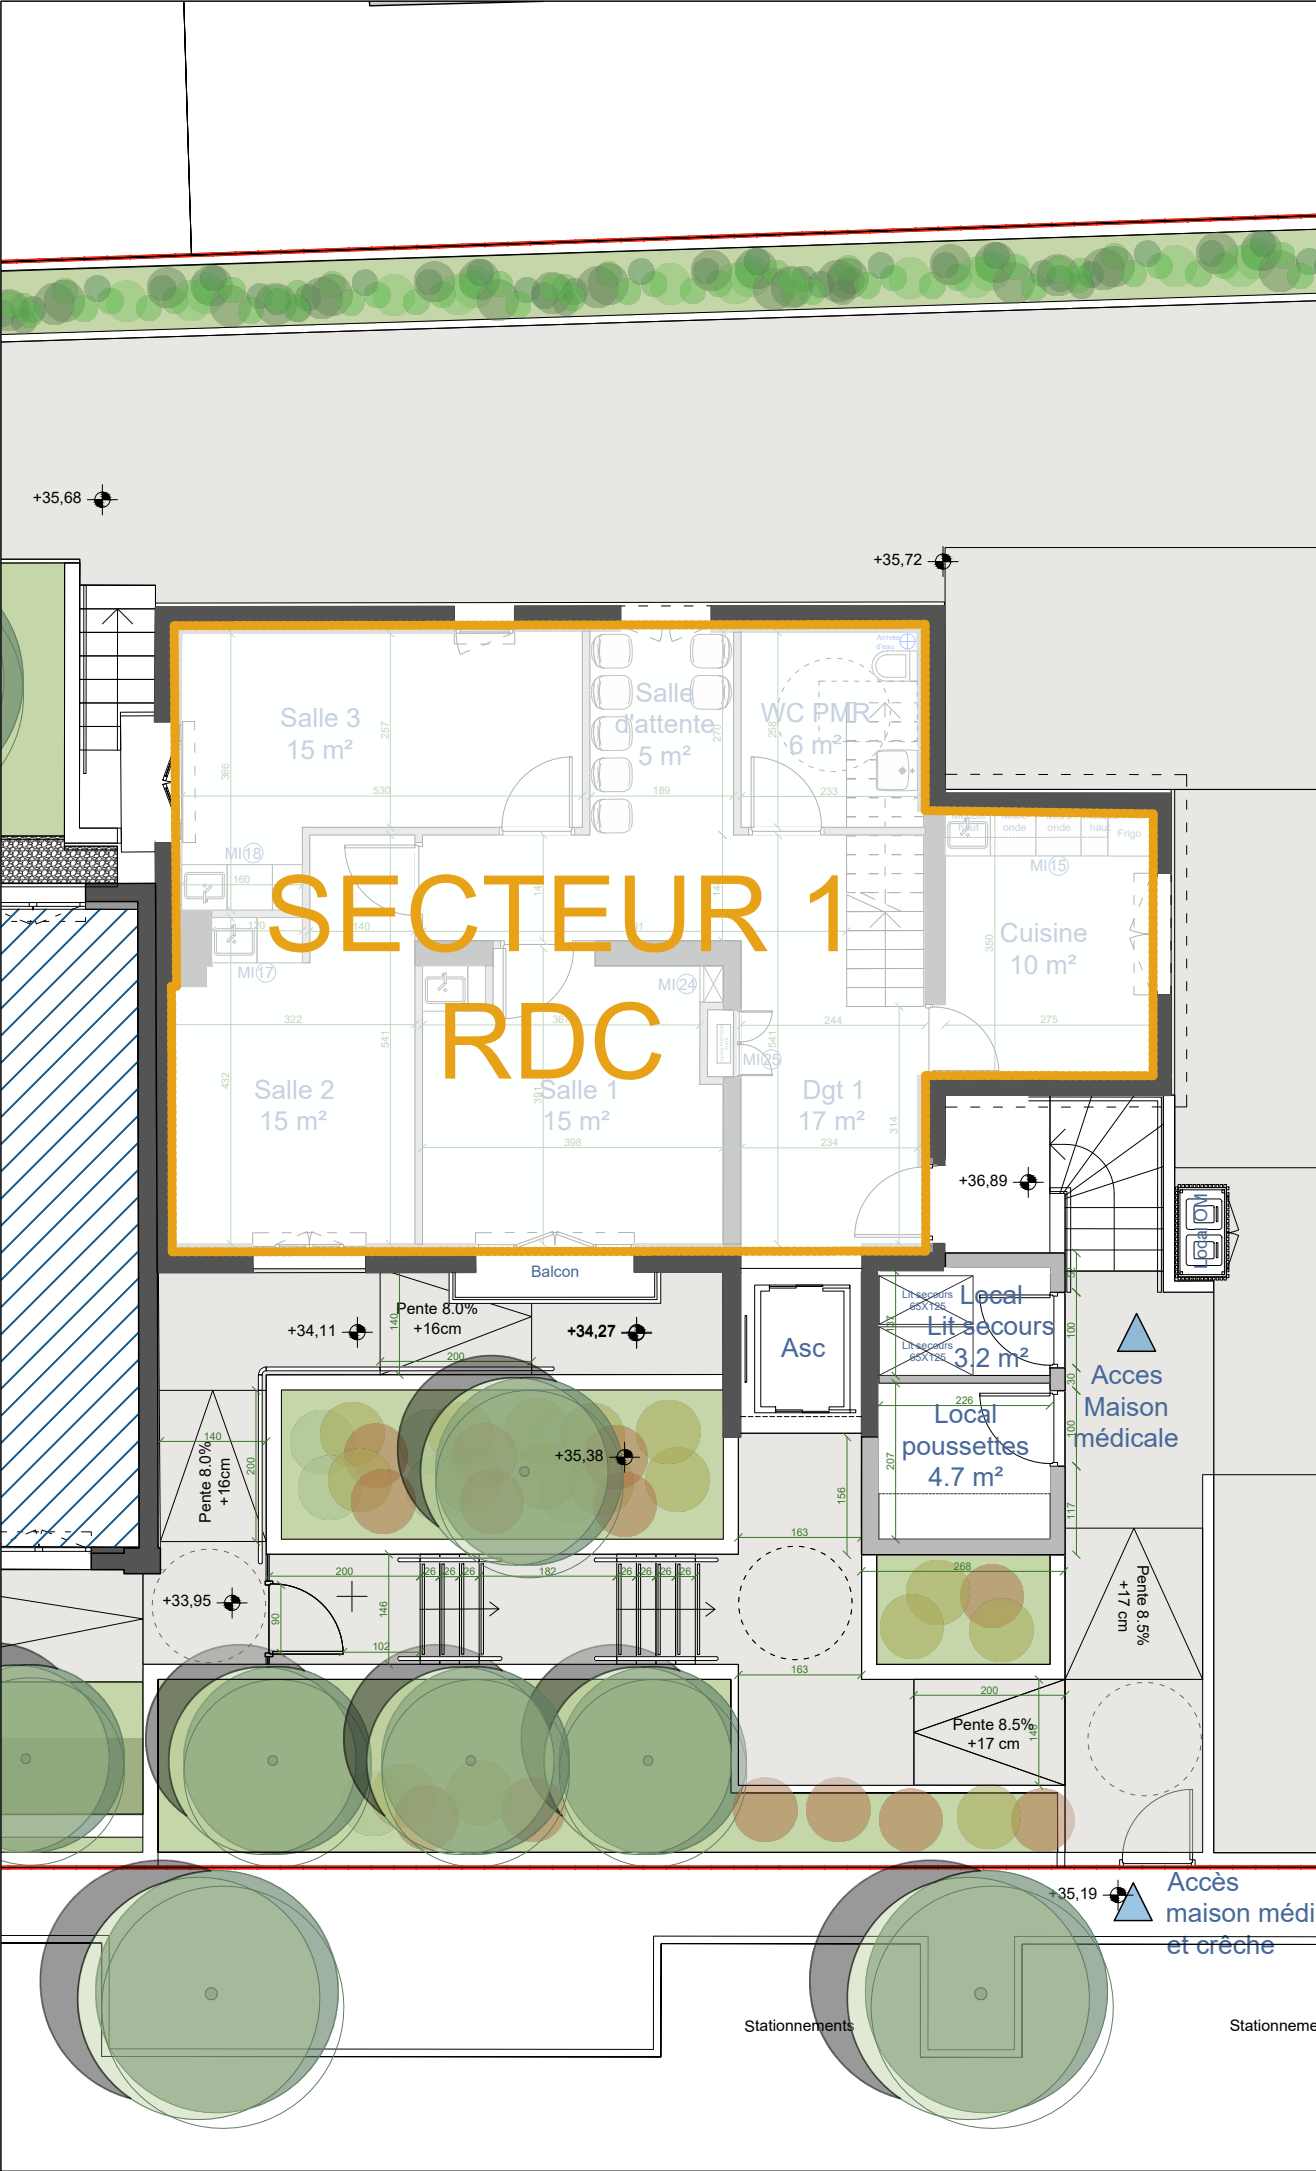


CREATION D'UN MULTI-ACCUEIL ET D'UNE MAISON MEDICALE 78400 CHATOU			
MOA	SARL LPC YVELINES 15 Rue de l'Orient78000 VERSAILLES		
MOE	NAHK ARCHITECTURE 24 Rue Yves Toudic, 75010 Paris		
NOM DU DOCUMENT			
PLAN DE LOCALISATION DES SECTEURS			
PHASE	PRO.DCE	ECH.	1/100
INDICE	1.1	DATE	04/07/2023
MODIFICATIONS			
INDICE DATE		OBJET	
1.1	04/07/2023	Diffusion initiale	
SECTEUR 1 SECTEUR 2			



CREATION D'UN MULTI-ACCUEIL ET D'UNE MAISON MEDICALE 78400 CHATOU			
MOA	SARL LPC YVELINES 15 Rue de l'Orient78000 VERSAILLES		
MOE	NAHK ARCHITECTURE 24 Rue Yves Toudic, 75010 Paris		
NOM DU DOCUMENT			
PLAN RDC SECTEUR 1			
PHASE	PRO.DCE	ECH.	1/50
INDICE	1.1	DATE	04/07/2023
MODIFICATIONS			
INDICE DATE		OBJET	
1.1	04/07/2023	Diffusion initiale	

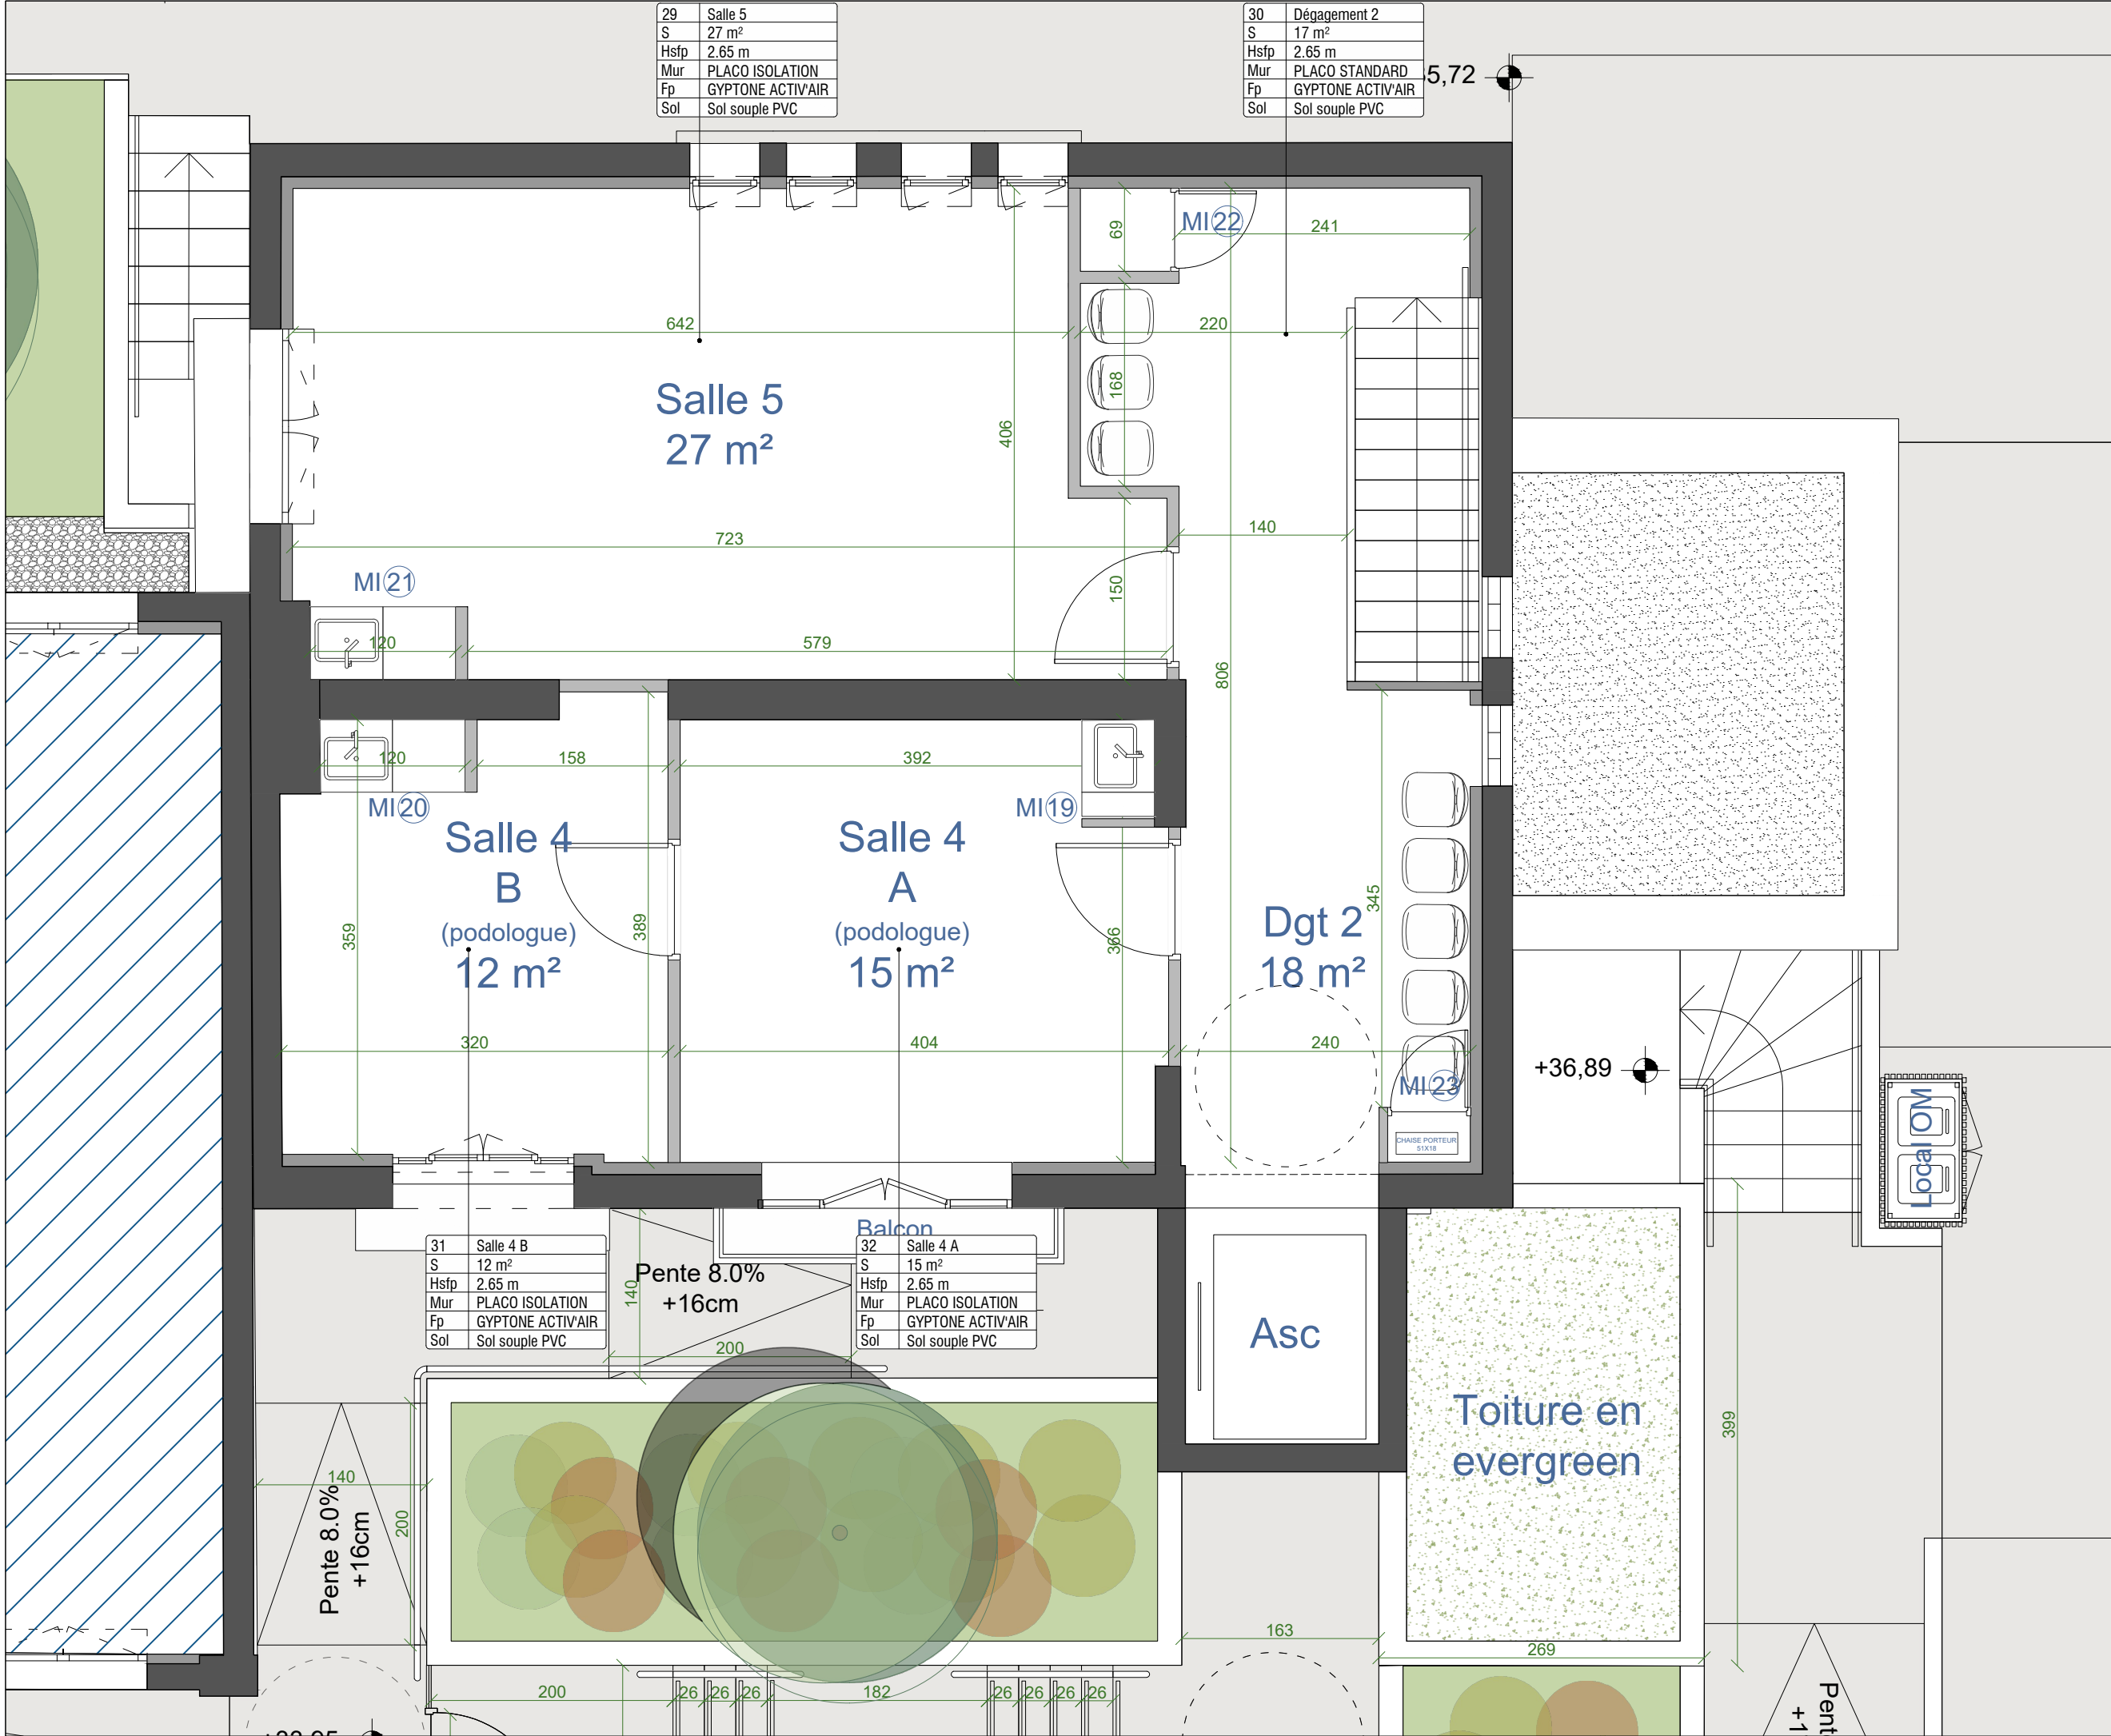

CREATION D'UN MULTI-ACCUEIL ET D'UNE MAISON MEDICALE 78400 CHATOU			
MOA	SARL LPC YVELINES 15 Rue de l'Orient78000 VERSAILLES		
MOE	NAHK ARCHITECTURE 24 Rue Yves Toudic, 75010 Paris		
NOM DU DOCUMENT			
PLAN R+1 SECTEUR 2			
PHASE	PRO.DCE	ECH.	1/50
INDICE	1.1	DATE	04/07/2023
MODIFICATIONS			
INDICE DATE		OBJET	
1.1	04/07/2023	Diffusion initiale	

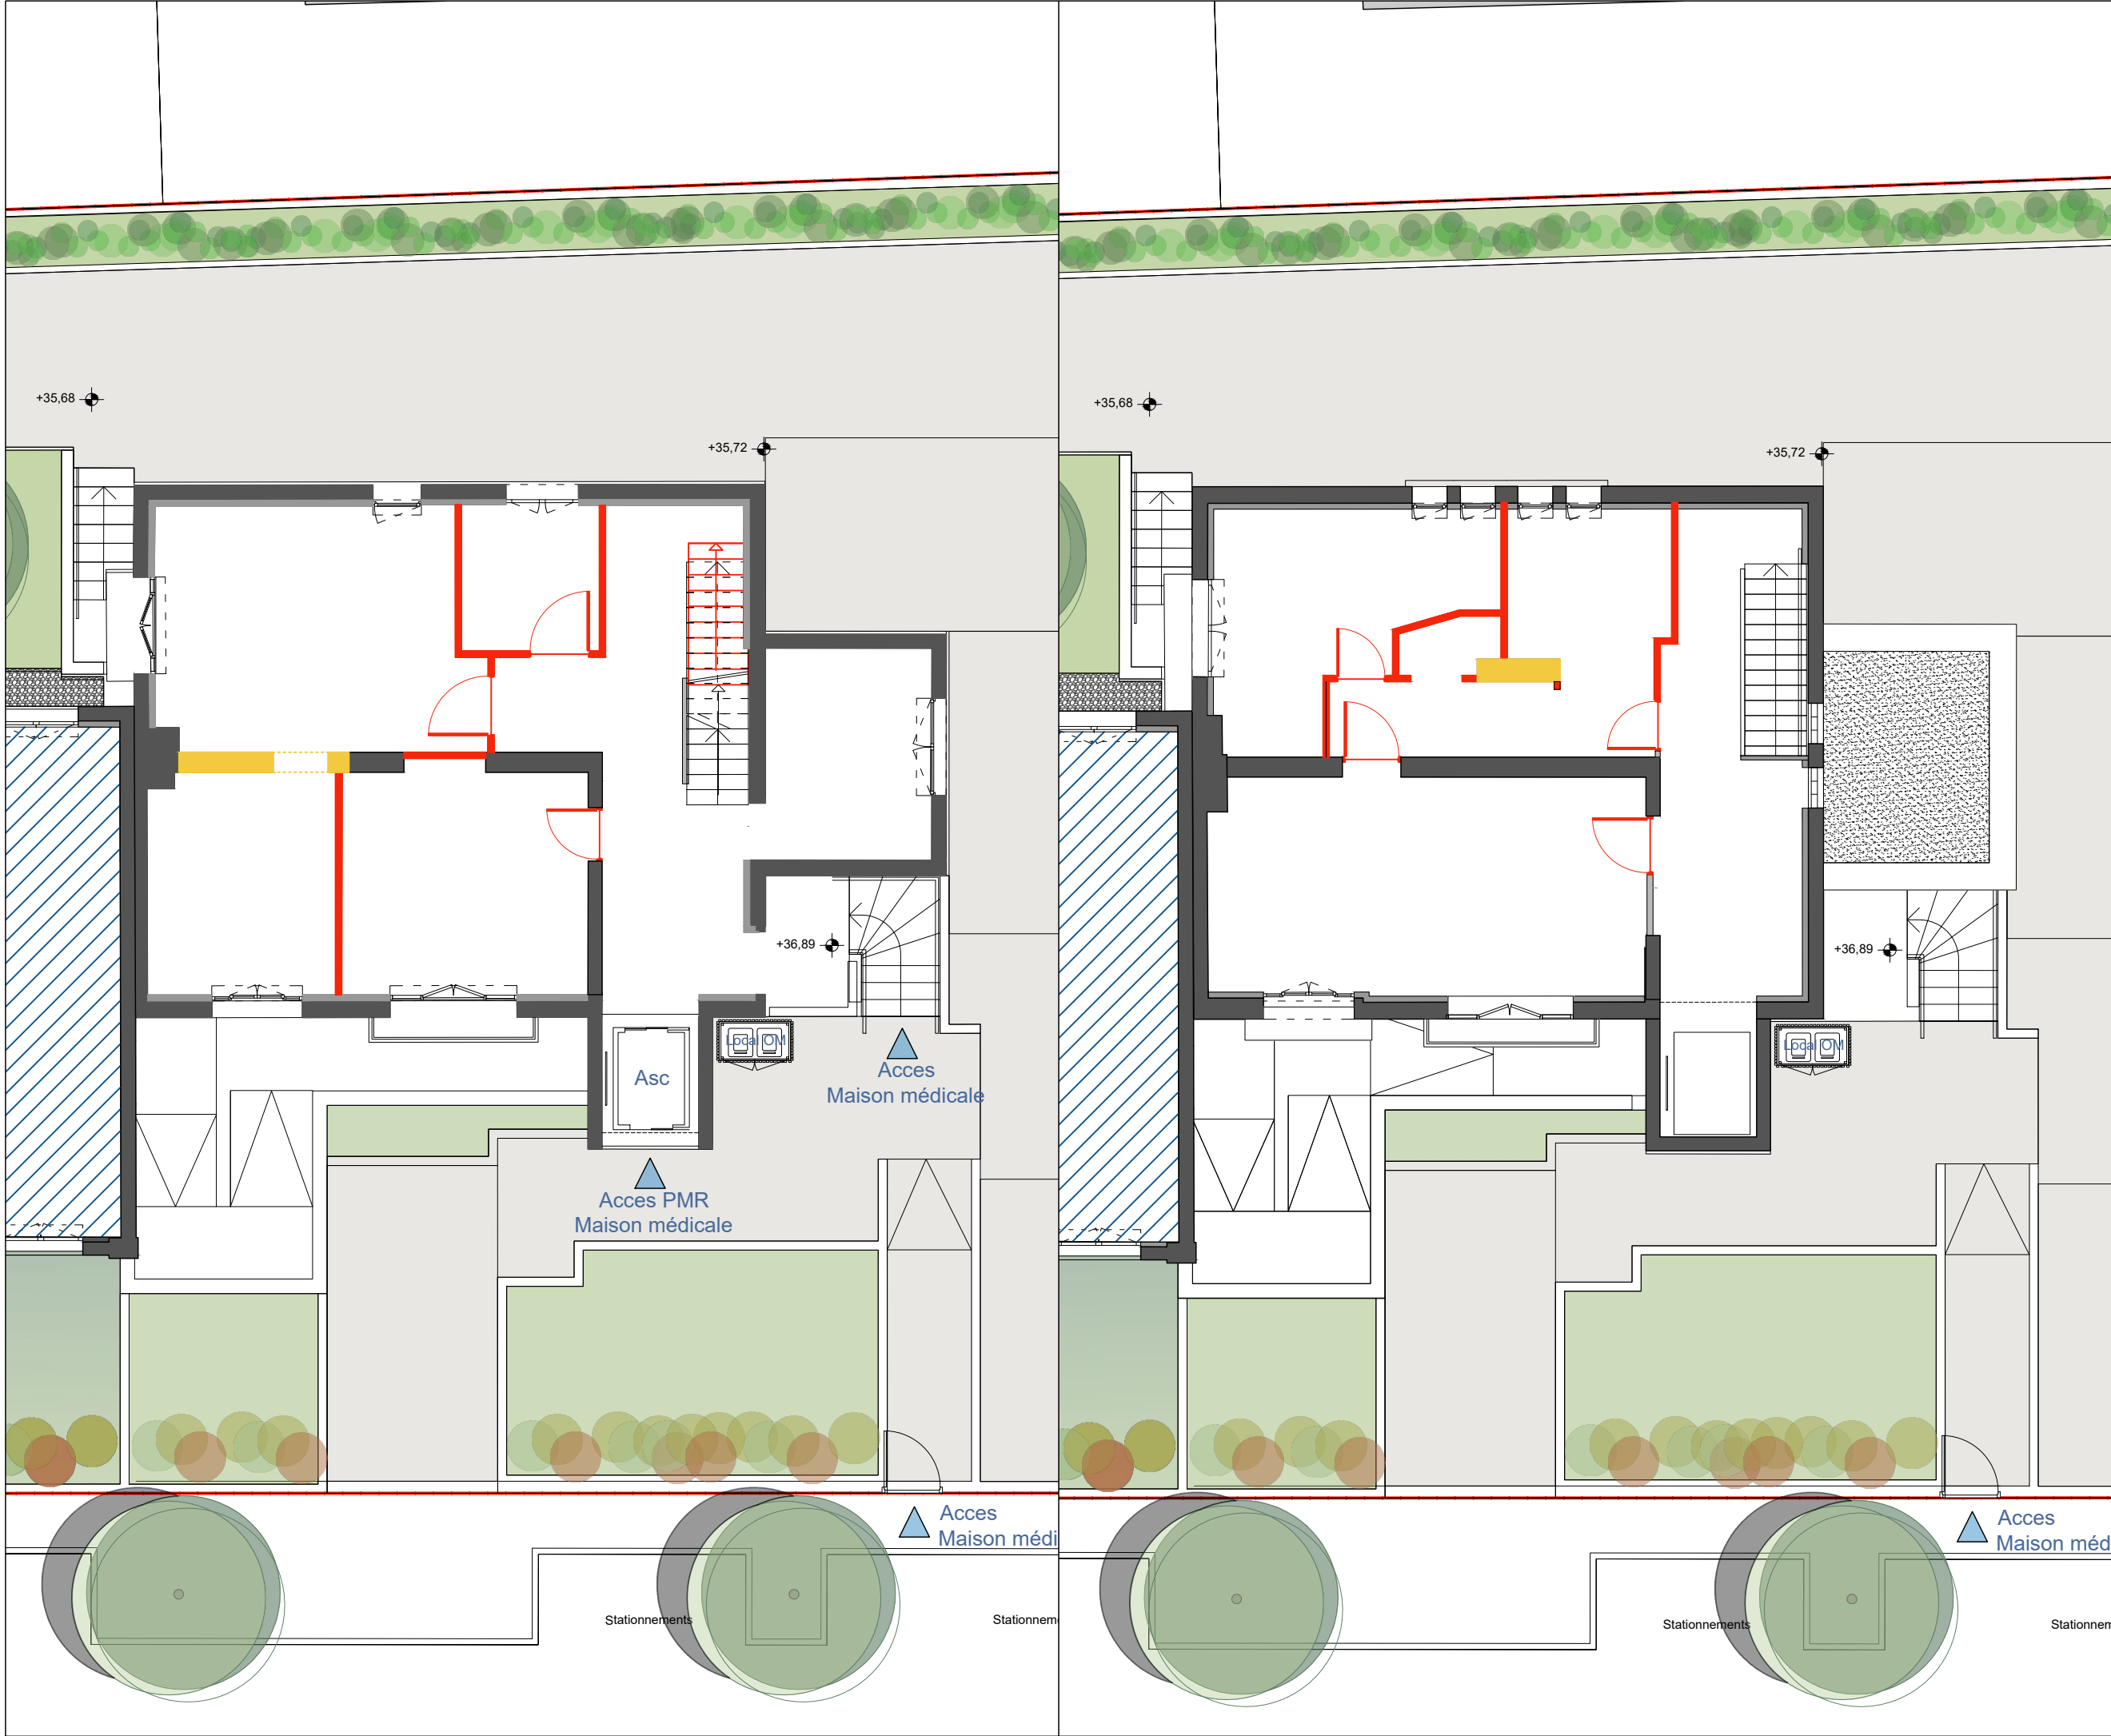

CREATION D'UN MULTI-ACCUEIL ET
D'UNE MAISON MEDICALE
78400 CHATOU

MOA

SARL LPC YVELINES
15 Rue de l'Orient78000 VERSAILLES

MOE

NAHK ARCHITECTURE
24 Rue Yves Toudic, 75010 Paris

NOM DU DOCUMENT

PLAN DE LOCALISATION
DES DEMOLITIONS

PHASE

PRO.DCE

ECH.

1/100

INDICE

1.1

DATE

04/07/2023

MODIFICATIONS

INDICE

DATE

OBJET

1.1


04/07/2023


Diffusion initiale


DEMOLITION


• CLOISON DEMOLIE

• MUR PORTEUR DEMOLIE

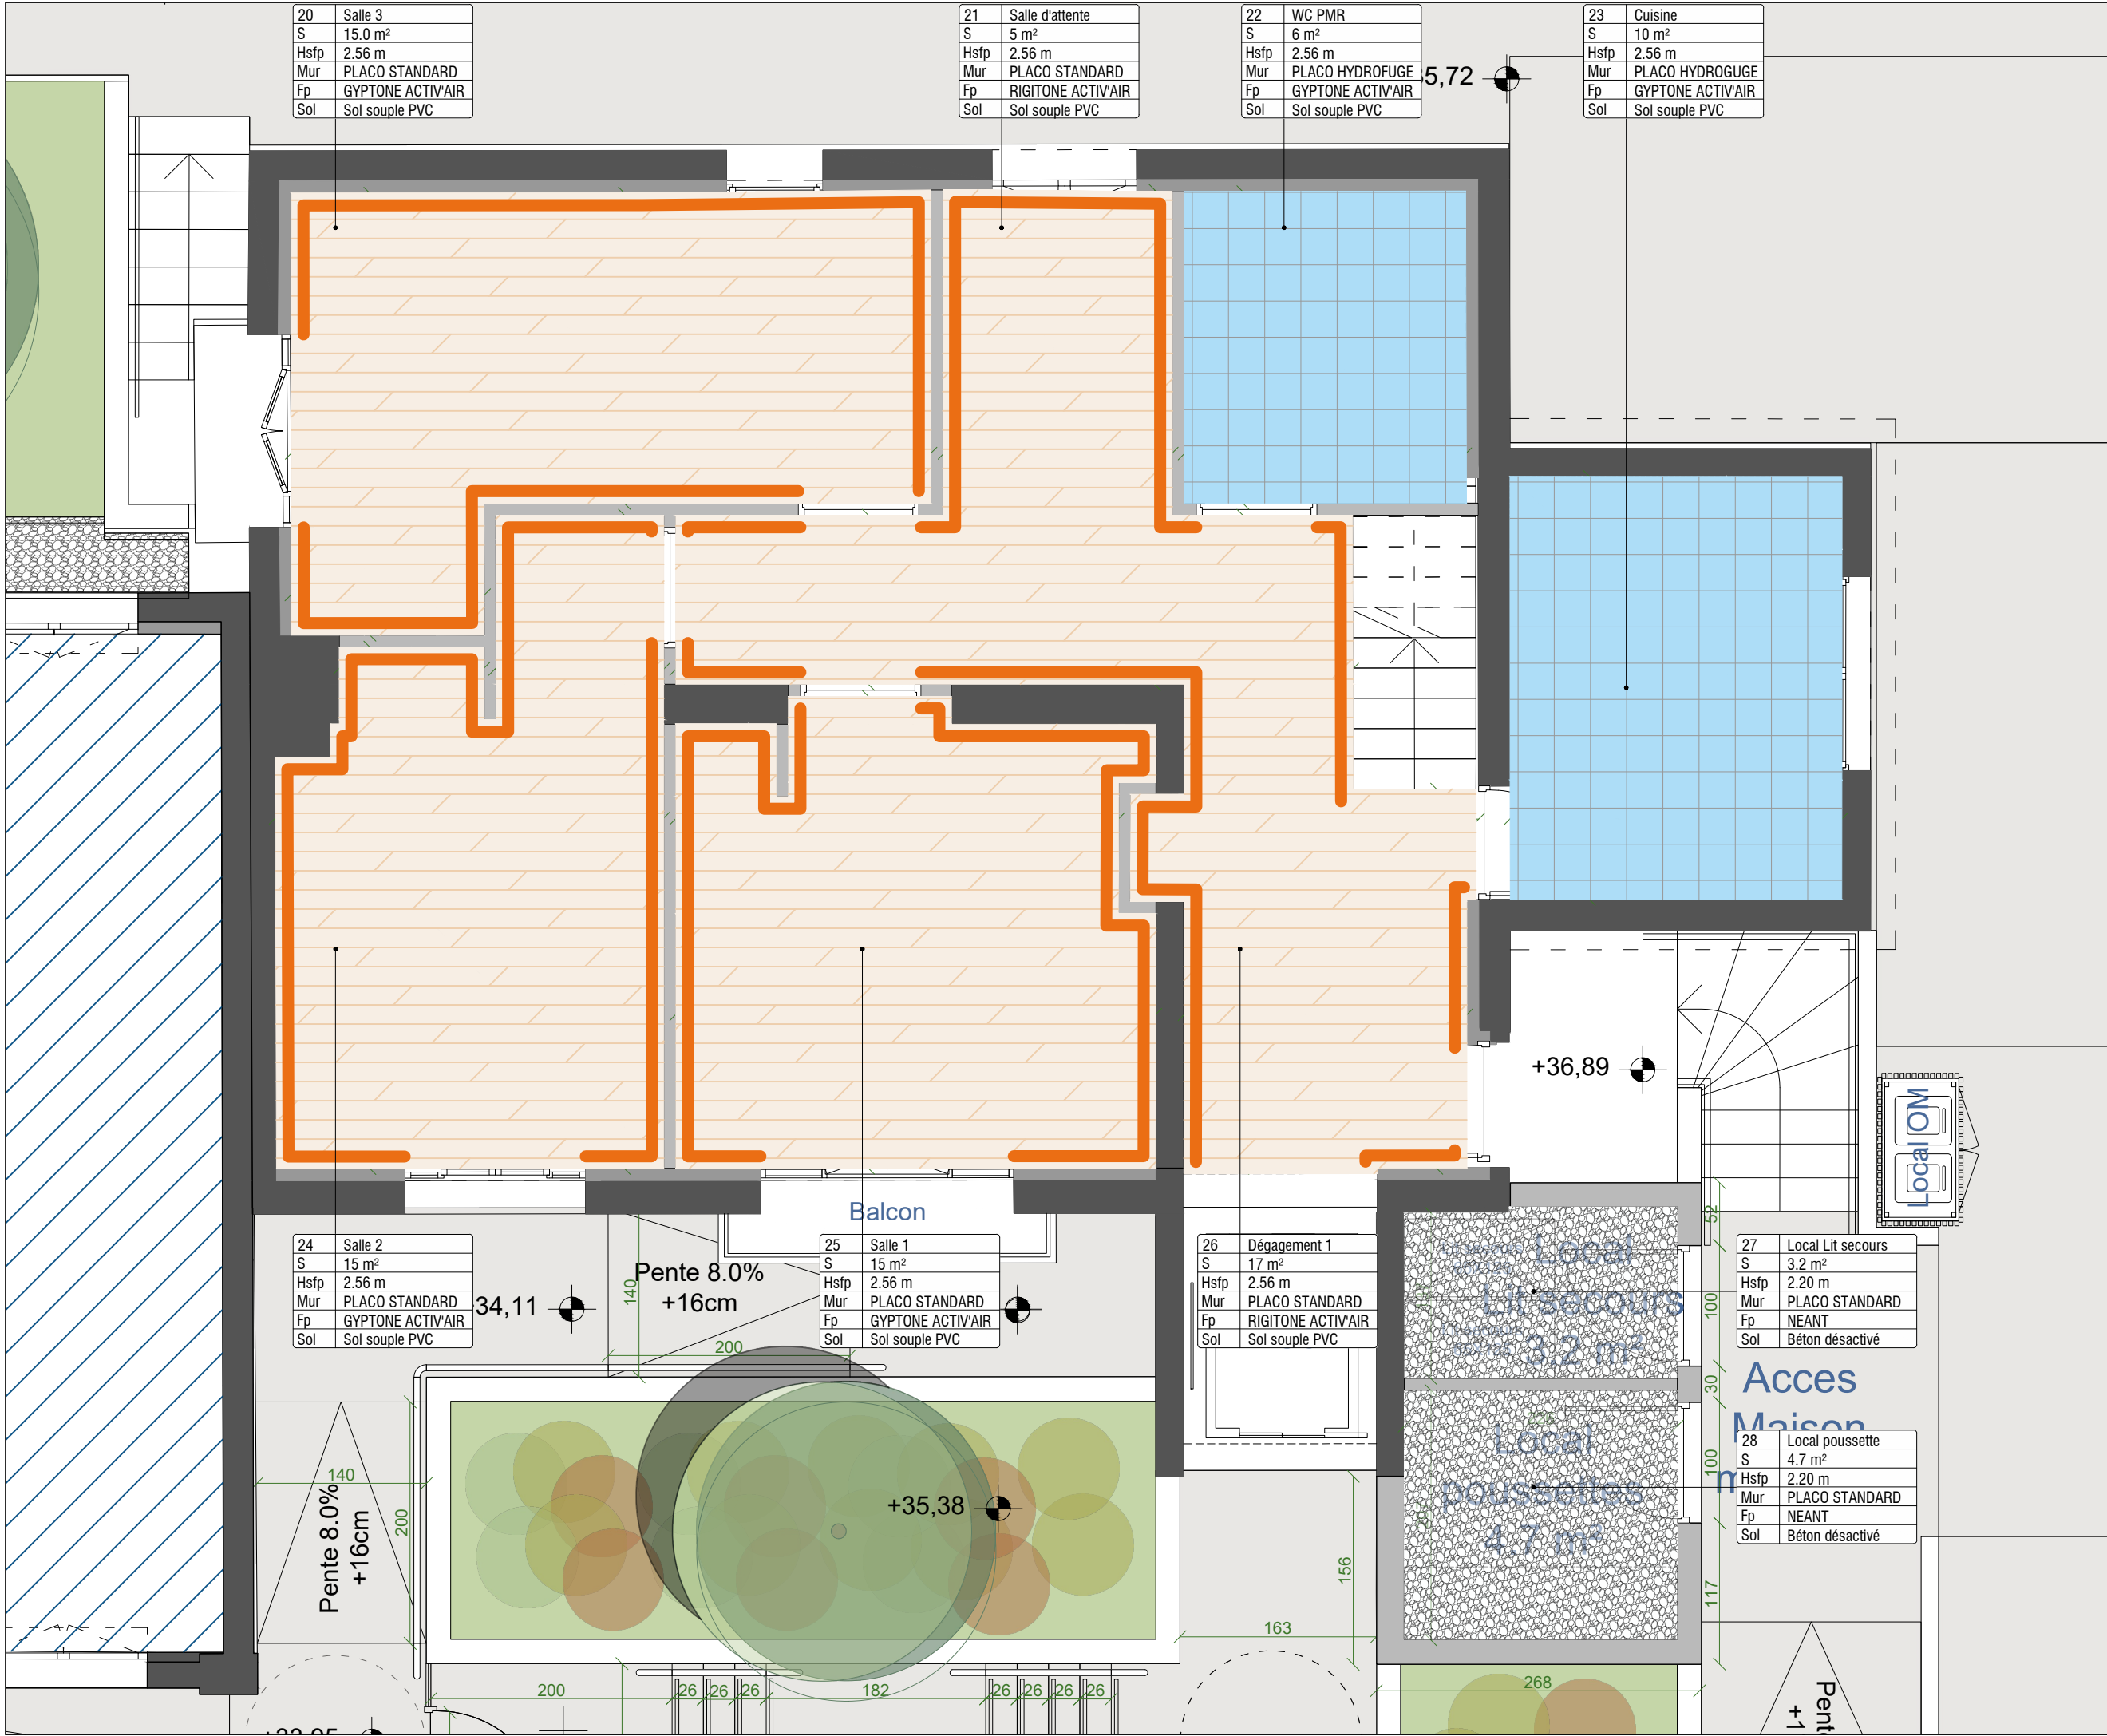

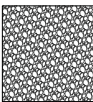
CREATION D'UN MULTI-ACCUEIL ET D'UNE MAISON MEDICALE 78400 CHATOU			
MOA	SARL LPC YVELINES 15 Rue de l'Orient78000 VERSAILLES		
MOE	NAHK ARCHITECTURE 24 Rue Yves Toudic, 75010 Paris		
NOM DU DOCUMENT			
REVETEMENTS DE SOL SECTEUR 1			
PHASE	PRO.DCE	ECH.	1/50
INDICE	1.1	DATE	04/07/2023
MODIFICATIONS			
INDICE	DATE	OBJET	
1.1	04/07/2023	Diffusion initiale	
LOT SOL SOUPLE / SOL DUR / PLINTHE			
 • SOL SOUPLE PVC EN LAMES Ref. Amtico Click Smart White C			
 • SOL EN CARRELAGE TYPE GRES CERAME R9 MIN			
 • PLINTHE EN BOIS			
 • SOL BETON DESACTIVE			

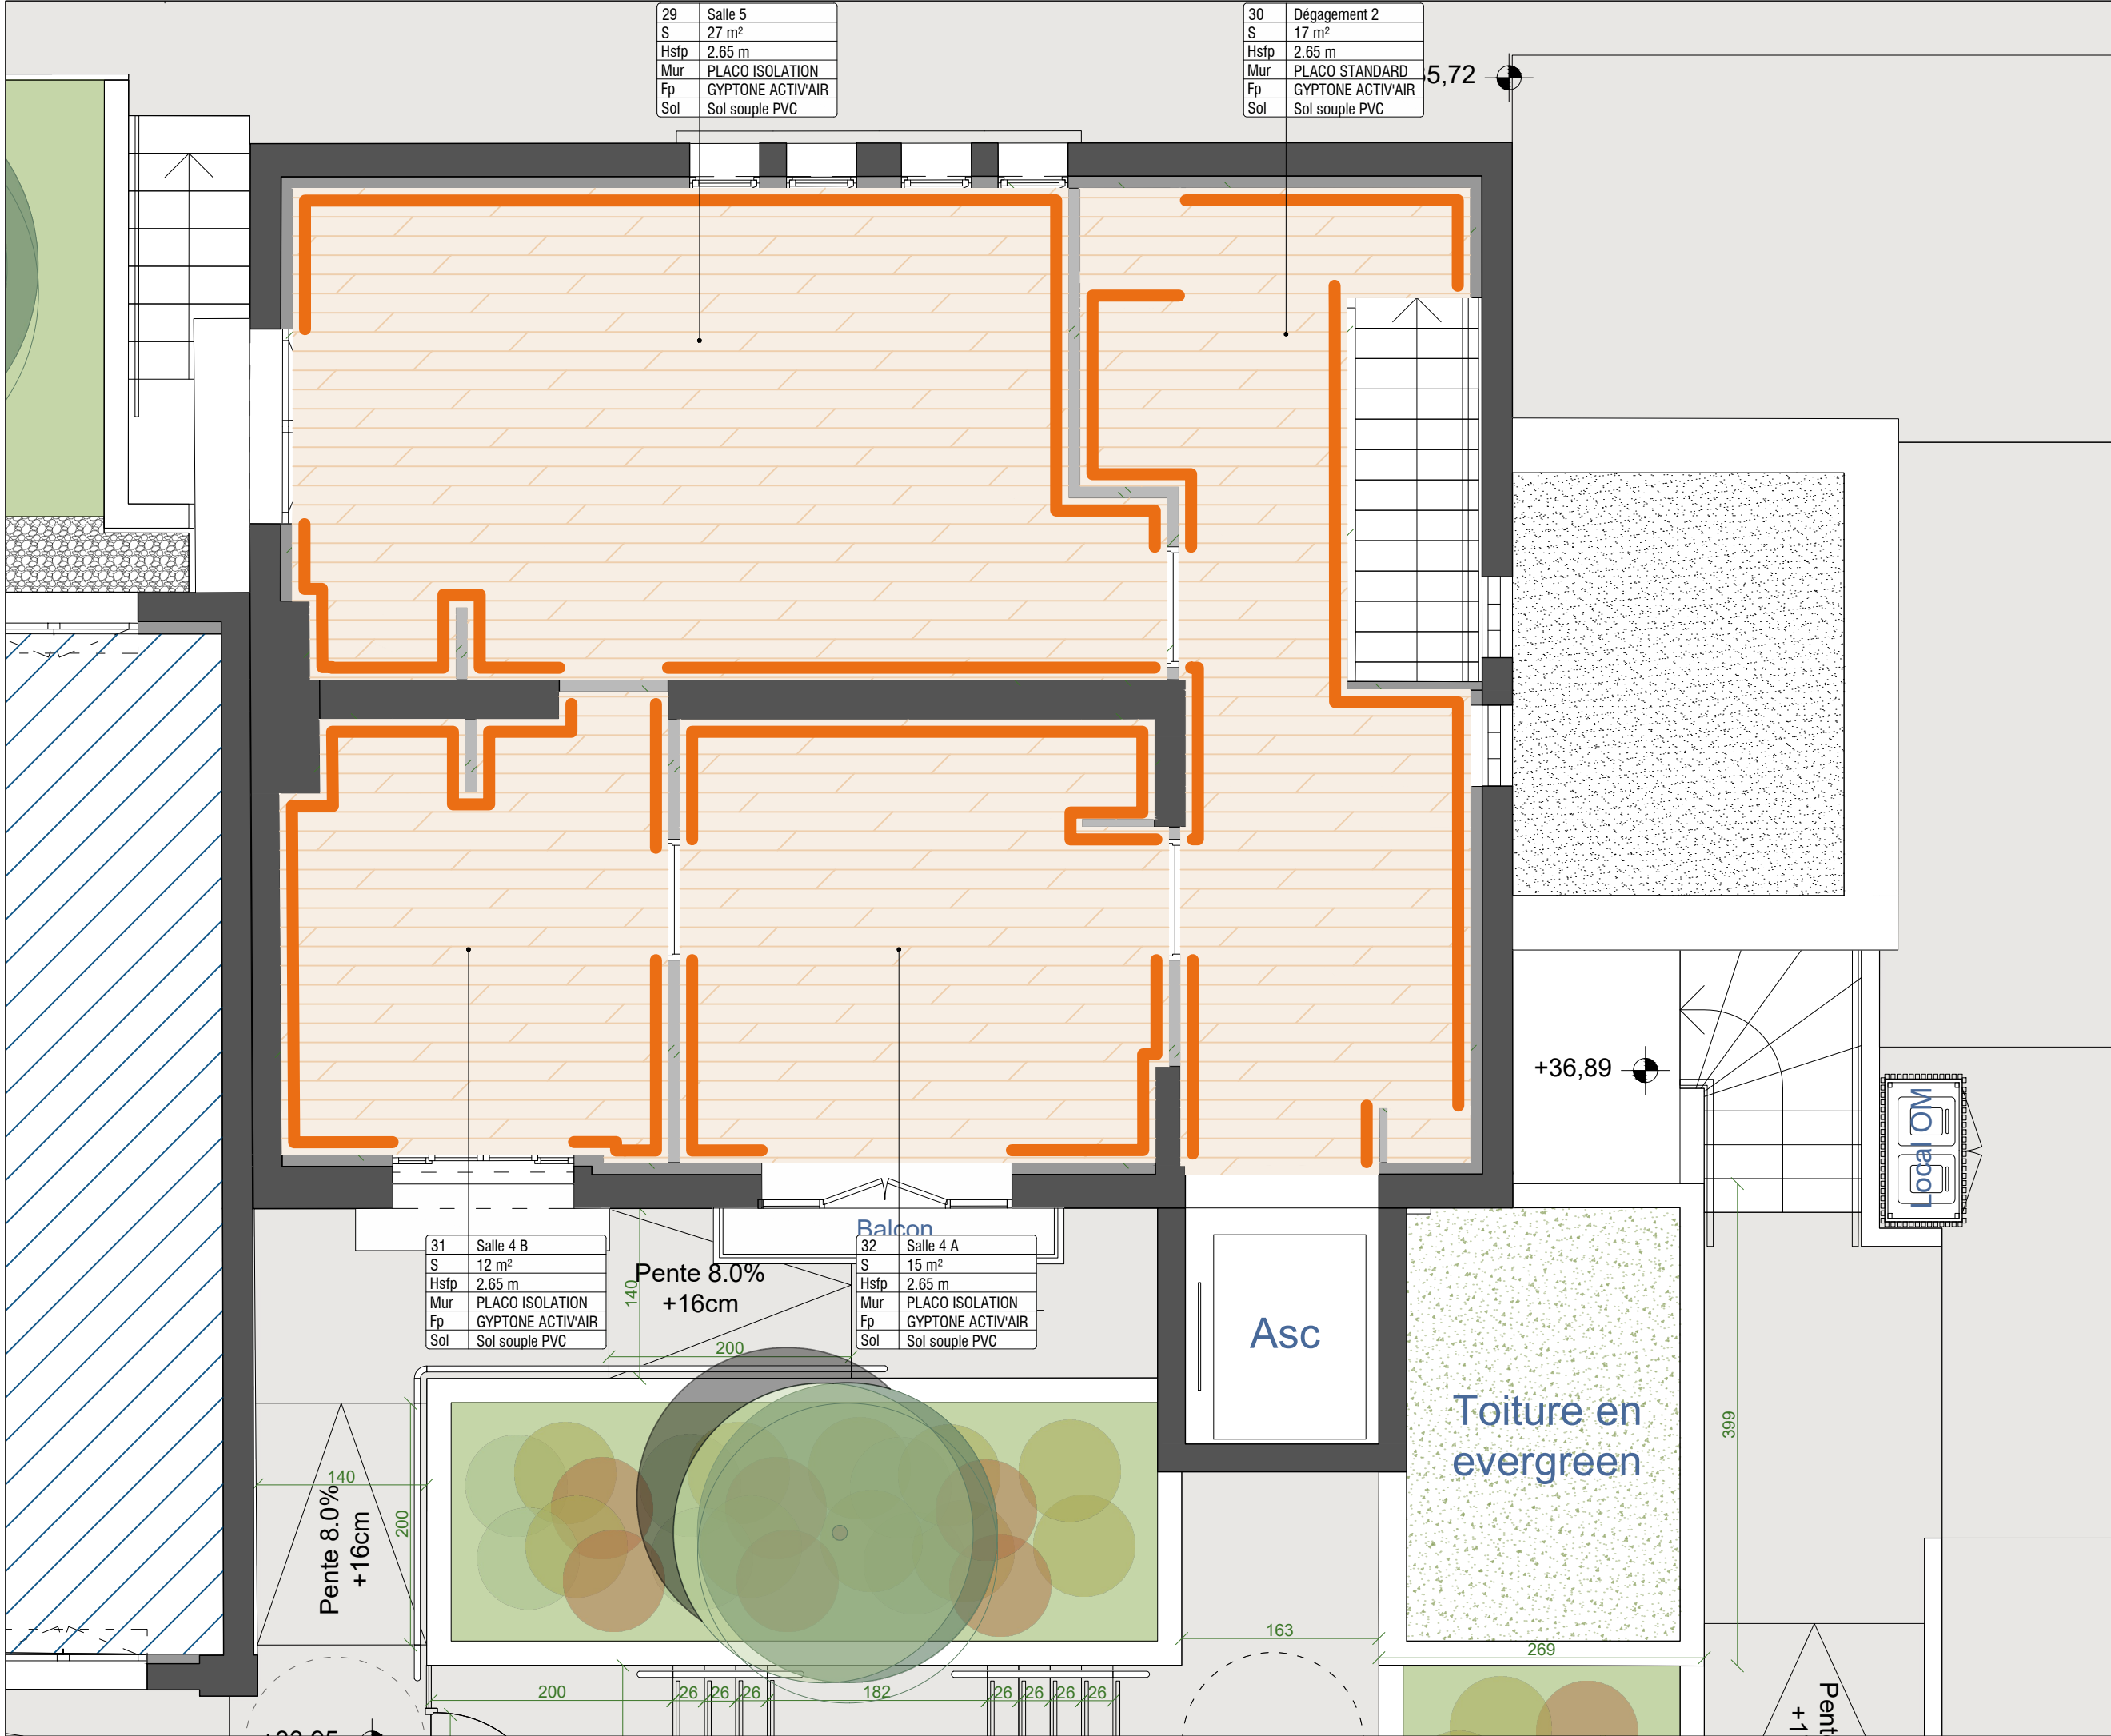

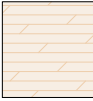CREATION D'UN MULTI-ACCUEIL ET D'UNE MAISON MEDICALE 78400 CHATOU			
MOA	SARL LPC YVELINES 15 Rue de l'Orient78000 VERSAILLES		
MOE	NAHK ARCHITECTURE 24 Rue Yves Toudic, 75010 Paris		
NOM DU DOCUMENT			
REVETEMENTS DE SOL SECTEUR 2			
PHASE	PRO.DCE	ECH.	1/50
INDICE	1.1	DATE	04/07/2023
MODIFICATIONS			
INDICE	DATE	OBJET	
1.1	04/07/2023	Diffusion initiale	
LOT SOL SOUPLE / SOL DUR / PLINTHE  • SOL SOUPLE PVC EN LAMES Ref. Amtico Click Smart White C  • SOL EN CARRELAGE TYPE GRES CERAME R9 MIN  • PLINTHE EN BOIS  • SOL BETON DESACTIVE			




CREATION D'UN MULTI-ACCUEIL ET D'UNE MAISON MEDICALE 78400 CHATOU			
MOA	SARL LPC YVELINES 15 Rue de l'Orient78000 VERSAILLES		
MOE	NAHK ARCHITECTURE 24 Rue Yves Toudic, 75010 Paris		
NOM DU DOCUMENT			
DOUBLAGE MURAL SECTEUR 2			
PHASE	PRO.DCE	ECH.	1/50
INDICE	1.1	DATE	04/07/2023
MODIFICATIONS			
INDICE	DATE	OBJET	
1.1	04/07/2023	Diffusion initiale	
DOUBLAGE MURAL • PLACOSTIL STANDART CLOISON EP 10 cm • PLACOSTIL HYDROFUGE CLOISON EP 10 cm • PLACOFLAM COUPLE HYDROFUGE CLOISON EP 10 cm • PLACOFLAM CLOISON EP 10 cm • PLACOSTIL ISOLATION PHONIQUE CLOISON EP 10 cm			

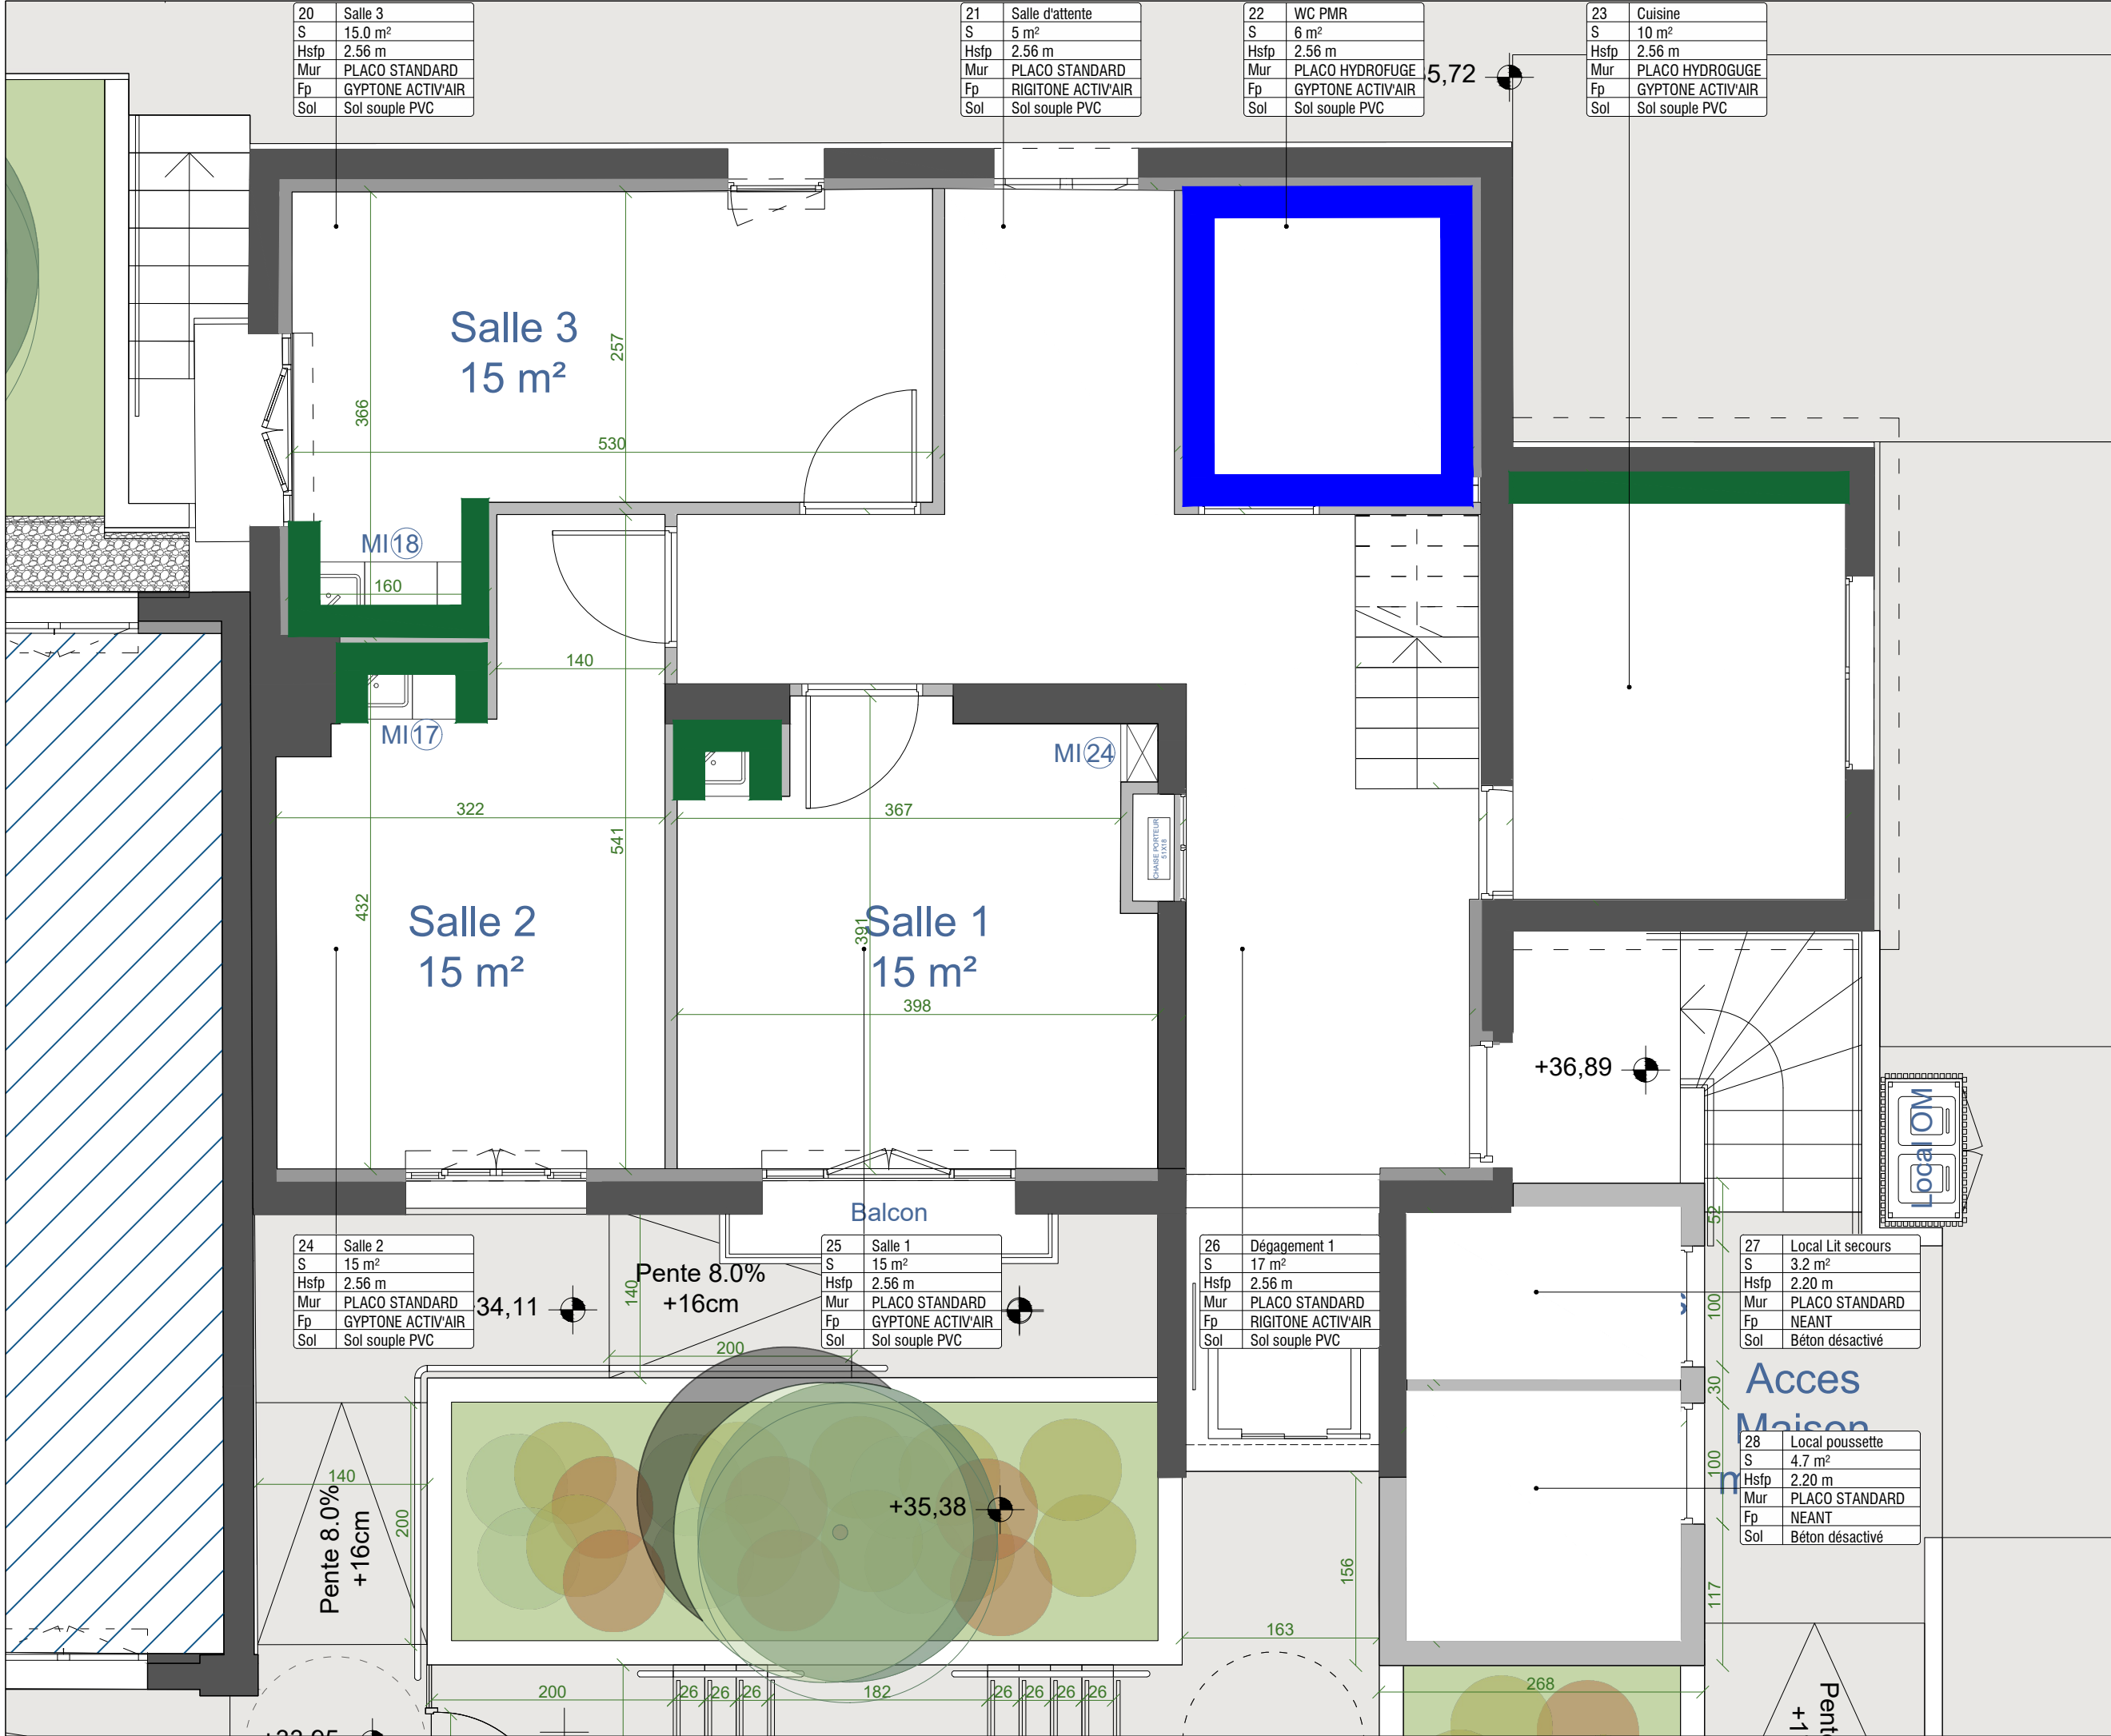


CREATION D'UN MULTI-ACCUEIL ET D'UNE MAISON MEDICALE 78400 CHATOU			
MOA	SARL LPC YVELINES 15 Rue de l'Orient78000 VERSAILLES		
MOE	NAHK ARCHITECTURE 24 Rue Yves Toudic, 75010 Paris		
NOM DU DOCUMENT			
REVETEMENT MURAL SECTEUR 1			
PHASE	PRO.DCE	ECH.	1/50
INDICE	1.1	DATE	04/07/2023
MODIFICATIONS			
INDICE	DATE	OBJET	
1.1	04/07/2023	Diffusion initiale	
FAIENCE • FAIENCE TOUTE HAUTEUR SOIT JUSQU'A 250 cm • FAIENCE JUSQU'A 120 CM • FAIENCE PLAN DE TRAVAIL DE 50 cm DE HATEUR PROTECTION MURALE • PROTECTION D'ANGLE • LISSE DE PROTECTION MURALE			



CREATION D'UN MULTI-ACCUEIL ET D'UNE MAISON MEDICALE 78400 CHATOU			
MOA	SARL LPC YVELINES 15 Rue de l'Orient78000 VERSAILLES		
MOE	NAHK ARCHITECTURE 24 Rue Yves Toudic, 75010 Paris		
NOM DU DOCUMENT			
REVETEMENT MURAL SECTEUR 2			
PHASE	PRO.DCE	ECH.	1/50
INDICE	1.1	DATE	04/07/2023
MODIFICATIONS			
INDICE	DATE	OBJET	
1.1	04/07/2023	Diffusion initiale	
FAIENCE • FAIENCE TOUTE HAUTEUR SOIT JUSQU'A 250 cm • FAIENCE JUSQU'A 120 CM • FAIENCE PLAN DE TRAVAIL DE 50 cm DE HATEUR PROTECTION MURALE • PROTECTION D'ANGLE • LISSE DE PROTECTION MURALE			

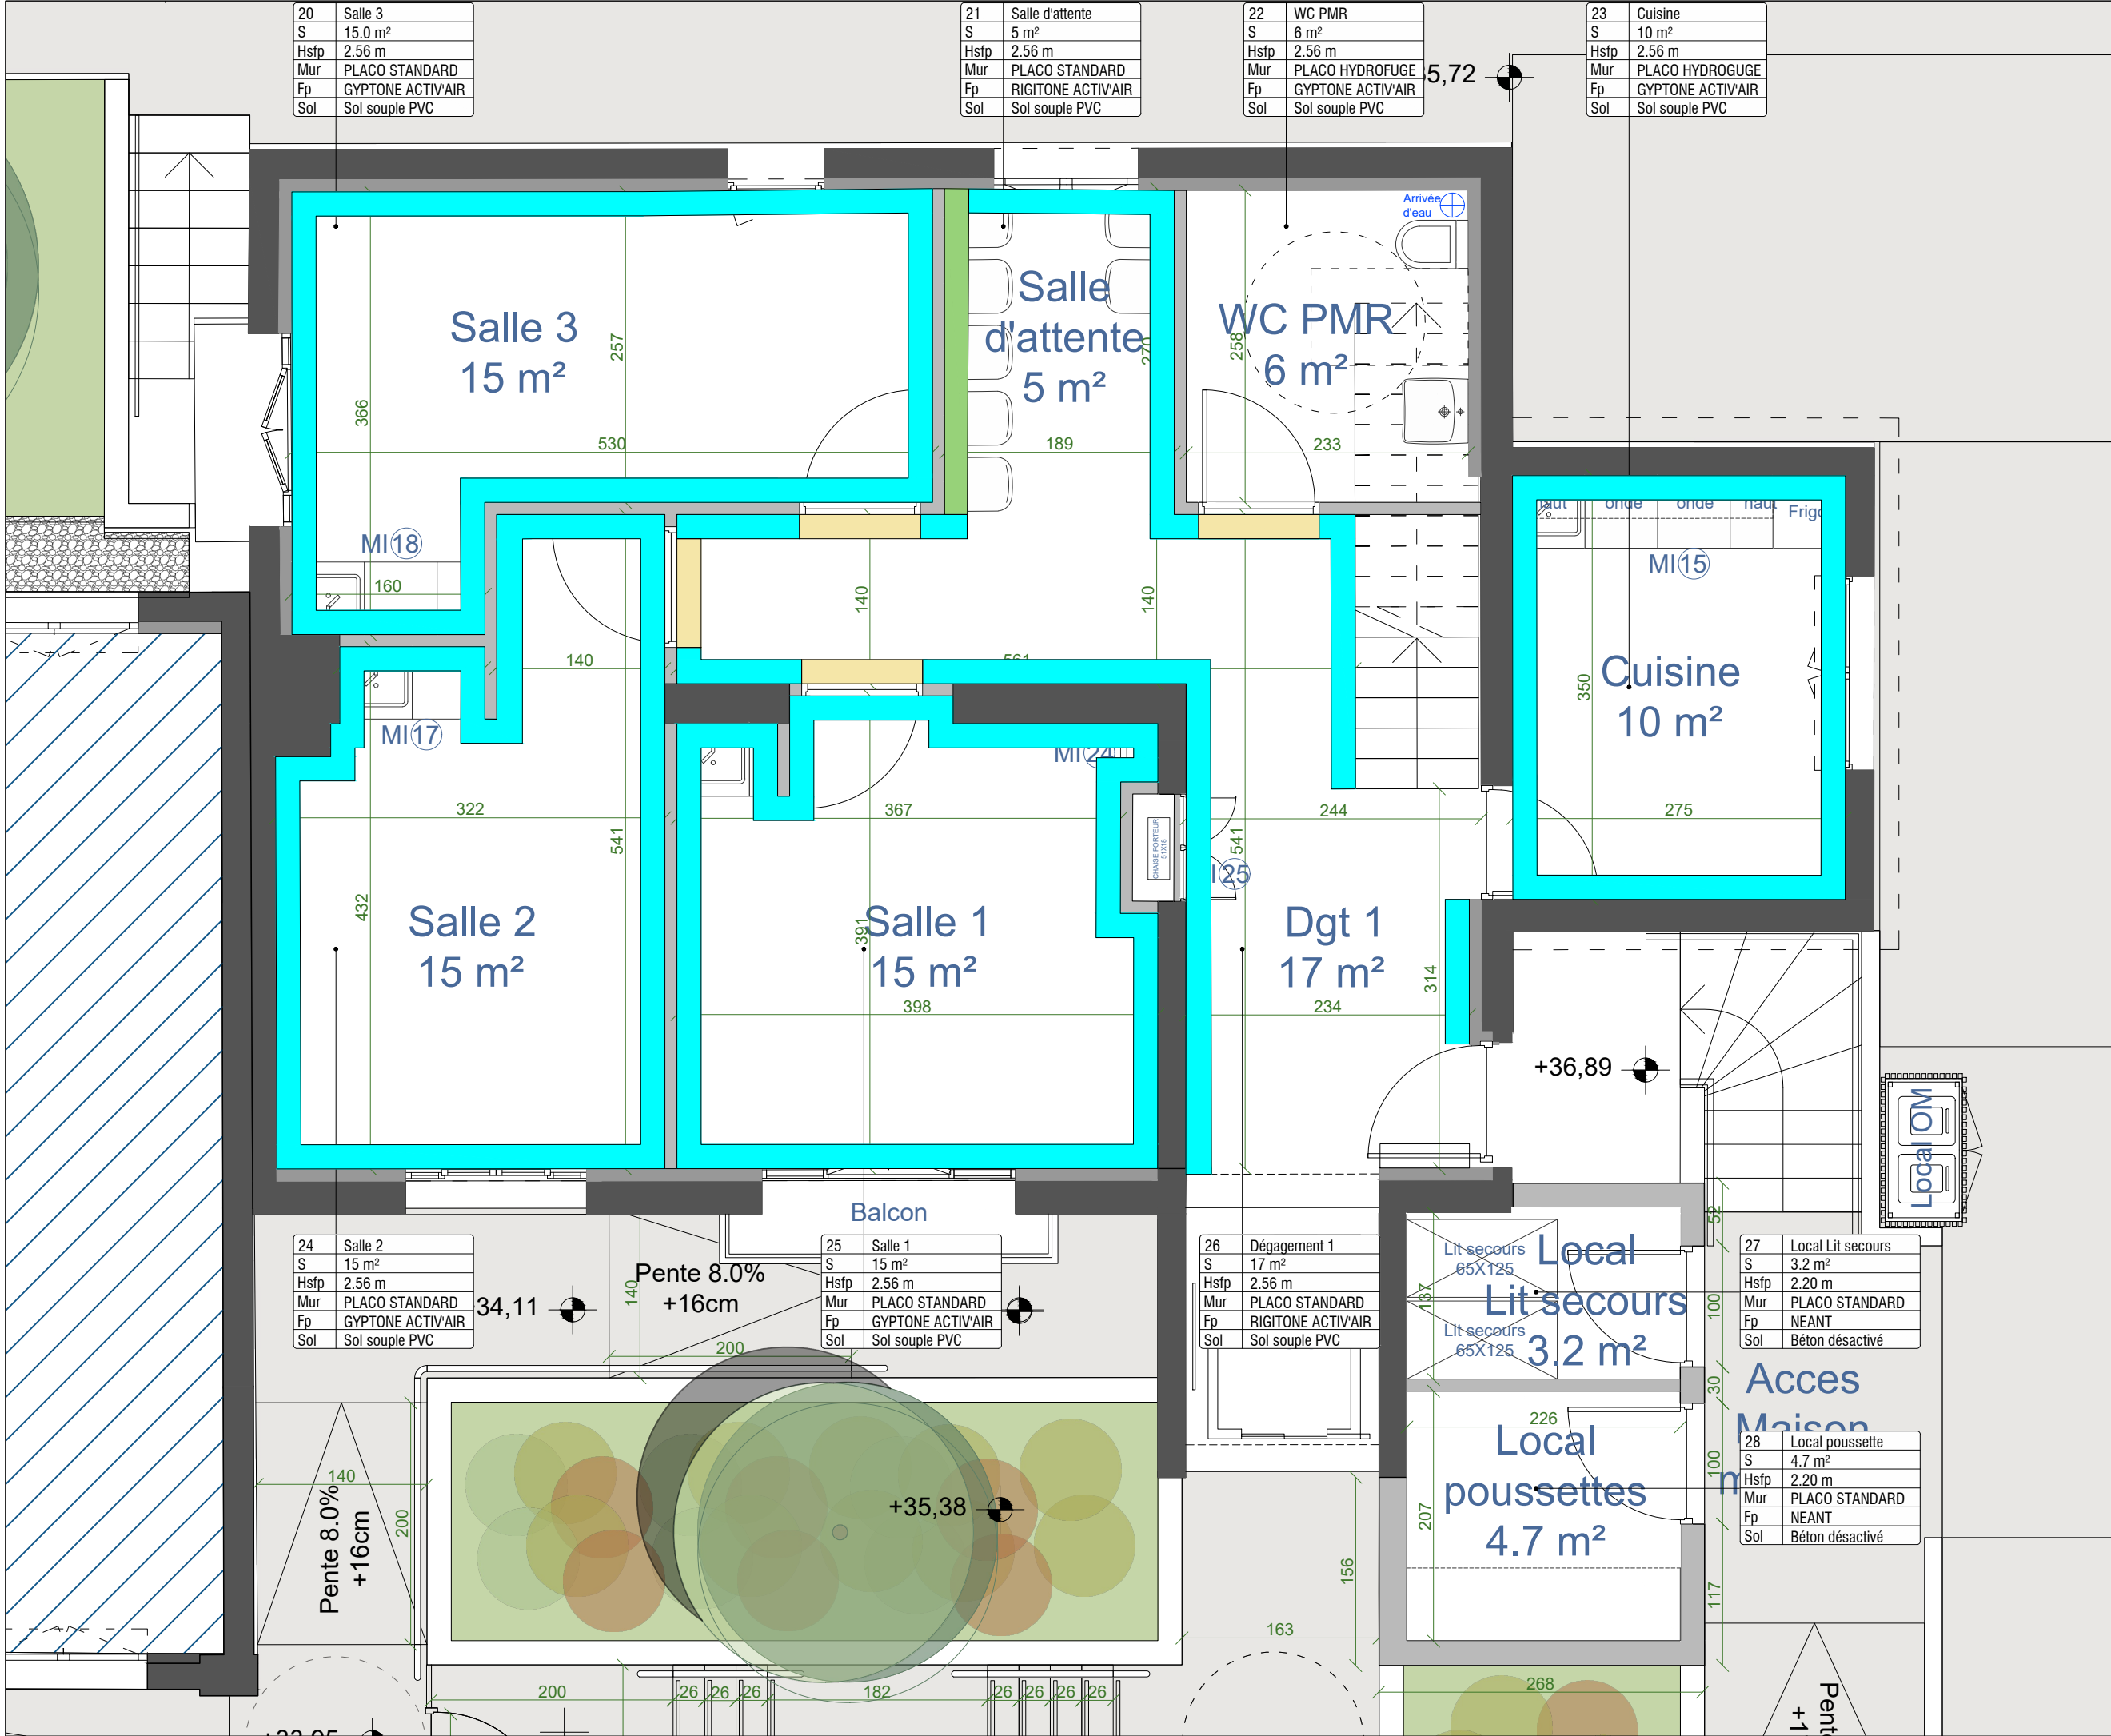

CREATION D'UN MULTI-ACCUEIL ET D'UNE MAISON MEDICALE 78400 CHATOU			
MOA	SARL LPC YVELINES 15 Rue de l'Orient78000 VERSAILLES		
MOE	NAHK ARCHITECTURE 24 Rue Yves Toudic, 75010 Paris		
NOM DU DOCUMENT			
PAPIER PEINT / PEINTURE SECTEUR 1			
PHASE	PRO.DCE	ECH.	1/50
INDICE	1.1	DATE	04/07/2023
MODIFICATIONS			
INDICE DATE		OBJET	
1.1	04/07/2023	Diffusion initiale	
PAPIER PEINT / PEINTURE			
• PEINTURE TOUTE HAUTEUR SOIT JUSQU'A 250 cm Ref. Champoussin CH2 0022			
• PEINTURE TOUTE HAUTEUR SOIT JUSQU'A 250 cm Ref.Vert pâle RAL 6021			
• PEINTURE TOUTE HAUTEUR SOIT JUSQU'A 250 cm Ref.Ivoire RAL 1015			

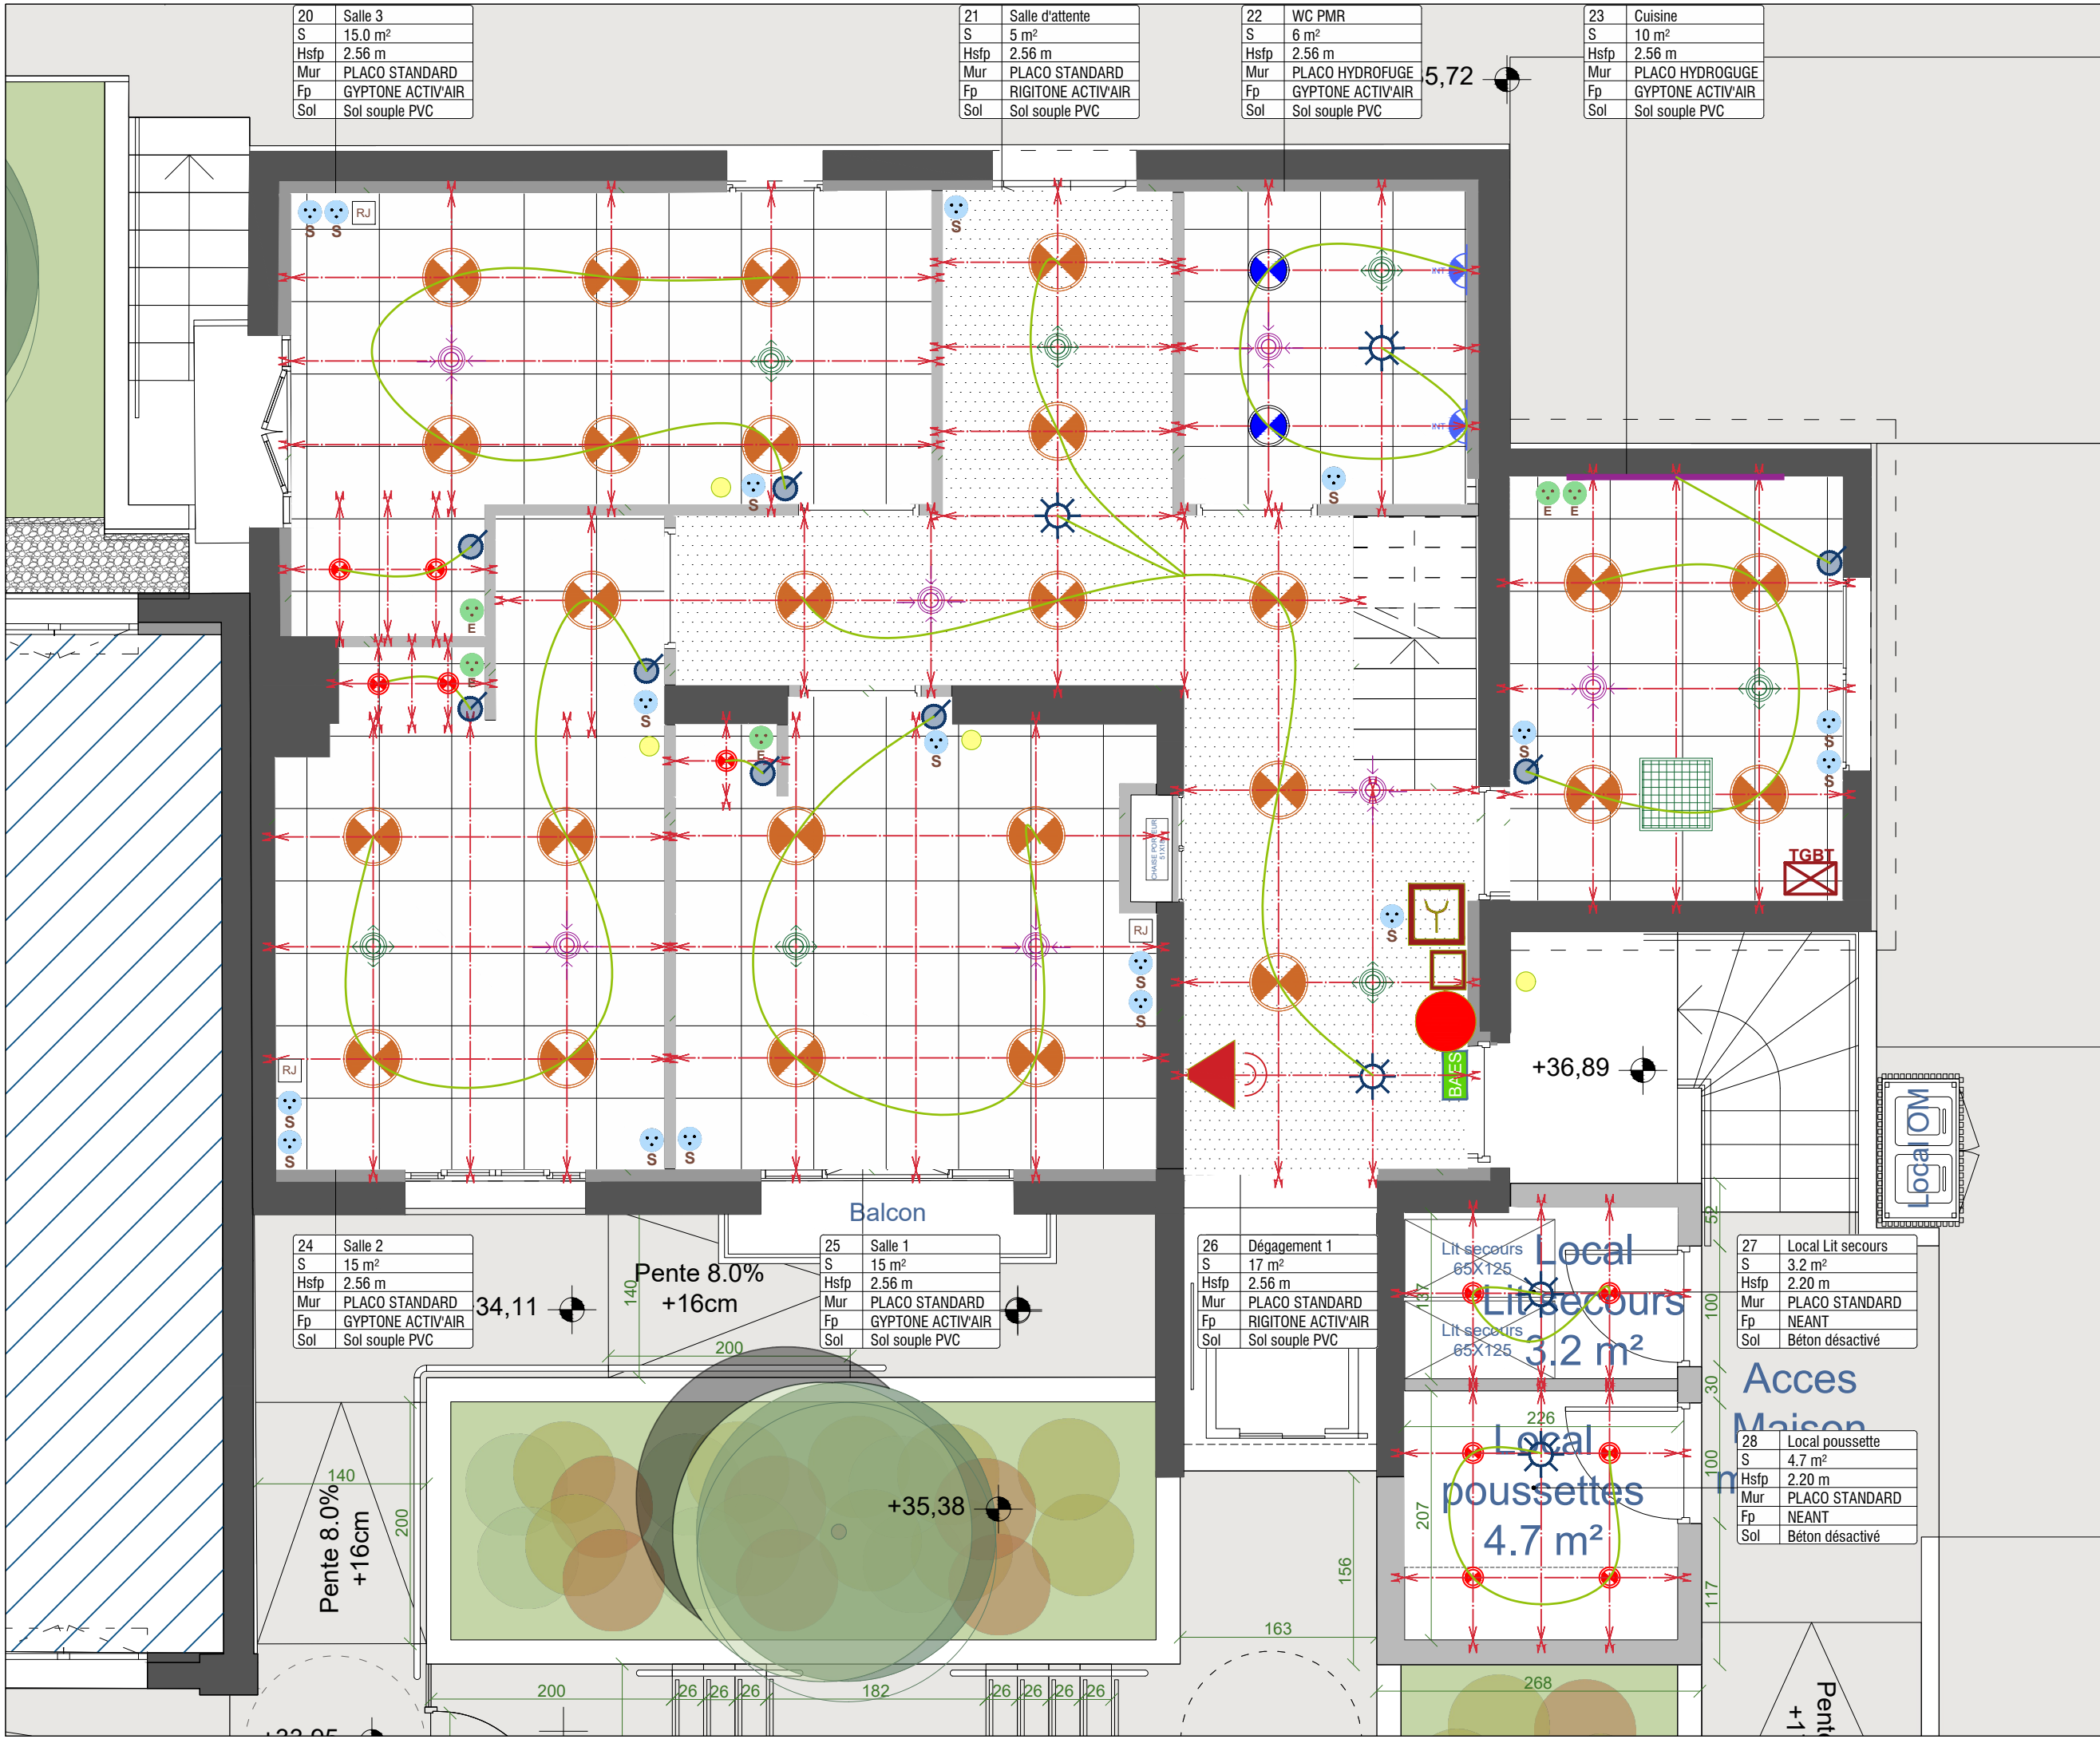

CREATION D'UN MULTI-ACCUEIL ET D'UNE MAISON MEDICALE
78400 CHATOU

MOA

SARL LPC YVELINES
15 Rue de l'Orient78000 VERSAILLES

MOE

NAHK ARCHITECTURE
24 Rue Yves Toudic, 75010 Paris

NOM DU DOCUMENT

ELECTRICITE
SECTEUR 1

PHASE

PRO.DCE

ECH.

1/50

INDICE

1.1

DATE

04/07/2023

MODIFICATIONS

INDICE

DATE

OBJET

1.1

04/07/2023

Diffusion initiale

ELECTRICITE

TYPE 1 - PLAFONNIER SLV
MEDO 60 REF. #1000726

TYPE 1 - DOWNLIGHTS TIGA 3
RD DIAM 240

TYPE 2 - SPOT IN HOUSE LED
UP007 DIAM 85

TYPE 3 - DOWNLIGHTS TIGA 1
RD DIAM 170

TYPE 4 - APPLIQUE MURALE
DELTALIGHT TOPIX WW

TYPE 5 - REGLETTE MURALE
EXTRA-PLATE

TYPE 5 - APPLIQUE
SLV QUADRASYL

INTERRUPTEUR SIMPLE

INTERRUPTEUR VA-ET-VIENT

VARIATEUR EN DALI

DETECTEUR DE PRESENCE
AVEC MINUTERIE

PRISE ELECTRIQUE
STANDARD H 130 CM DU SOL

PRISE ETANCHE ENCASTREE
20 CM DU PLAN DE TRAVAIL

ALIMENTATION APPAREIL

PRISE RJ45

BAES

CENTRALE D'ALARME INCENDIE

DIFFUSEUR SONORE

DIFFUSEUR LUMINEUX

DECLENCHEUR D'ALARME MANUEL

DEVEROUILLEGE PORTE

ARRET D'URGENCE ELECTRICITE
ET VENTILATION

EXTINCTEUR

VISIOPHONE AVEC VENTOUSE

DIGICODE

SERRURE A CODE

SONDE DE QUALITE DE L'AIR

TGBT

CTA AU PLAFOND

BALLON



CREATION D'UN MULTI-ACCUEIL ET D'UNE MAISON MEDICALE
78400 CHATOU

MOA

SARL LPC YVELINES
15 Rue de l'Orient78000 VERSAILLES

MOE

NAHK ARCHITECTURE
24 Rue Yves Toudic, 75010 Paris

NOM DU DOCUMENT

ELECTRICITE
SECTEUR 2

PHASE

PRO.DCE

ECH.

1/50

INDICE

1.1

DATE

04/07/2023

MODIFICATIONS

INDICE DATE OBJET

1.1 04/07/2023 Diffusion initiale

ELECTRICITE

TYPE 1 - PLAFONNIER SLV
MEDO 60 REF. #1000726

TYPE 1 - DOWNLIGHTS TIGA 3
RD DIAM 240

TYPE 2 - SPOT IN HOUSE LED
UP007 DIAM 85

TYPE 3 - DOWNLIGHTS TIGA 1
RD DIAM 170

TYPE 4 - APPLIQUE MURALE
DELTALIGHT TOPIX WW

TYPE 5 - REGLETTE MURALE
EXTRA-PLATE

TYPE 5 - APPLIQUE
SLV QUADRASYL

INTERRUPTEUR SIMPLE

INTERRUPTEUR VA-ET-VIENT

VARIATEUR EN DALI

DETECTEUR DE PRESENCE
AVEC MINUTERIE

PRISE ELECTRIQUE
STANDARD H 130 CM DU SOL

PRISE ETANCHE ENCASTREE
20 CM DU PLAN DE TRAVAIL

ALIMENTATION APPAREIL

PRISE RJ45

BAES

CENTRALE D'ALARME INCENDIE

DIFFUSEUR SONORE

DIFFUSEUR LUMINEUX

DECLENCHEUR D'ALARME MANUEL

DEVEROUILLAGE PORTE

ARRET D'URGENCE ELECTRICITE
ET VENTILATION

EXTINCTEUR

VISIOPHONE AVEC VENTOUSE

DIGICODE


SERRURE A CODE

SONDE DE QUALITE DE L'AIR

TGBT

CTA AU PLAFOND

BALLON

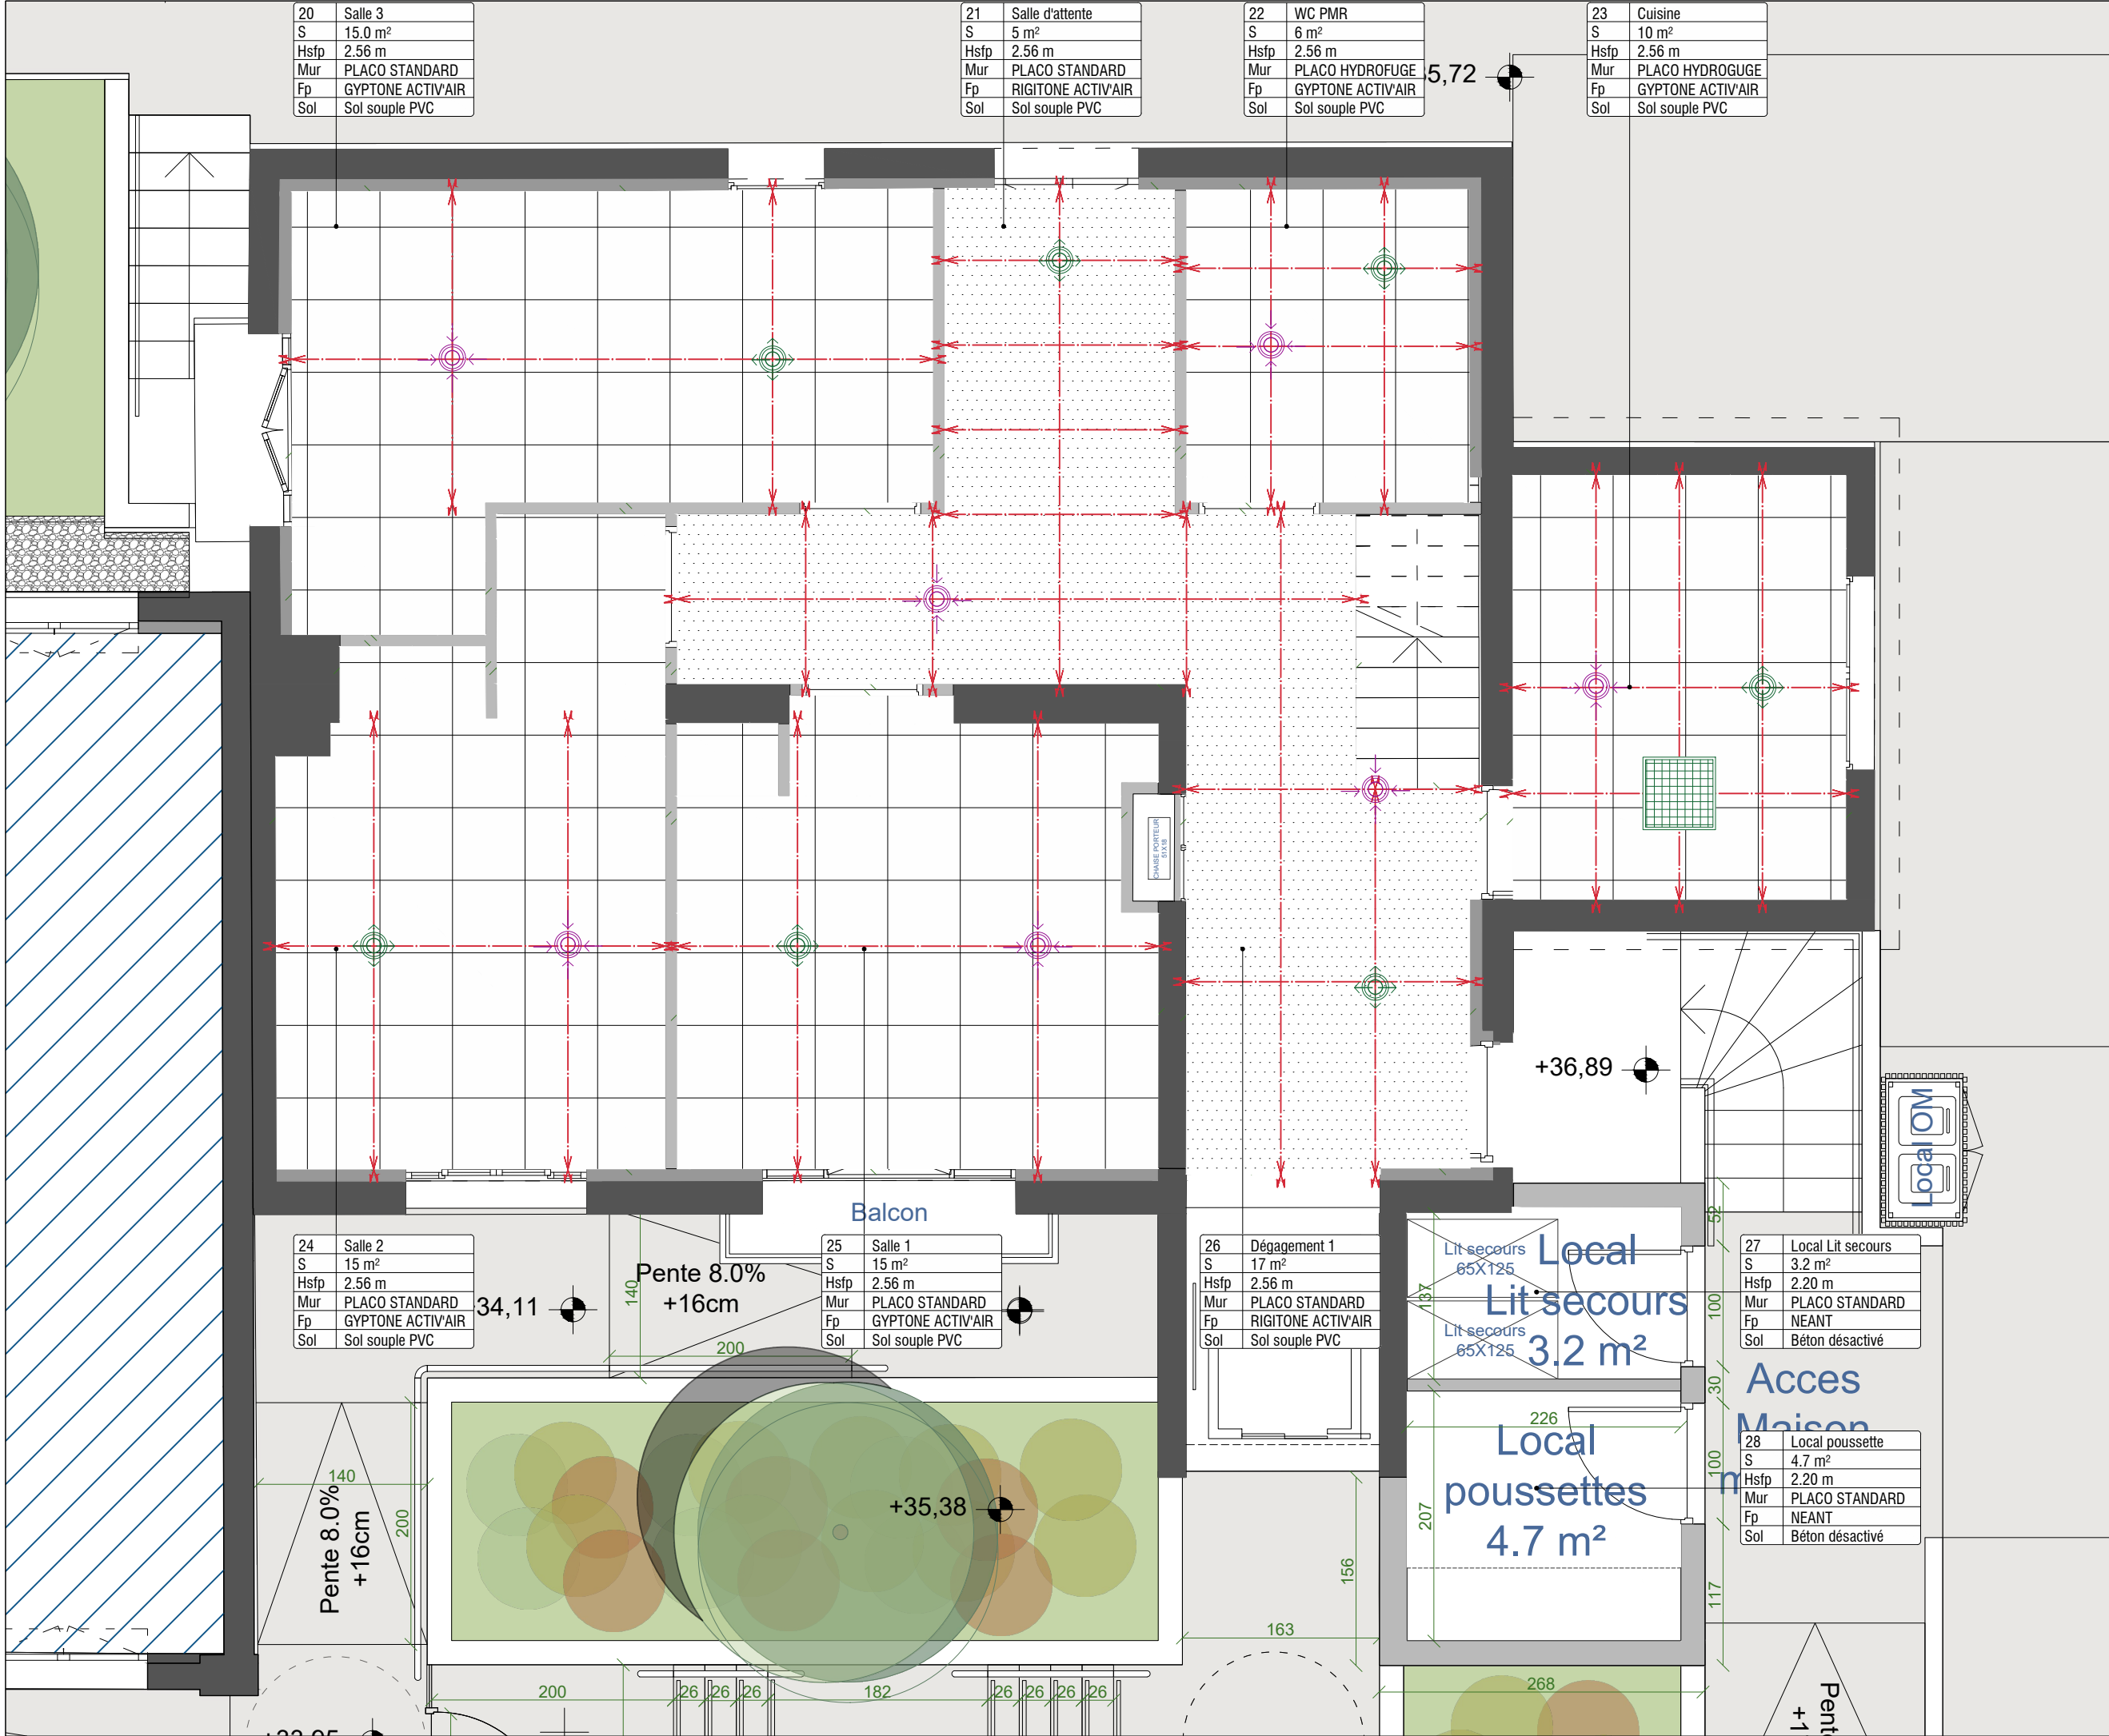

CREATION D'UN MULTI-ACCUEIL ET D'UNE MAISON MEDICALE
78400 CHATOU

MOA

SARL LPC YVELINES
15 Rue de l'Orient78000 VERSAILLES

MOE

NAHK ARCHITECTURE
24 Rue Yves Toudic, 75010 Paris

NOM DU DOCUMENT

C.V.C
SECTEUR 1

PHASE

PRO.DCE

ECH.

1/50

INDICE

1.1

DATE

04/07/2023

MODIFICATIONS

INDICE DATE OBJET

1.1 04/07/2023 Diffusion initiale

CLIMATISATION / VENTILATION

• DIFFUSEUR REGLABLE CA
60 x 60 cm SOUFFLAGE / REP


• DIFFUSEUR CIRCULAIRE
SOUFFLAGE

• DIFFUSEUR CIRCULAIRE
REPRISE


• BOUCHE D'EXTRACTION

CTA

• CTA au plafond

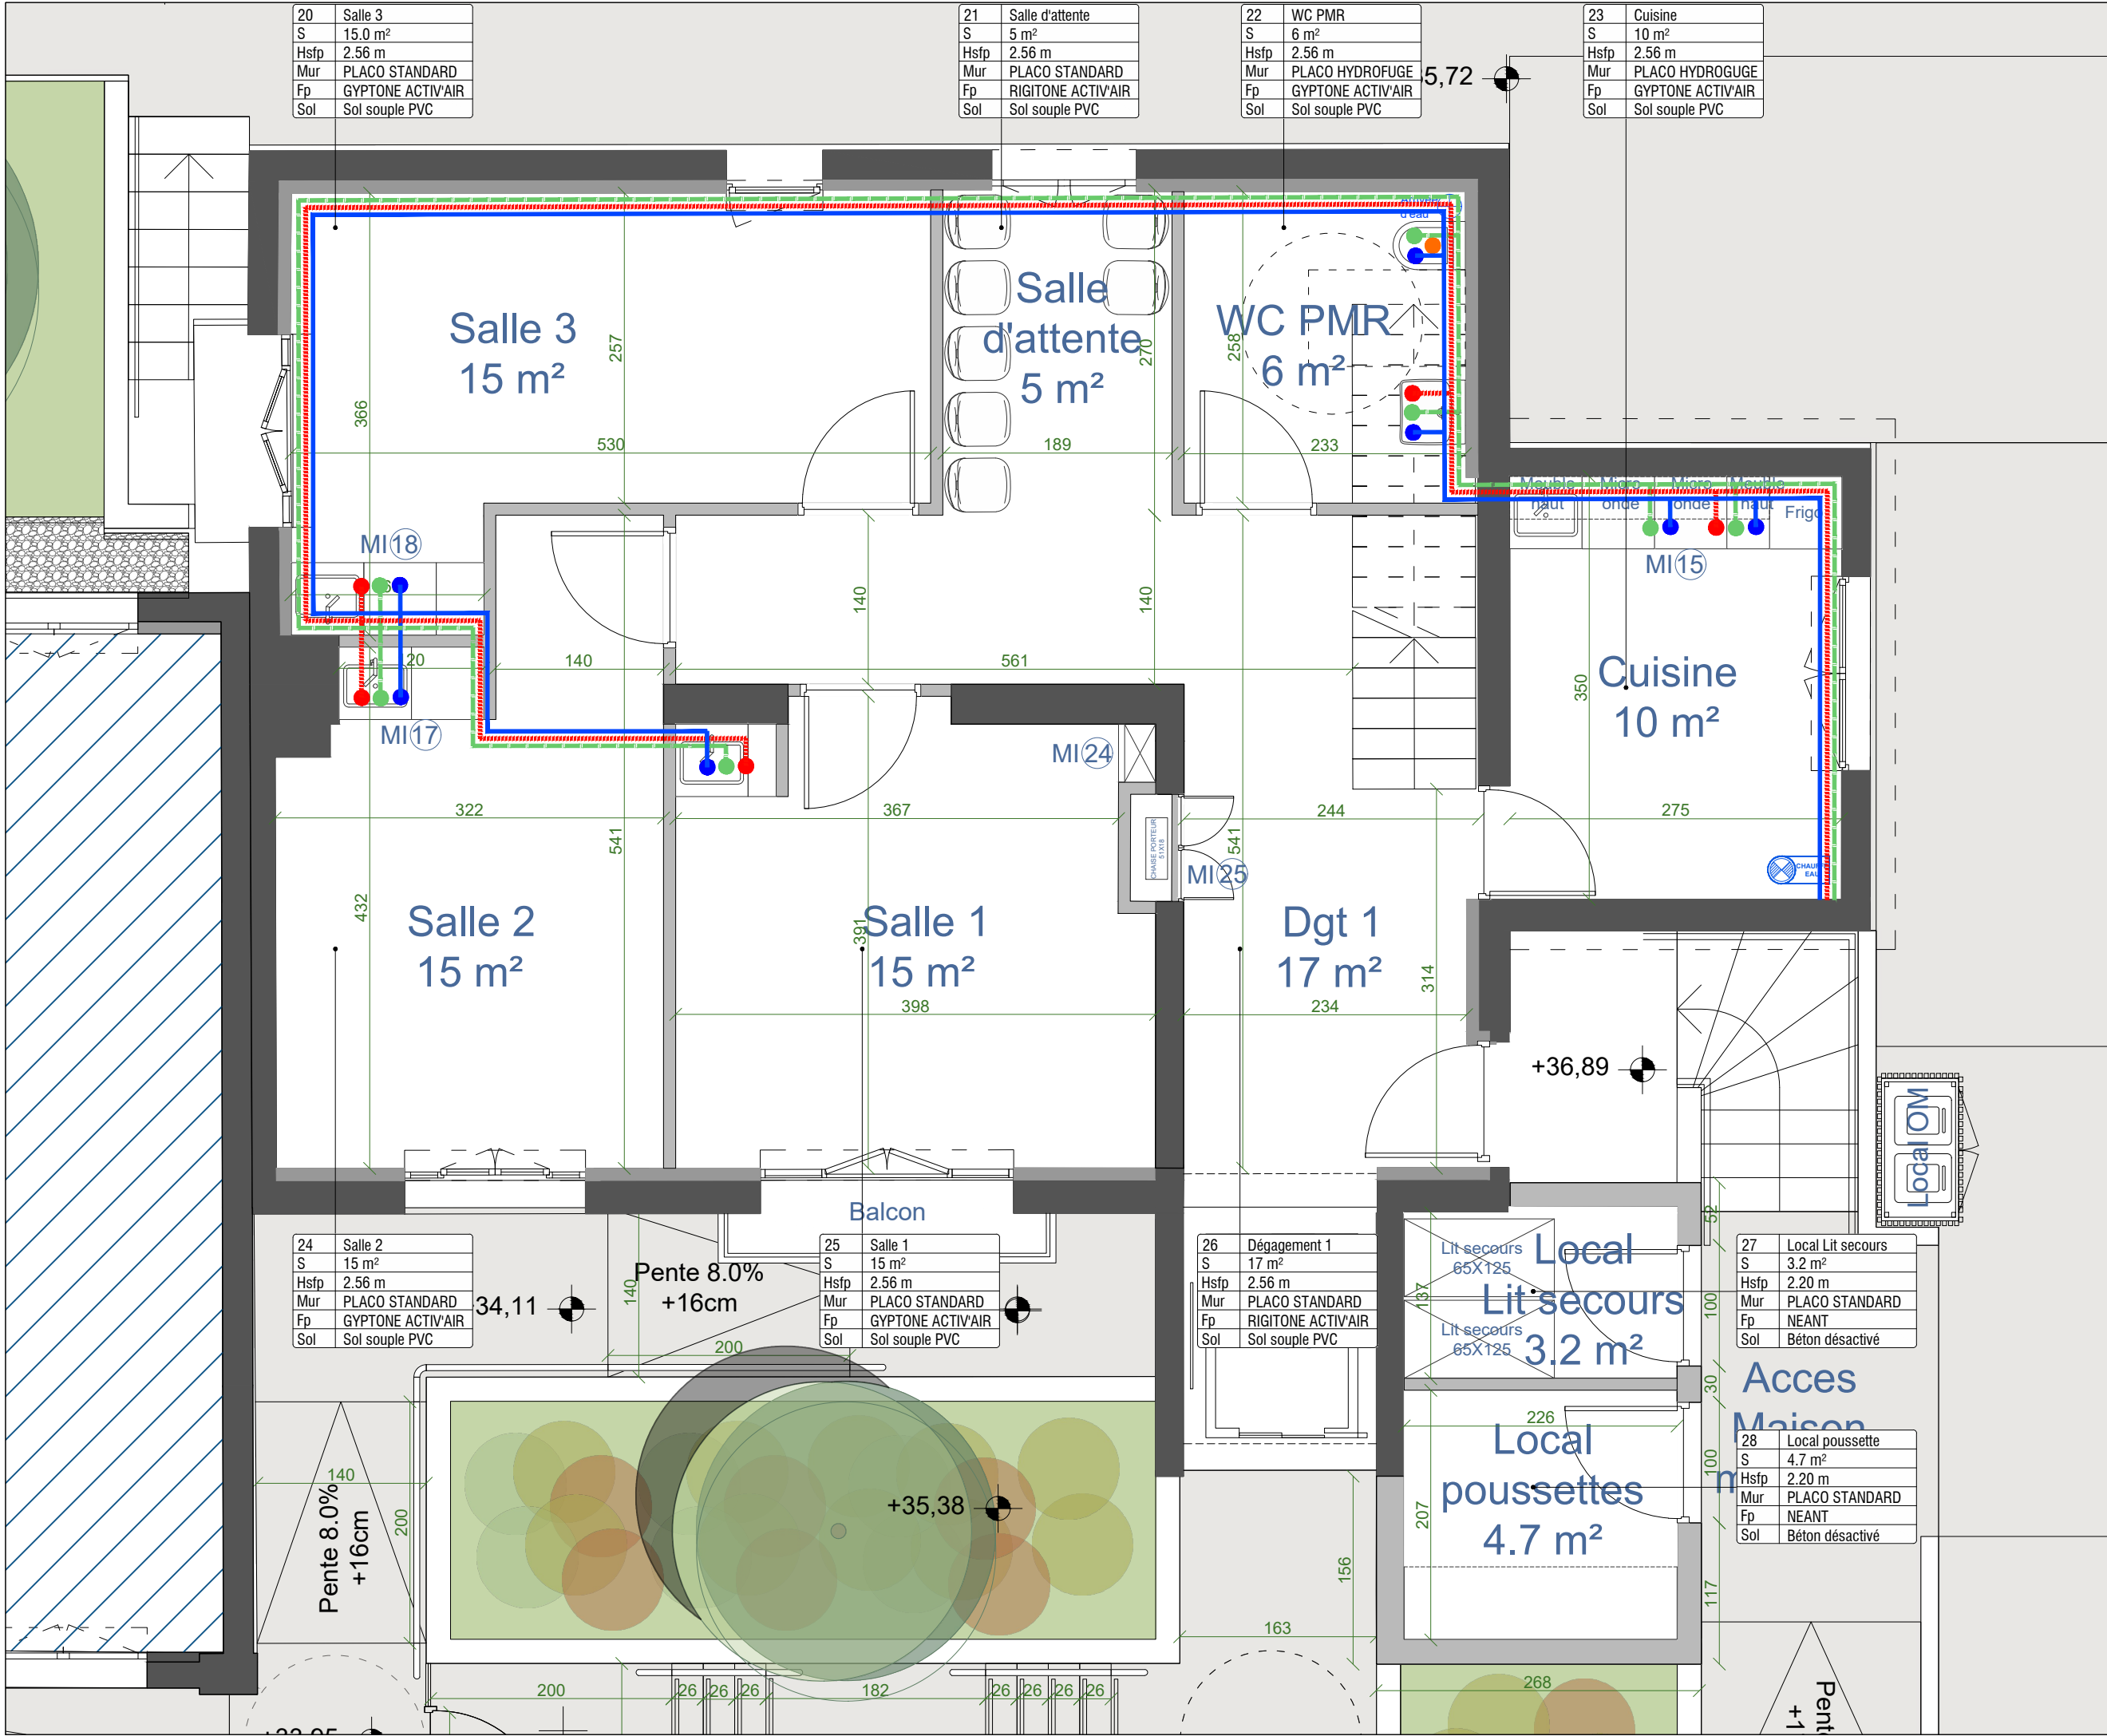

CREATION D'UN MULTI-ACCUEIL ET D'UNE MAISON MEDICALE 78400 CHATOU			
MOA	SARL LPC YVELINES 15 Rue de l'Orient78000 VERSAILLES		
MOE	NAHK ARCHITECTURE 24 Rue Yves Toudic, 75010 Paris		
NOM DU DOCUMENT			
PLOMBERIE SECTEUR 1			
PHASE	PRO.DCE	ECH.	1/50
INDICE	1.1	DATE	04/07/2023
MODIFICATIONS			
INDICE	DATE	OBJET	
1.1	04/07/2023	Diffusion initiale	
PLOMBERIE			
 • CHAUFFE-EAU  • ATTENTE EAU FROIDE  • RESEAU EAU FROIDE  • RESEAU EAU CHAUDE  • RESEAU EAU USEES  • RESEAU EAU VANNES  • DESCENTE CONDUIT EVACUATION EV  • ARRIVEE PAR LE HAUT CONDUIT EVACUATION EV  • DESCENTE CONDUIT EVACUATION EU  • ARRIVEE PAR LE HAUT CONDUIT EVACUATION EU  • CARROTAGE REALISE			

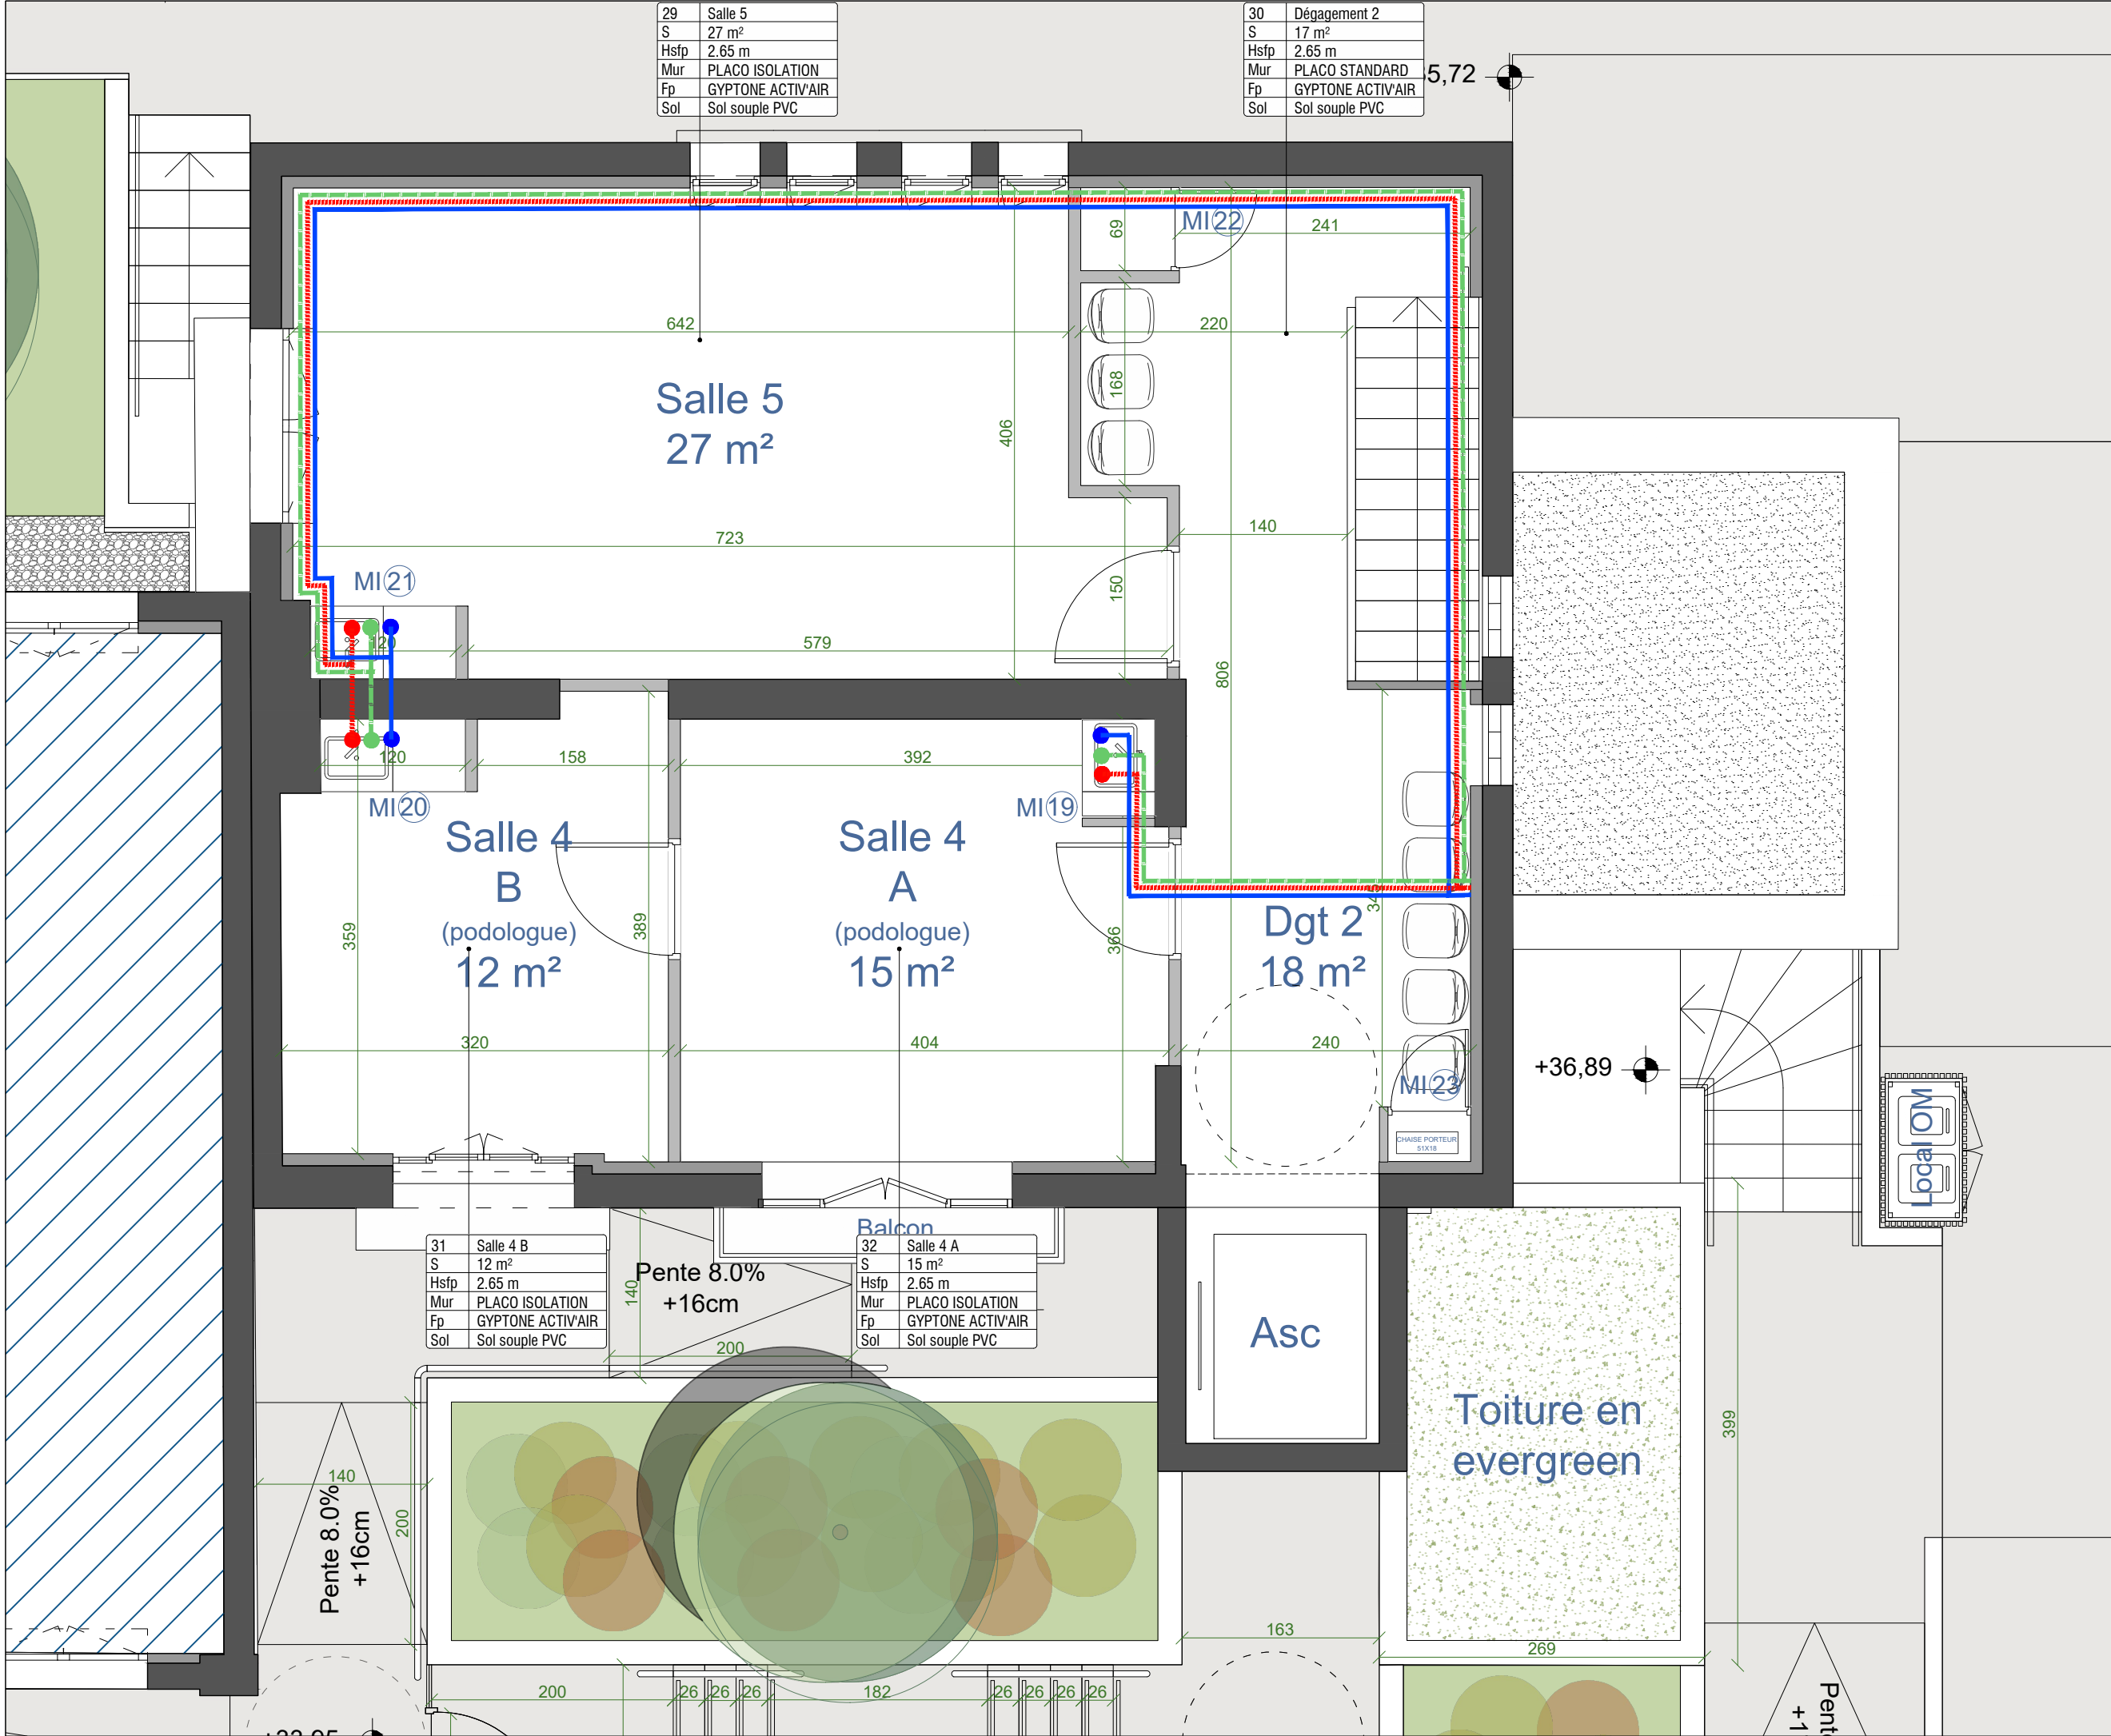

CREATION D'UN MULTI-ACCUEIL ET D'UNE MAISON MEDICALE
78400 CHATOU

MOA

SARL LPC YVELINES
15 Rue de l'Orient78000 VERSAILLES

MOE

NAHK ARCHITECTURE
24 Rue Yves Toudic, 75010 Paris

NOM DU DOCUMENT

PLOMBERIE
SECTEUR 2

PHASE

PRO.DCE

ECH.

1/50

INDICE

1.1

DATE

04/07/2023

MODIFICATIONS

INDICE

DATE

OBJET

1.1

04/07/2023

Diffusion initiale

PLOMBERIE

• CHAUFFE-EAU

• ATTENTE EAU FROIDE

• RESEAU EAU FROIDE

• RESEAU EAU CHAUDE

• RESEAU EAU USEES

• RESEAU EAU VANNES

• DESCENTE CONDUIT EVACUATION EV

• ARRIVEE PAR LE HAUT CONDUIT EVACUATION EV


• DESCENTE CONDUIT EVACUATION EU

• ARRIVEE PAR LE HAUT CONDUIT EVACUATION EU

• CARROTAGE REALISE



CREATION D'UN MULTI-ACCUEIL ET D'UNE MAISON MEDICALE 78400 CHATOU			
MOA	SARL LPC YVELINES 15 Rue de l'Orient78000 VERSAILLES		
MOE	NAHK ARCHITECTURE 24 Rue Yves Toudic, 75010 Paris		
NOM DU DOCUMENT			
MENUISERIE SECTEUR 1			
PHASE	PRO.DCE	ECH.	1/50
INDICE	1.1	DATE	04/07/2023
MODIFICATIONS			
INDICE DATE OBJET			
1.1	04/07/2023	Diffusion initiale	

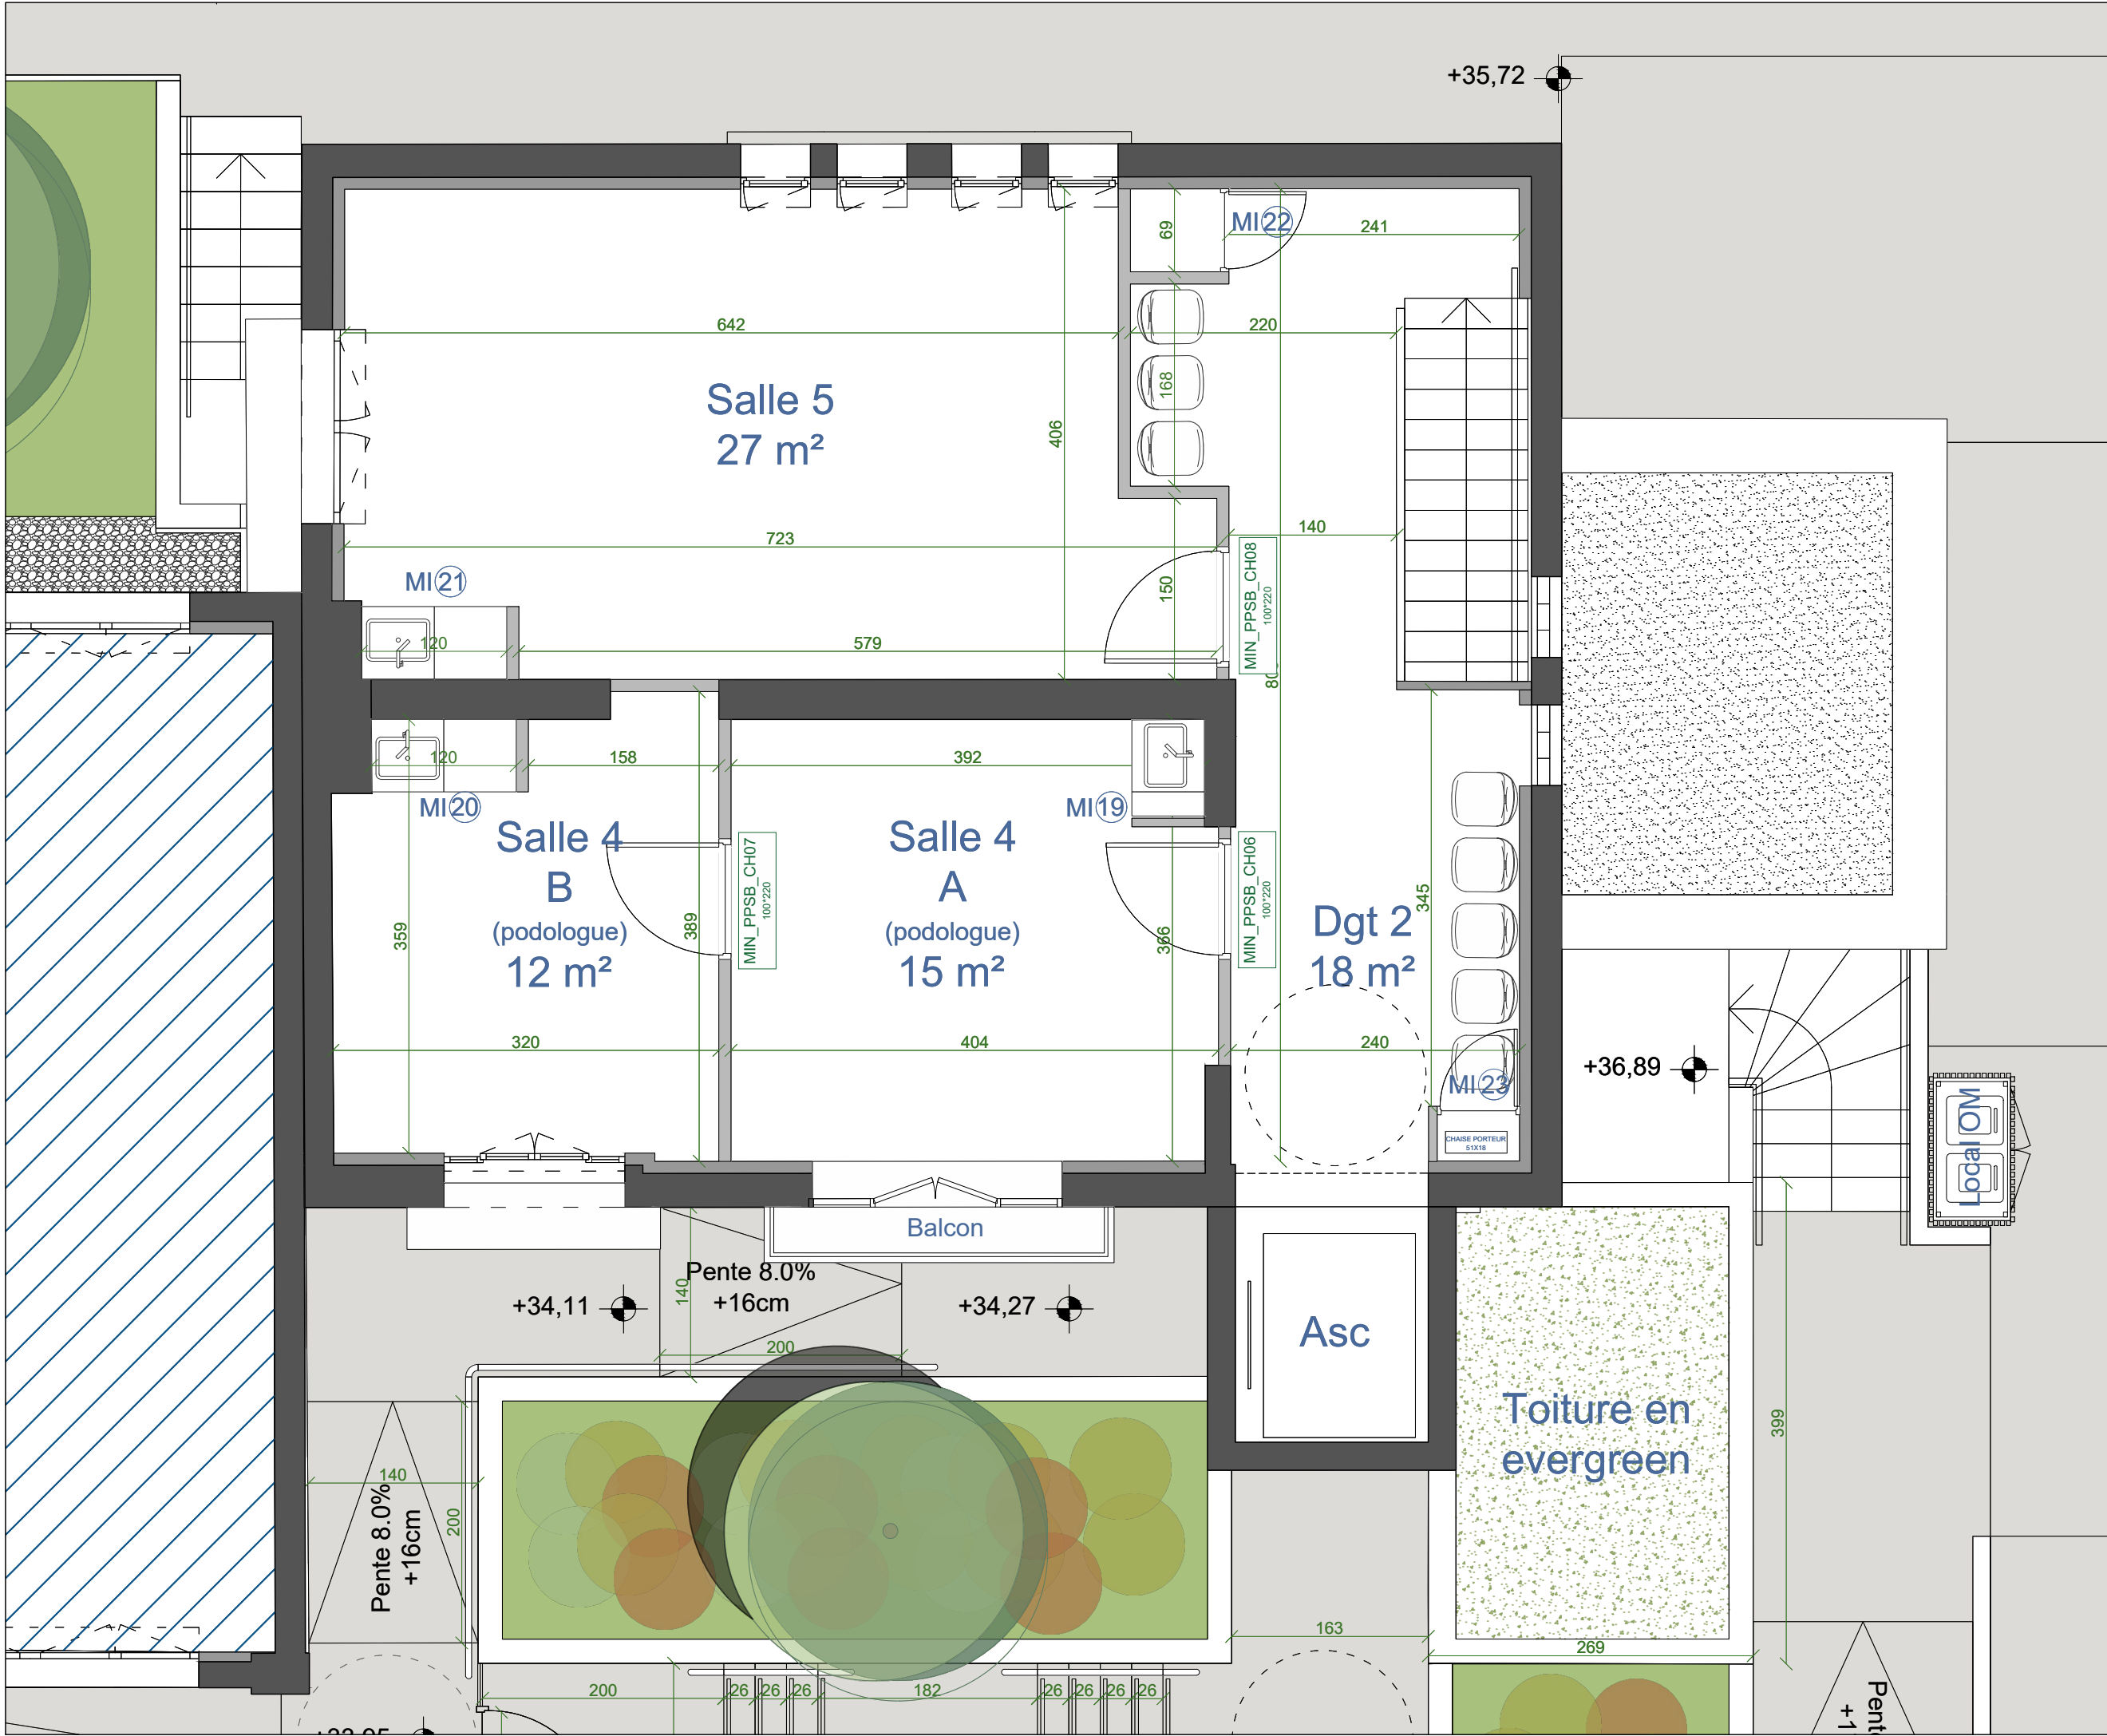

CREATION D'UN MULTI-ACCUEIL ET D'UNE MAISON MEDICALE 78400 CHATOU			
MOA	SARL LPC YVELINES 15 Rue de l'Orient78000 VERSAILLES		
MOE	NAHK ARCHITECTURE 24 Rue Yves Toudic, 75010 Paris		
NOM DU DOCUMENT			
MENUISERIE SECTEUR 2			
PHASE	PRO.DCE	ECH.	1/50
INDICE	1.1	DATE	04/07/2023
MODIFICATIONS			
INDICE DATE OBJET			
1.1	04/07/2023	Diffusion initiale	

NOMENCLATURE MENUISERIES INTÉRIEURES

MIN_PPSB. Simple battant
Dimensions : 100 x 220cm
Quantité : 8
Battants : Simple à âme pleine
Localisation : WC, Salle 1, Salle 2, Salle 3, Salle 4 A, Salle 4 B, Cuisine
Remarques : serrure, ferme porte intégré, H poignée 100 cm

MIN_PPSB_CH01
100*220

MIN_PPSB_CH02
100*220

MIN_PPSB_CH03
100*220

MIN_PPSB_CH04
100*220


MIN_PPSB_CH05
100*220

MIN_PPSB_CH06
100*220


MIN_PPSB_CH07
100*220

MIN_PPSB_CH08
100*220

Vue en plan :

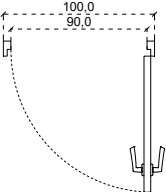

Élévation :

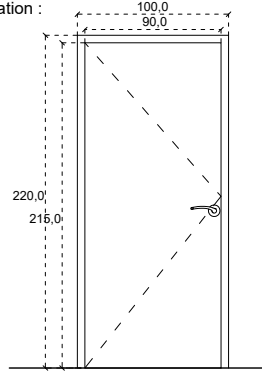


NOMENCLATURE MENUISERIES EXTÉRIEURES

MEXT_PPSB. Simple battant aluminium
Dimensions : 100 x 220 cm
Quantité : 2
Battants : Simple à âme pleine
Localisation : Local poussettes, Local lit secours
Remarques : serrure, ferme porte intégré, H poignée 100cm


MEXT_PPSB_CH10
220*100

MEXT_PPSB_CH11
220*100

Vue en plan :

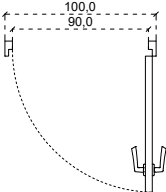

Élévation :

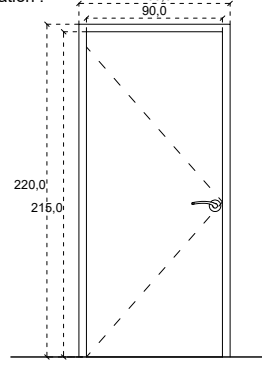

CREATION D'UN MULTI-ACCUEIL ET D'UNE MAISON MEDICALE
78400 CHATOU

MOA SARL LPC YVELINES
15 Rue de l'Orient78000 VERSAILLES

MOE NAHK ARCHITECTURE
24 Rue Yves Toudic, 75010 Paris

NOM DU DOCUMENT

TABLEAU DES MENUISERIES INTERIEURES ET EXTERIEURES

PHASE	PRO.DCE	ECH.	1/50
INDICE	1.1	DATE	04/07/2023

MODIFICATIONS
INDICE DATE OBJET

1.1	04/07/2023	Diffusion initiale
-----	------------	--------------------

--	--	--