



MAITRE D'OUVRAGE



LES PETITES CANAILLES
36 rue Pierret
92 200 - NEUILLY SUR SEINE
Tel : 01 58 83 48 35
Mail : dtondelli@lespetitescanailles.fr

CRECHE

56 Chaussée Jules César - 95 130 LE PLESSIS BOUCHARD

-

MAITRE D'OEUVRE



A+A architectes
SARL d'architecture et d'aménagement
Ordre des architectes IDF 716
1 bis villa Guizot - 75017 PARIS
Tel : 01 58 05 04 80
Mail : atelier@apa.archi

BUREAU ETUDES STRUCTURE



NOM BET structure
adresse
00000 VILLE
00 00 00 00 00
betstructure@mail.fr

BUREAU ETUDES FLUIDES



NOM BET fluides
adresse
00000 VILLE
00 00 00 00 00
betfluides@mail.fr

BUREAU DE CONTROLE



NOM BEC
adresse
00000 VILLE
00 00 00 00 00
bureaucontrôle@mail.fr

Phase :


DCE

Affaire et plan n°:


**23014 - 400
p.**

Date :

**Indice G
30/10/2023**

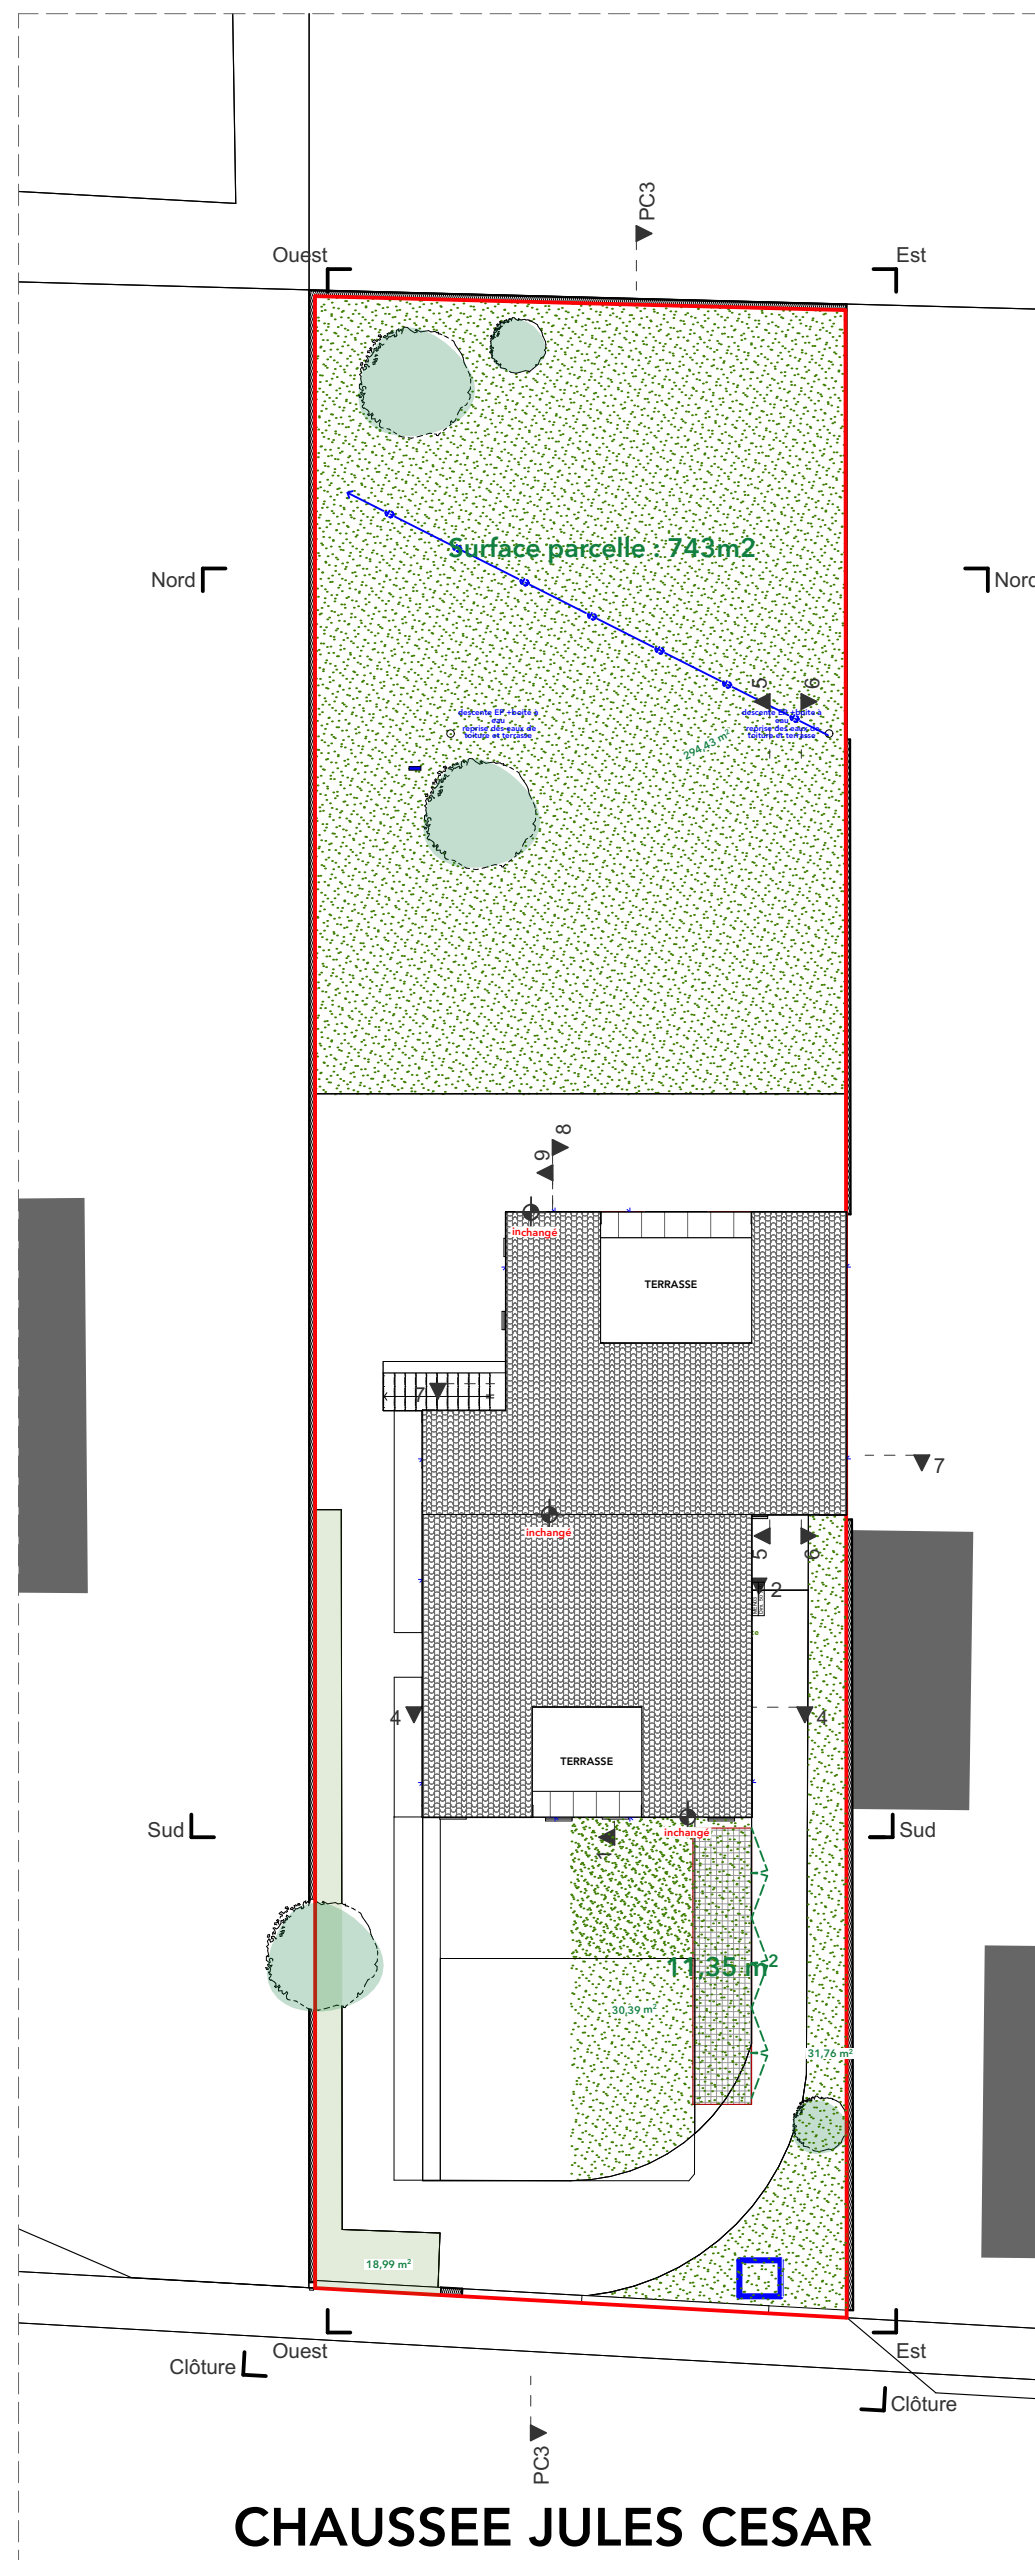


Plan masse - Existant

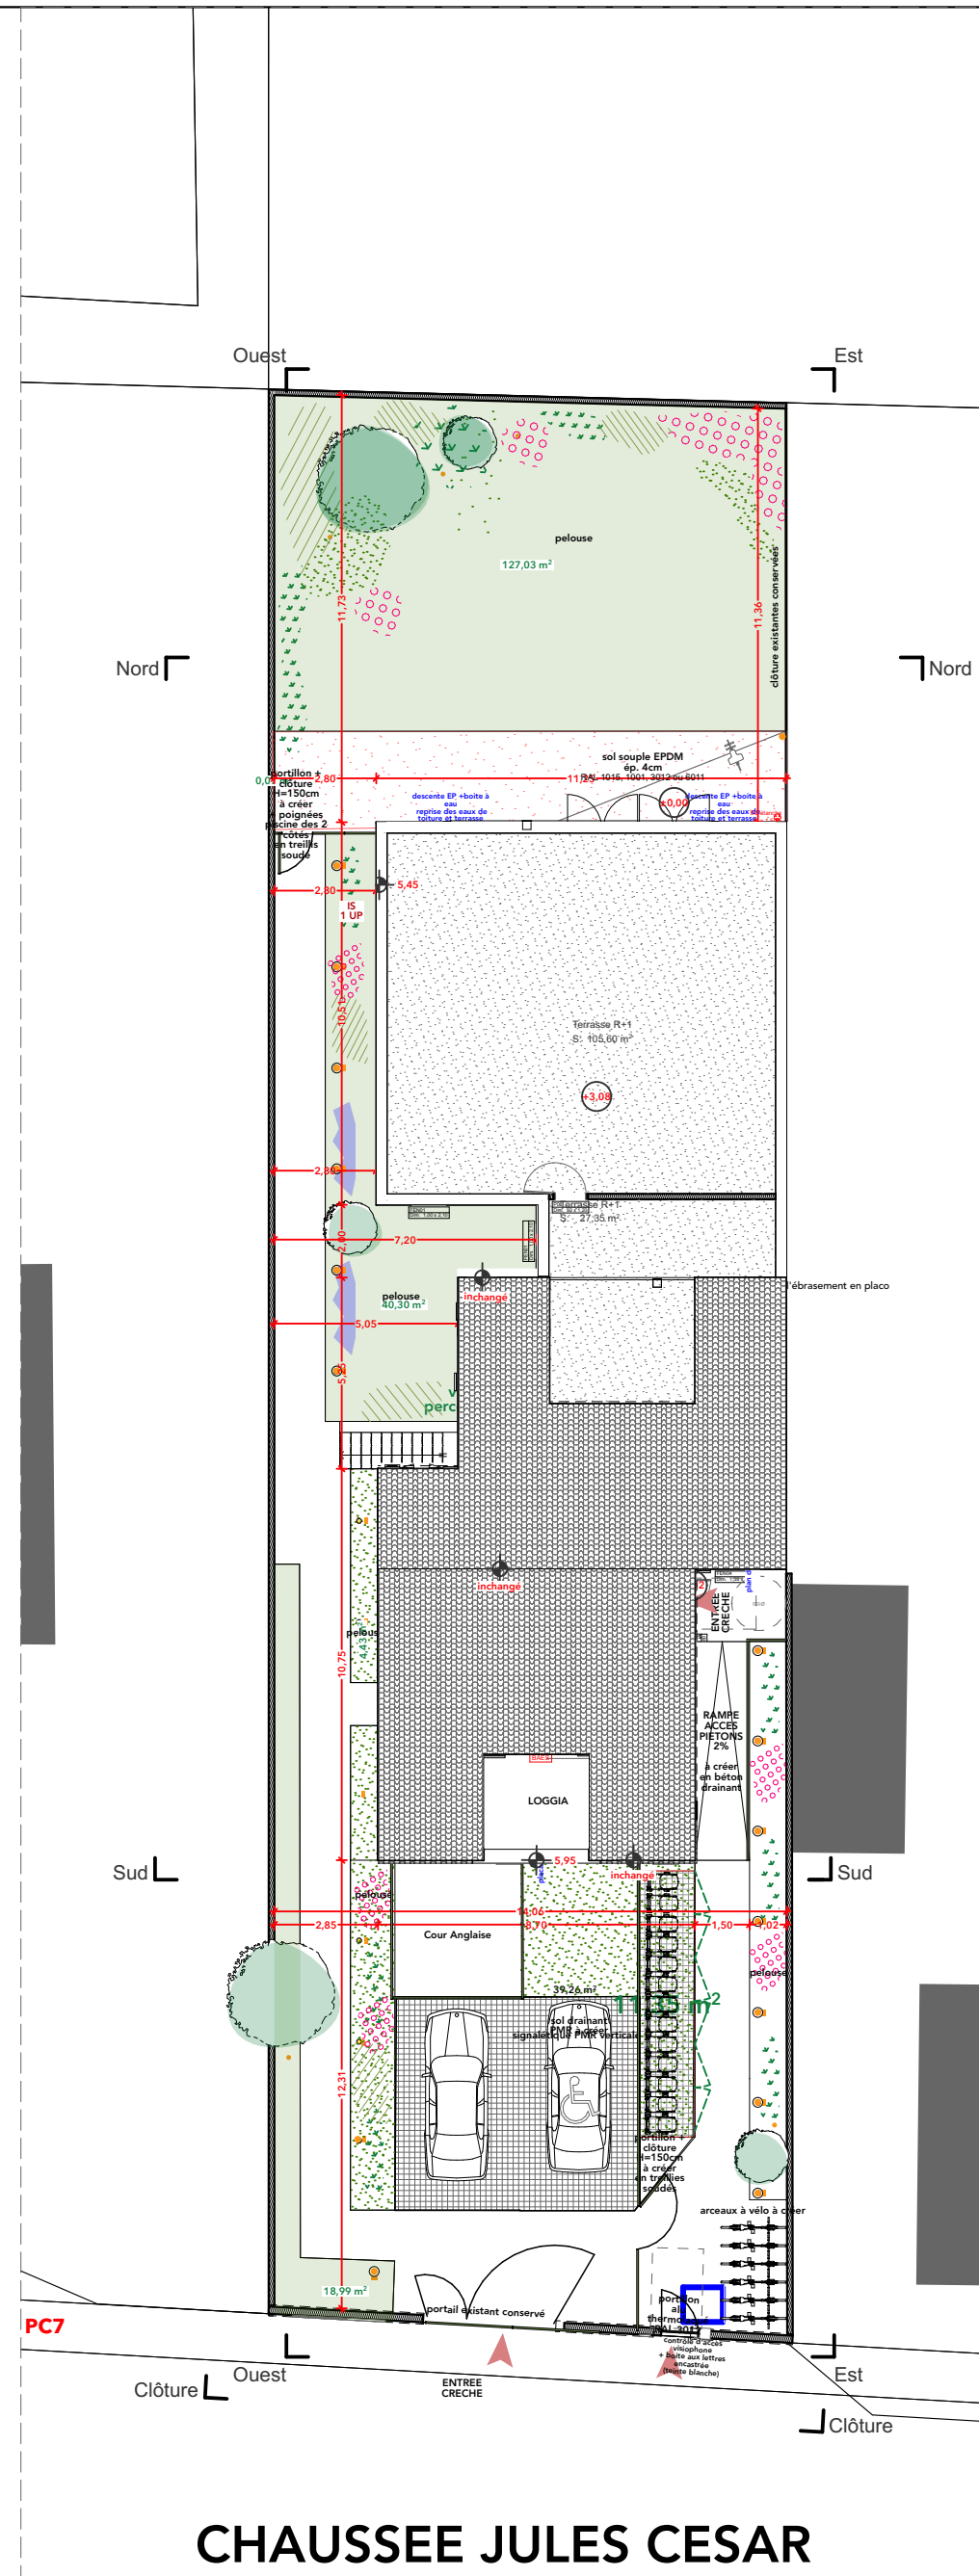

Plan masse - Projet

LEGENDE PLAFONDS ET LUMINAIRES

- | | |
|---|--|
|  | Bandeau LED encastré haut cuisine et biberonnerie - 3000K |
|  | Pavé LED 60x60cm - IRO - 3000K - DALI - RESISTEX |
|  | Downlight LED rond encastré dans faux-plafond (extension) |
|  | S1 - Suspension type 1 (hall) |
|  | S2 - Suspension type 2 (direction) |
|  | P1 - Plafonnier type 1 (local personnel...) |
|  | P2 - Plafonnier type 2 (WC PMR, Poussette, stock, locaux techniques, poubelles...) |
|  | A1 - Applique type 1 (repos 1 et 2, activités) |
|  | A2 - Applique type 2 (locaux techniques) |
|  | Borne extérieure - ton blanc ou beige |
|  | Spot LED - 3000k (éclairage arbres - à fixer sur murs de clôture) |

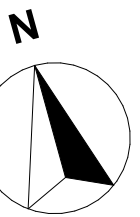

CRECHE
56 Chaussée Jules César -
95 130 LE PLESSIS BOUCHARD

	MAITRE D'OUVRAGE	LES PETITES CANAILLES	36 rue Pierret 92 200 - NEUILLY SUR SEINE	Tel : 01 58 83 48 35 Mail : dtondelli@lespetitescanailles.fr
	MAITRE D'OEUVRE	A+A architectes	1 bis villa Guizot 75017 PARIS	Tel : 01 58 05 04 80 Mail : atelier@apa.archi
	BET STRUCTURE	NOM BET structure	adresse 00000 VILLE	Tel : 00 00 00 00 00 Mail : betstructure@mail.fr
	BET FLUIDES	NOM BET fluides	adresse 00000 VILLE	Tel : 00 00 00 00 00 Mail : betfluides@mail.fr
	BUREAU CONTROLE	NOM BEC	adresse 00000 VILLE	Tel : 00 00 00 00 00 Mail : bureaucontrole@mail.fr

Plan de masse

Phase :

DCE

Affaire et plan n°:

23014

02


Format :

A2

Echelle:

1:200,

1:50

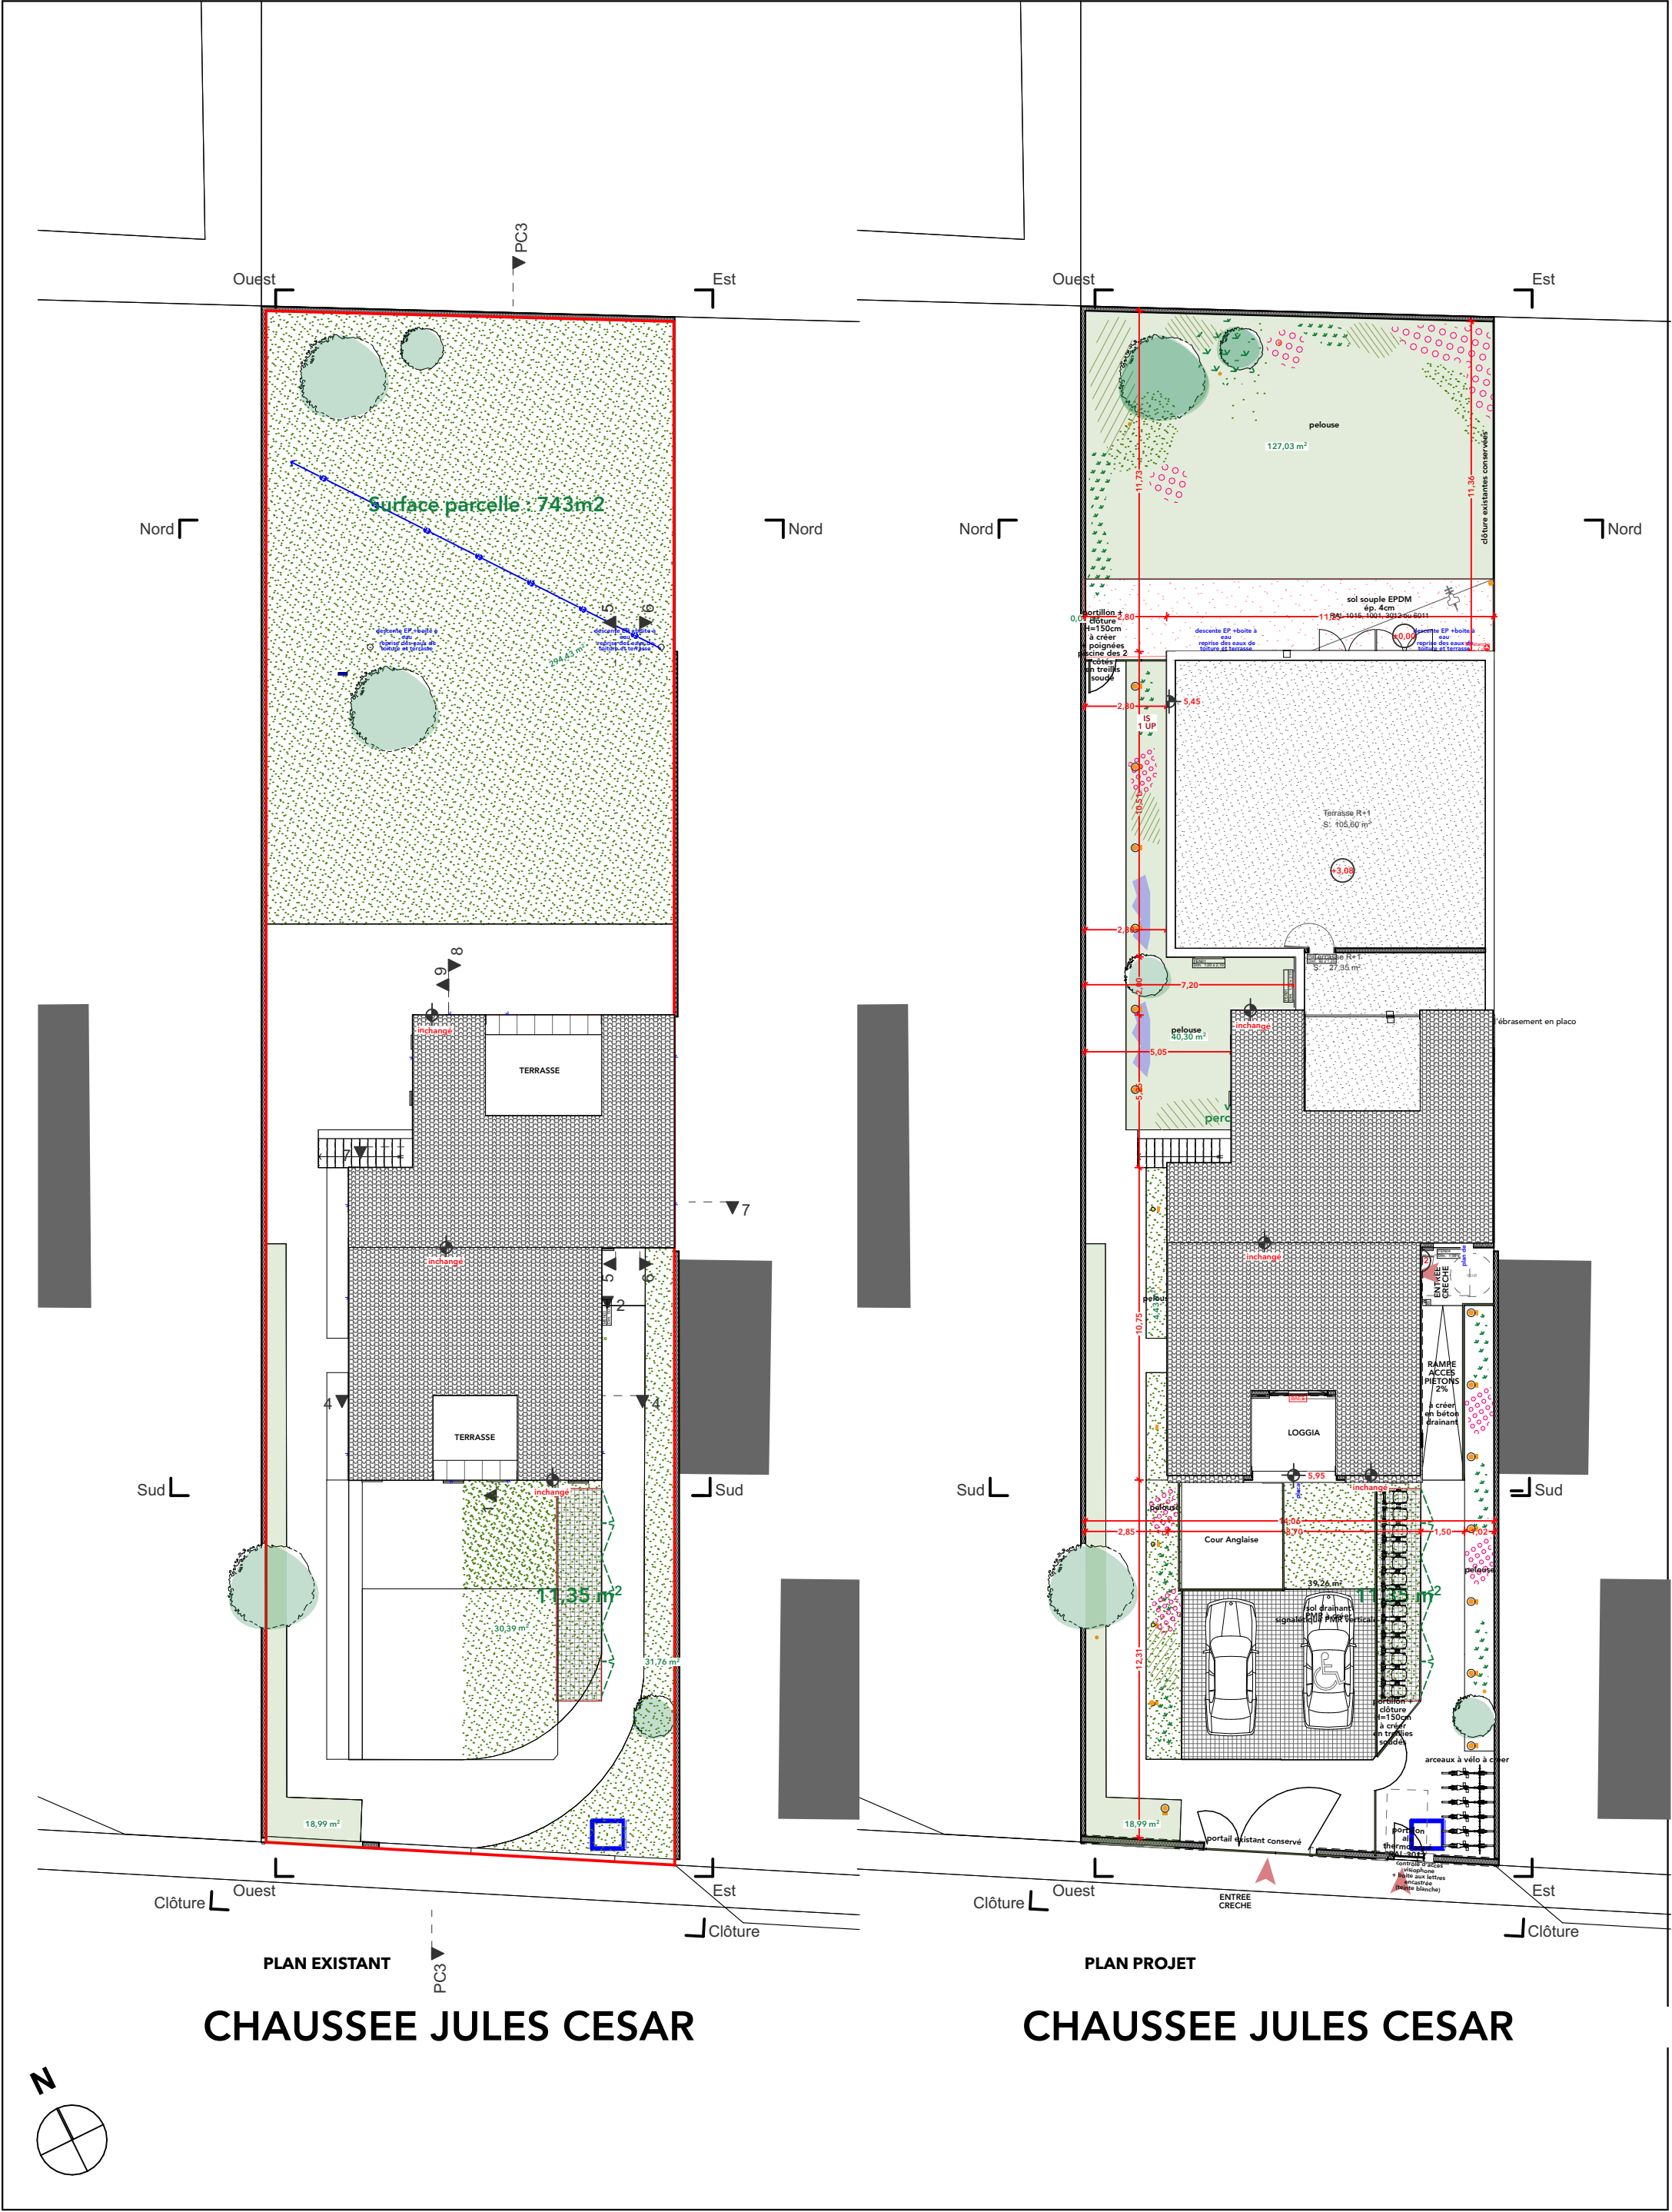

MAITRE D'OUVRAGE



LES PETITES CANAILLES
36 rue Pierret
92 200 - NEUILLY SUR SEINE
Tel : 01 58 83 48 35
Mail : dtondelli@lespetitescanailles.fr

MAITRE D'OEUVRE




A+A architectes
SARL d'architecture et d'aménagement
Ordre des architectes IDF 716
1 bis villa Guizot - 75017 PARIS
Tel : 01 58 05 04 80
Mail : atelier@apa.archi

CRECHE

56 Chaussée Jules César - 95 130 LE PLESSIS BOUCHARD

Plan de toitures

Affaire et plan n°:	Phase :	
p.08	DCE	
Echelle :	Indice initial :	Indice en cours :
1:200	indice 0 17/05/2023	indice F 27/10/2023

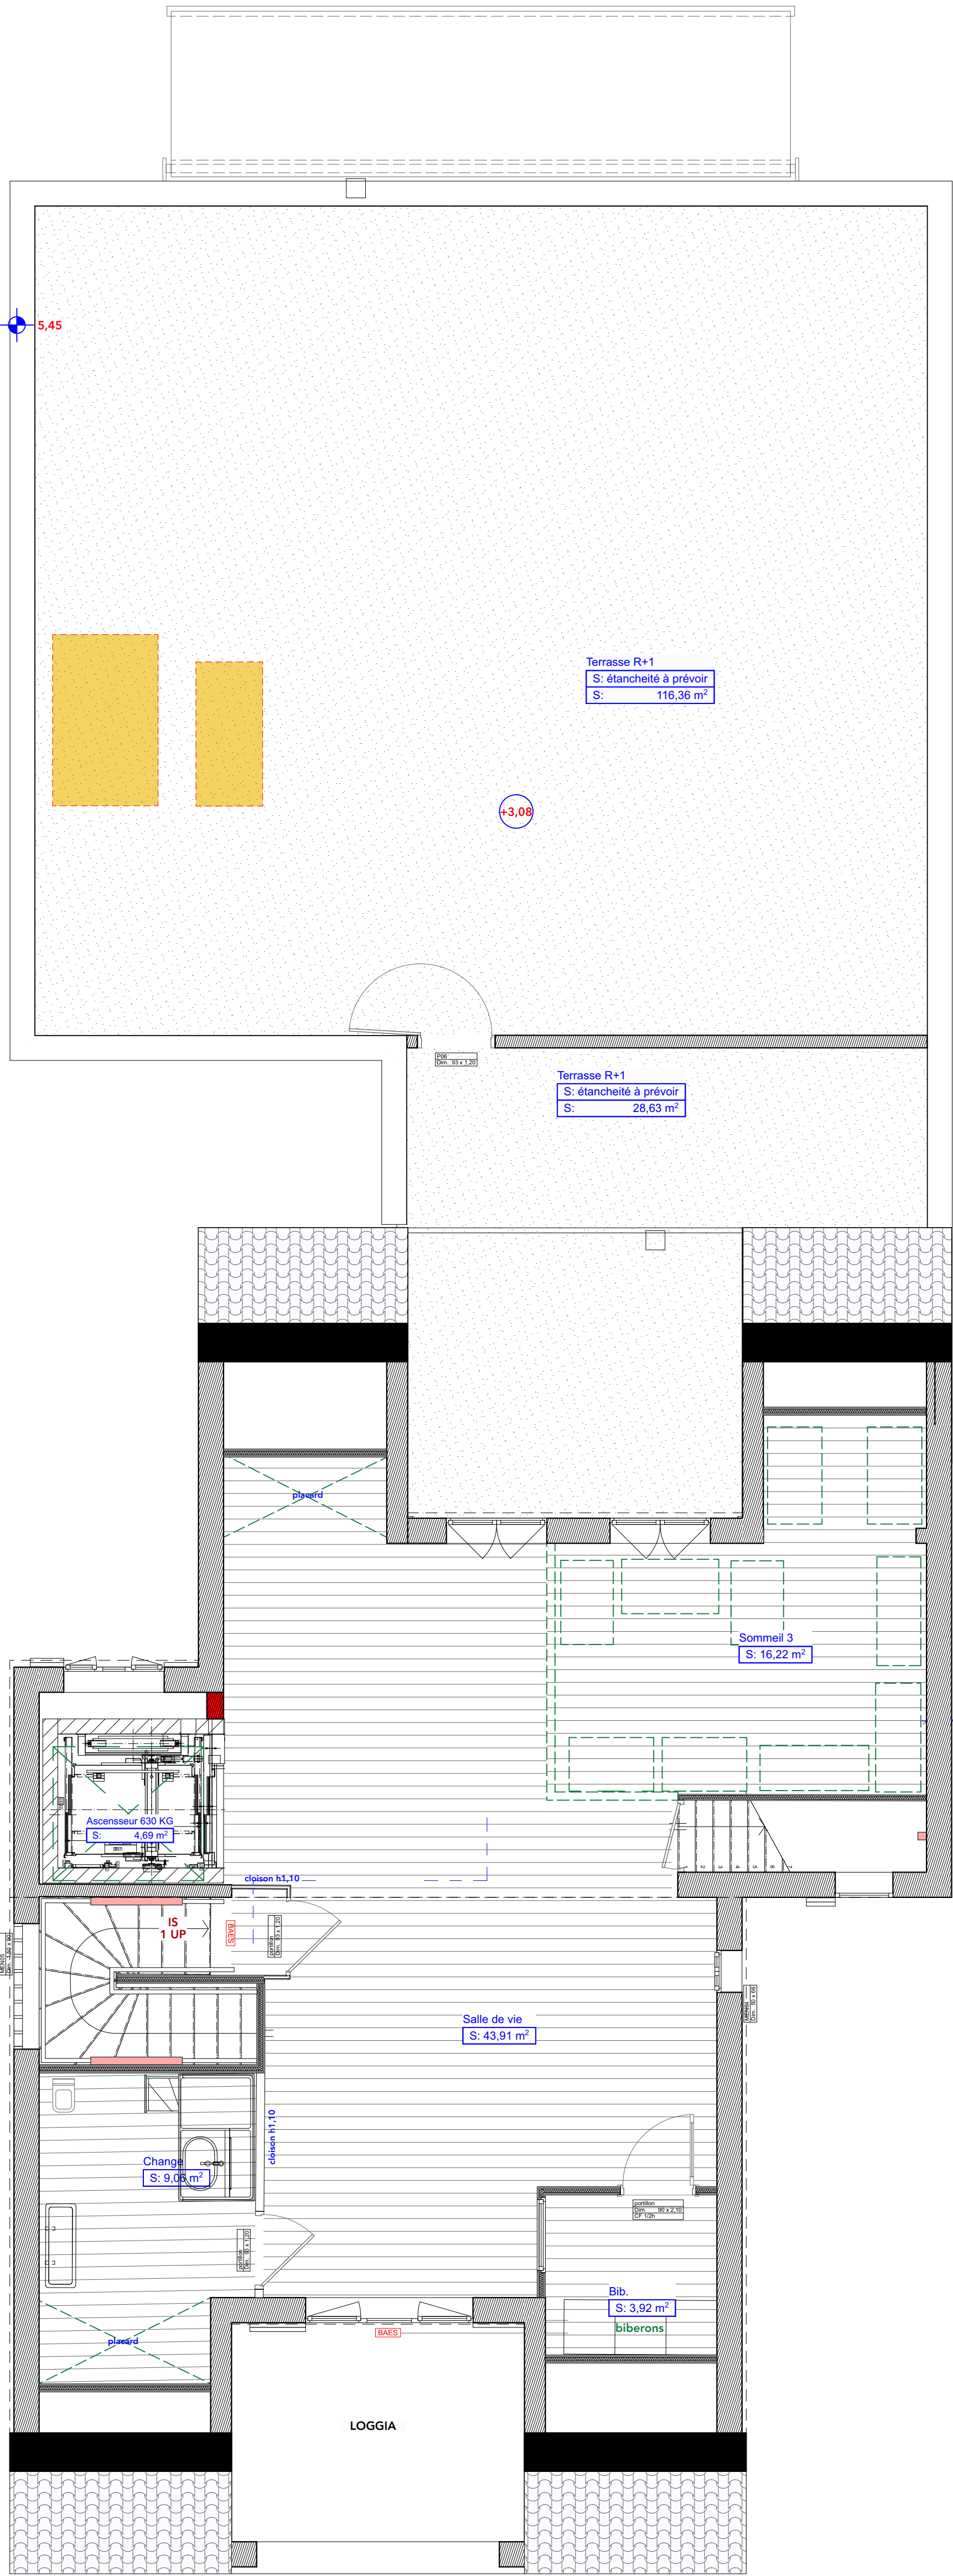

LEGENDE SECURITE INCENDIE		LEGENDE PORTES
	bloc d'eclairage de secours sur porte	Porte PF 1/2h
	extincteur eau pulvérisée 6L	Porte avec joints anti-pinces doigts - côté poignée et côté poussoir 1h-140cm
	extincteur pour danger électrique CO2	Vitrophanie selon détail
	alarme	Pictogramme repérage de local selon détail
	déclencheur manuel	
	flash	
LEGENDE ELECTRICITE		LEGENDE REVETEMENT MURAL
	thermostat	Faïence type 1 - voir CCTP
	visiophone	Faïence type 2 - voir CCTP
	visiophone + digicode à menu défilant	Papier-peint 1 - voir CCTP
	PC	Papier-peint 2 - voir CCTP
	PC 1,30m	Tasseaux bois + feutre acoustique - voir CCTP
	RJ45	Peinture CHROMATIC CH1 0529 VERT CEVENNES
	PC sèche-linge	
	PC lave-linge	
	PC réfrigérateur	
	PC lave-vaisselle	
	PC plaques de cuisson	
	PC four	
	Alimentation élec en attente	
	Détecteur de présence	
	Interrupteur à variateur	
	Interrupteur simple	
	Douille DCL	
	Détecteur autonome avertisseur de fumée	
NOTA : Toutes les commandes situées dans la crèche et l'école seront "sanitized"		

LEGENDE

CRECHE			
56 Chaussée Jules César - 95 130 LE PLESSIS BOUCHARD			
	MAITRE D'OUVRAGE	LES PETITES CANAILLES	36 rue Pierret 92 200 - NEUILLY SUR SEINE
	MAITRE D'OEUVRE	A+A architectes	1 bis villa Guizot 75017 PARIS
	BET STRUCTURE	NOM BET structure	adresse 00000 VILLE
	BET FLUIDES	NOM BET fluides	adresse 00000 VILLE
	BUREAU CONTROLE	NOM BEC	adresse 00000 VILLE
	BET VRD		
	PAYSAGISTE		
	ECONOMISTE		
	M. OEUVRE EXECUTION		

Plan - R+1

	Phase :
	DCE
	Affaire et plan n° : 23014
	Format : A1
	Echelle : 1:50

56 Chaussée Jules César - Le Plessis Bouchard
Tableau de surfaces du 27/10/2023. ref plan DCE indiceG du 31/10/2023

ETABLISSEMENT D'ACCUEIL POUR JEUNES ENFANTS

Nombre de berceaux	34	Surfaces (m²)		Ratio (en m²/berceau)		
Bébés :		Espaces enfants	234,91	Espaces enfants	6,91	
Moyens :		Espaces personnel	86,08	Espaces personnel	2,53	
Grands :		Surface utile	381,75	Surface utile	11,23	
		Surface de plancher	455,99	Surface de plancher	13,41	

	Type	Locaux	Public	Enfants	Privé	Circulations	Surfaces utiles
Public	Accueil	Bureau de Direction	13,52				60,76
		Hall	29,93				
		WC PMR	4,12				
		Local motricité	13,19				
Enfants	Section 1	Salle de vie 1		114,03			165,72
		Salle de change 1		12,39			
		Sommeil 1		19,22			
		Sommeil 2		20,08			
	Section 2	Salle de vie 2		43,91			69,19
		Salle de change 2		9,06			
Personnel	Technique	Sommeil 3		16,22			56,15
		Circulation - Sous-sol				14,59	
		Entretien - Sous-sol			2,82		
		Local technique - Sous-sol			6,28		
		Poubelles - Sous-sol			2,53		
		lingerie - Sous-sol			0		
		Buanderie - Sous-sol			10,8		
		Office de remise en température - Sous-sol			9,99		
		Stock - SS-1			10,71		
		Circulation - RDC				0	
		Entretien - RDC			1,22		
		Poubelles - RDC			1,22		
		Stocks - RDC			1,22		
		Biberonnerie 1 - RDC			5,44		
	Personnel	Circulation - R+1			0	0	29,93
		Poubelles - R+1			0		
		Stocks - R+1			0		
		Biberonnerie 2 - R+1			3,92		
		Repos personnel			19,53		
		Vestiaires			8,93		
		WC personnel			1,47		
		Circulation - R+2				0	

Surfaces Utiles (en m²)	60,76	234,91	86,08	14,59	381,75
	381,75				
	396,34				

Extérieur	Pelouse		135			135
Extérieur	Sol coulé RDC		35			35
Extérieur	Terrasse R+1		144			144
		0	314	0	0	314

Surfaces de plancher (en m²)			
	Réhabilitation	Extension	Total
SS-1	94,15		94,15
RDC	123,42	119,1	242,52
R+1	87,95	0	87,95
R+2	31,37	0	31,37
Total	336,89	119,1	455,99